



VISTA FRONTAL
CON PUERTA

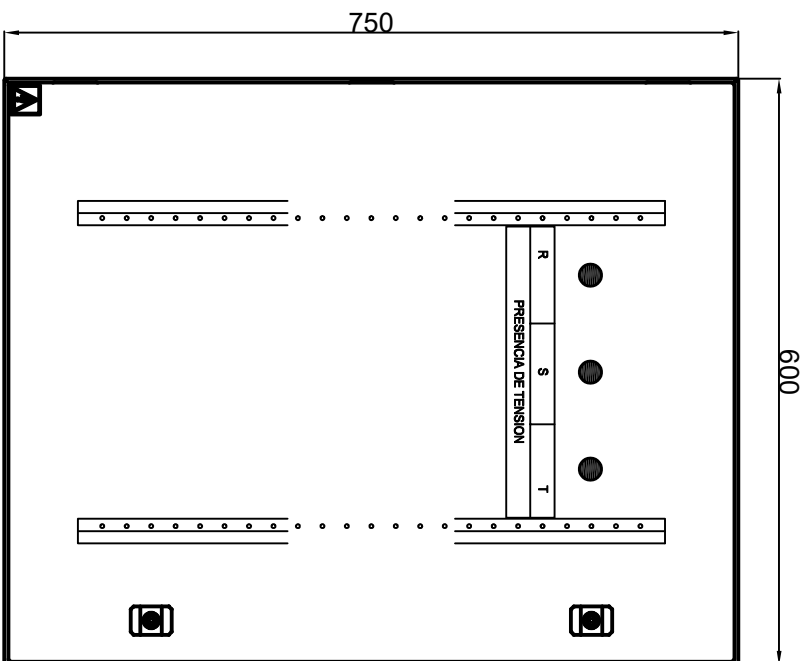


VISTA LATERAL
DERECHA




VISTA FRONTAL SIN PUERTA
CON BANDEJA

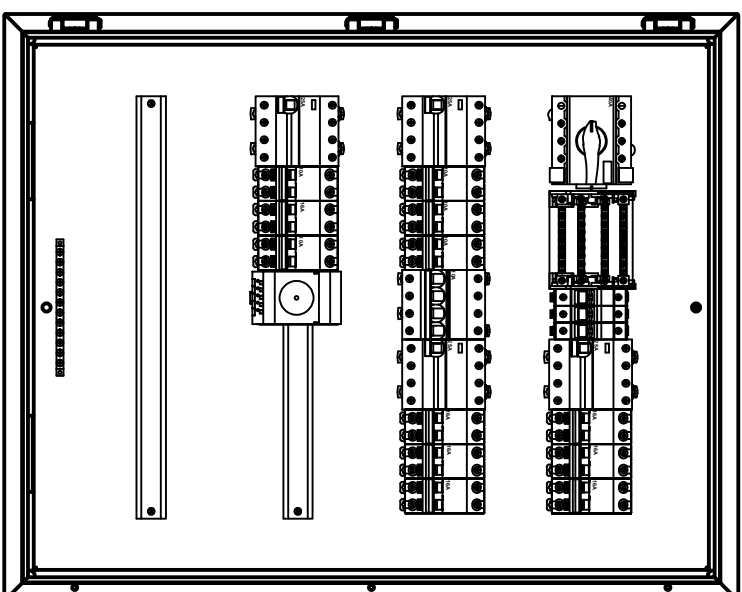

VISTA FRONTAL SIN PUERTA
CON CONTRAFRENTE

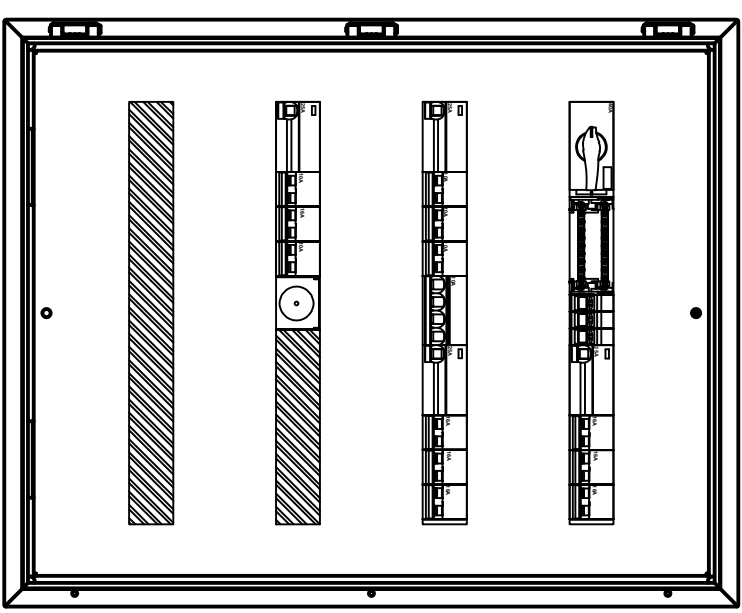

Tablero Seccional
Sector: - Gobierno Sub Unidad

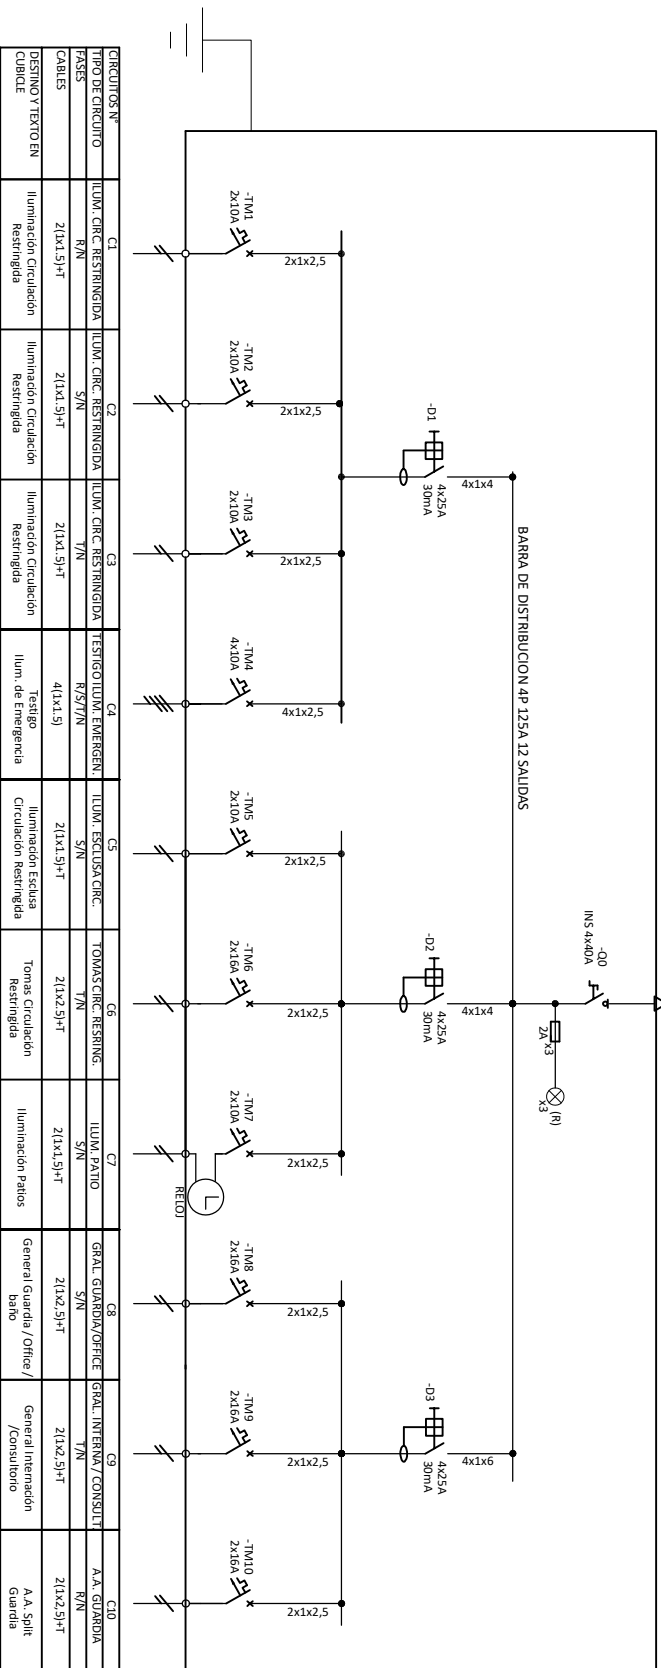

NOTA: TODOS LOS INTERRUPTORES SERAN DE PRIMERA MARCA TIPO SCHNEIDER - SIEMENS O SIMILAR
LAS ENVOLVENTES SERAN TIPO TECNOBOX - GENROD O SIMILAR



SEMI
CONSTRUCCIONES SRL
WWW.SEMICONSTRUCCIONES.IL.COM

OBRA: LP N°8

COMITENTE: EDECA SA, PECAM SA, DYSCON SA, MINERVINO SA

PLANO: UNIFILARES Y TOPOGRAFICOS

ESCALA: Grafica

OBRA: LUP N°8	REV A
COMITENTE: EDECA SA, PECAM SA, DYSCON SA, MINERWIND SA	
PLANO: UNIFLARES Y TOPOGRAFICOS	
ESCALA: Grafica	
	FECHA: 01/05/2025
	HOLLA: 1/1