


VISTA FRONTAL CON PUERTA

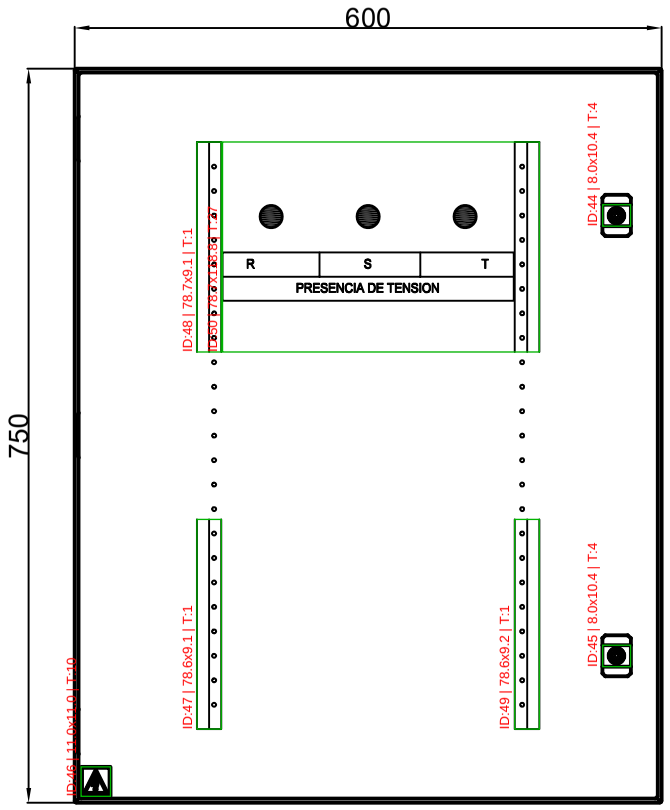


VISTA LATERAL DERECHA

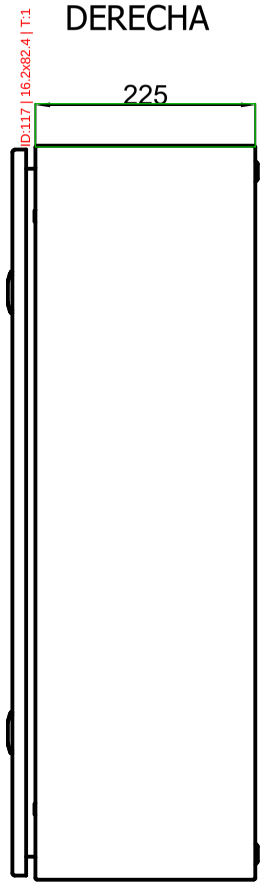

VISTA FRONTAL SIN PUERTA CON BANDEJA

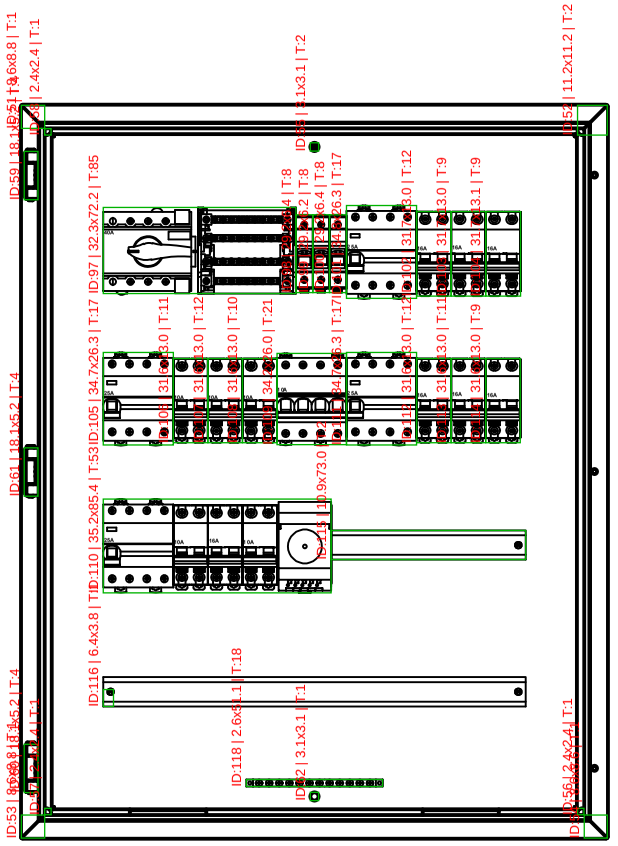


VISTA FRONTAL SIN PUERTA CON CONTRAFRENTE

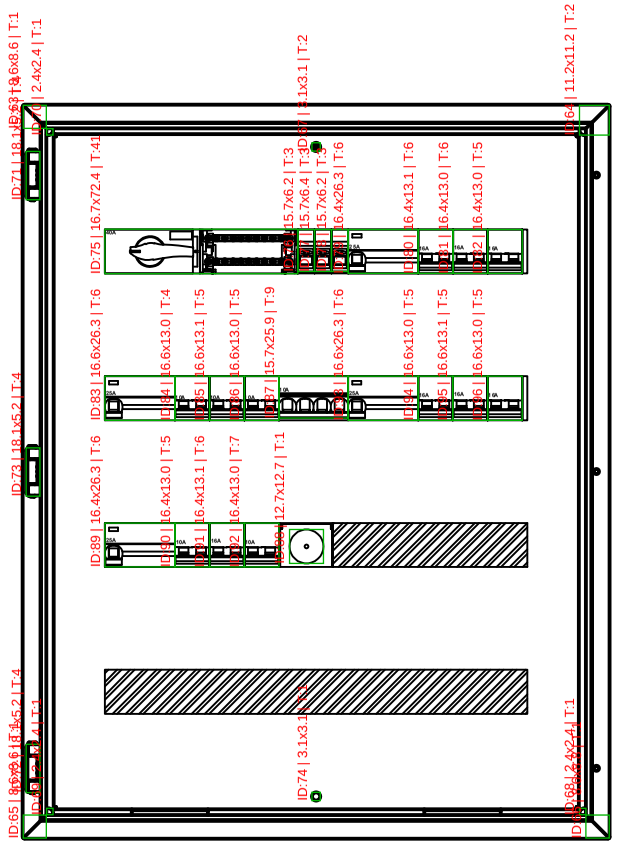

ESQUEMA UNIFILAR
"TABLERO CIRCULACION RESTRINGIDA NORTE."

Tablero Seccional
Sector: - Gobierno Sub Unidad

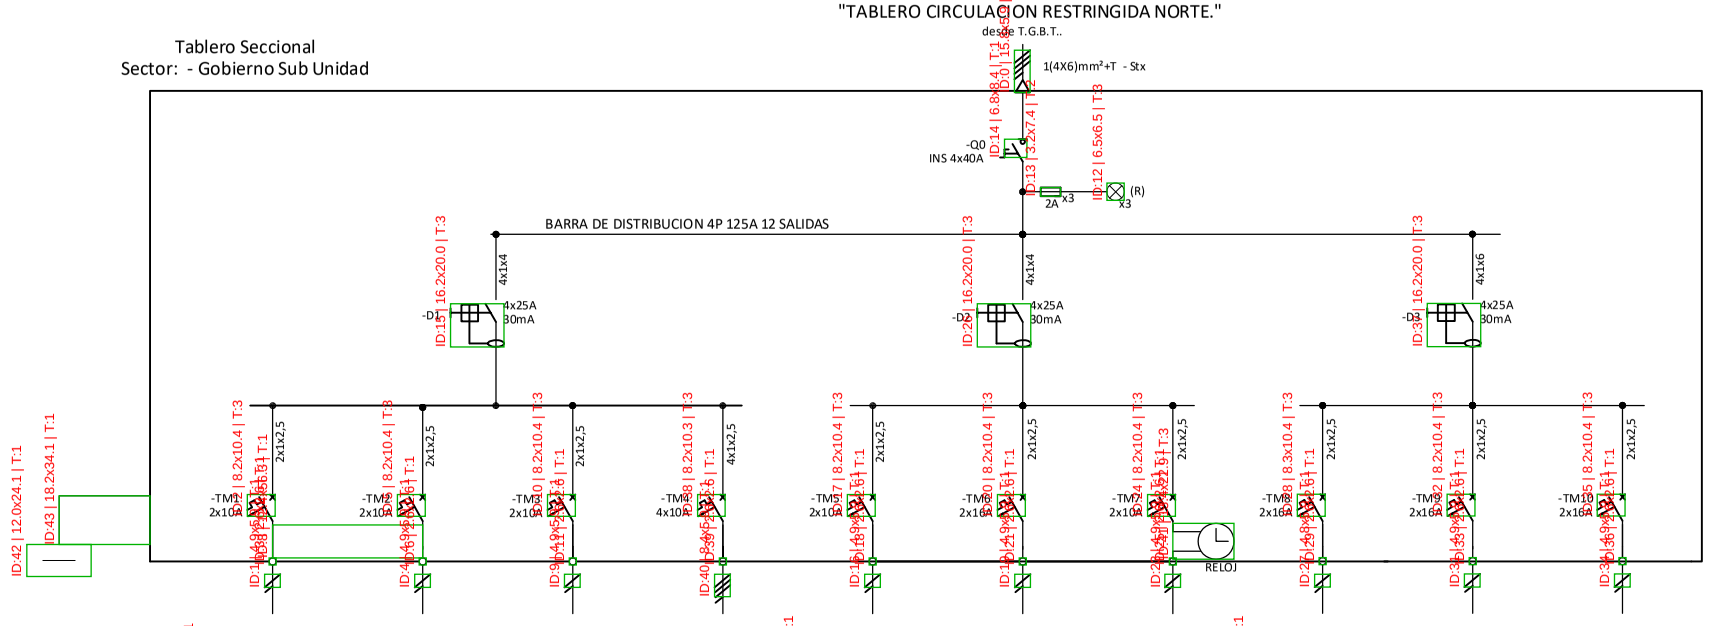

CIRCUITOS N°	C1	C2	C3	C4	C5	C6	C7	C8	C9	C10
TIPO DE CIRCUITO	ILUM. CIRC. RESTRINGIDA	ILUM. CIRC. RESTRINGIDA	ILUM. CIRC. RESTRINGIDA	TESTIGO ILUM. EMERGEN.	ILUM. ESCLUSA CIRC.	TOMAS CIRC. RESTRING.	ILUM. PATIO	GRAL. GUARDIA/OFFICE	GRAL. INTERNA / CONSULT.	A.A. GUARDIA
FASES	R/N	S/N	T/N	R/S/T/N	S/N	T/N	S/N	S/N	T/N	R/N
CABLES	2(1x1.5)+T	2(1x1.5)+T	2(1x1.5)+T	4(1x1.5)	2(1x1.5)+T	2(1x2.5)+T	2(1x1,5)+T	2(1x2,5)+T	2(1x2,5)+T	2(1x2,5)+T
DESTINO Y TEXTO EN CUBICLE	Iluminación Circulación Restringida	Iluminación Circulación Restringida	Iluminación Circulación Restringida	Testigo Ilum. de Emergencia	Iluminación Esclusa Circulación Restringida	Tomas Circulación Restringida	Iluminación Patios	General Guardia / Office / baño	General Internación /Consultorio	A.A. Split Guardia

NOTA: TODOS LO INTERRUPTORES SERAN DE PRIMERA MARCA TIPO SCHNEIDER - SIEMENS o SIMILAR
LAS ENVOLVENTES SERAN TIPO TECNOBOX - GENROD O SIMILAR

SEM CONSTRUCCIONES SRL
WWW.SEMCONSTRUCCIONESSRL.COM

OBRA: UP N°8	REV A
COMITENTE: EDECA SA, PECAM SA, DYSCON SA, MINERVINO SA	
PLANO: UNIFILARES Y TOPOGRAFICOS	FECHA: 01/05/2025
ESCALA: Gráfica	HOJA: 1/1