

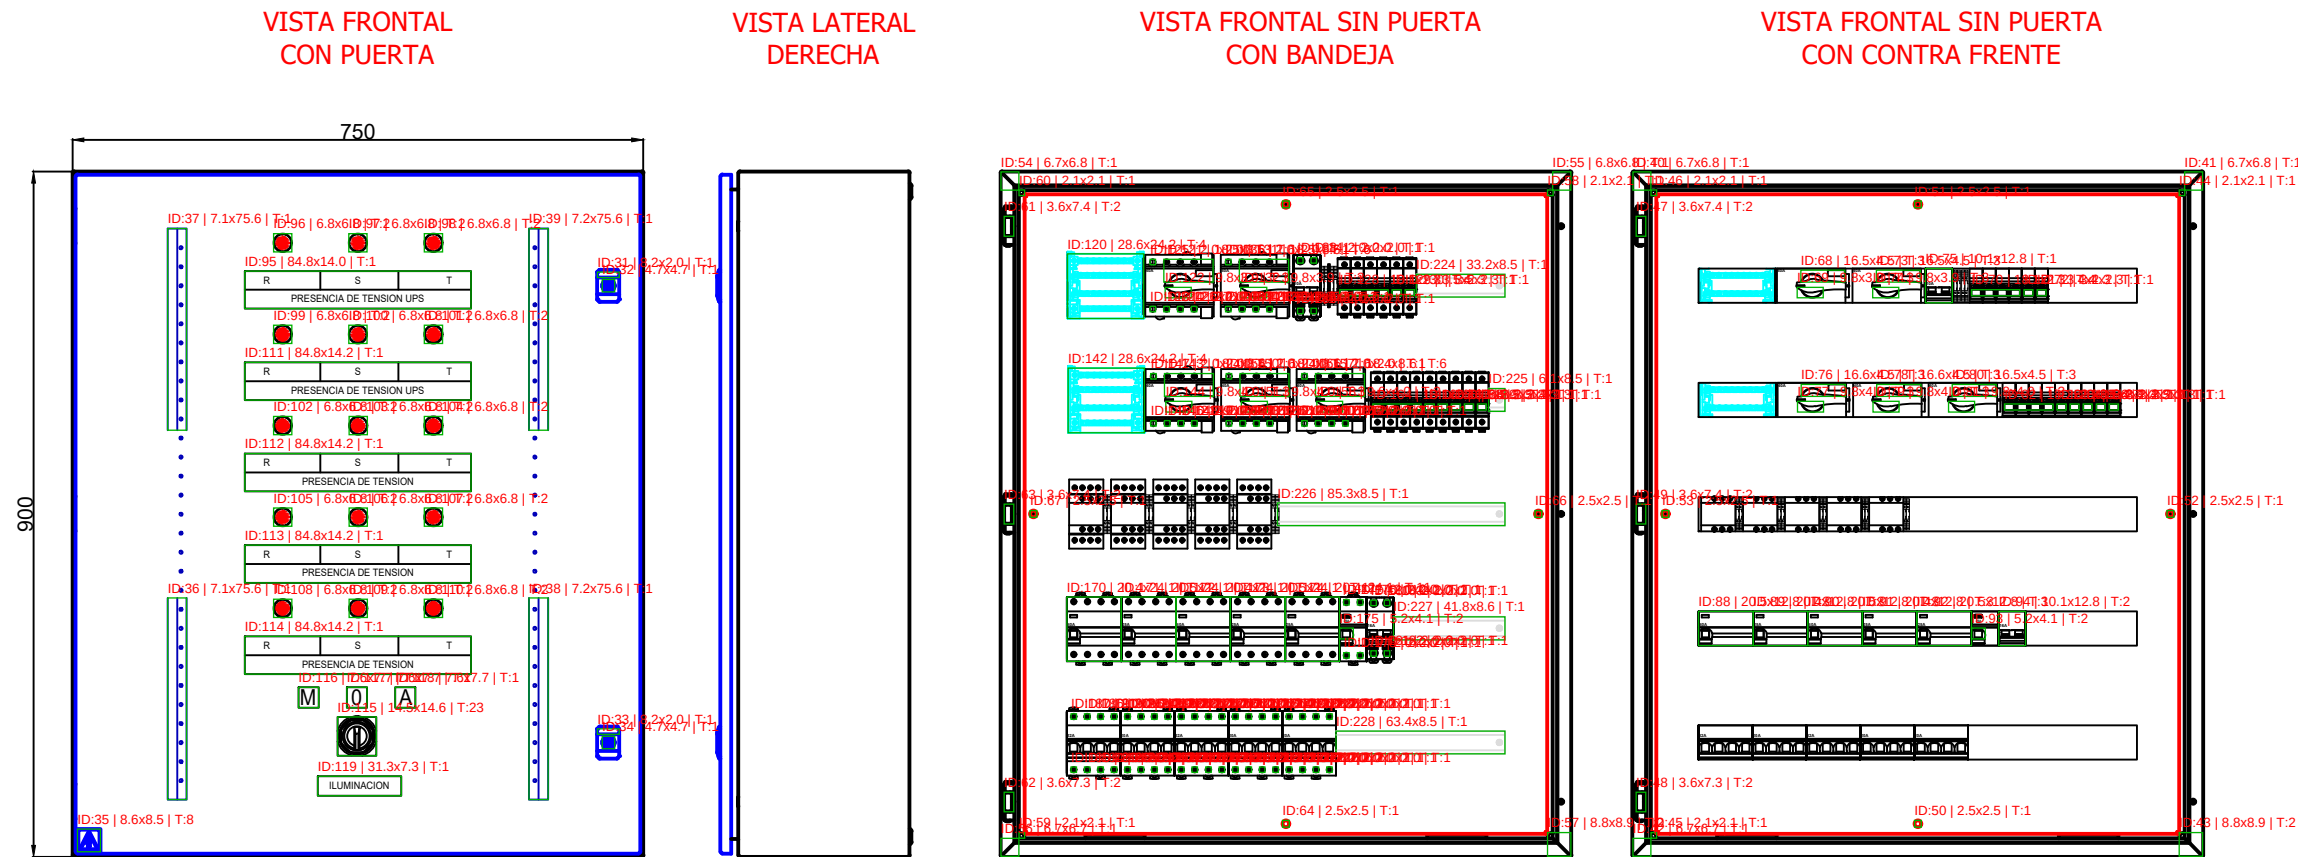


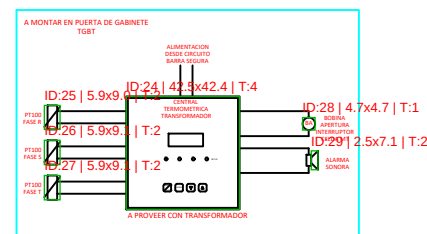

MODULOS

TABLERO TIE MODULOS (ILUMINACIÓN EXTERIOR)

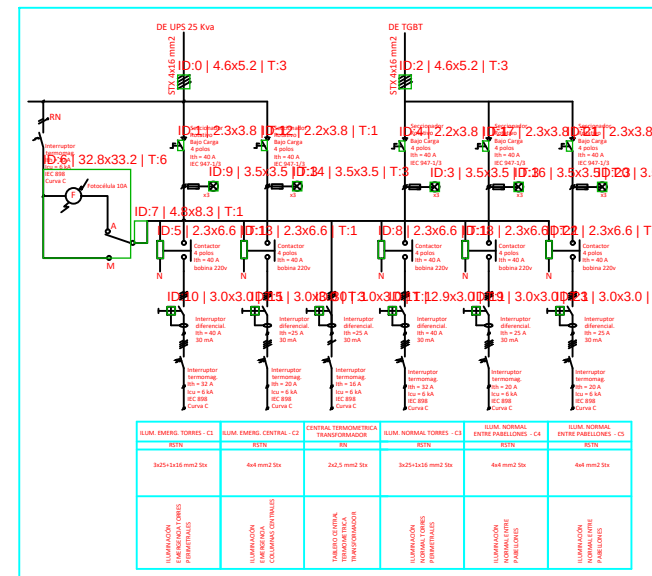

OBRA: UP N°8

COMITENTE: EDECA SA, PECAM SA, DYSCON SA, MINERVINO SA

PLANO: UNIFILARES Y TOPOGRAFICOS

ESCALA: Gráfica

REV A

FECHA: 17/06/2025

HOJA: 1/1