



2

1

2

CARACTERISTICAS.

- TENSION NOMINAL = 400 V.
- TENSION MAXIMA = 1.000 V.
- FRECUENCIA = 50 Hz.
- FASES = 3 (TRES)
- BARRA DE TIERRA.
- GRADO DE PROTECCION = IP55
- COLOR GRIS RAL 7032/7035.
- PLACA DE MONTAJE GALVANIZADA.
- ACOMETIDA= INFERIOR.
- MARCA GABINETES: HIMEL / RITTAL

CONDUCTOR DE PROTECCION EN TABLEROS (PE, PEN)

S: SECCION MAYOR CONDUCTOR DE FASE.
SPE: SECCION CONDUCTOR DE PROTECCION (PE, PEN).

$S \leq 16 \text{ mm}^2 \Rightarrow S_{PE} = S$
$16 \text{ mm}^2 < S \leq 35 \text{ mm}^2 \Rightarrow S_{PE} = 16 \text{ mm}^2$
$35 \text{ mm}^2 < S \leq 400 \text{ mm}^2 \Rightarrow S_{PE} = S/2$
$400 \text{ mm}^2 < S \leq 800 \text{ mm}^2 \Rightarrow S_{PE} = 200 \text{ mm}^2$
$800 \text{ mm}^2 < S \Rightarrow S_{PE} = S/4$

TIPICO


B	TIPICO	14/06/24	G.A.D.
A	TIPICO	31/05/24	G.A.D.
REV.	DESCRIPCION	FECHA	NOMBRE
Proyecto: TABLERO INSTALADO FUERA DE SET.			
Ubicación:			
Plano: TB COS : TABLERO CORRECCION COSENO PHI – 500 kVar			
	Contenido: CARATULA		Dibujó: G.A.D.
	Proyecto: ARCOR S.A.I.C.		Colaboró: GMT–JAD
			Aprobó:
			Fecha: 31/05/24
		Escala	Hoja
00 – 00 – 0000 – EE – 000 – 01 – B		Sin Escala	1



1

Negocio	Planta	Proyecto	Area	Sector	Secuencia	Rev.
00	00	0000	EE	000	01	B

Recorrido:	31/05/24
Escala	Hoja
Sin Escala	2

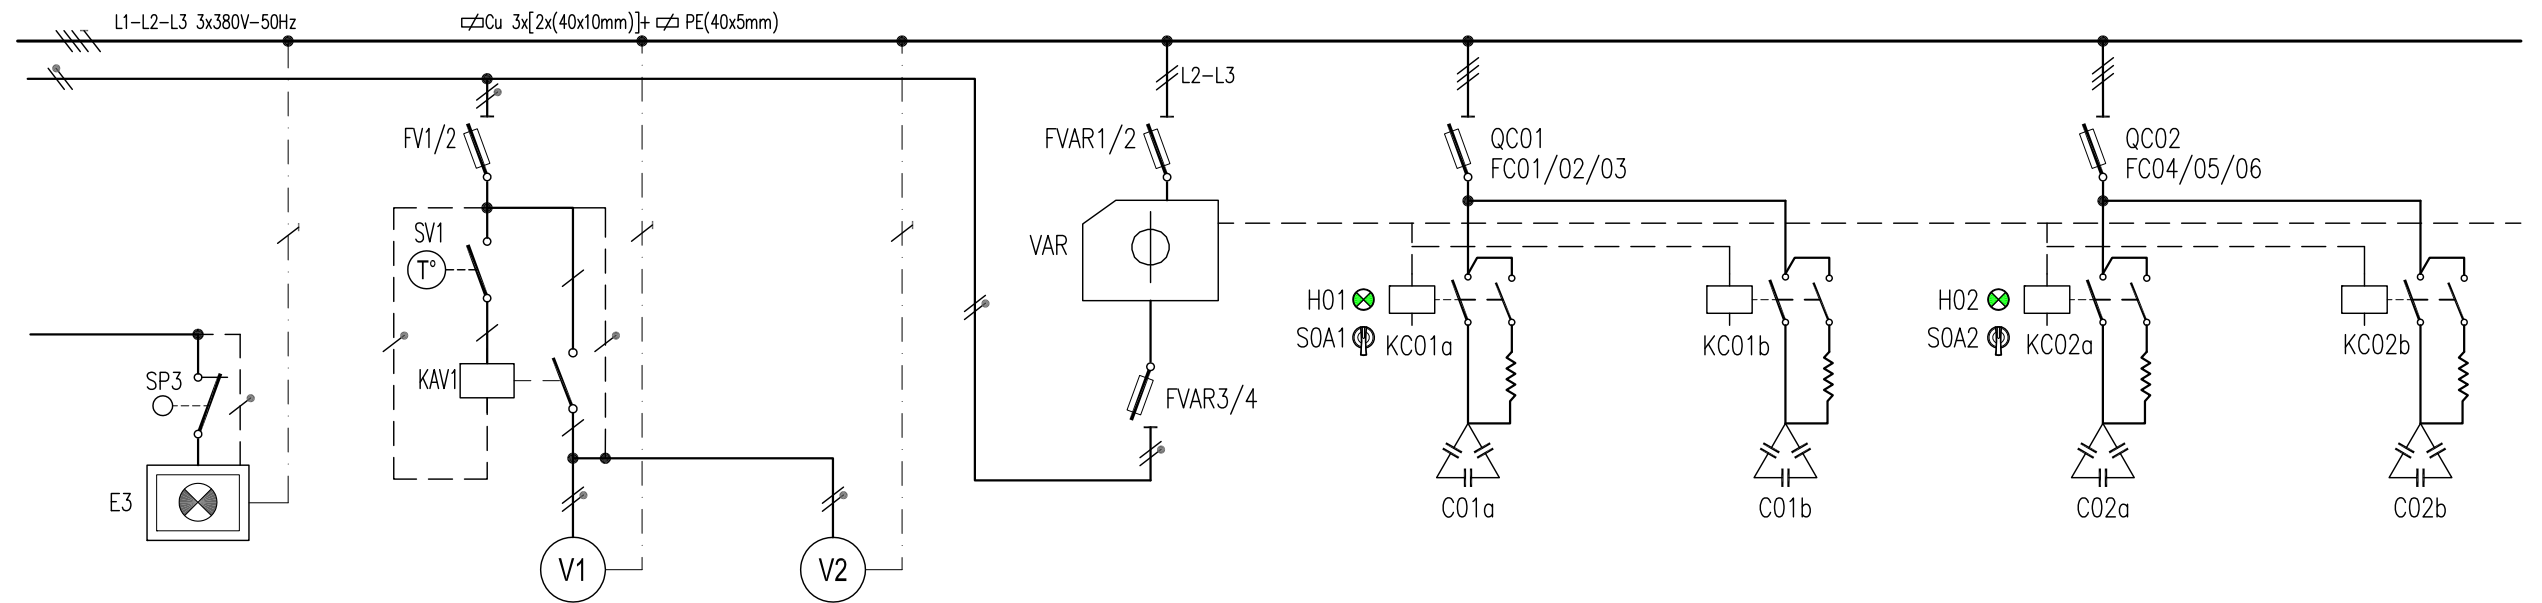[illegible]

Proyecto: **TABLERO INSTALADO FUERA DE SET.**
Ubicación:


Plano: TB COS : TABLERO CORRECCION COSENO PHI – 500 kVAr

Contenido: **ESQUEMA UNIFILAR**
Proyectó: **ARCOR SAIC**

Negocio	Planta	Proyecto	Area	Sector	Secuencia	Rev.
00	00	0000	EE	000	01	B

Dibujó:	G.A.D.
Colaboró:	GMT-JAD
Aprobó:	
Fecha:	31/05/24
Escala:	Hoja

Escala	Noja
Sin Escala	3

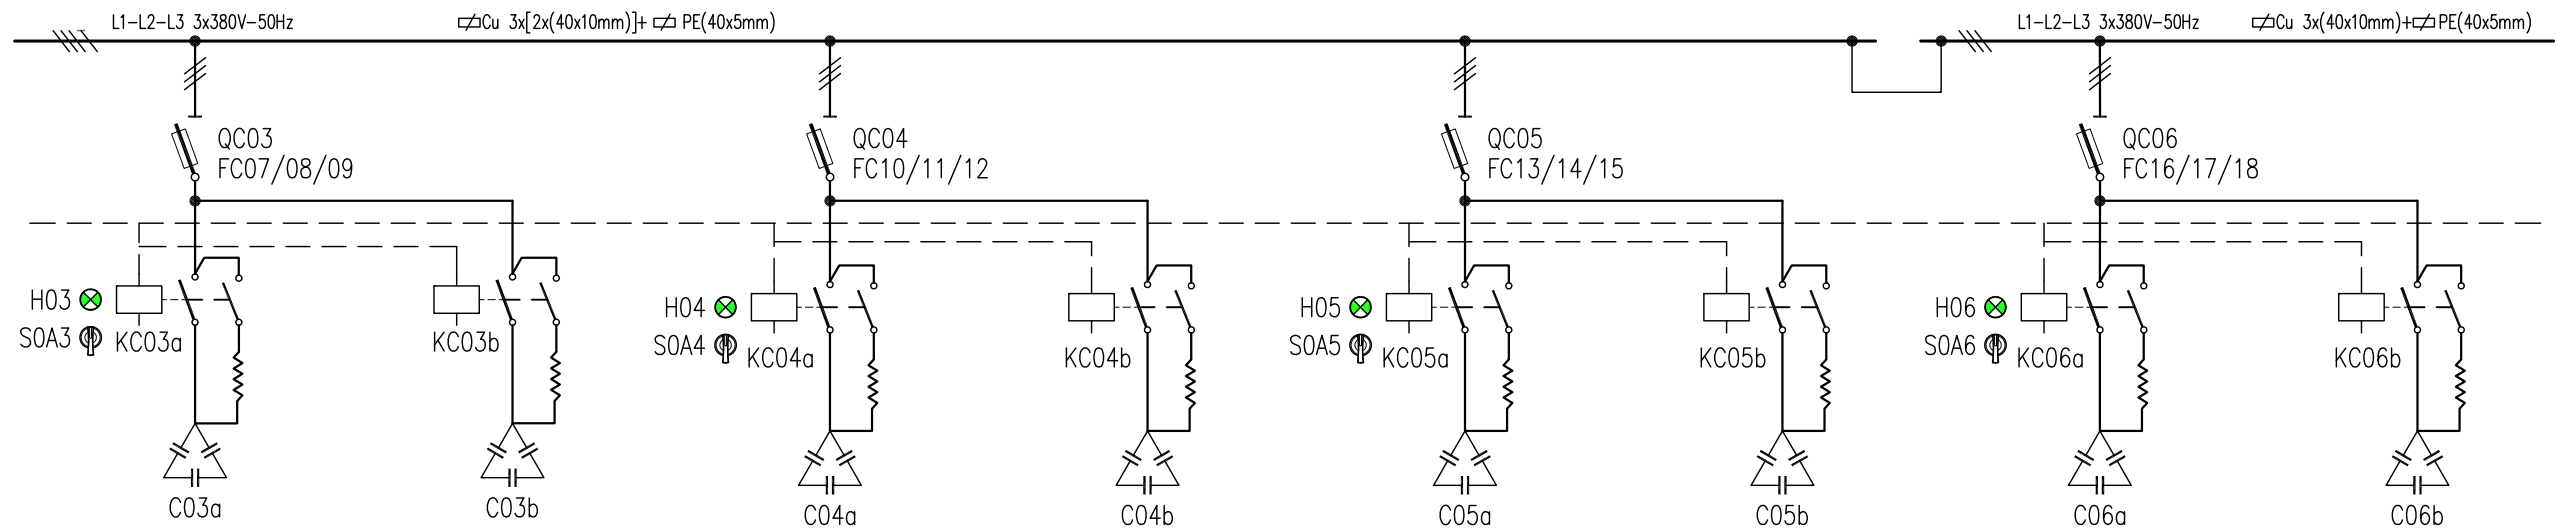[illegible]


Proyecto: **TABLERO INSTALADO FUERA DE SET.**
Ubicación:

Plano: TB COS : TABLERO CORRECCION COSENO PHI – 500 kVAr

Contenido: ESQUEMA UNIFILAR
Proyectó: ARCOR SAIC

Negocio	Planta	Proyecto	Area	Sector	Secuencia	Rev.
00	00	0000	EE	000	01	B

Dibujó:	G.A.D.	
Colaboró:	GMT-JAD	
Aprobó:		
Fecha:	31/05/24	
Escala	Hoja	
Sin Escala	1	

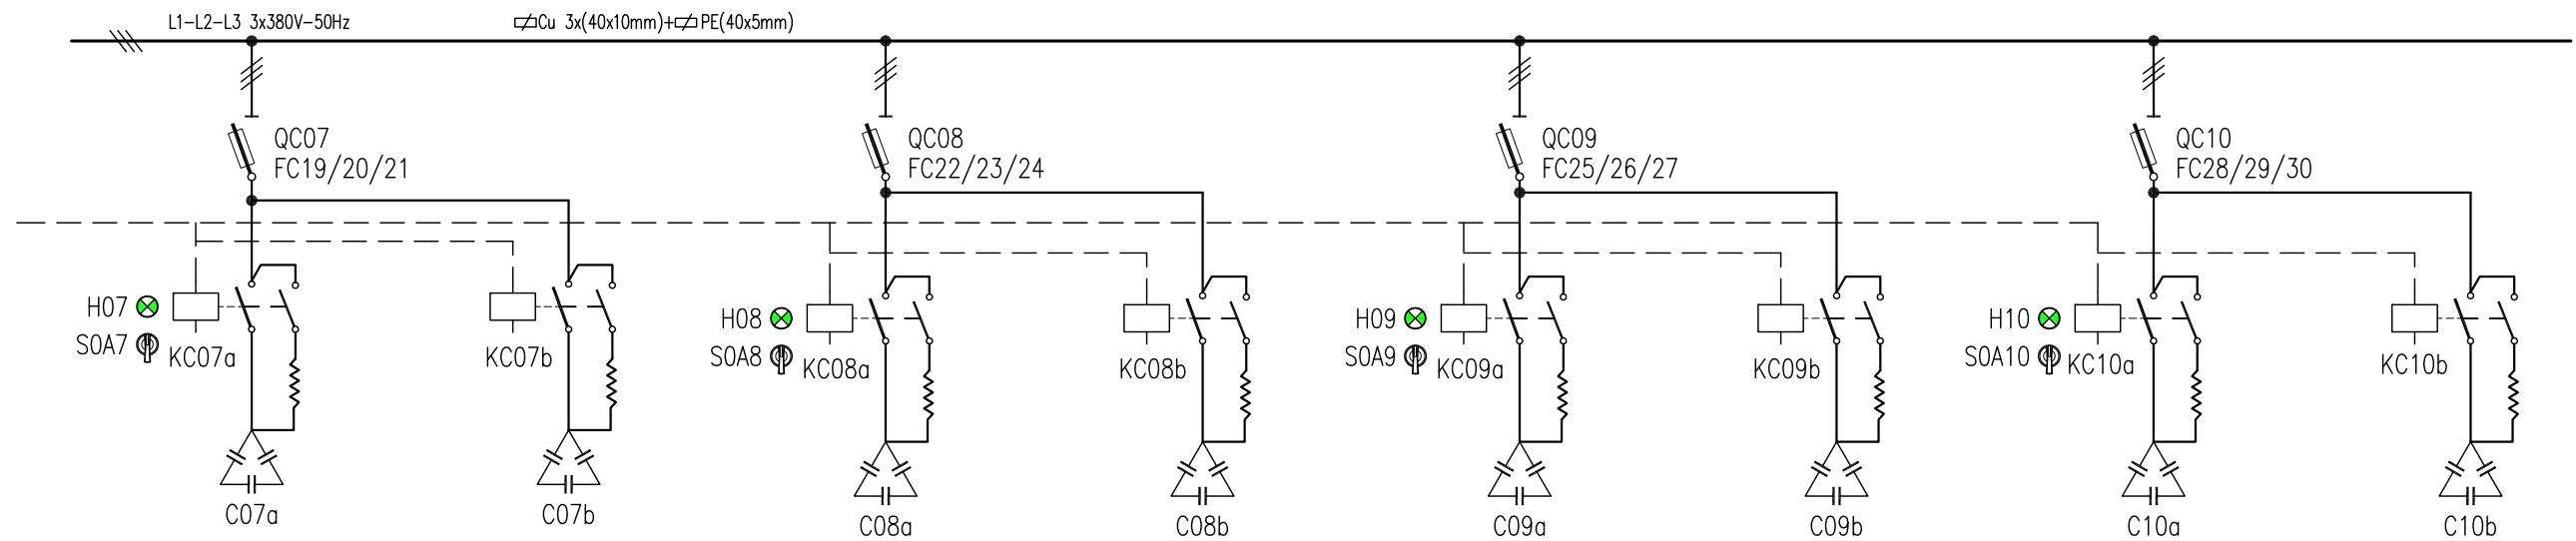[illegible]

Proyecto: **TABLERO INSTALADO FUERA DE SET.**
Ubicación:

Plano: TB COS : TABLERO CORRECCION COSENO PHI – 500 kVAr


Contenido: ESQUEMA UNIFILAR

Proyectó: **ARCOR SAIC**


Negocio	Planta	Proyecto	Area	Sector	Secuencia	Rev.
00	00	0000	EE	000	01	B

Dibujó:	G.A.D.
Colaboró:	GMT-JAD
Aprobó:	
Fecha:	31/05/24

Escala	Hoja
Sin Escala	5

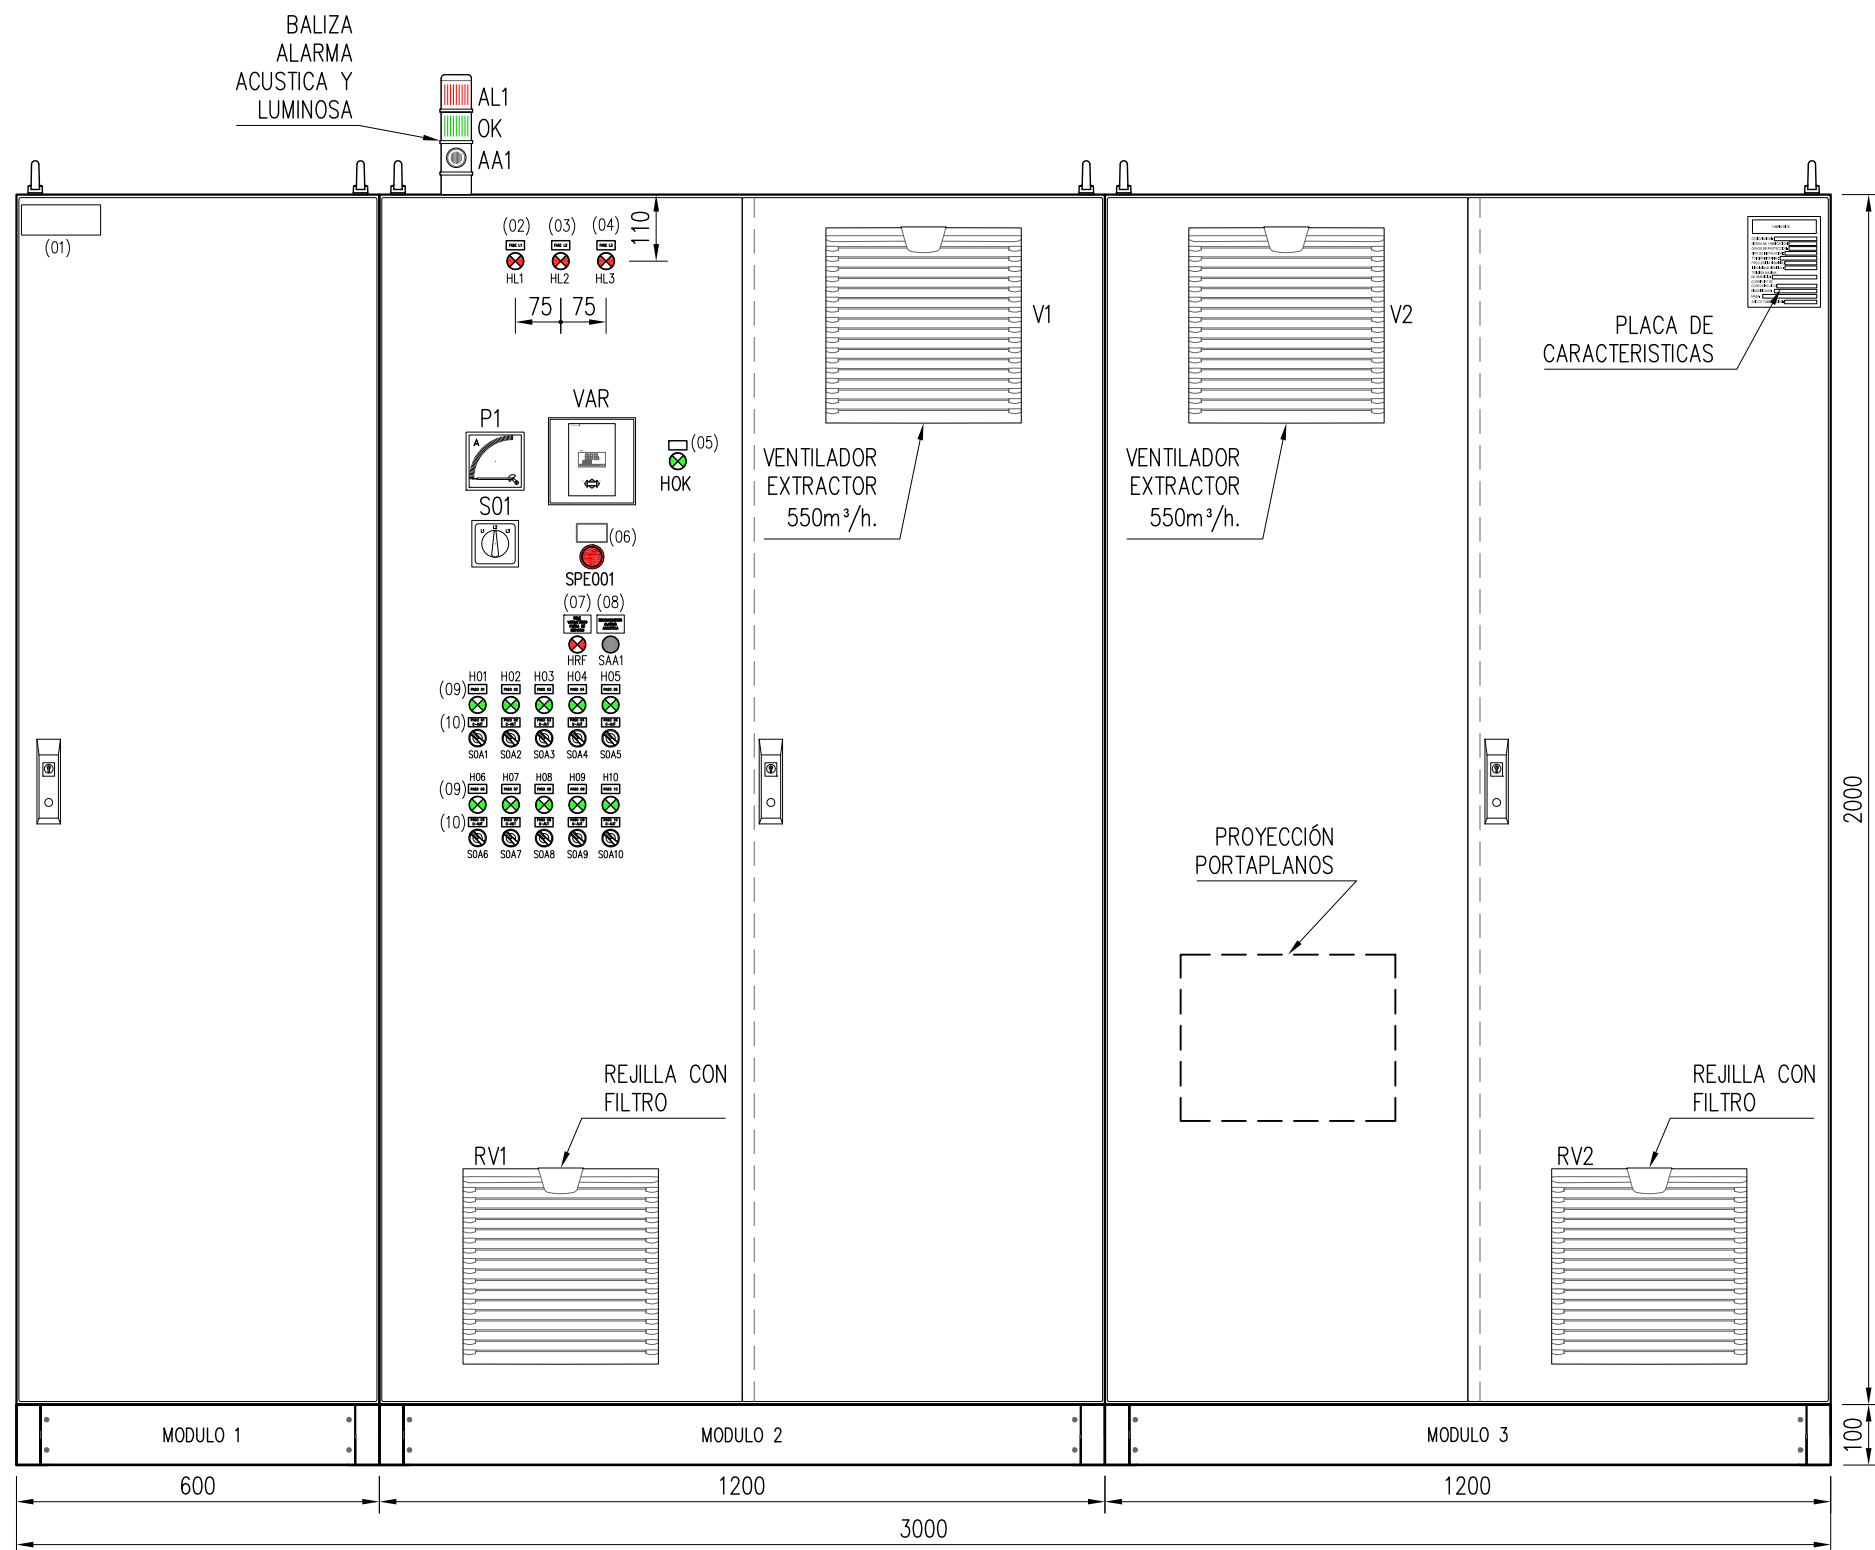

■ VISTA FRONTAL CON PUERTA

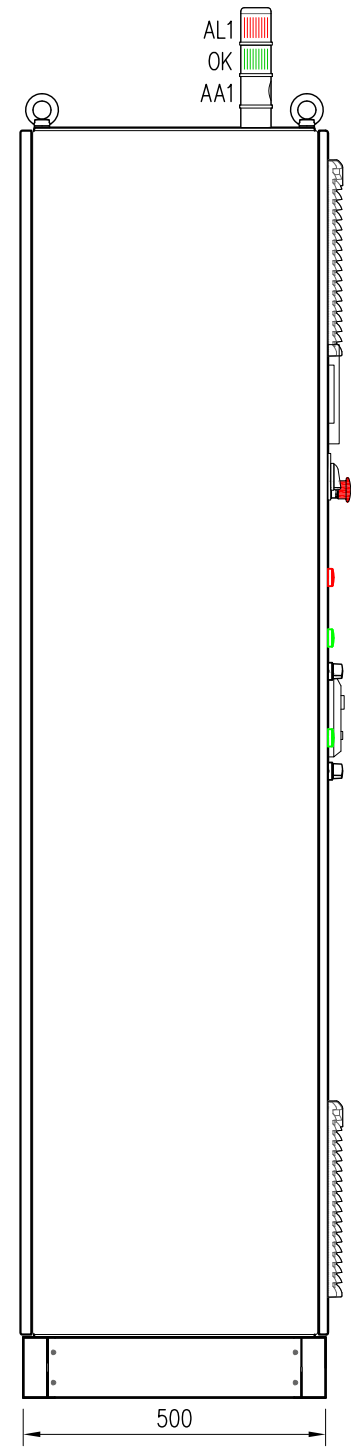

■ VISTA LATERAL

NOTAS:

- 1- VER DETALLE DE CARTELES INDICADORES EN HOJA 10.
- 2- VER DETALLE DE PLACA DE CARACTERISTICAS EN HOJA 11.



Proyecto: **TABLERO INSTALADO FUERA DE SET.**


Ubicación: **TB COS : TABLERO CORRECCION COSENO PHI - 500 kVar**

Contenido: ESQUEMA TOPOGRAFICO

Proyectó: ARCOR SAIC

Negocio	Planta	Proyecto	Area	Sector	Secuencia	Rev.
00	00	0000	EE	000	01	B

Dibujó:	G.A.D.
Colaboró:	GMT-JAD
Aprobó:	
Fecha:	31/05/24
Escala	Hoja
Sin Escala	6

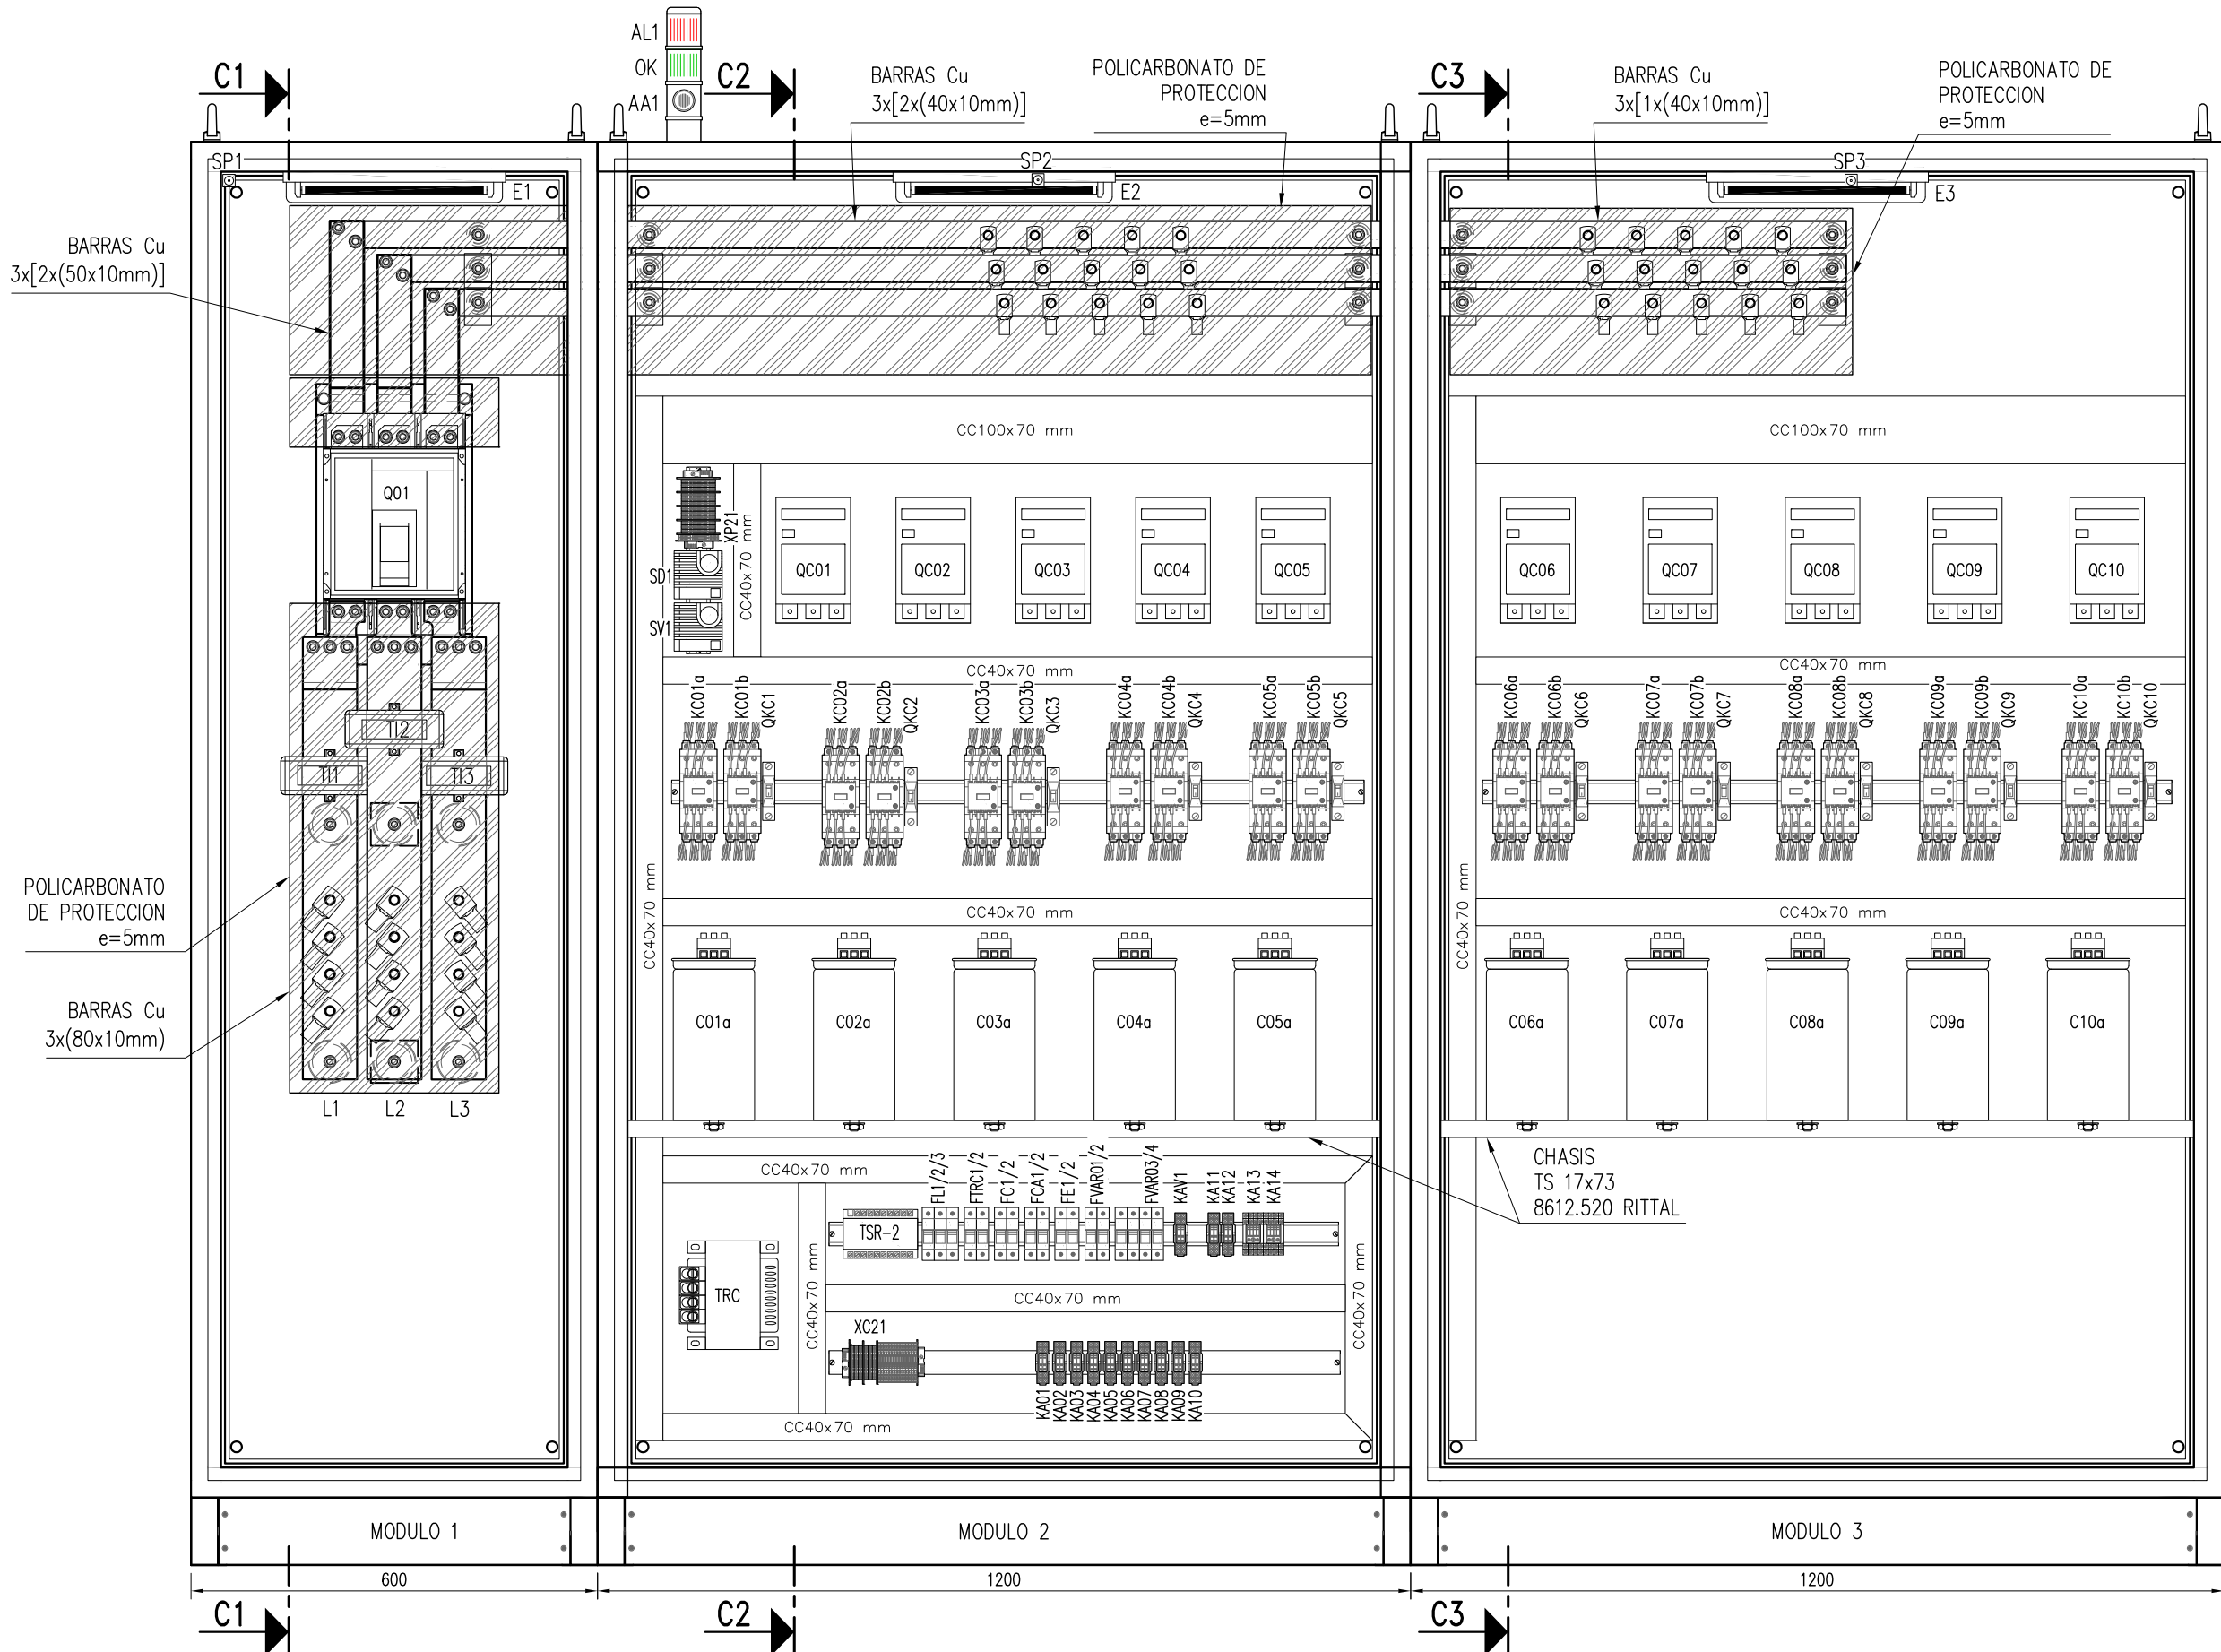


■ VISTA FRONTAL SIN PUERTA



Proyecto: **TABLERO INSTALADO FUERA DE SET.**
Ubicación:
Plano: TB COS : TABLERO CORRECCION COSENO PHI – 500 kVar

Contenido: ESQUEMA TOPOGRAFICO
Proyecto: ARCOR SAIC
Negocio Planta Proyecto Area Sector Secuencia Rev.
00 – 00 – 0000 – EE – 000 – 01 – B

Dibujó:	G.A.D.
Colaboró:	GMT-JAD
Aprobó:	
Fecha:	31/05/24
Escala	Hoja
Sin Escala	7

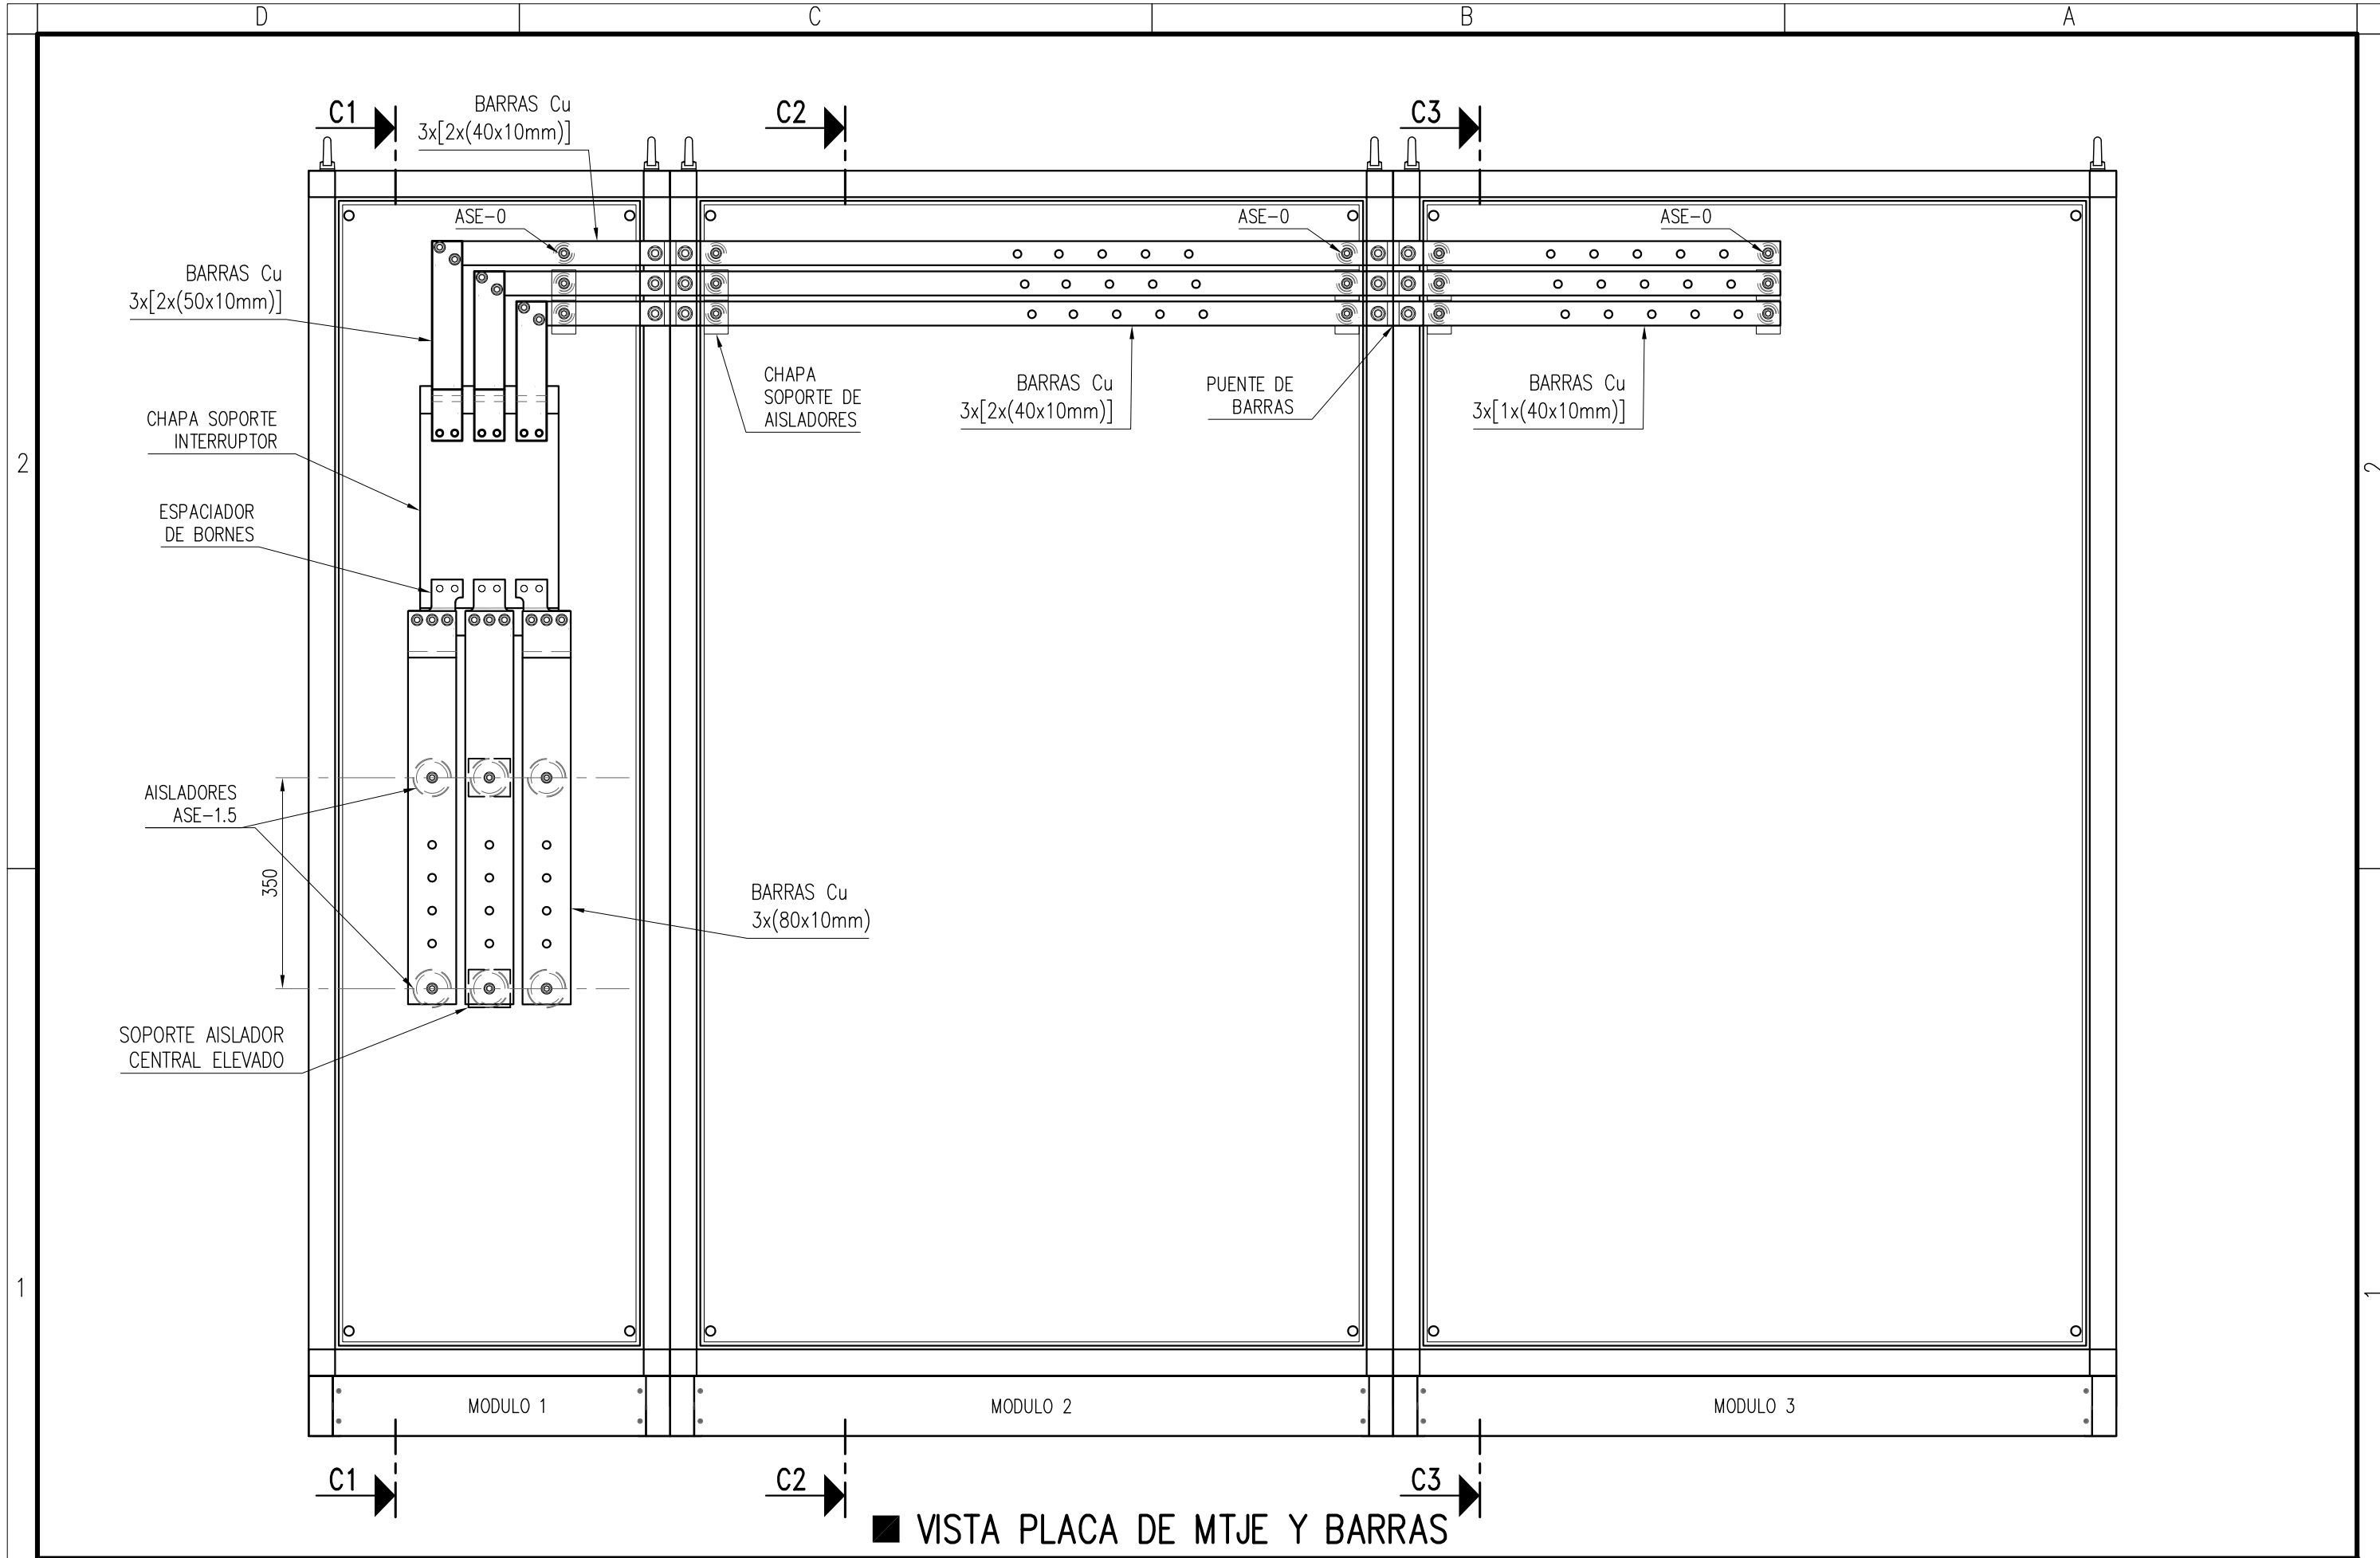

■ VISTA PLACA DE MTJE Y BARRAS



Proyecto: **TABLERO INSTALADO FUERA DE SET.**

Ubicación:

Plano: TB COS : TABLERO CORRECCION COSENO PHI – 500 kVAr




Contenido: ESQUEMA TOPOGRAFICO

Proyectó: ARCOR SAIC

Negocio	Planta	Proyecto	Area	Sector	Secuencia	Rev.
00	00	0000	EE	000	01	B

Dibujó:	G.A.D.
Colaboró:	GMT-JAD
Aprobó:	
Fecha:	31/05/24

Escala	Hoja
Sin Escala	8

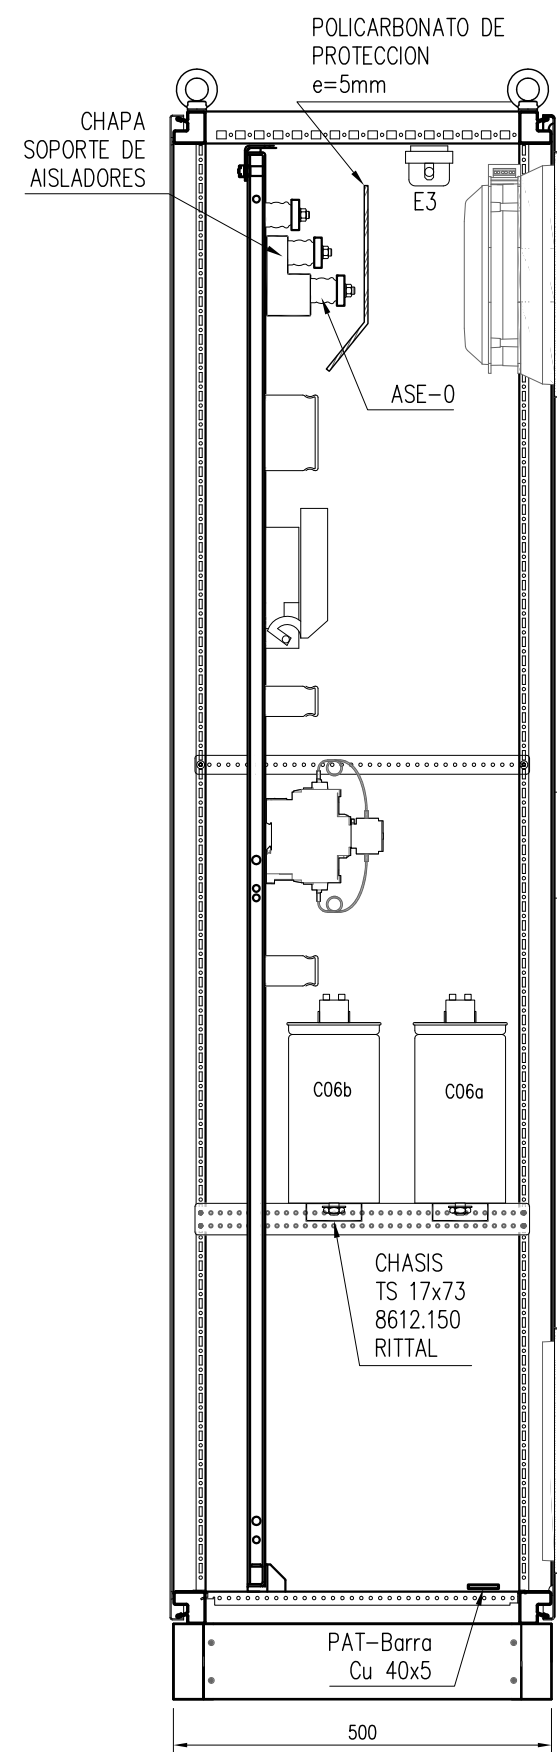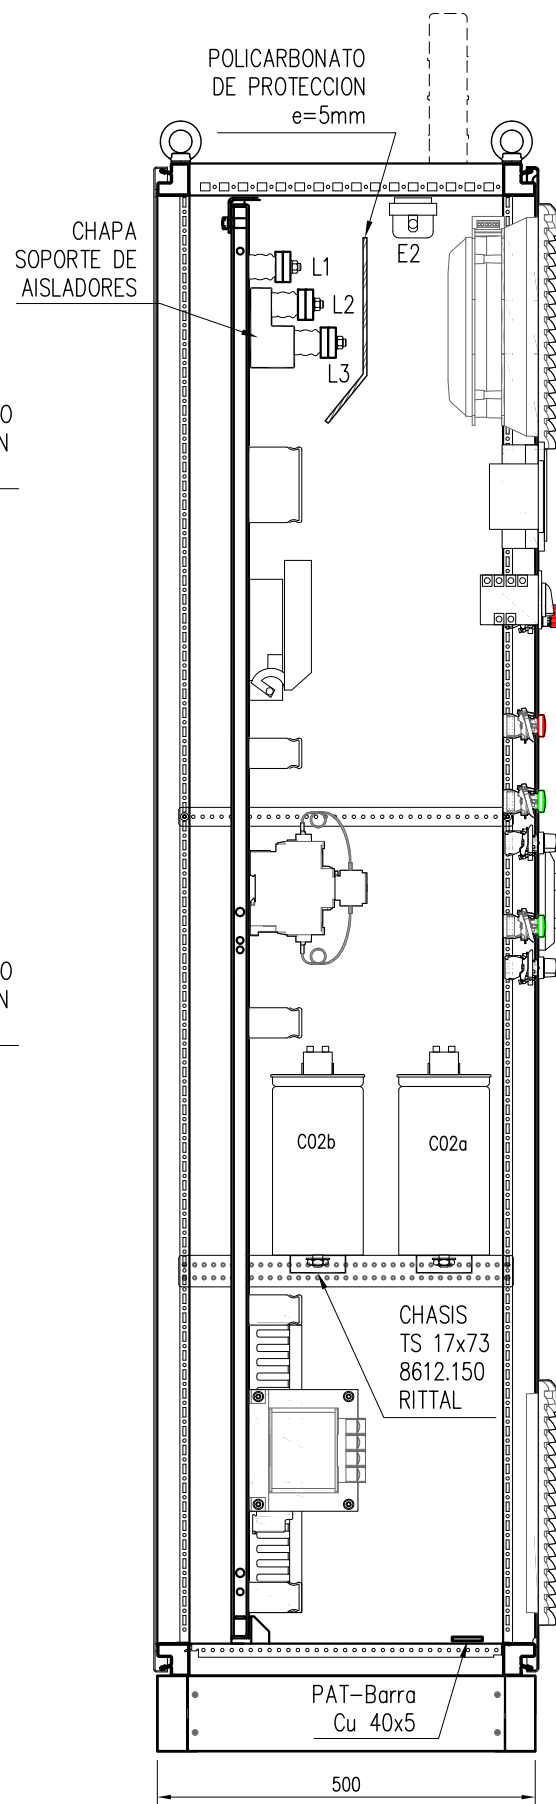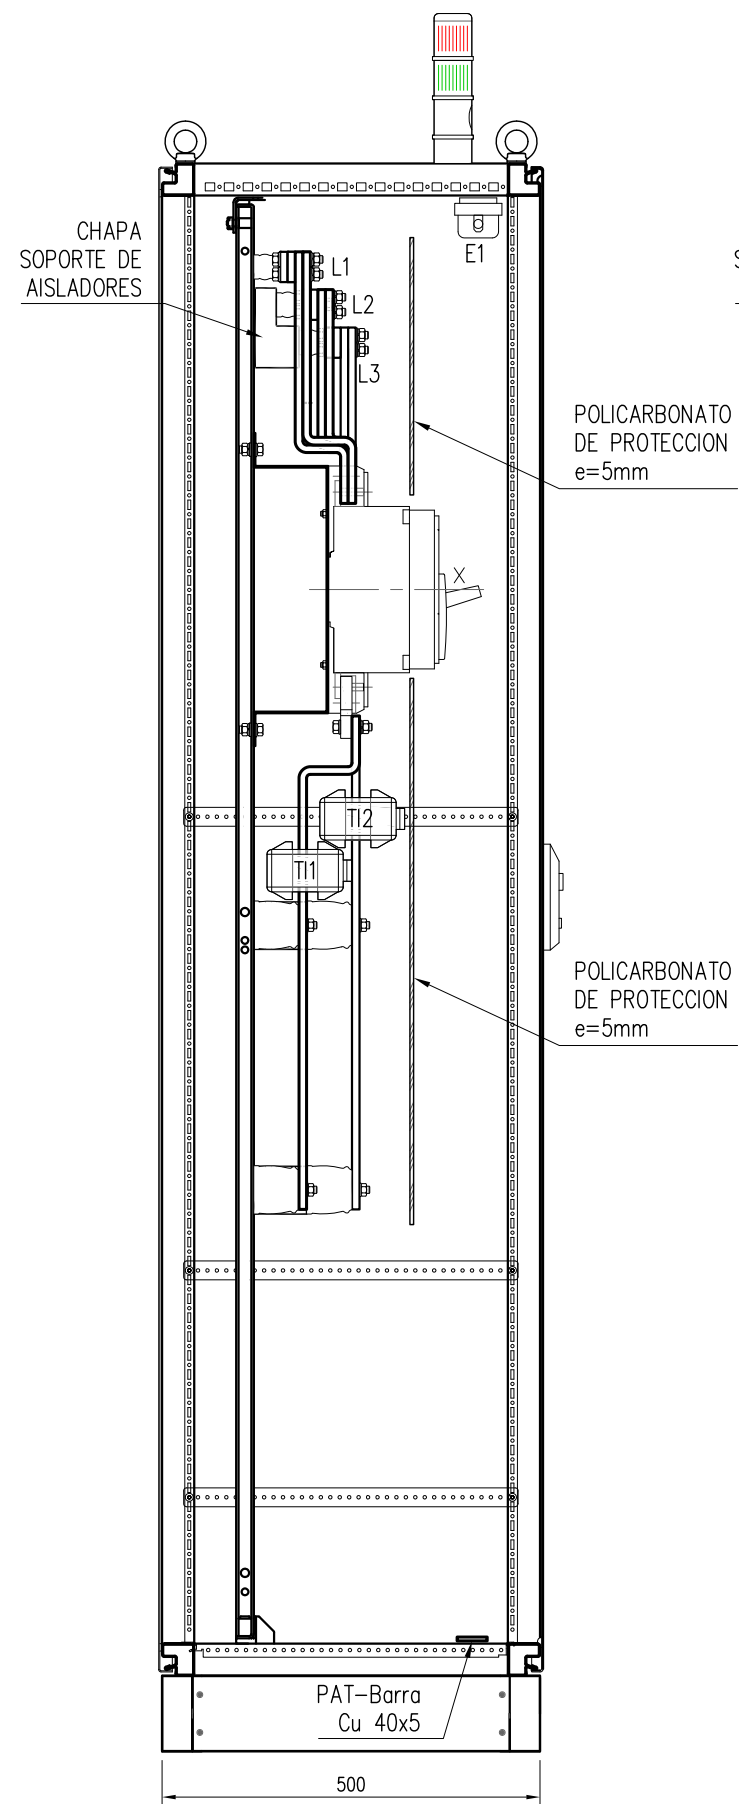Proyecto: **TABLERO INSTALADO FUERA DE SET.**

Ubicación:

Plano: TB COS : TABLERO CORRECCION COSENO PHI - 500 kVAr

Contenido: ESQUEMA TOPOGRAFICO

Proyector: ARCOR SAIC








Negocio	Planta	Proyecto	Area	Sector	Secuencia	Rev.
---------	--------	----------	------	--------	-----------	------

00-00-0000-EE-000-01-B


Dibujó:	G.A.D.
Colaboró:	GMT-JAD
Aprobó:	
Fecha:	31/05/24

Fecha:	31/03/24
Escala	Hoja

Sin Escala	9
------------	---

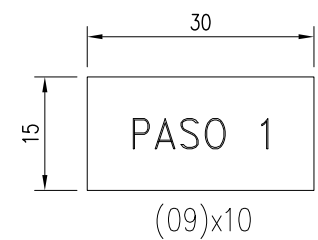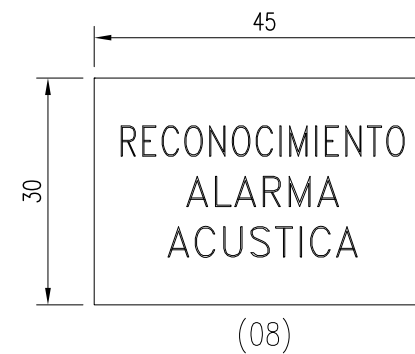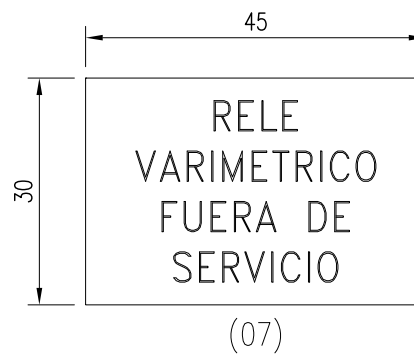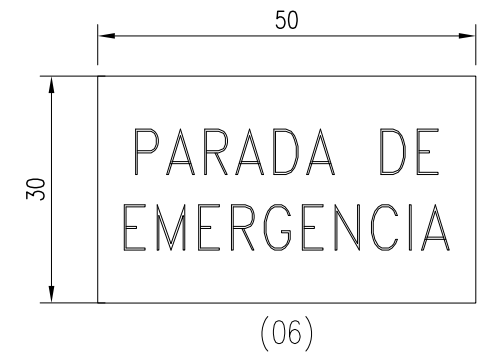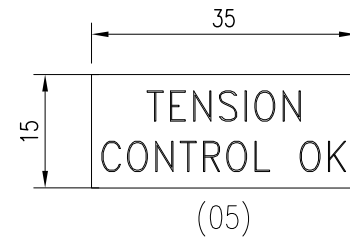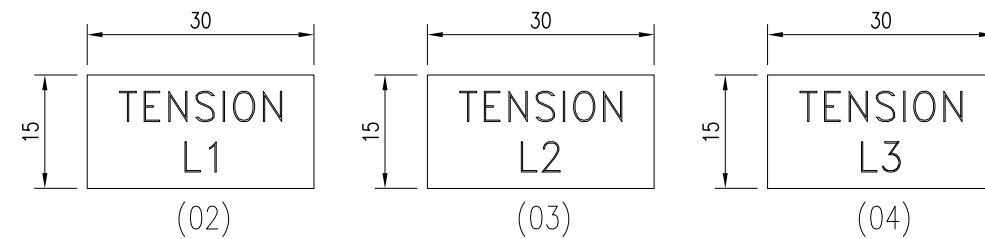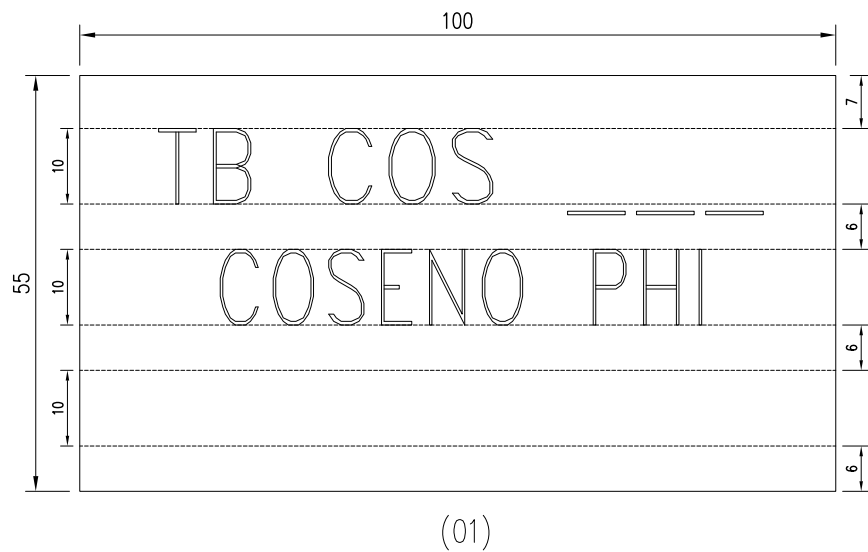

HACER 1 POR CADA PASO

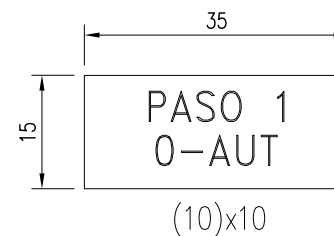

HACER 1 POR CADA PASO

ESPECIFICACIONES:

MATERIAL: POLICARBONATO.
ESPESOR: 3mm
FONDO: BLANCO.
LETRAS: NEGRAS.
ALTURA LETRAS: 4mm / 6mm / 10mm.
FIJACION: ADHESIVO DE SILICONA.

NOTA:

– CONSIDERAR ADEMAS, LA CARTELERIA DE IDENTIFICACION DE TODOS LOS ELEMENTOS Y LLAVES INTERIORES DEL TABLERO.



Proyecto: **TABLERO INSTALADO FUERA DE SET.**
Ubicación:
Plano: TB COS : TABLERO CORRECCION COSENO PHI – 500 kVar

Contenido: CARTELERIA
Proyectó: ARCOR SAIC

Negocio	Planta	Proyecto	Area	Sector	Secuencia	Rev.
00	00	0000	EE	000	01	B

Dibujó:	G.A.D.
Colaboró:	GMT-JAD
Aprobó:	
Fecha:	31/05/24
Escala	Hoja
Sin Escala	10

	D	C	B	A	
2	FABRICANTE DESIGNACION: NORMA DE FABRICACIÓN: GRADO DE PROTECCIÓN: TIPO DE INSTALACION: TENSIÓN NOMINAL: FRECUENCIA NOMINAL: POTENCIA NOMINAL: INTENSIDAD NOMINAL: TENSION MAXIMA DE SERVICIO: CORRIENTE DE CORTOCIRCUITO: DIMENSIONES: MASA: AÑO DE FABRICACIÓN: 150 <td>2</td>				2
	ESPECIFICACIONES: MATERIAL: ALUMINIO. DIMENSIONES: LAS INDICADAS SON SUGERIDAS. NORMA: IRAM 2181. FIJACION: POR TORNILLO O REMACHES. GRABADO DE DATOS: POR DEFORMACION EN FRIO. BAJO RELIEVE.				
	NOTA: LOS DATOS A GRABAR EN LA PLACA DE CARACTERISTICAS SON LOS ESTABLECIDOS POR LA NORMA IRAM 2181.				
1	120				1



Proyecto: **TABLERO INSTALADO FUERA DE SET.**

Ubicación:


Plano: TB COS : TABLERO CORRECCION COSENO PHI – 500 kVAr

Contenido: PLACA DE CARACTERISTICAS

Proyectó: ARCOR SAIC

Negocio	Planta	Proyecto	Area	Sector	Secuencia	Rev.
00 – 00 – 0000 – EE – 000 – 01 – B						

Dibujó:	G.A.D.
Colaboró:	GMT–JAD
Aprobó:	
Fecha:	31/05/24
Escala	Hoja
Sin Escala	11

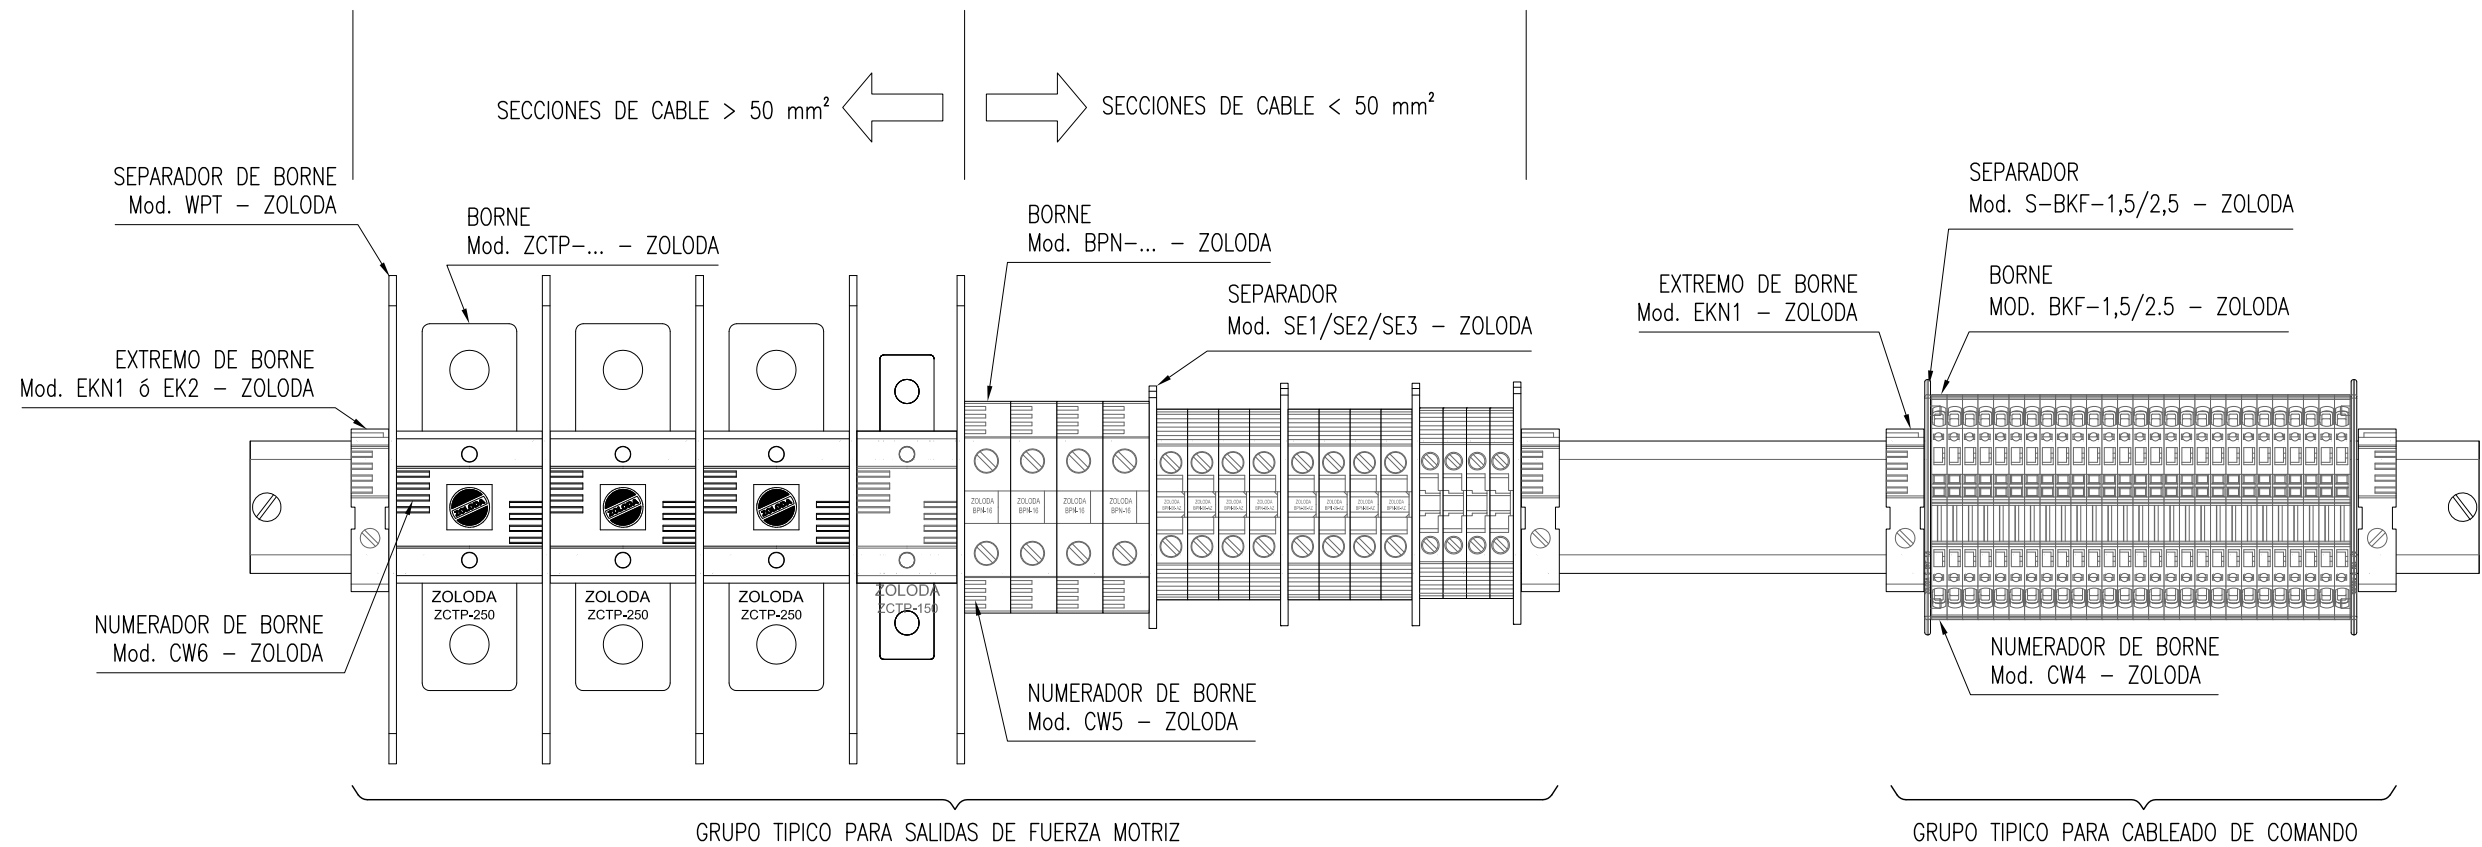


Proyecto: **TABLERO INSTALADO FUERA DE SET.**
Ubicación:
Plano: TB COS : TABLERO CORRECCION COSENO PHI - 500 kVAr

Contenido: TÍPICO CONEXIÓN BORNERAS DE FUERZA Y COMANDO
Proyectó: ARCOR SAIC

Negocio	Planta	Proyecto	Area	Sector	Secuencia	Rev.
00	00	0000	EE	000	01	B

Dibujó:	G.A.D.
Colaboró:	GMT-JAD
Aprobó:	
Fecha:	31/05/24
Escala	Hoja
Sin Escala	12

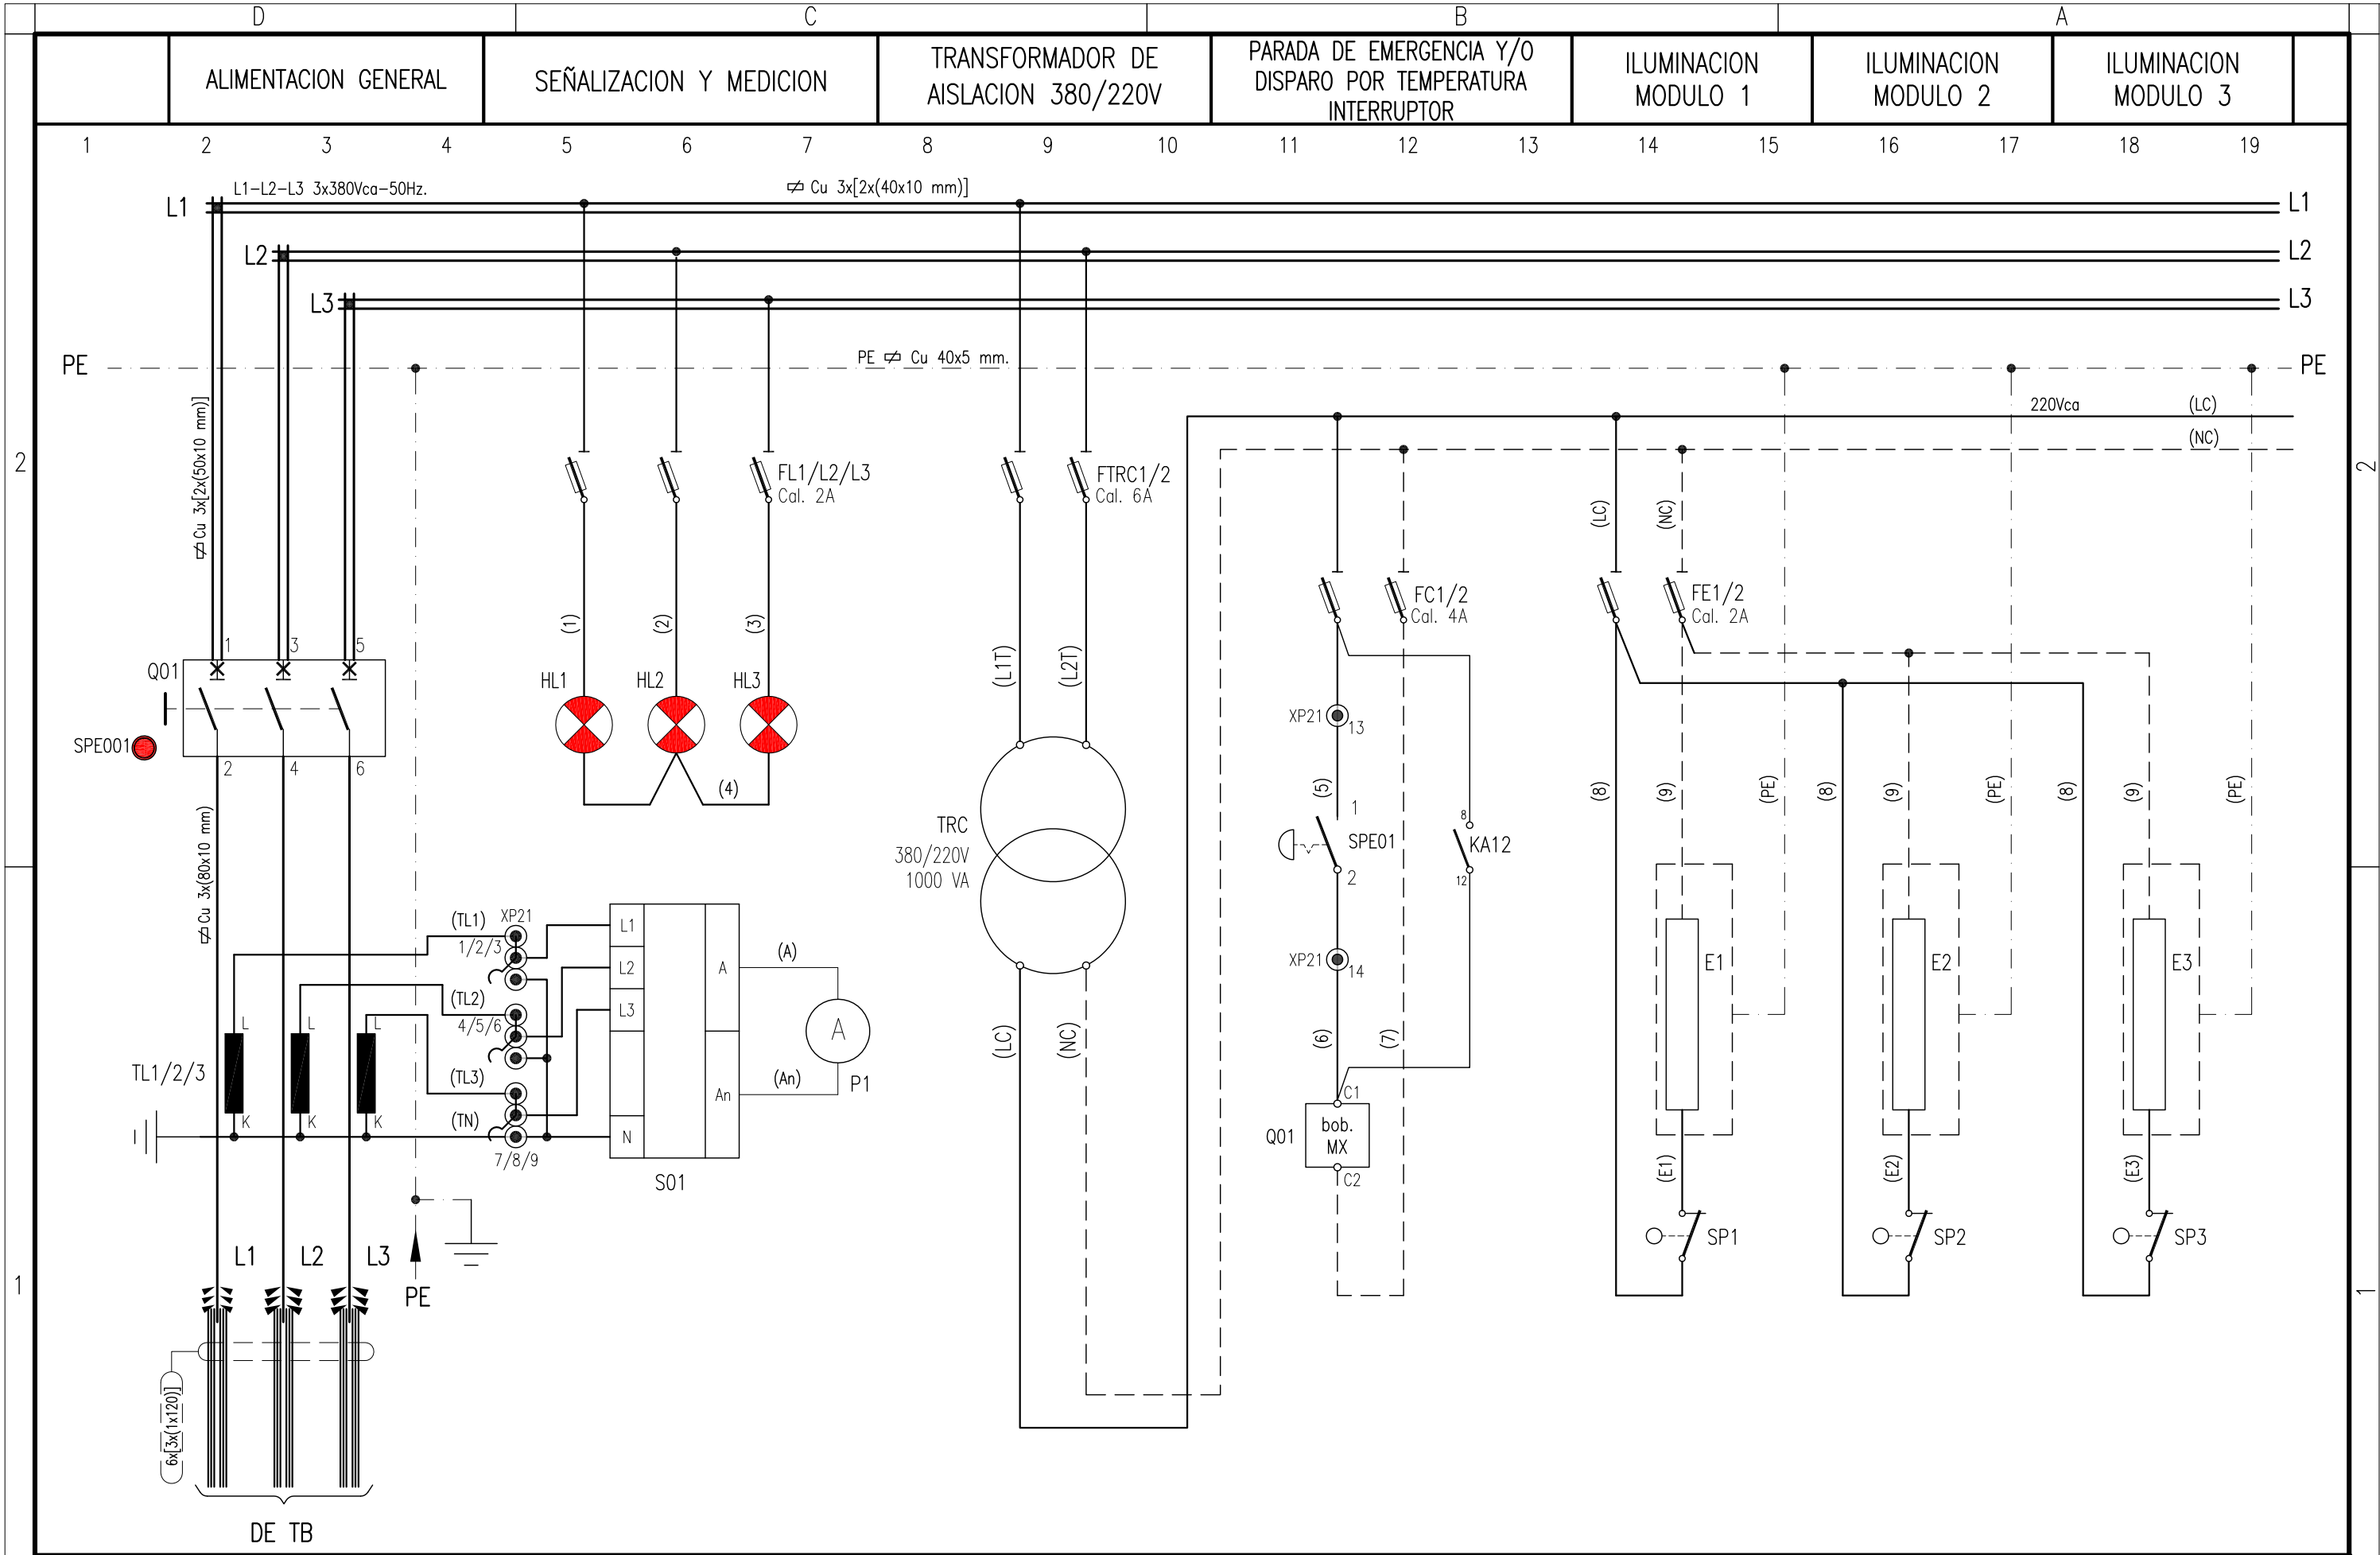


Proyecto: **TABLERO INSTALADO FUERA DE SET.**
Ubicación:
Plano: TB COS : TABLERO CORRECCION COSENO PHI – 500 kVar

Contenido: ESQUEMA FUNCIONAL
Proyecto: ARCOR SAIC

Negocio	Planta	Proyecto	Area	Sector	Secuencia	Rev.
00	00	0000	EE	000	01	B

Dibujó:	G.A.D.
Colaboró:	GMT-JAD
Aprobó:	
Fecha:	31/05/24
Escala	Hoja
Sin Escala	13

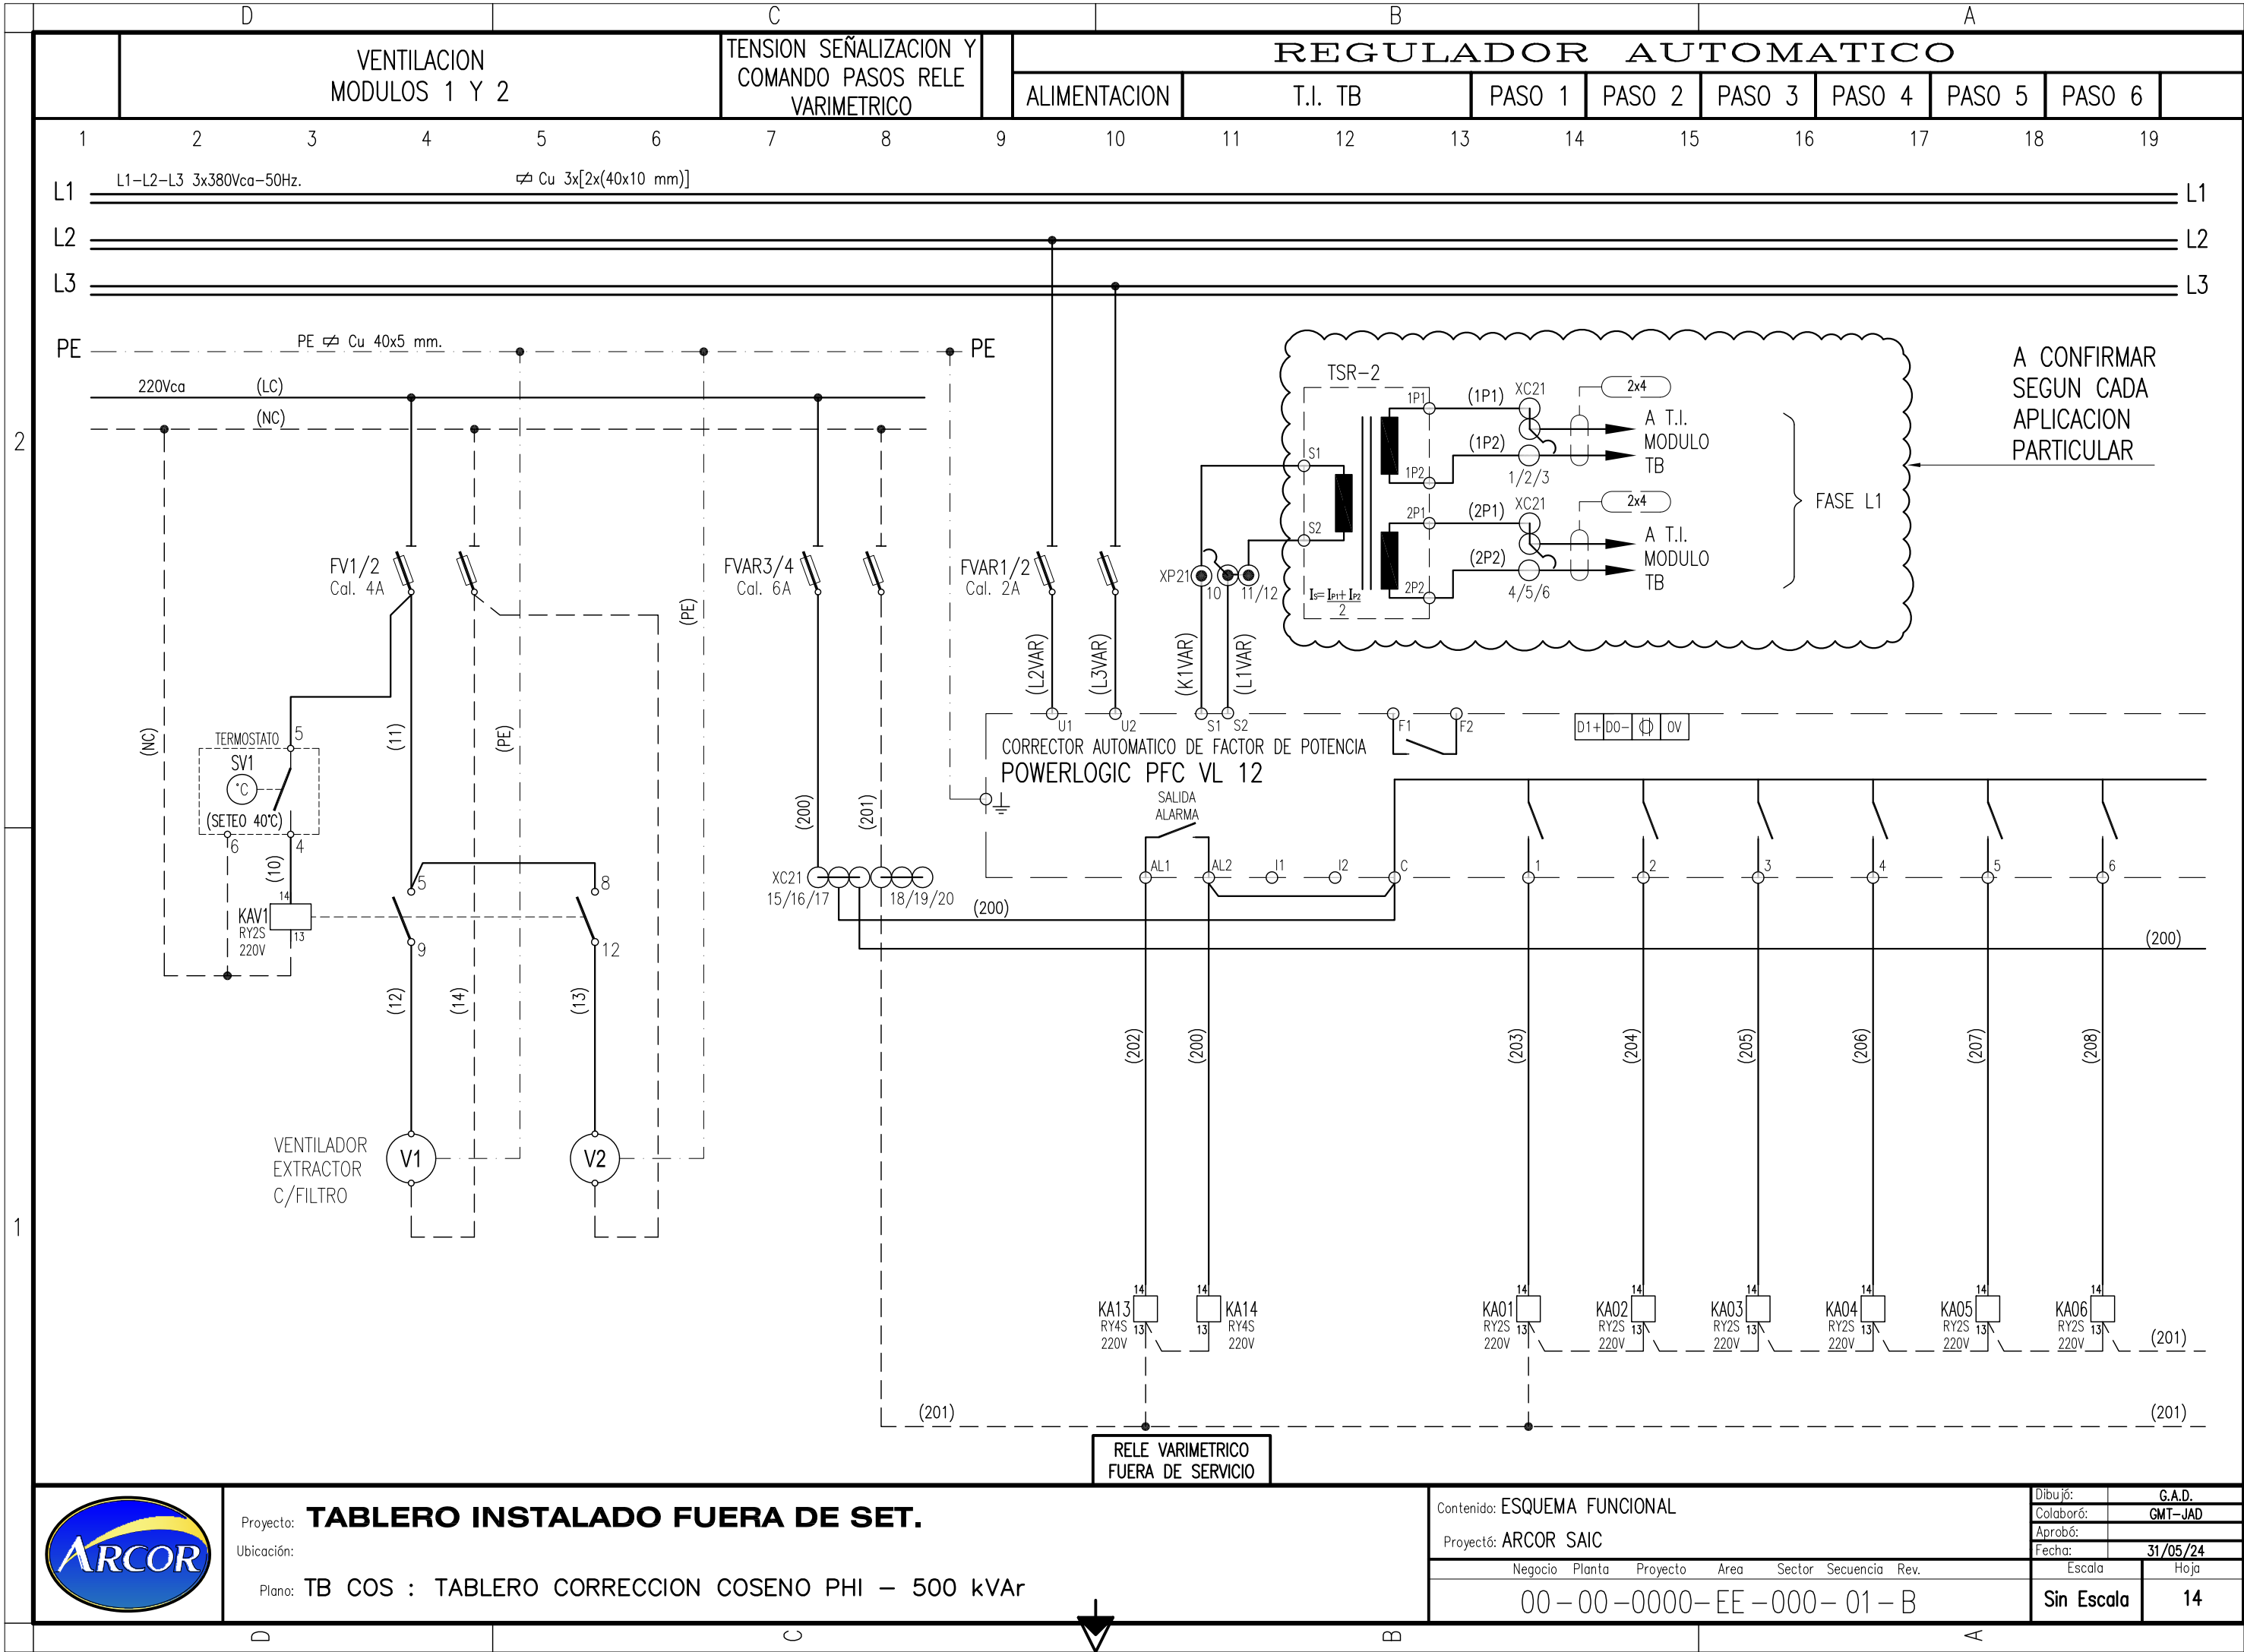

Proyecto: **TABLERO INSTALADO FUERA DE SET.**

Ubicación:


Plano: TB COS : TABLERO CORRECCION COSENO PHI – 500 kVar

Contenido: ESQUEMA FUNCIONAL

Proyectó: ARCOR SAIC

Negocio	Planta	Proyecto	Area	Sector	Secuencia	Rev.
00-00-0000-EE-000-01-B						

Dibujó:	G.A.D.
Colaboró:	GMT-JAD
Aprobó:	
Fecha:	31/05/24
Escala	Hoja
Sin Escala	14

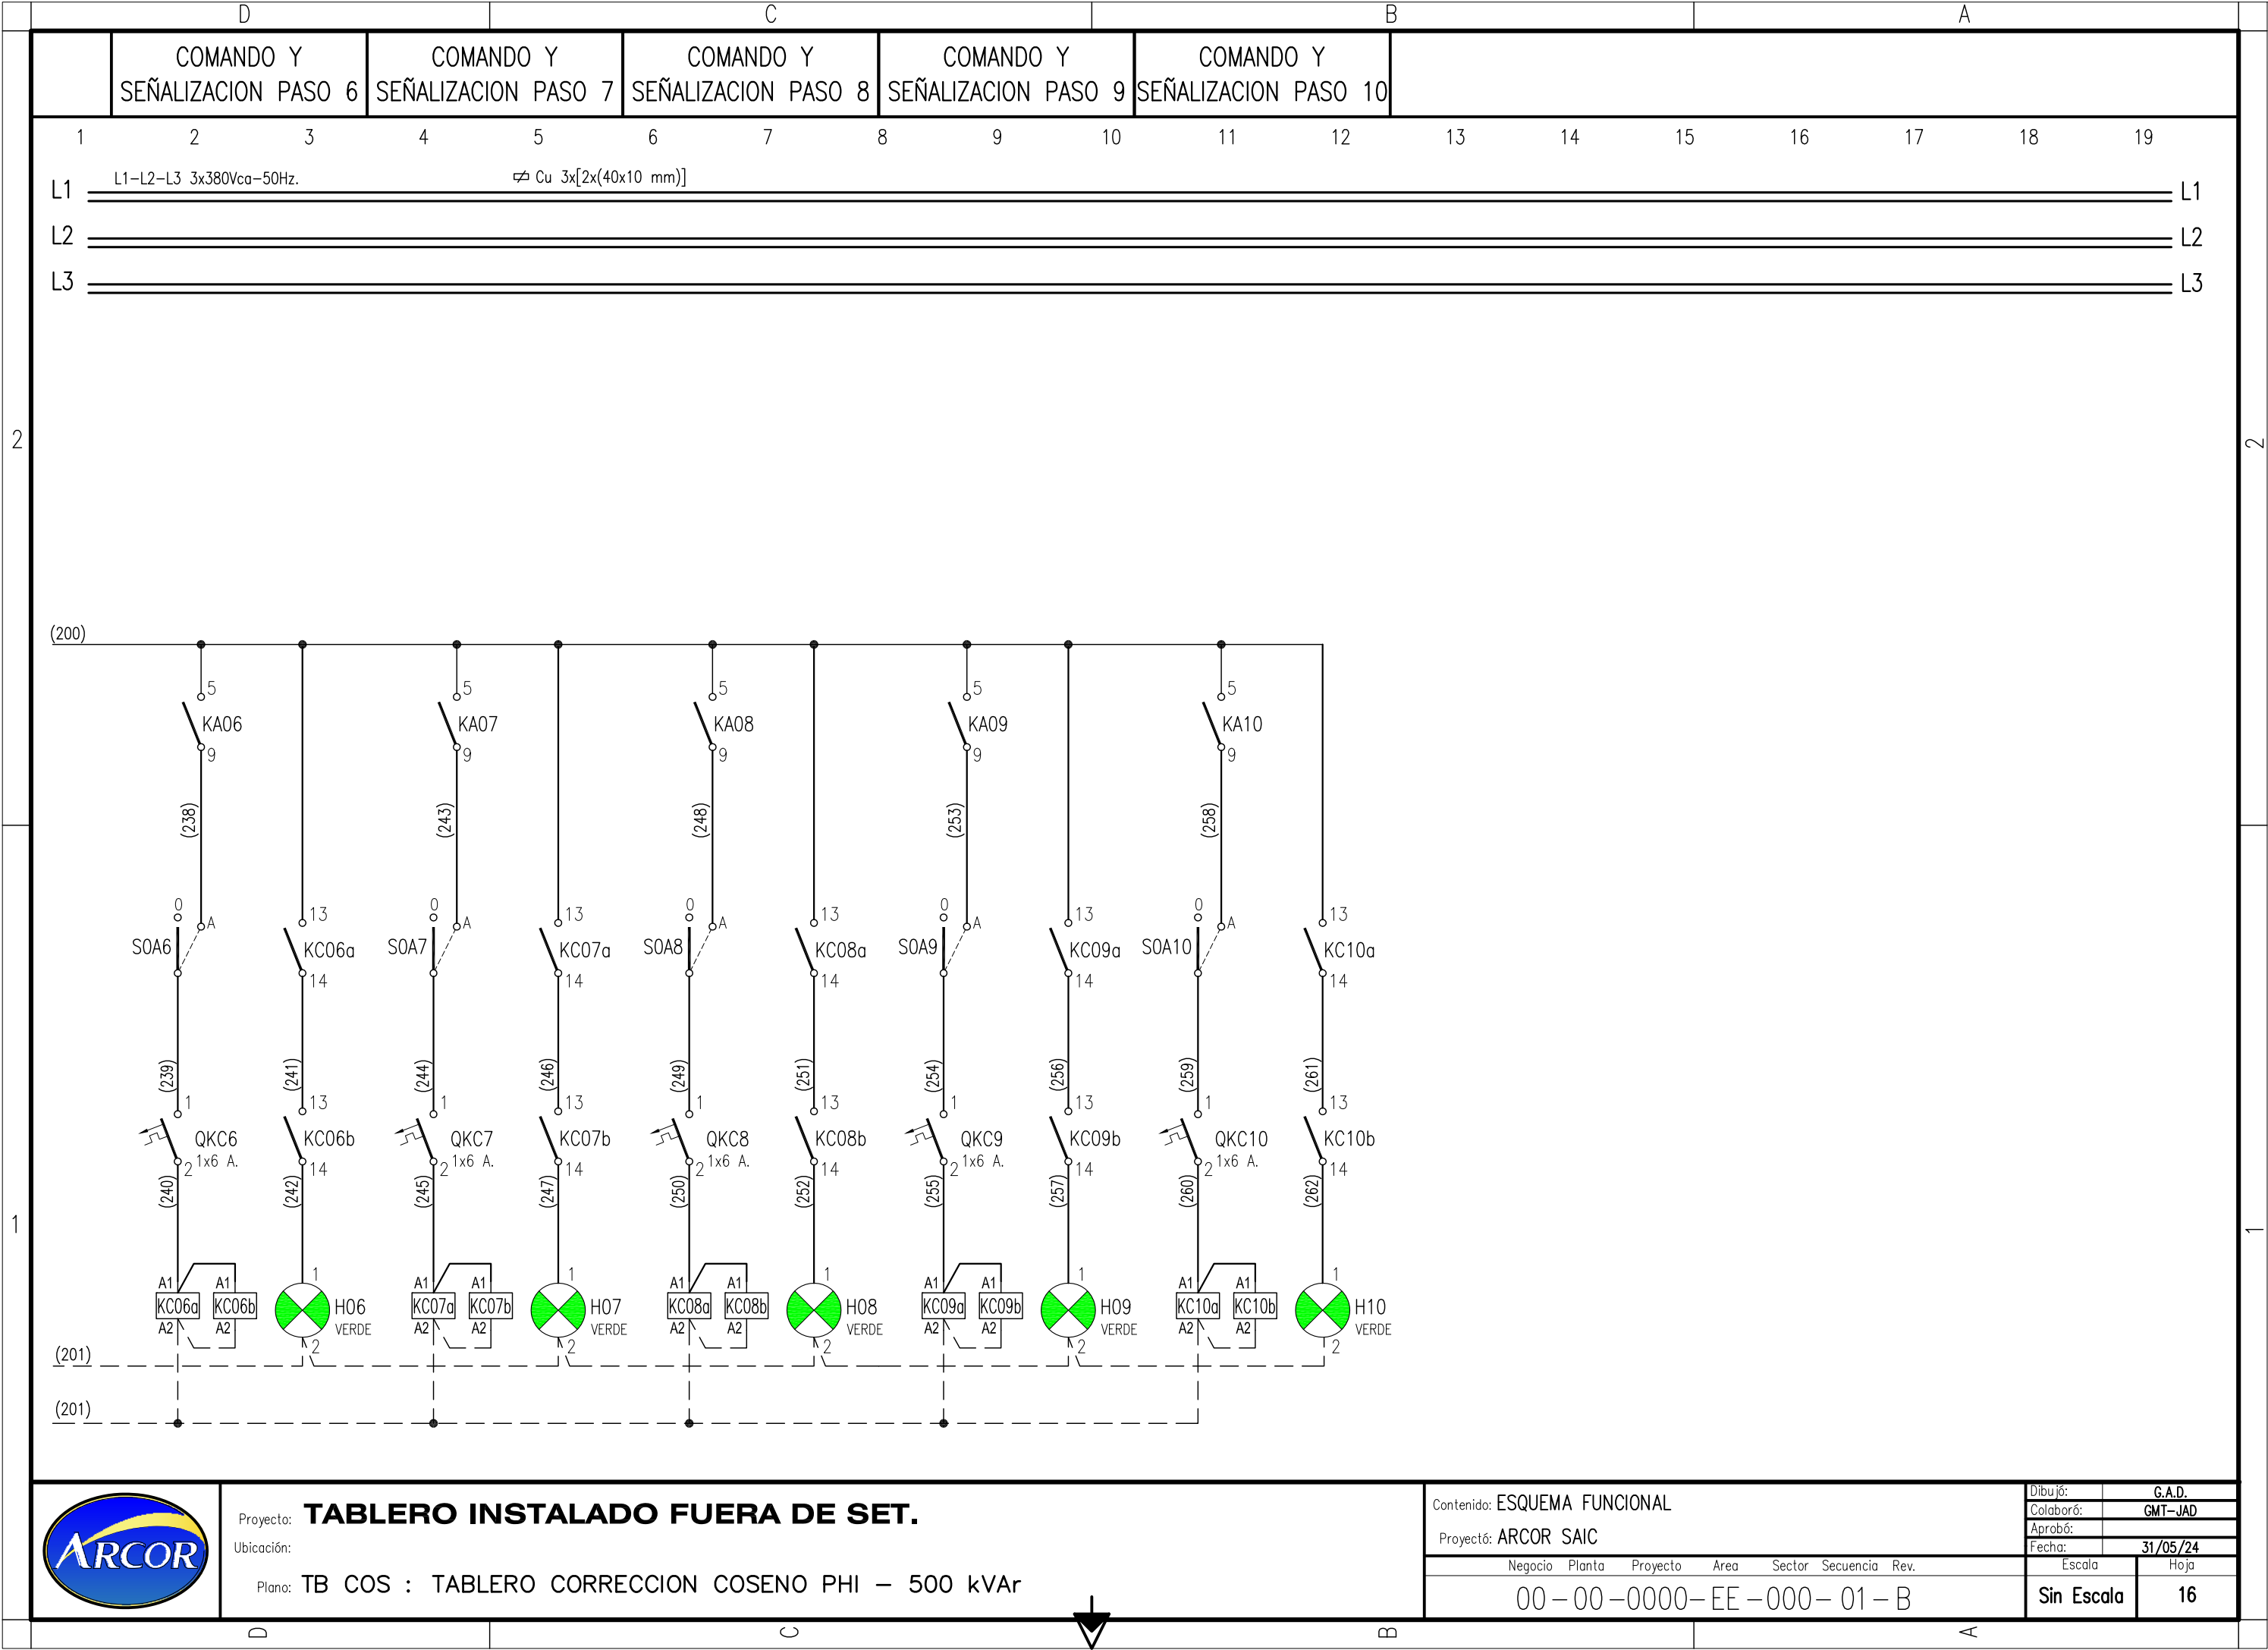

Proyecto: **TABLERO INSTALADO FUERA DE SET.**

Ubicación:


Plano: TB COS : TABLERO CORRECCION COSENO PHI – 500 kVar


Contenido: ESQUEMA FUNCIONAL

Proyectó: ARCOR SAIC

Negocio	Planta	Proyecto	Area	Sector	Secuencia	Rev.
00	00	0000	EE	000	01	B

Dibujó:	G.A.D.
Colaboró:	GMT-JAD
Aprobó:	
Fecha:	31/05/24
Escala	Hoja
Sin Escala	16

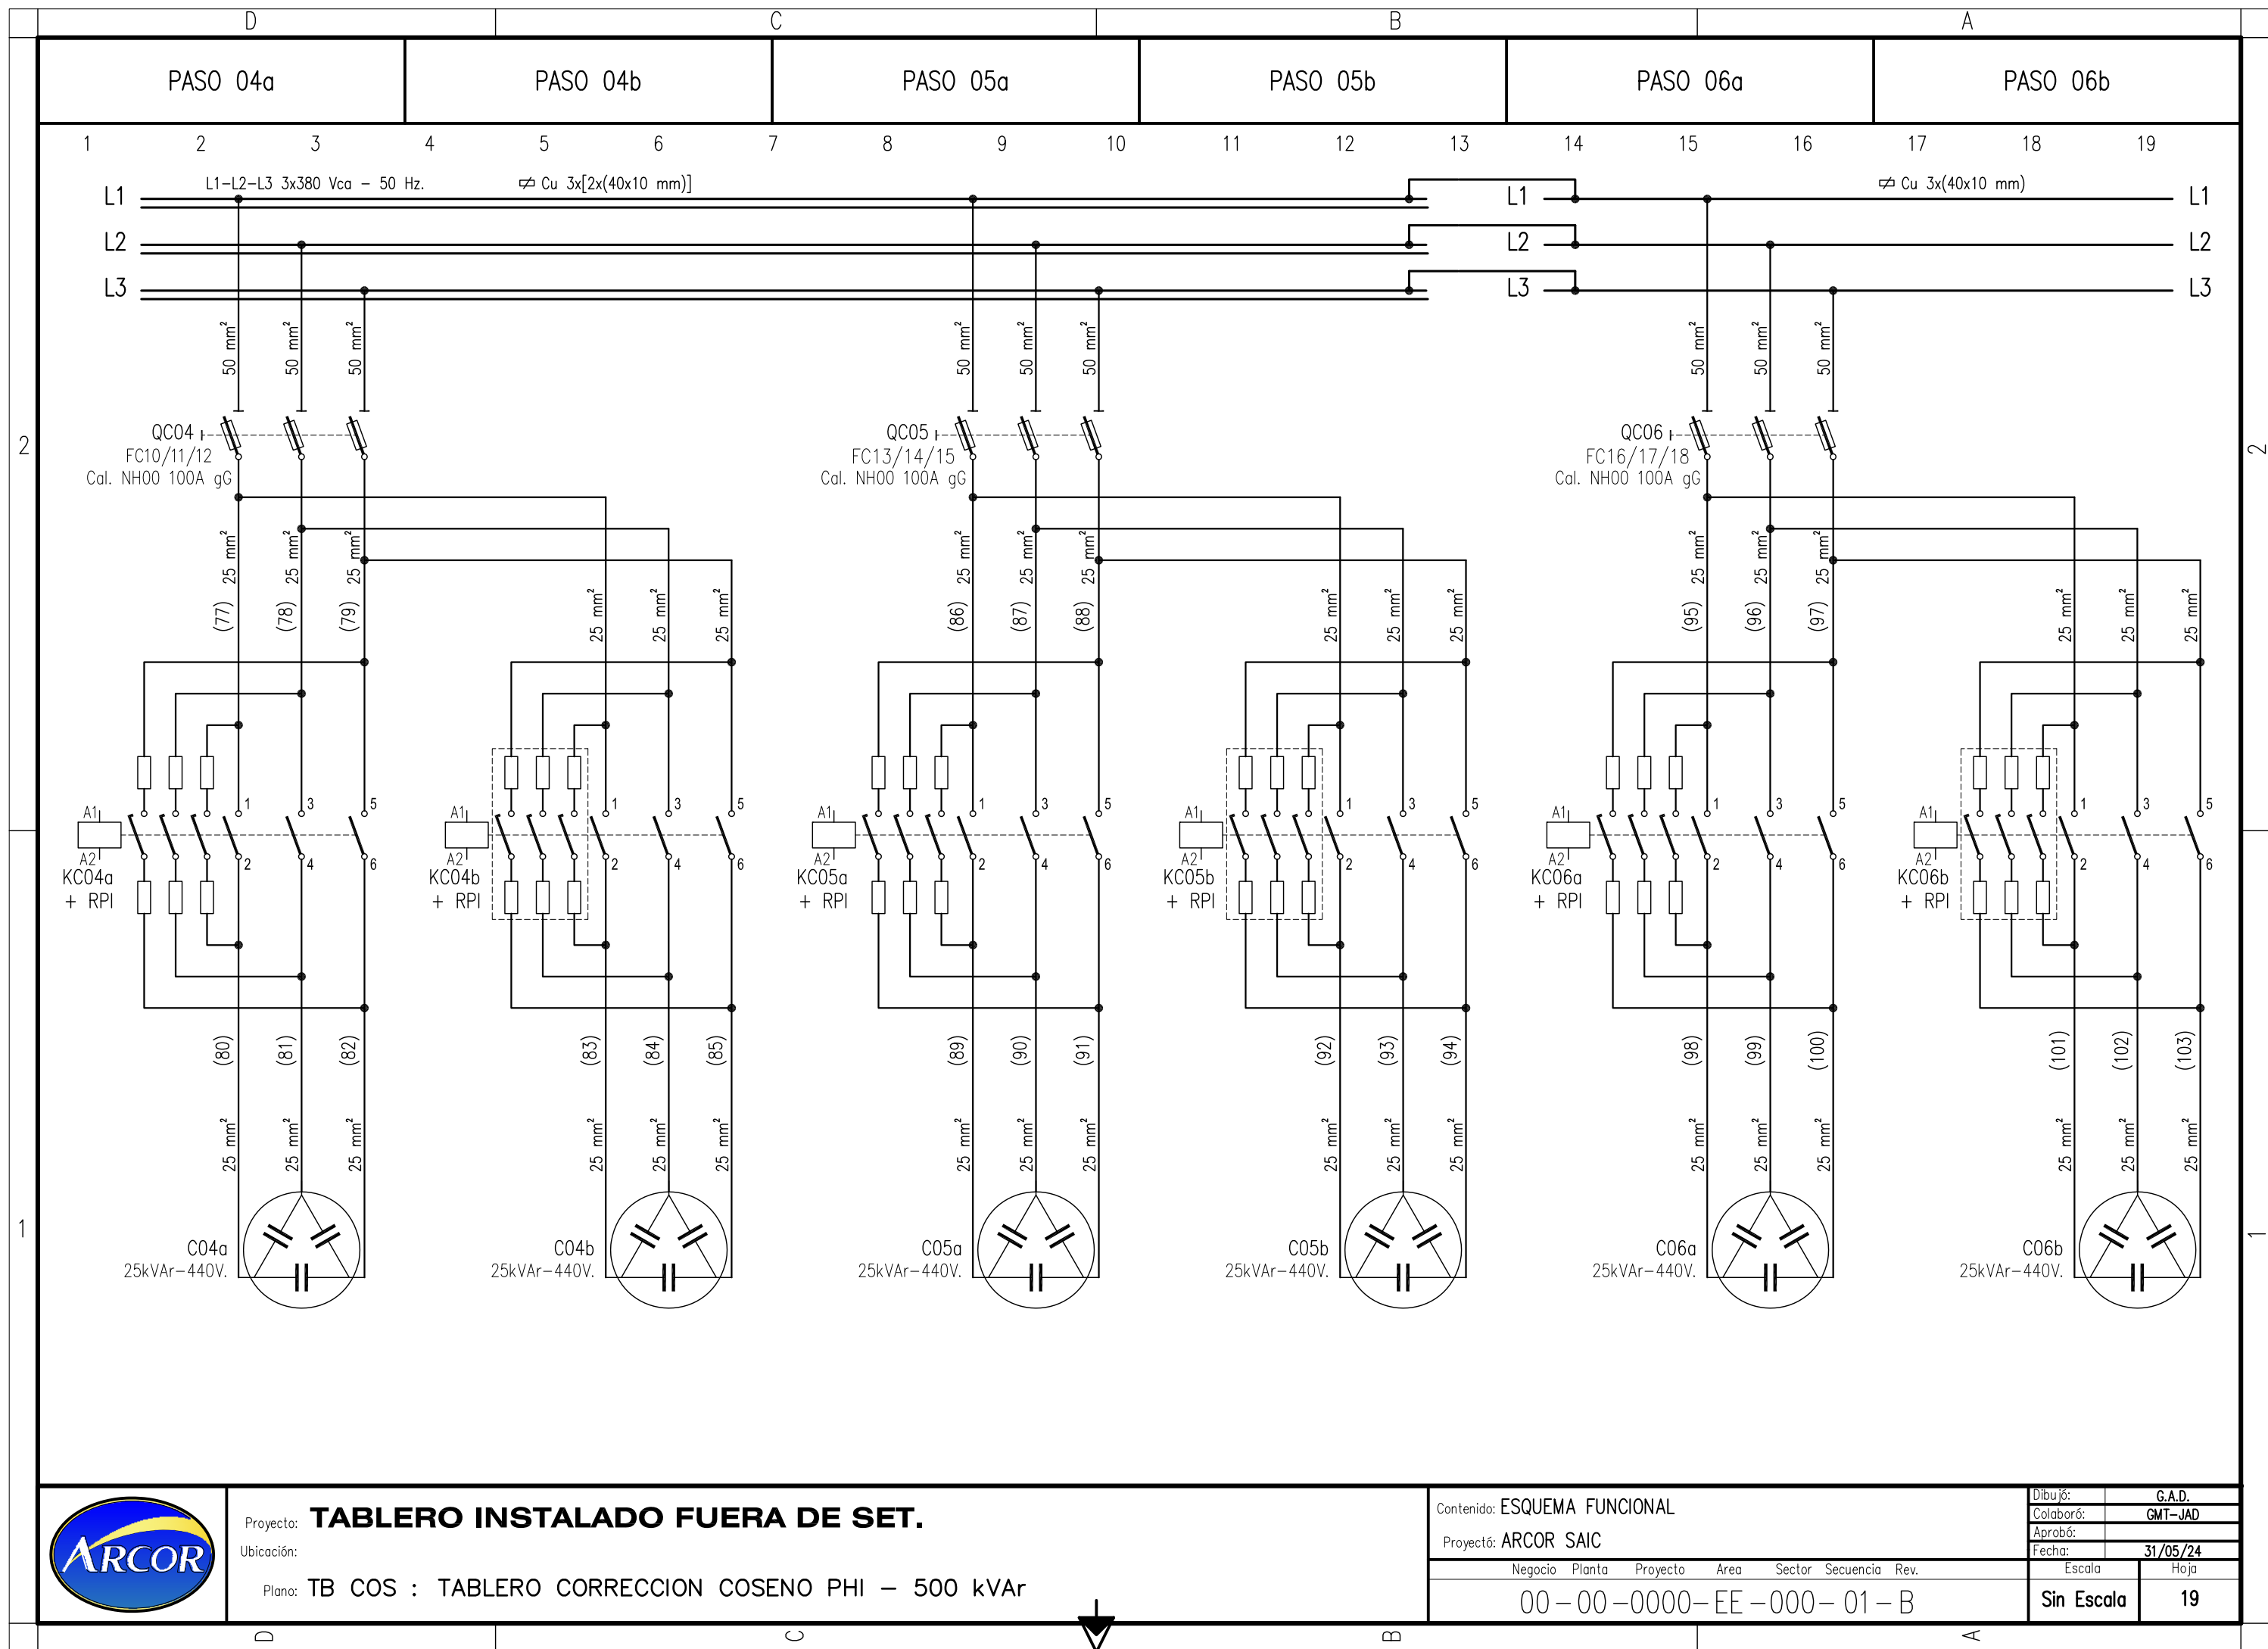

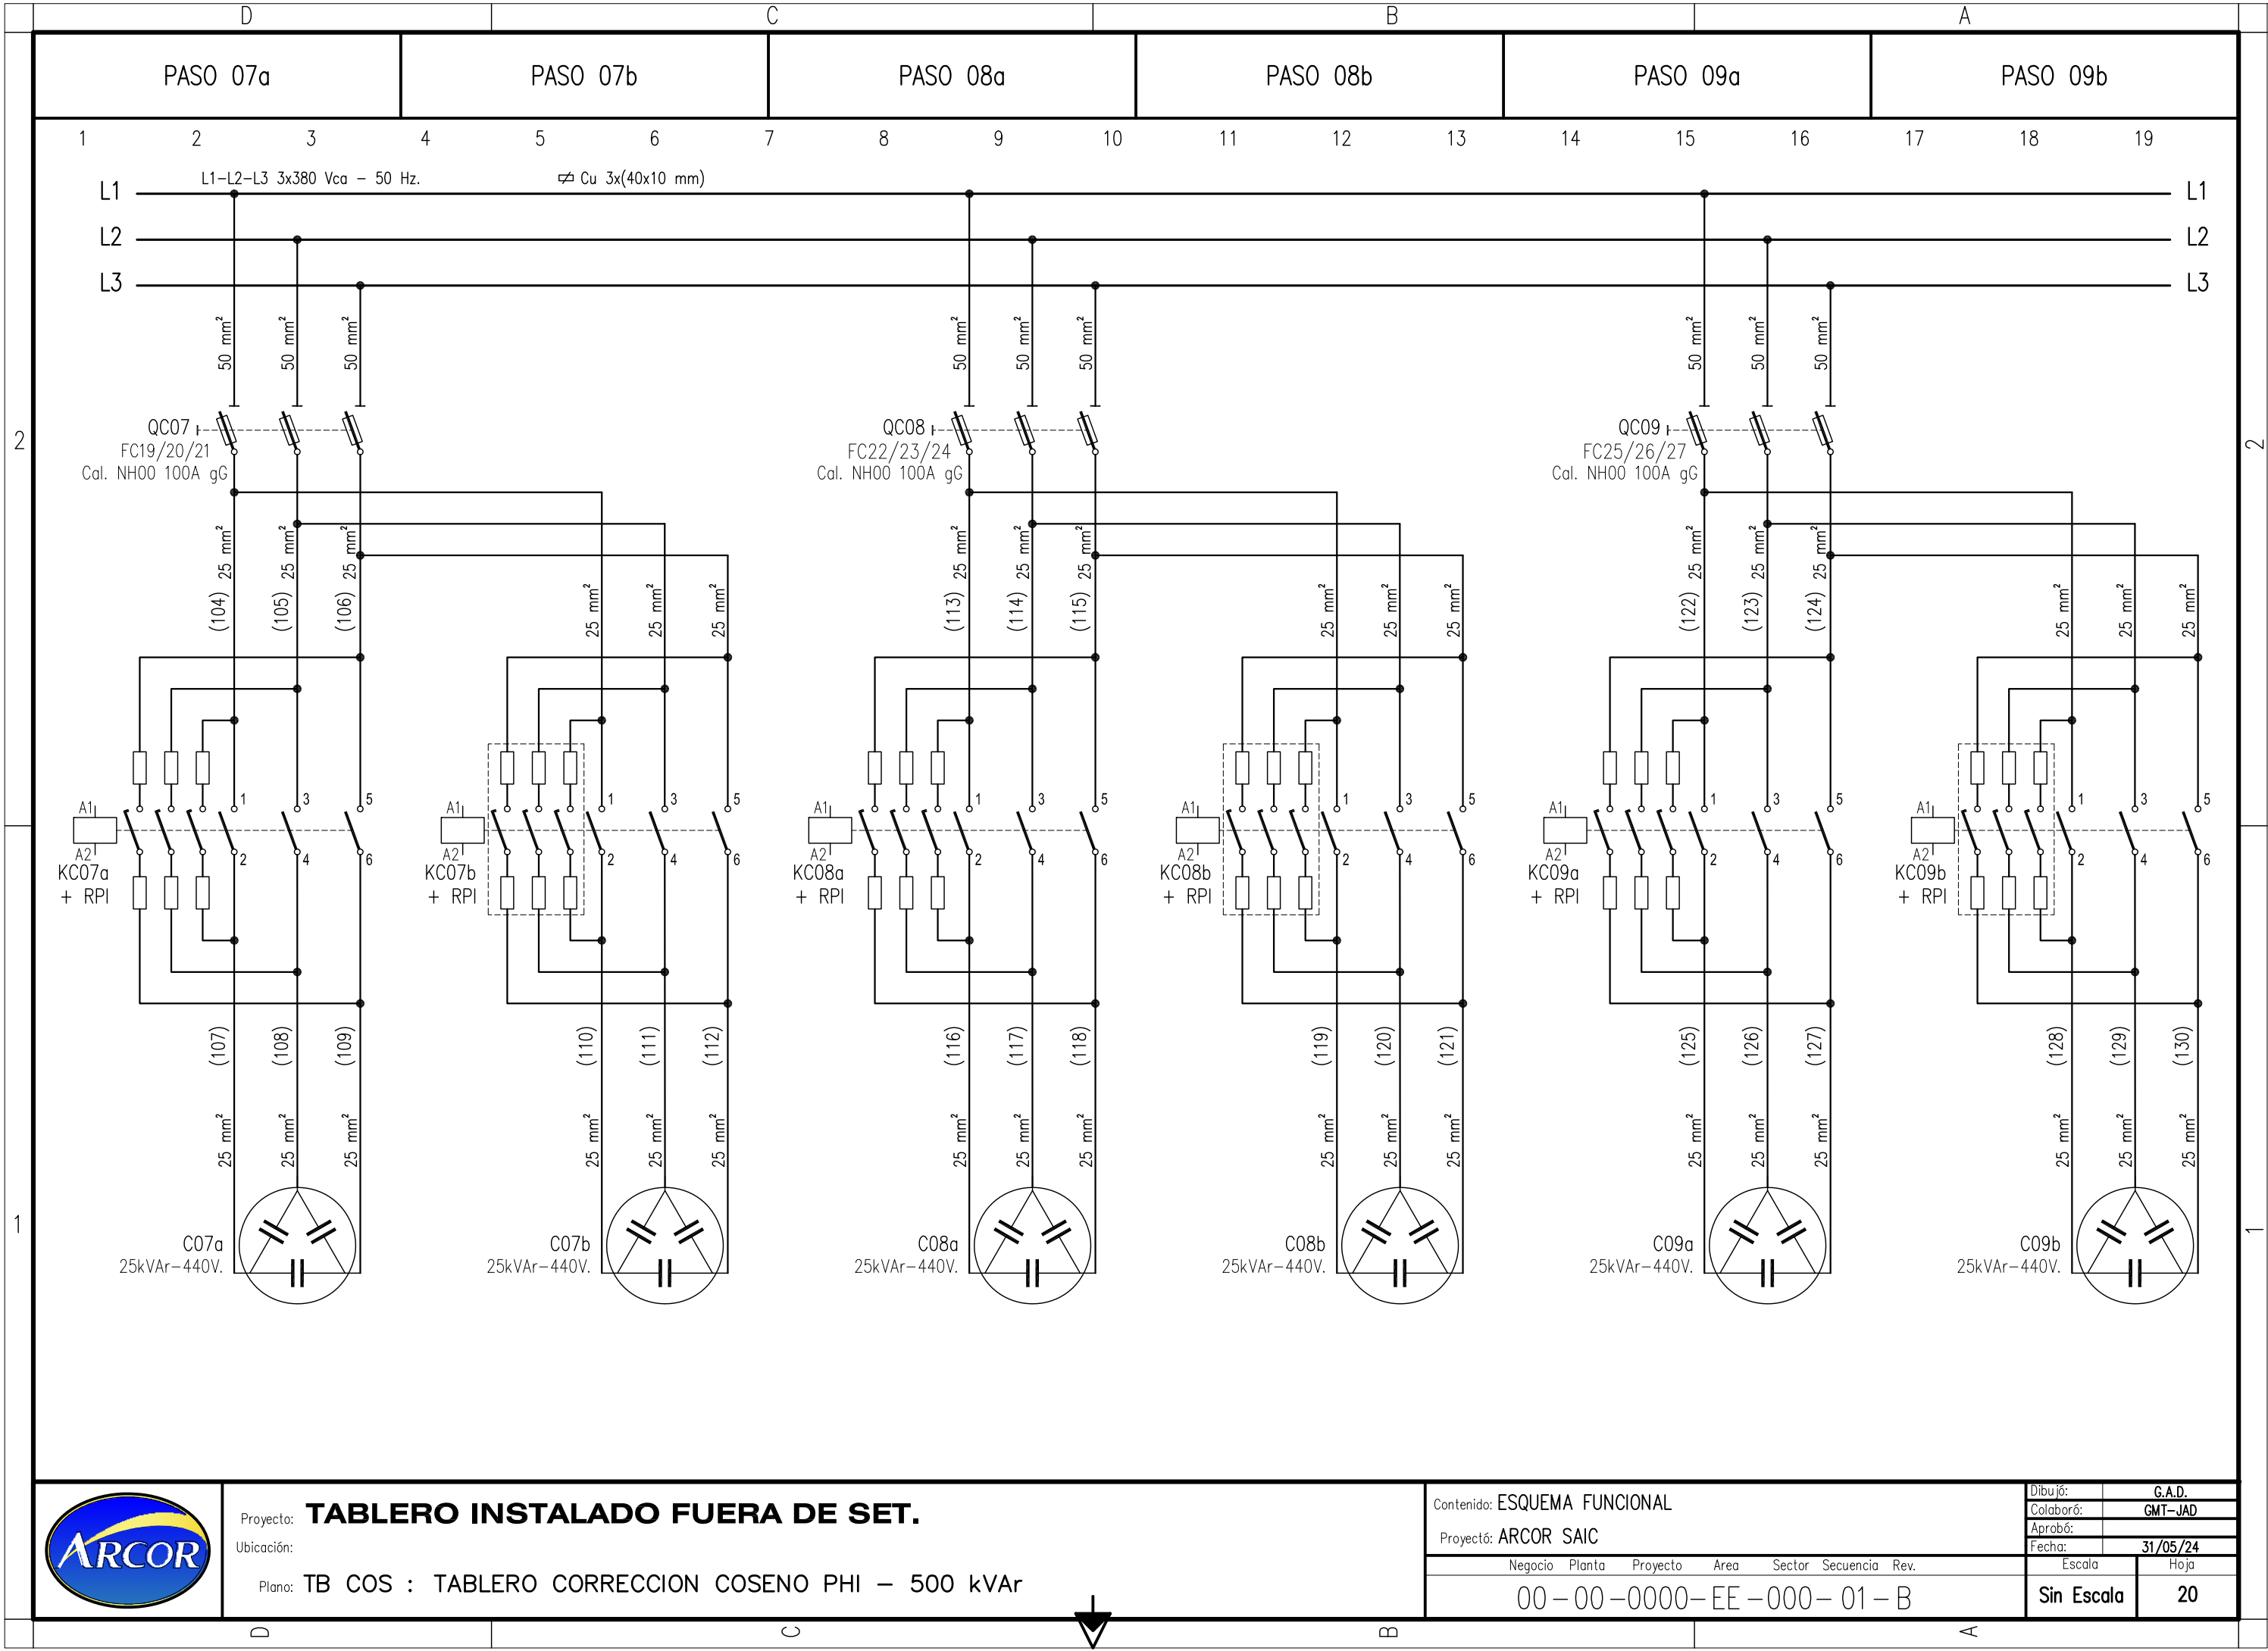

Proyecto: **TABLERO INSTALADO FUERA DE SET.**
Ubicación:
Plano: TB COS : TABLERO CORRECCION COSENO PHI - 500 kVar

Contenido: ESQUEMA FUNCIONAL
Proyecto: ARCOR SAIC
Negocio Planta Proyecto Area Sector Secuencia Rev.
00-00-0000-EE-000-01-B

Dibujó:	G.A.D.
Colaboró:	GMT-JAD
Aprobó:	
Fecha:	31/05/24
Escala	Hoja
Sin Escala	20



