

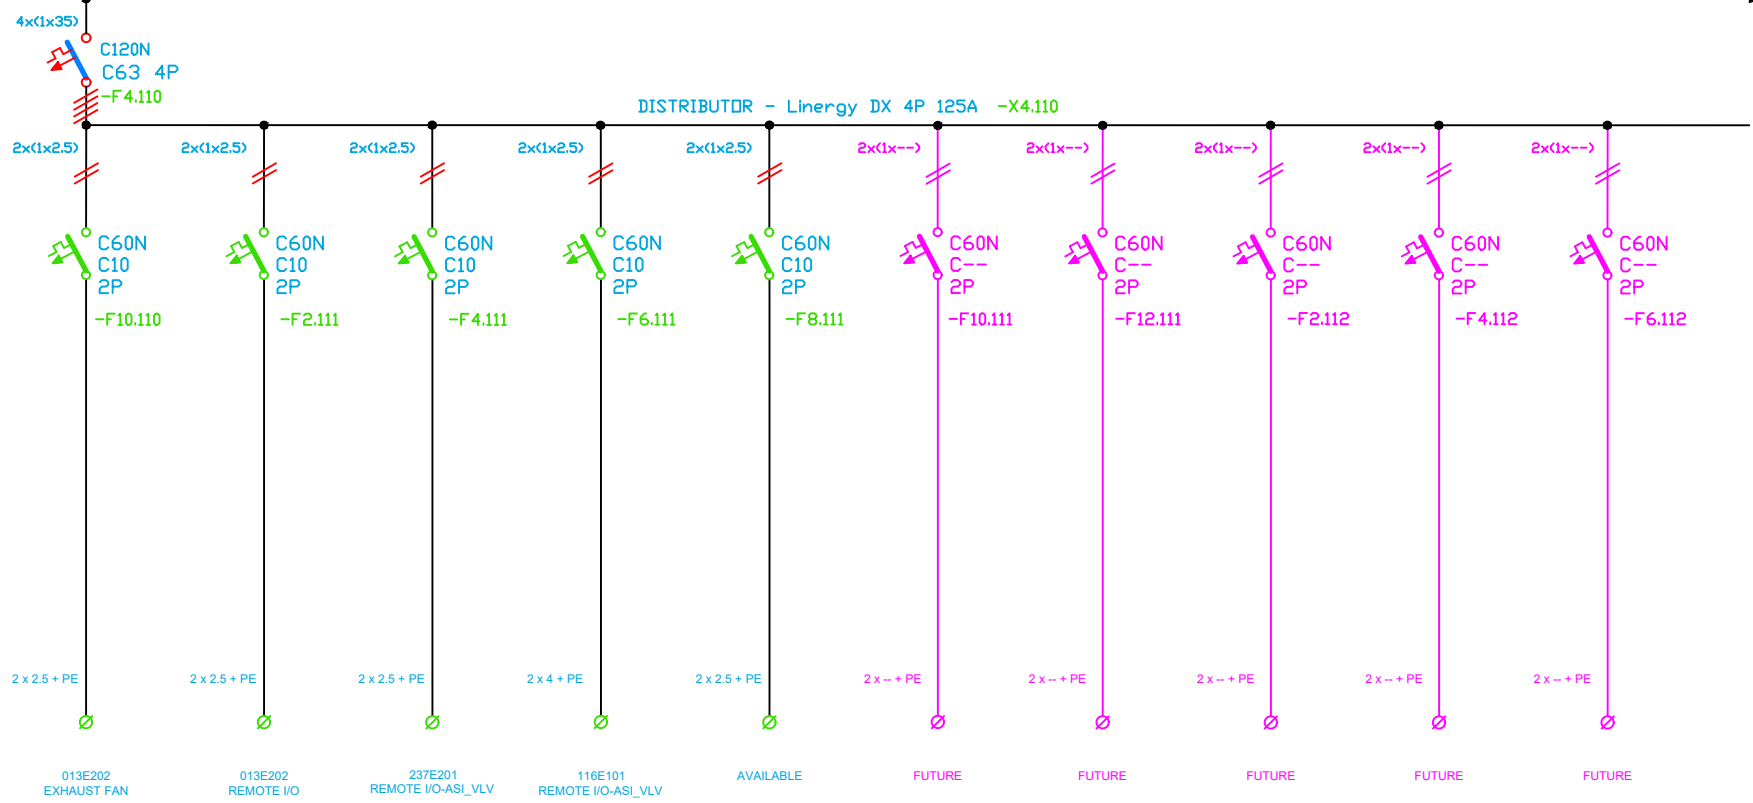


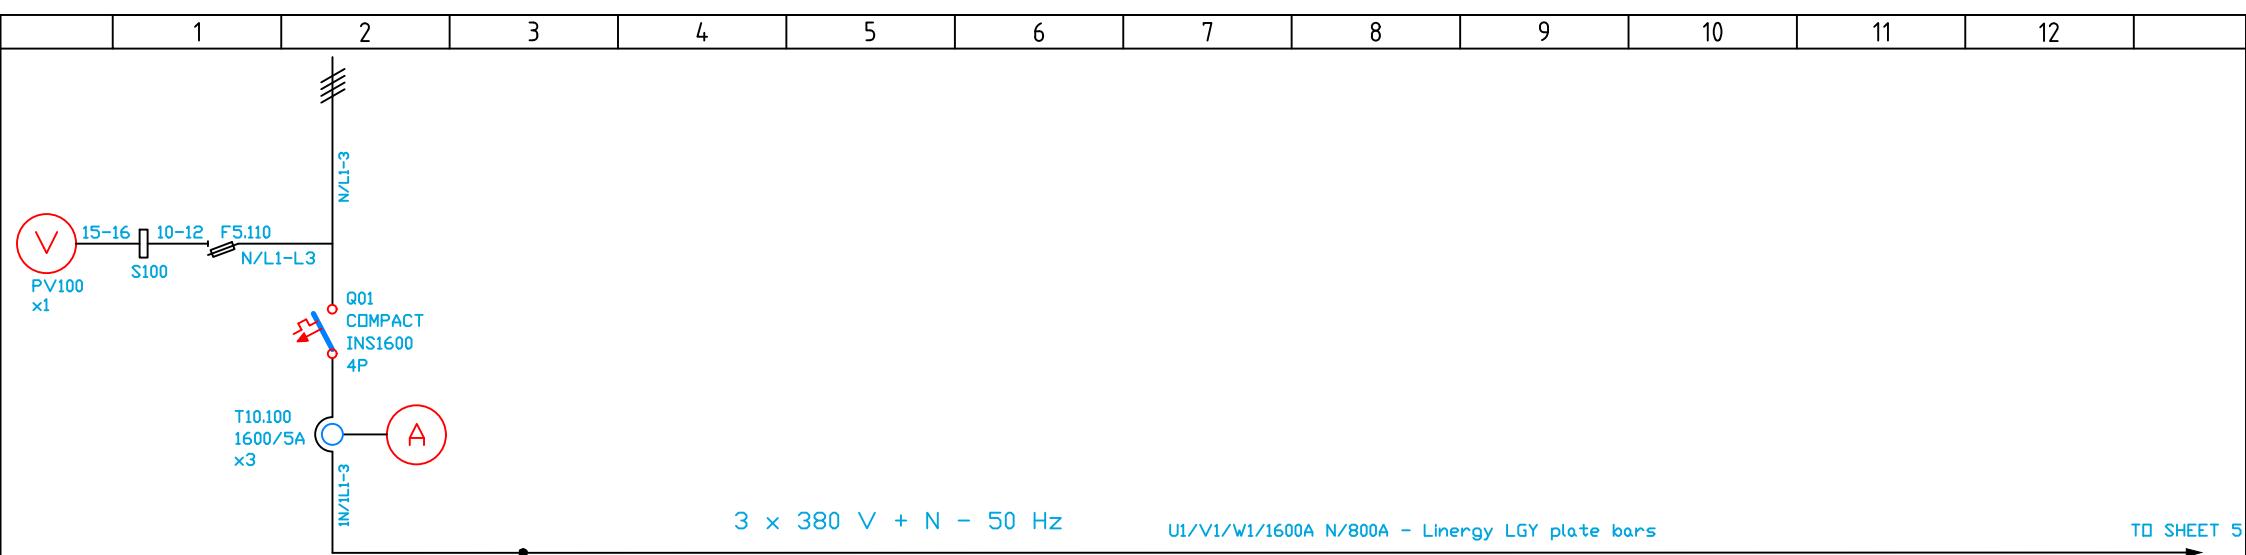

ARLA FOODS INGREDIENTS S.A.
TECHNICAL OFFICE
 Ruta Provincial Nro 1 Km 37 - Porte? - C?doba - Argentina
 Tel: 54-3564-451200 - Fax: 54-3564-451336

AFISA
 WPC PLANT
 CIRCUIT DIAGRAM MCC 013E202

JOB NUMBER AFISA0501		DRAWING NUMBER 3011	
DESIGNED BY	ESBAR	SECTION X	SHEET 1
CONTROLLED BY	---	REV. A0	CONT SHEET 5
DATE 11/12/2020			

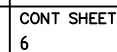


FROM SHEET 5 $3 \times 380 \text{ V} + \text{N} - 50 \text{ Hz}$

U1/V1/W1/1600A N/800A - Linergy LGY plate bars

FROM SHEET 5

U1/V1/W1/1600A N/800A - Linergy LGY plate bars

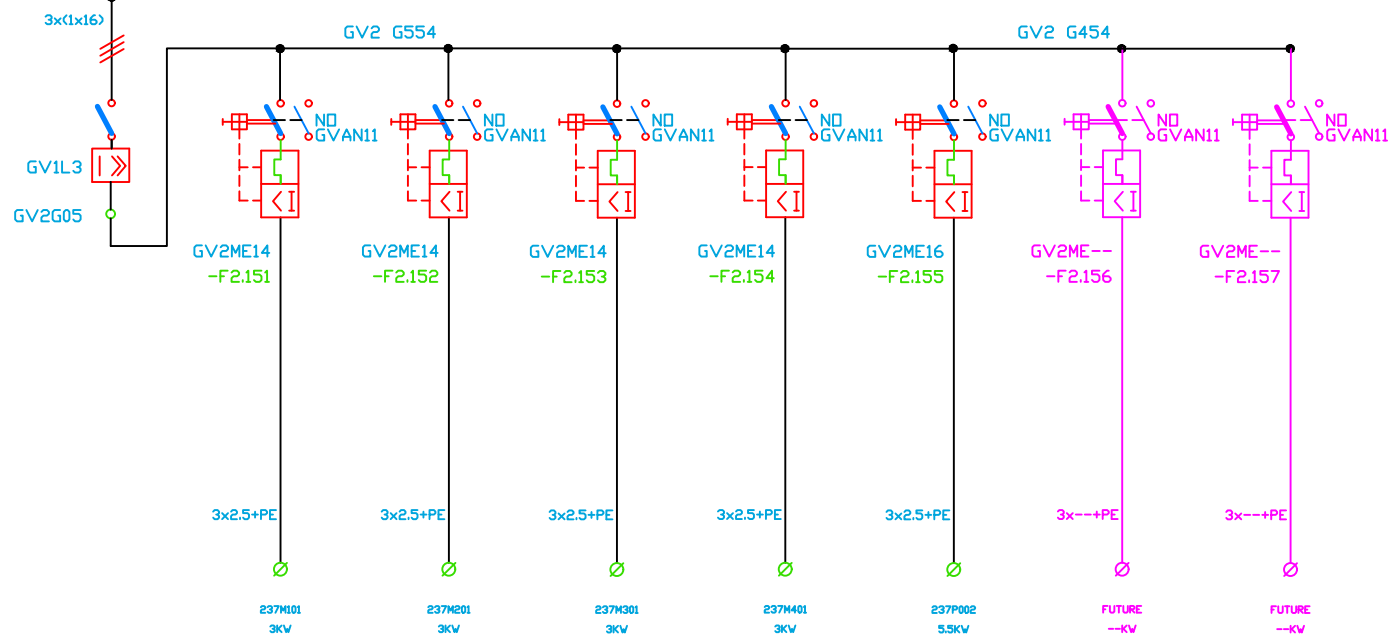**ARLA FOODS INGREDIENTS S.A.**
TECHNICAL OFFICERuta Provincial Nro 1 Km 37 - Porte? - C?doba - Argentina
Tel: 54-3564-451200 - Fax: 54-3564-451336AFISA
WPC PLANT


CIRCUIT DIAGRAM MCC 013E202

JOB NUMBER
AFISA0501

DESIGNED BY ESBAR

CONTROLLED BY ---

DATE
11/12/2020DRAWING NUMBER
3011SECTION
XREV.
A0SHEET
6CONT SHEET
-

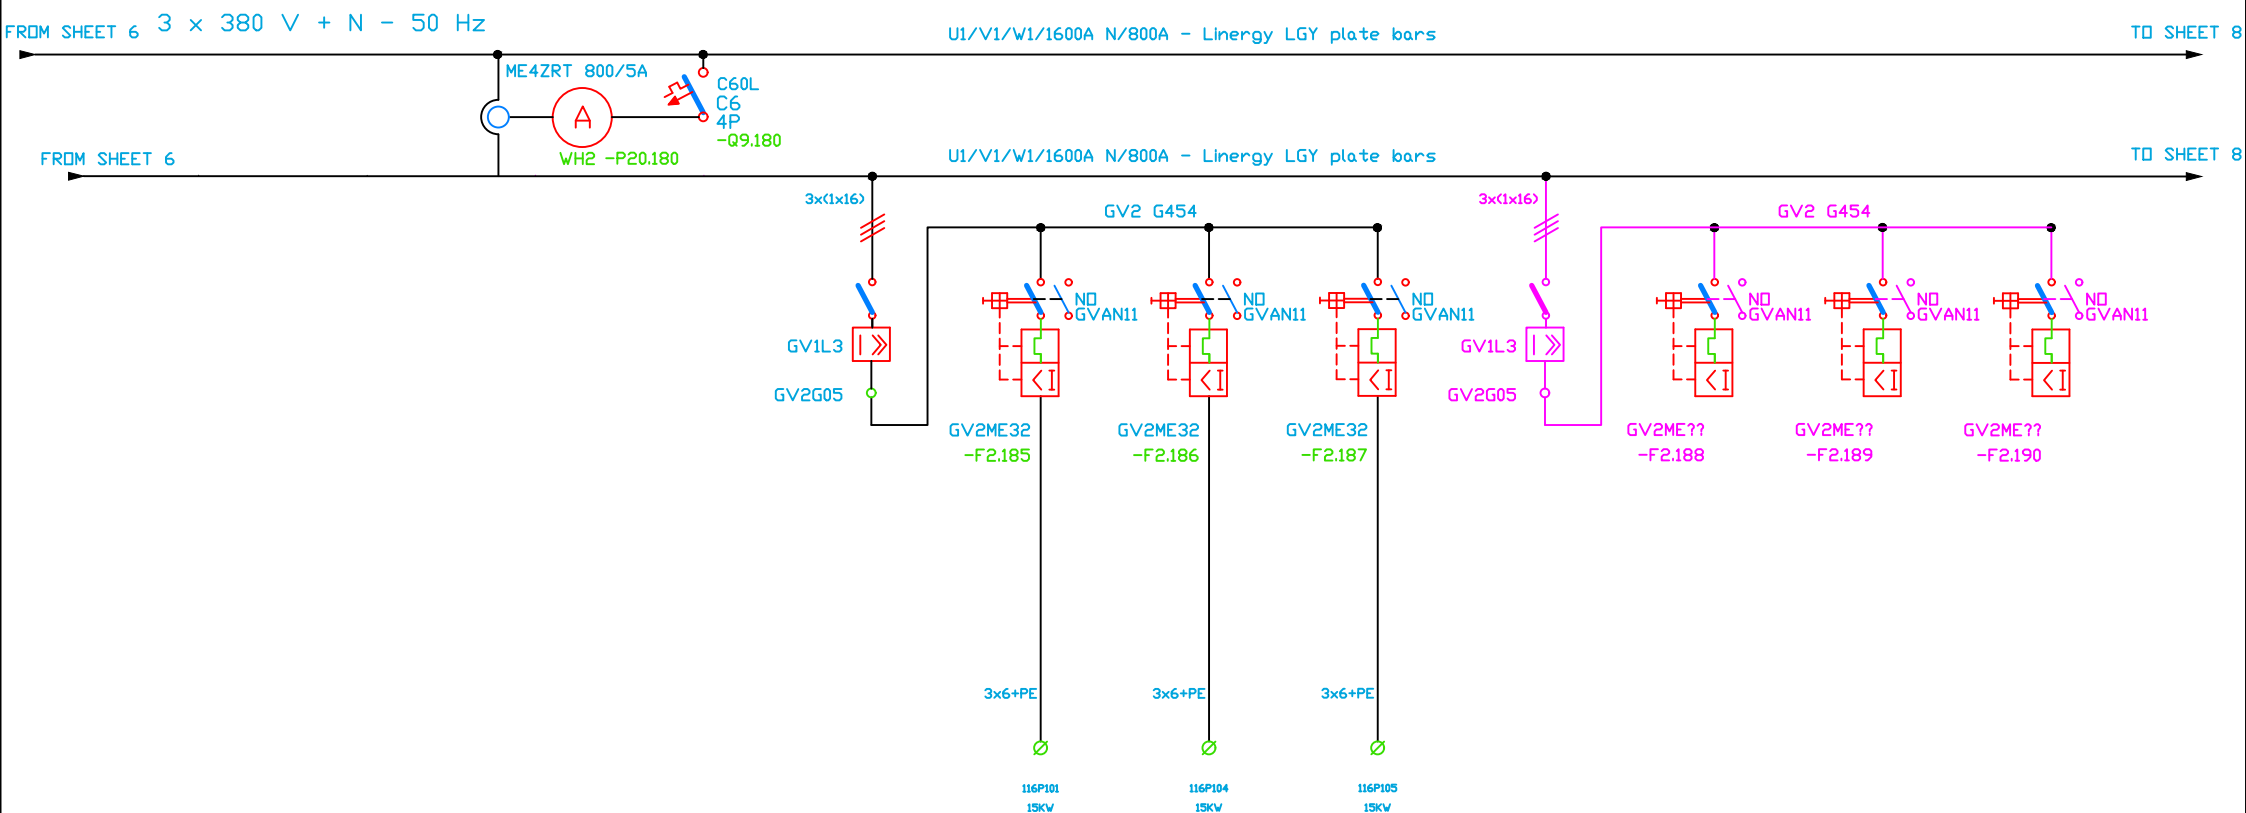

ARLA FOODS INGREDIENTS S.A.
TECHNICAL OFFICE

Ruta Provincial Nro 1 Km 37 - Porte? - C?doba - Argentina
Tel: 54-3564-451200 - Fax: 54-3564-451336

AFISA
WPC PLANT

CIRCUIT DIAGRAM MCC 013E202

JOB NUMBER
AFISA0501

DESIGNED BY ESBAR
CONTROLLED BY ---

DATE
11/12/2020

DRAWING NUMBER
3011

SECTION X
SHEET 7

REV. A1
CONT SHEET 8

FROM SHEET 7 3 x 380 V + N - 50 Hz

U1/V1/W1/1600A N/800A - Linergy LGY plate bars

FROM SHEET 7

U1/V1/W1/1600A N/800A - Linergy LGY plate bars

