



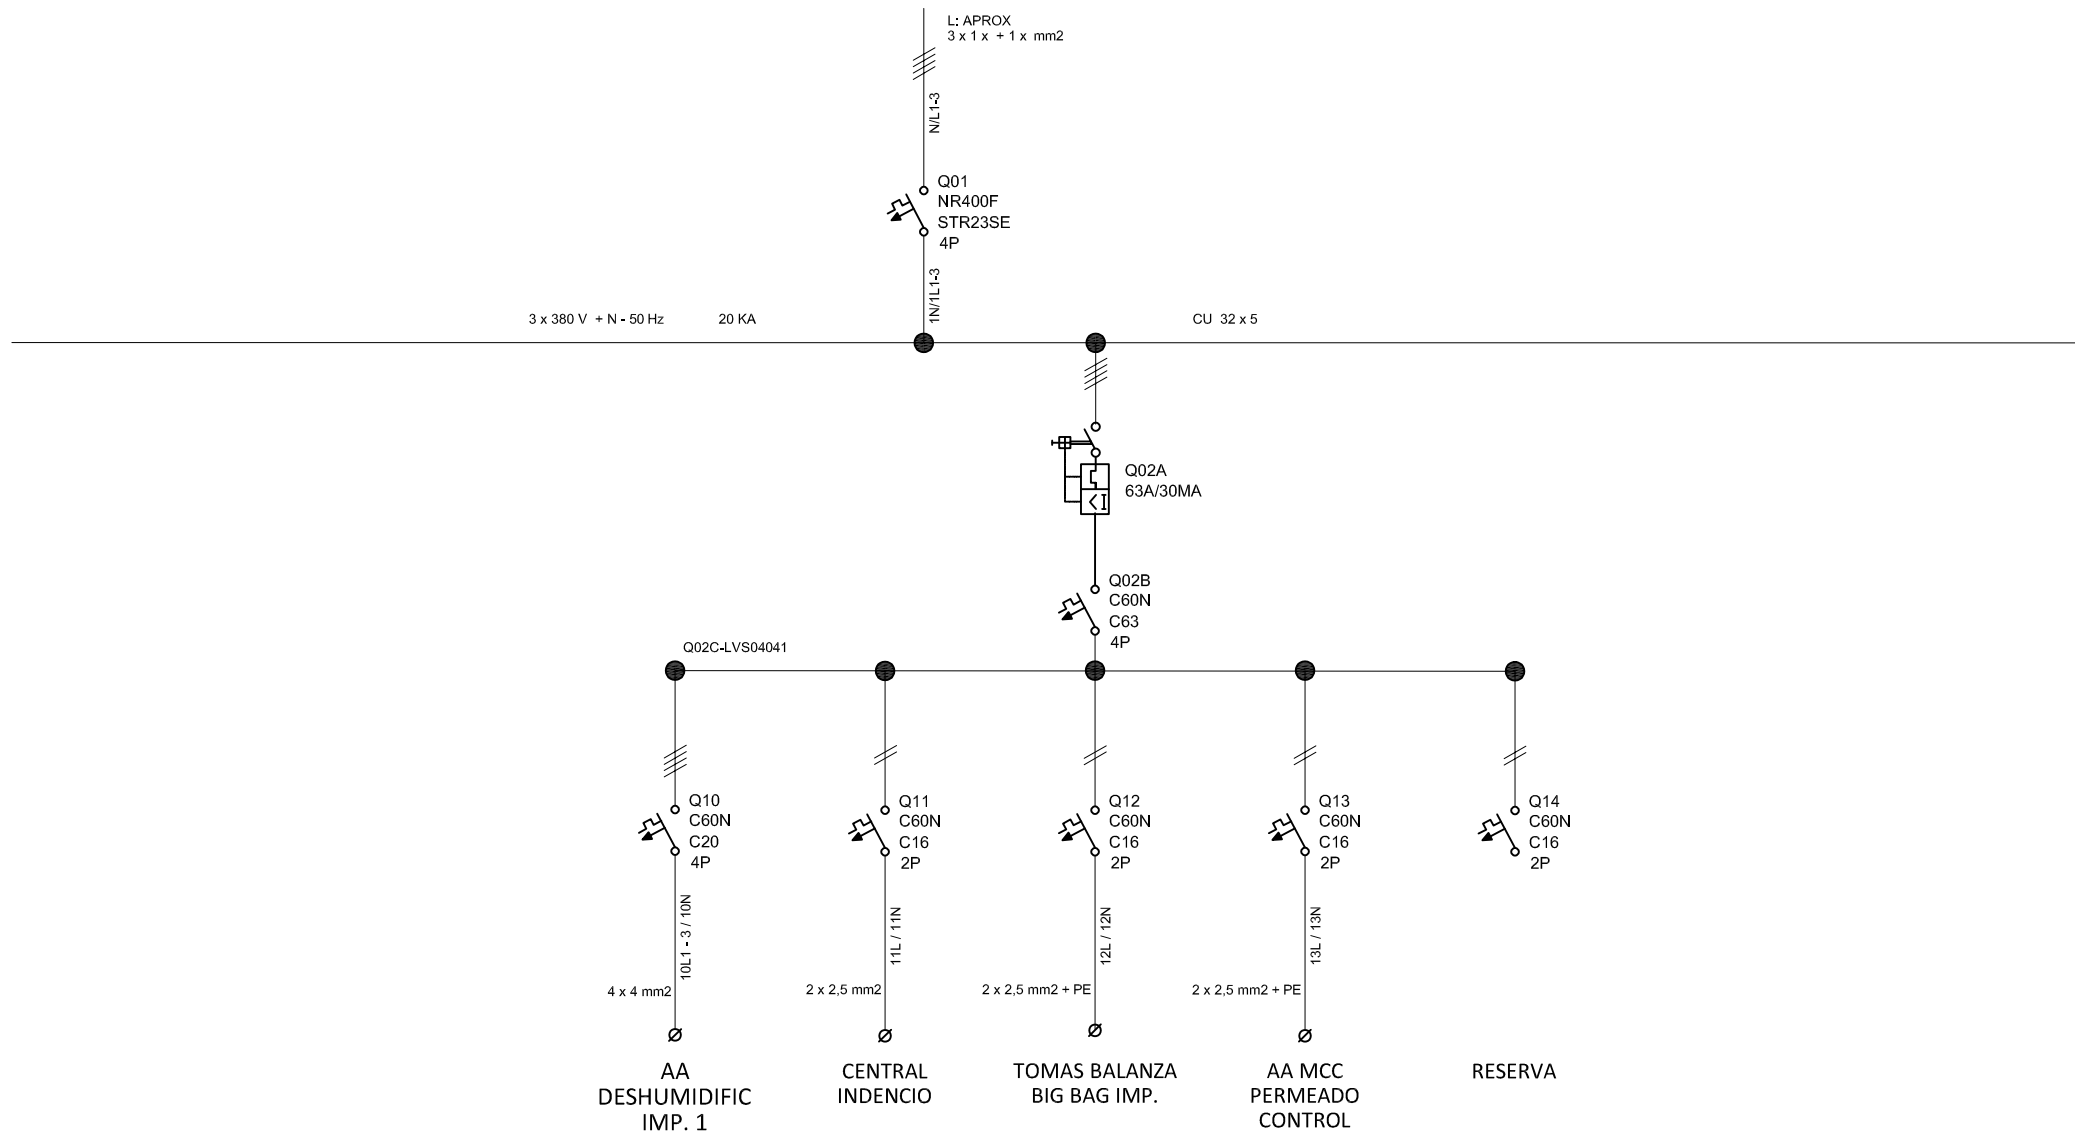

						TABLERO FEM PERMEADO	 SERVICIOS DE INGENIERIA	ESC	S / E
0	EDICION ORIGINAL	—	—	03/03/24				HOJA	1
REV	MODIFICACION	DIB	REV	FECHA				SIGUE	2

3 x 380 V + N - 50 Hz 20 KA

CU 32 x 5

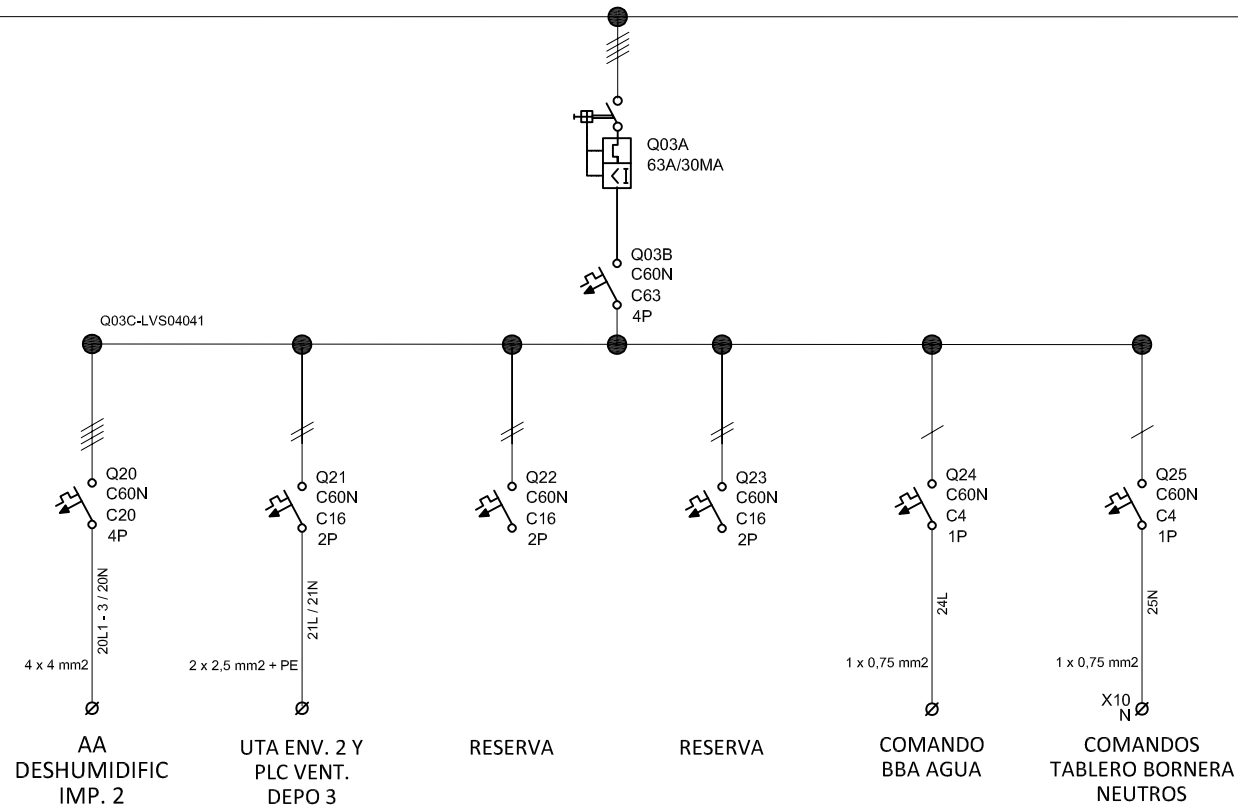


0	EDICION ORIGINAL	—	—	03/03/24
REV	MODIFICACION	DIB	REV	FECHA



TABLERO FEM
PERMEADO



ESC	S / E
HOJA	2
SIGUE	3

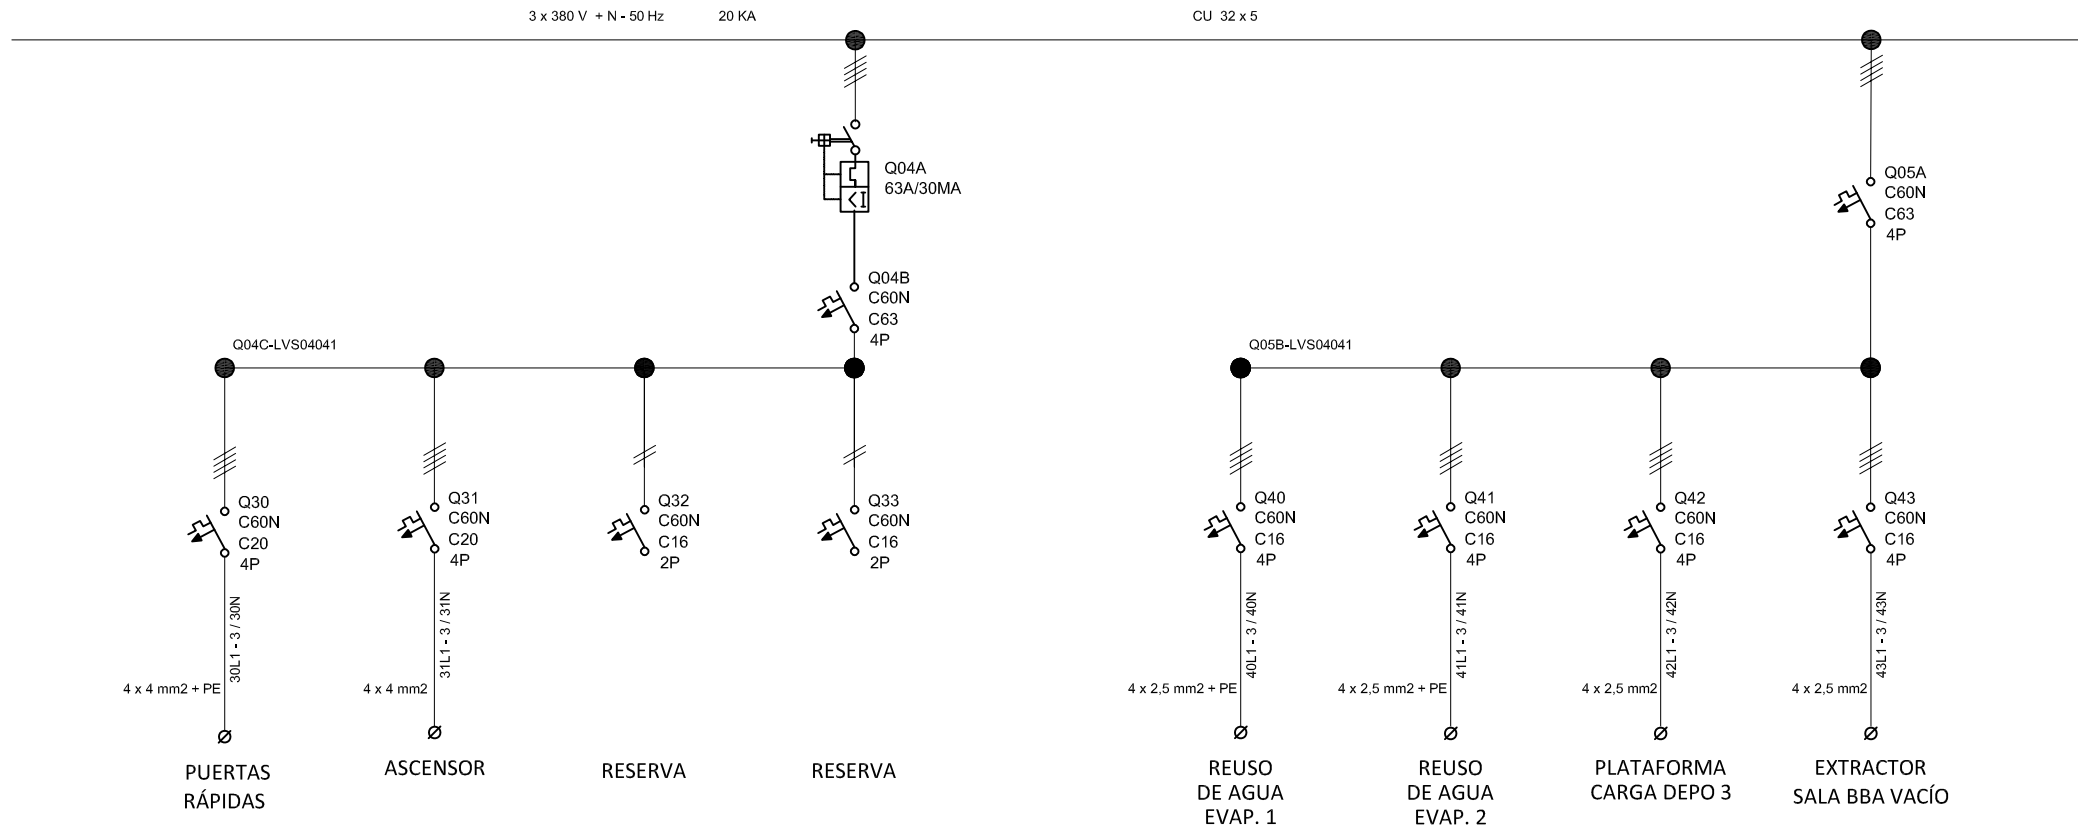


0	EDICION ORIGINAL	—	—	03/03/24
REV	MODIFICACION	DIB	REV	FECHA



TABLERO FEM
PERMEADO



ESC	S / E
HOJA	3
SIGUE	4

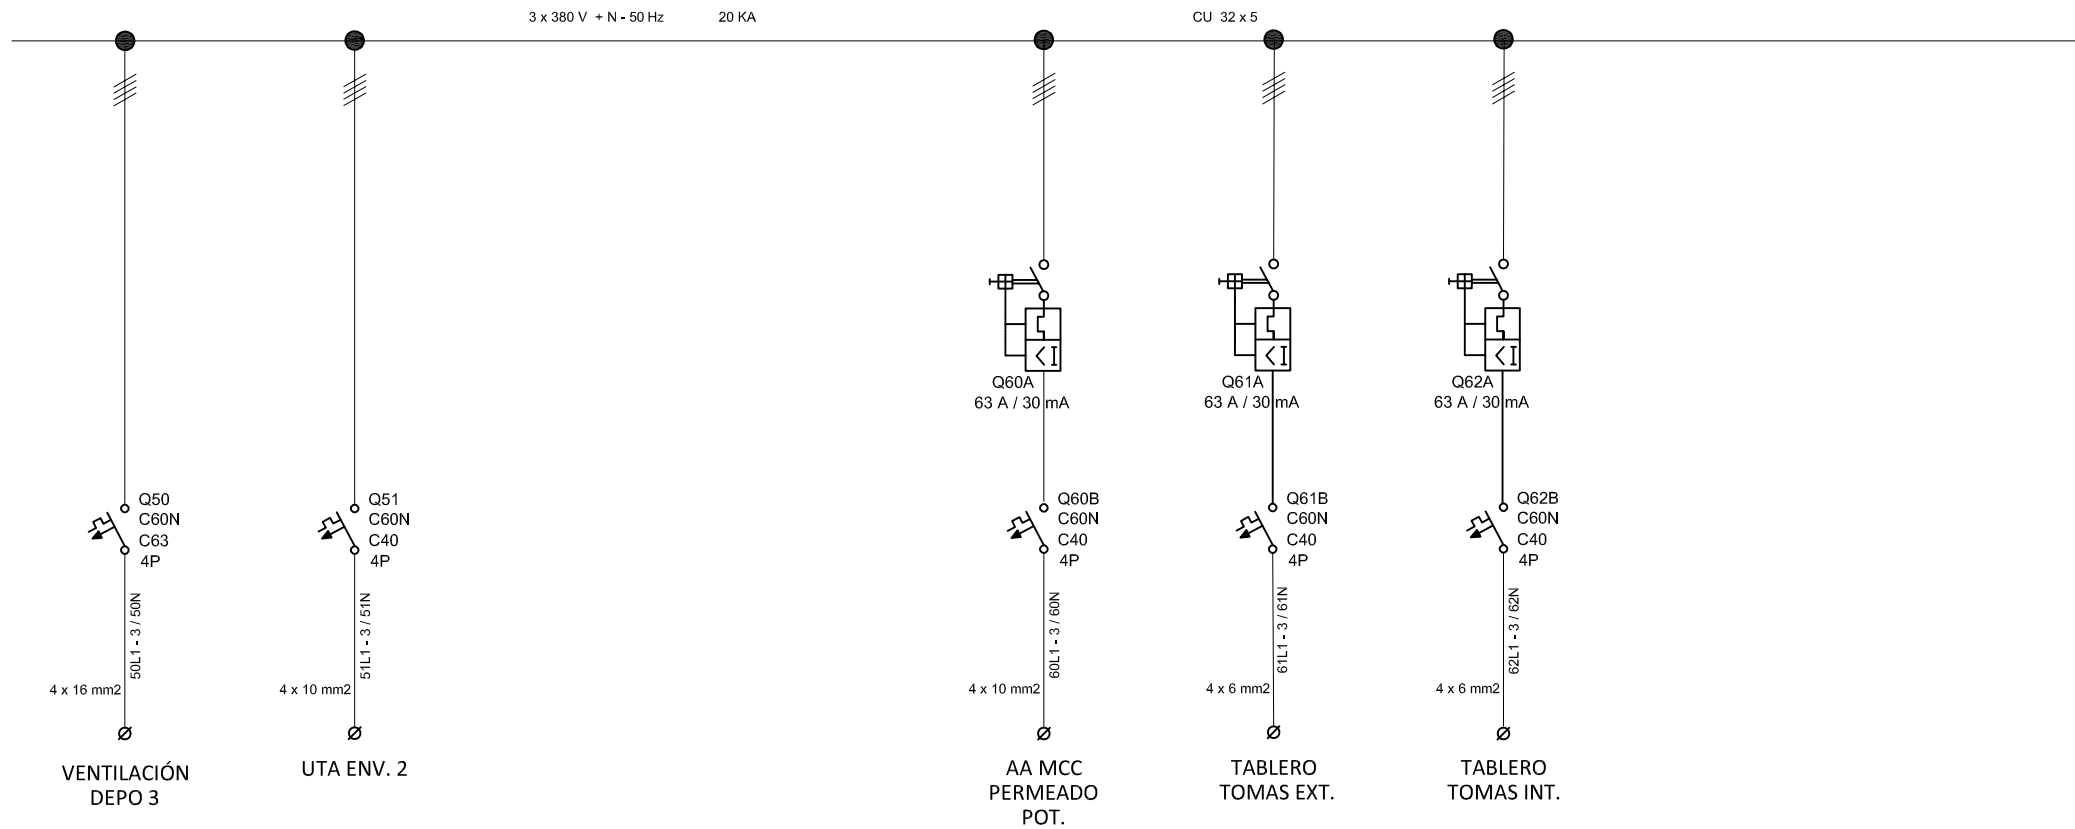


0	EDICION ORIGINAL	—	—	03/03/24
REV	MODIFICACION	DIB	REV	FECHA



TABLERO FEM
PERMEADO




ESC	S / E
HOJA	4
SIGUE	5

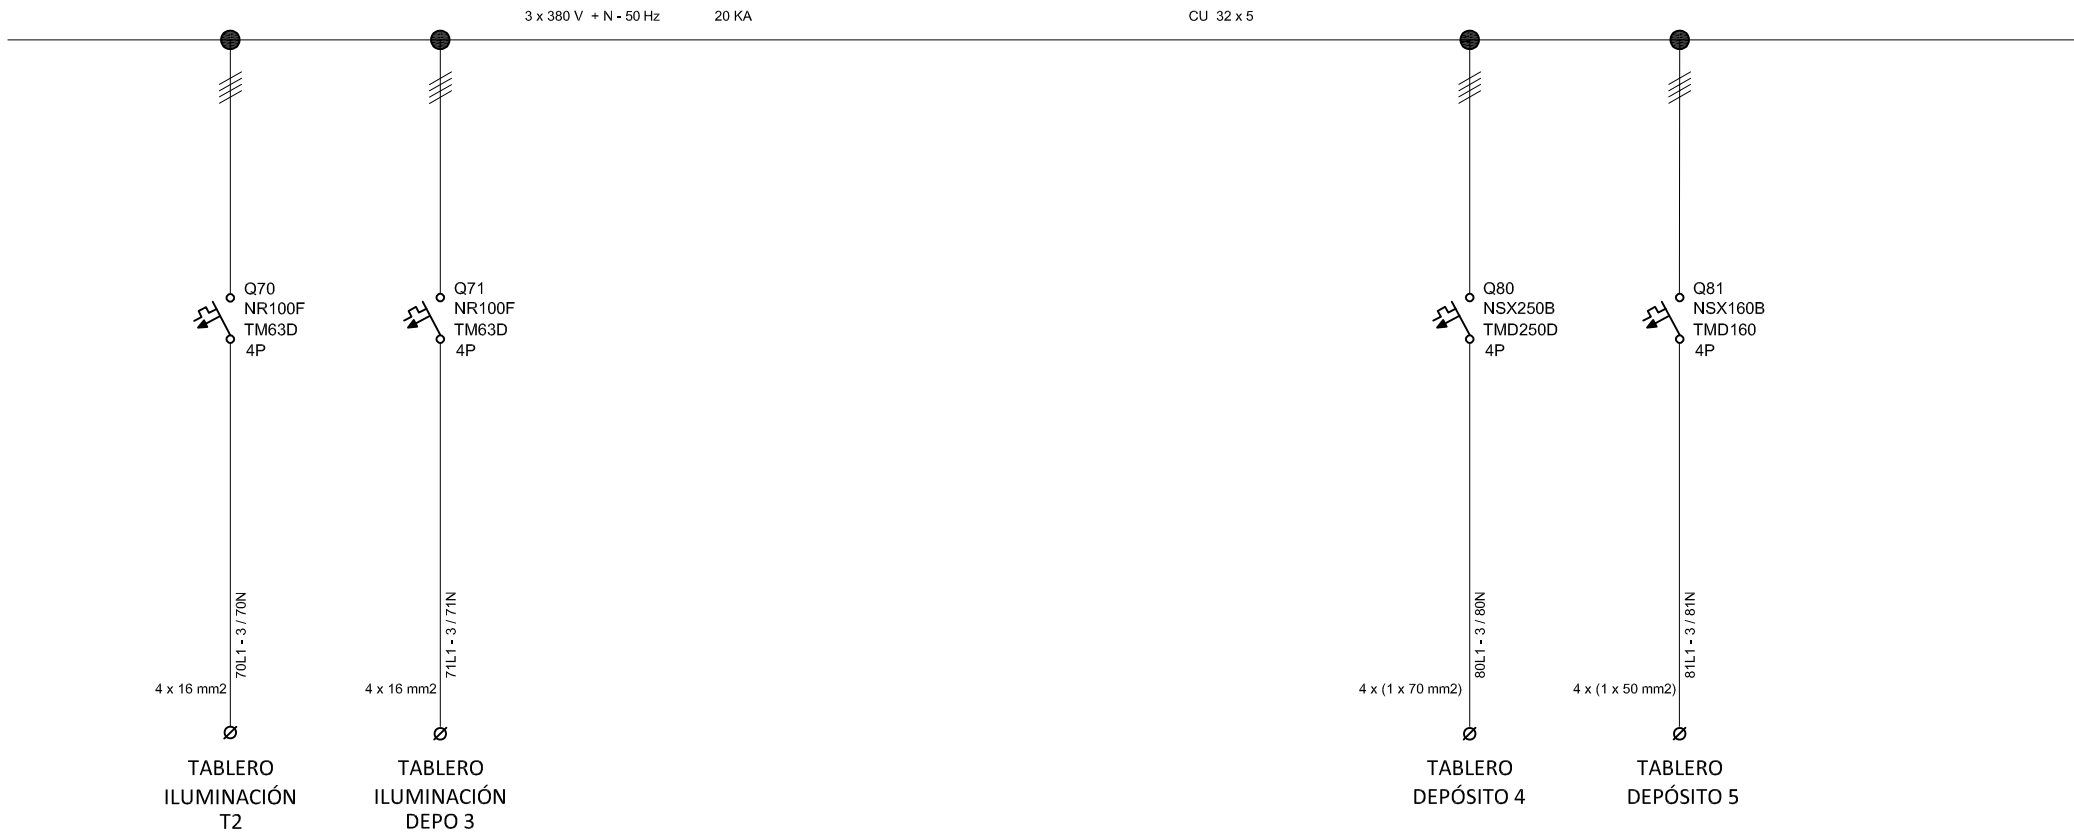

						TABLERO FEM PERMEADO	 SERVICIOS DE INGENIERIA	ESC	S / E
0	EDICION ORIGINAL	—	—	03/03/24				HOJA	5
REV	MODIFICACION	DIB	REV	FECHA				SIGUE	6

3 x 380 V + N - 50 Hz 20 KA

CU 32 x 5

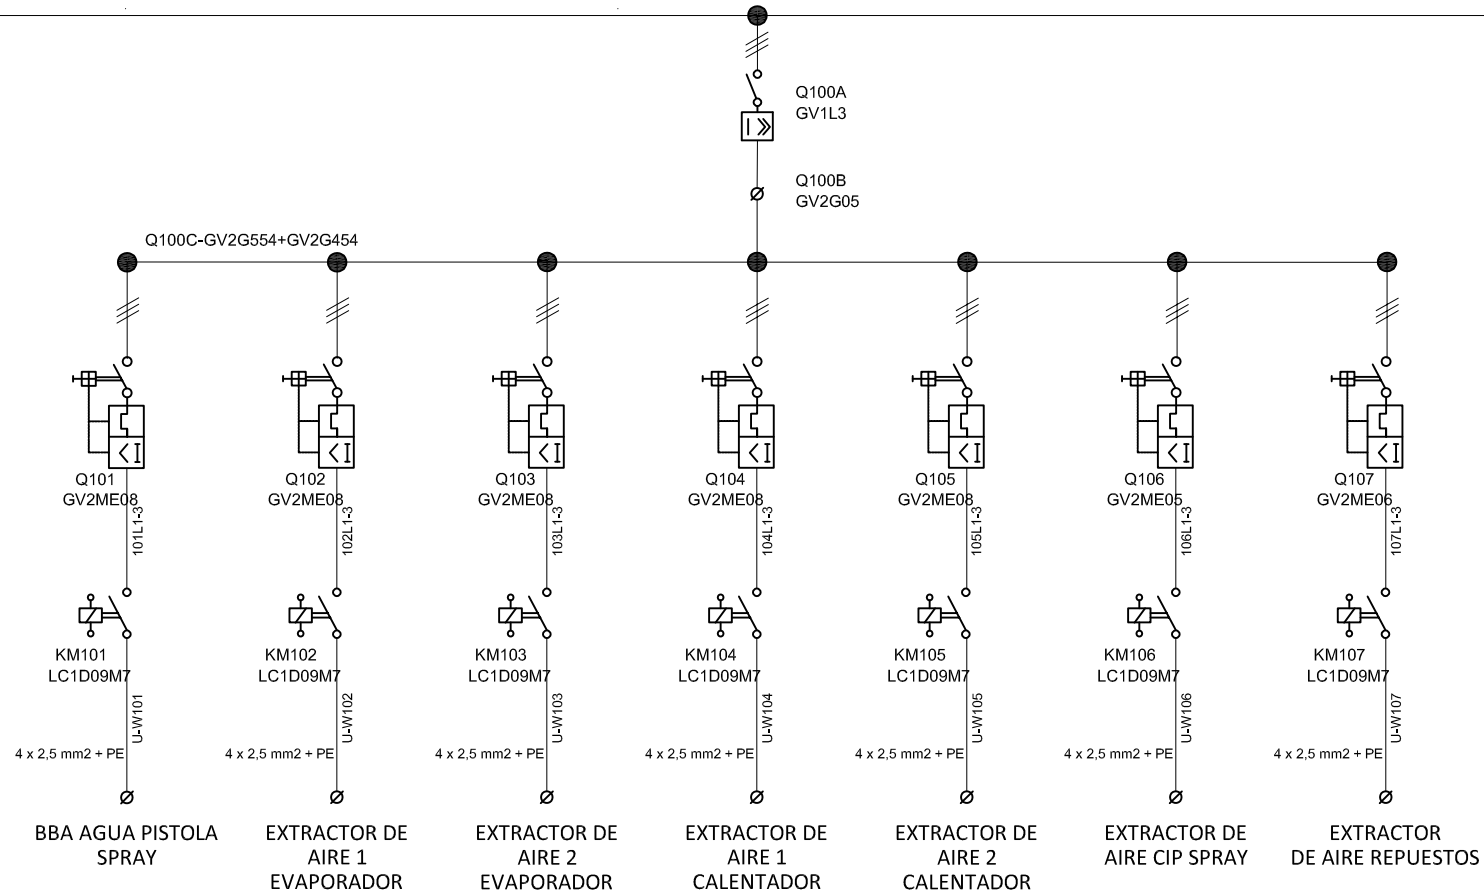

0	EDICION ORIGINAL	—	—	03/03/24
REV	MODIFICACION	DIB	REV	FECHA




TABLERO FEM
PERMEADO




ESC	S / E
HOJA	6
SIGUE	7

3 x 380 V + N - 50 Hz 20 KA

CU 32 x 5

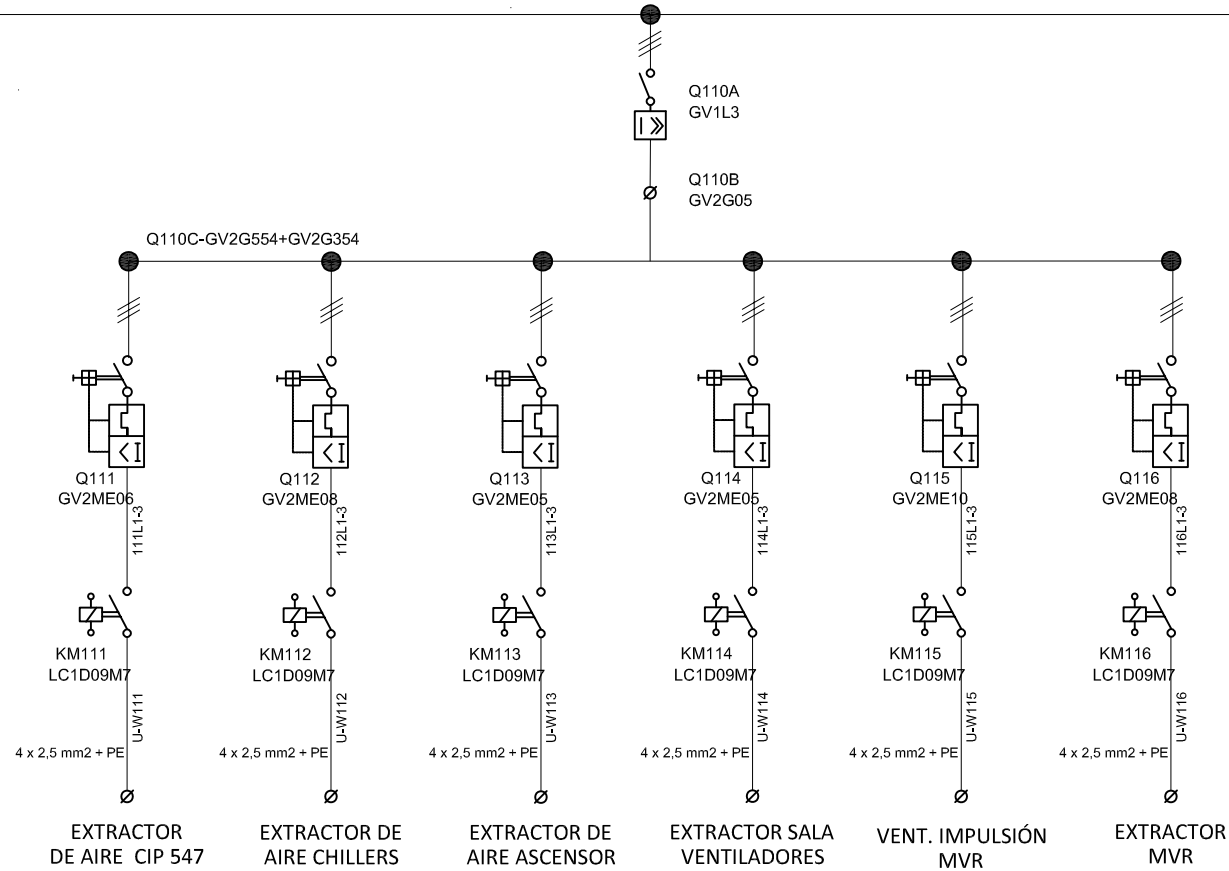

						TABLERO FEM PERMEADO	 SERVICIOS DE INGENIERIA	ESC	S / E
0	EDICION ORIGINAL	—	—	03/03/24				HOJA	7
REV	MODIFICACION	DIB	REV	FECHA				SIGUE	8

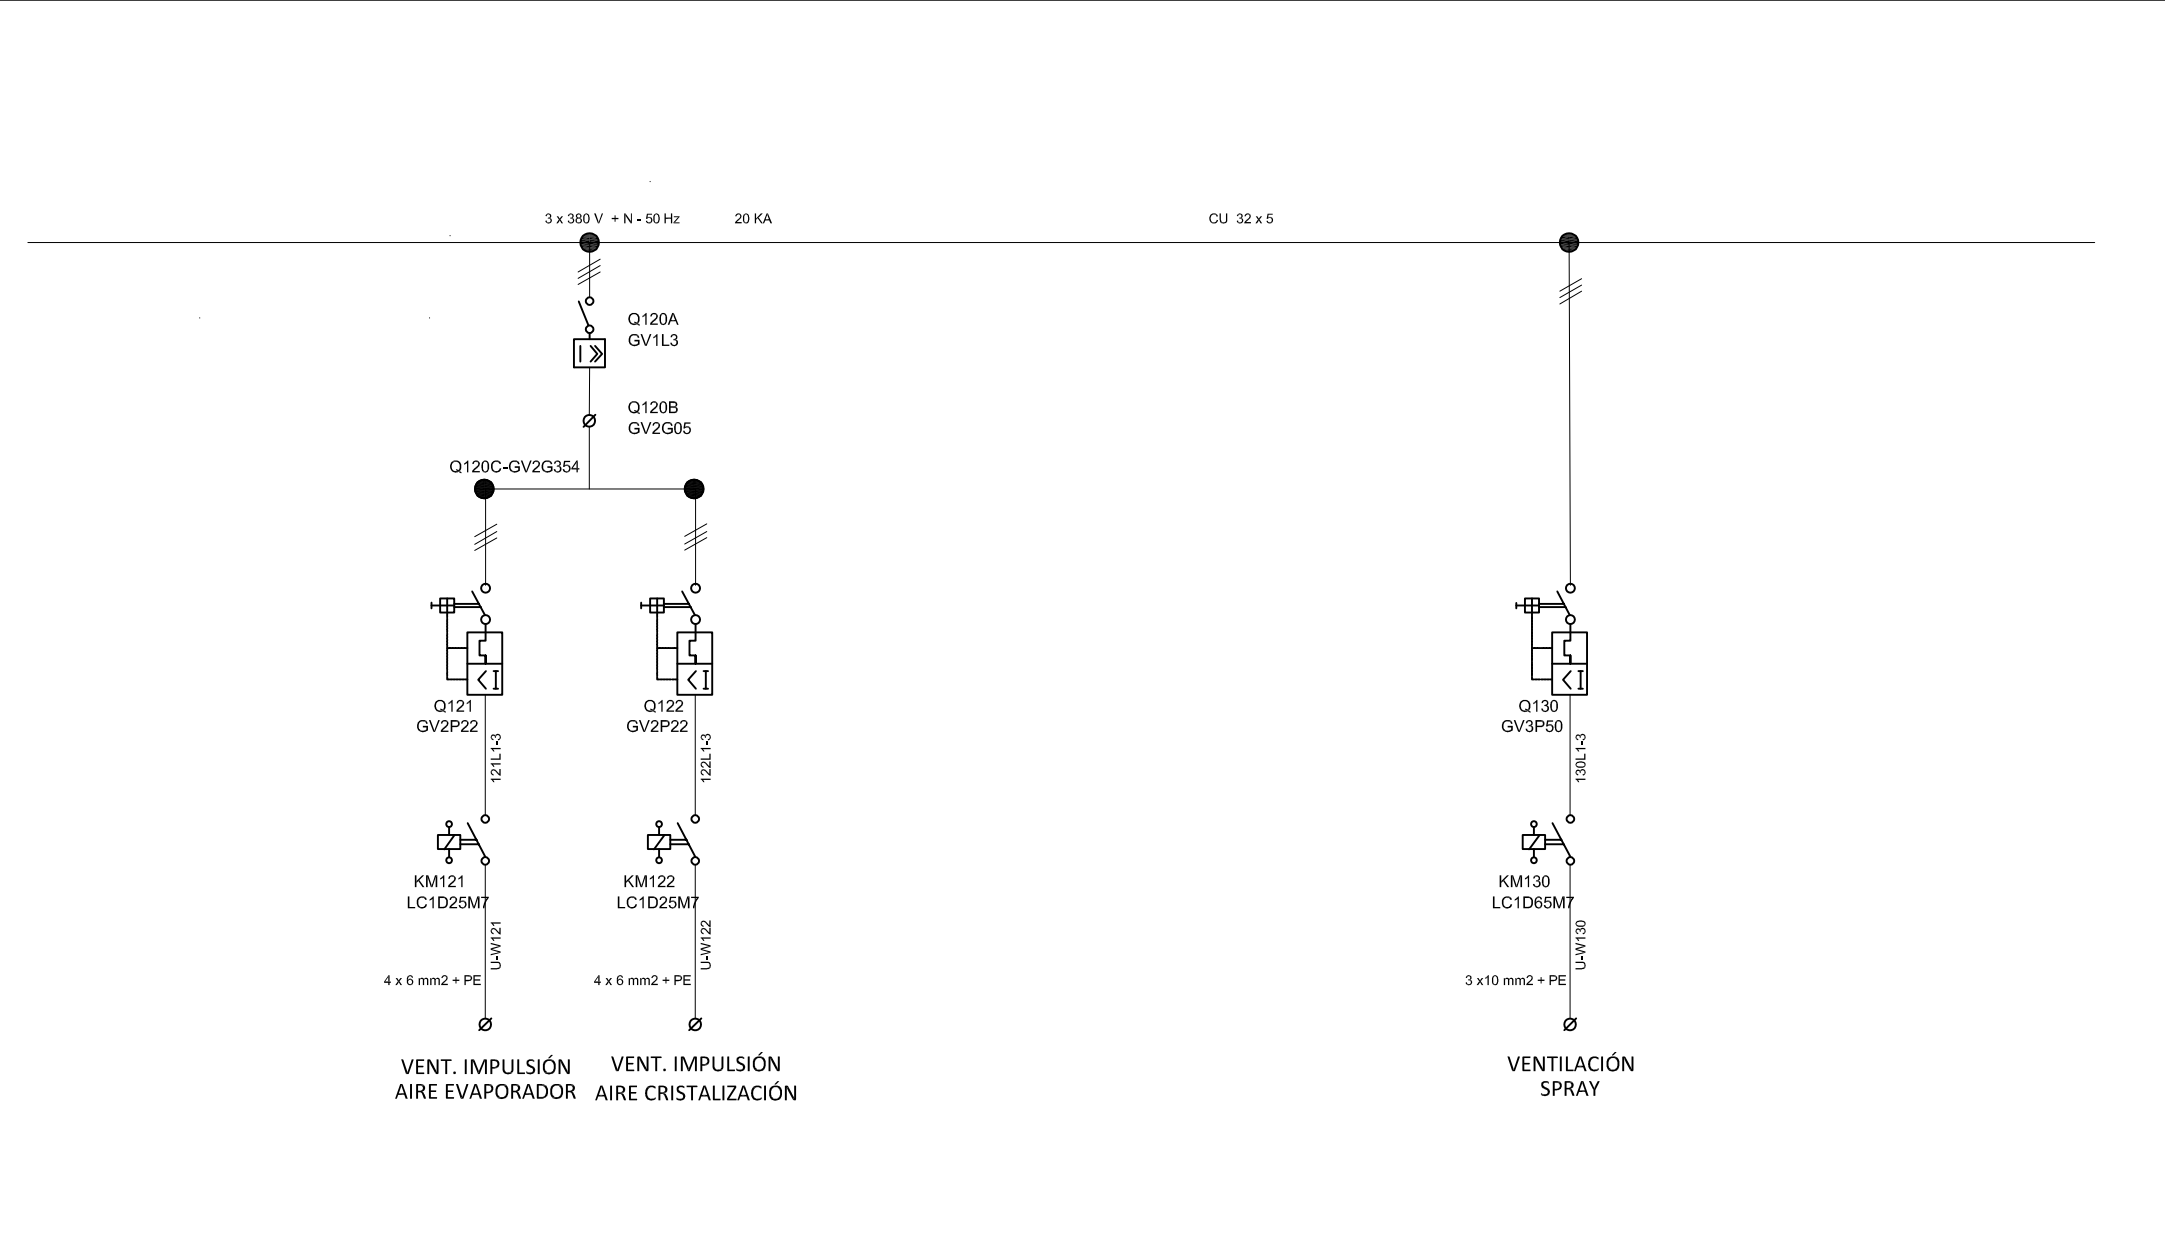

						TABLERO FEM PERMEADO	 SERVICIOS DE INGENIERIA	ESC	S / E
0	EDICION ORIGINAL	—	—	03/03/24				HOJA	8
REV	MODIFICACION	DIB	REV	FECHA				SIGUE	20




							TABLERO FEM PERMEADO	 JPI SERVICIOS DE INGENIERIA		ESC	S / E
0	EDICION ORIGINAL	—	—	03/03/24						HOJA	20
REV	MODIFICACION	DIB	REV	FECHA						SIGUE	21



							TABLERO FEM PERMEADO	 JPI SERVICIOS DE INGENIERIA		ESC	S / E
0	EDICION ORIGINAL	—	—	03/03/24						HOJA	21
REV	MODIFICACION	DIB	REV	FECHA						SIGUE	22



							TABLERO FEM PERMEADO	 JPI SERVICIOS DE INGENIERIA		ESC	S / E
0	EDICION ORIGINAL	—	—	03/03/24						HOJA	22
REV	MODIFICACION	DIB	REV	FECHA						SIGUE	30

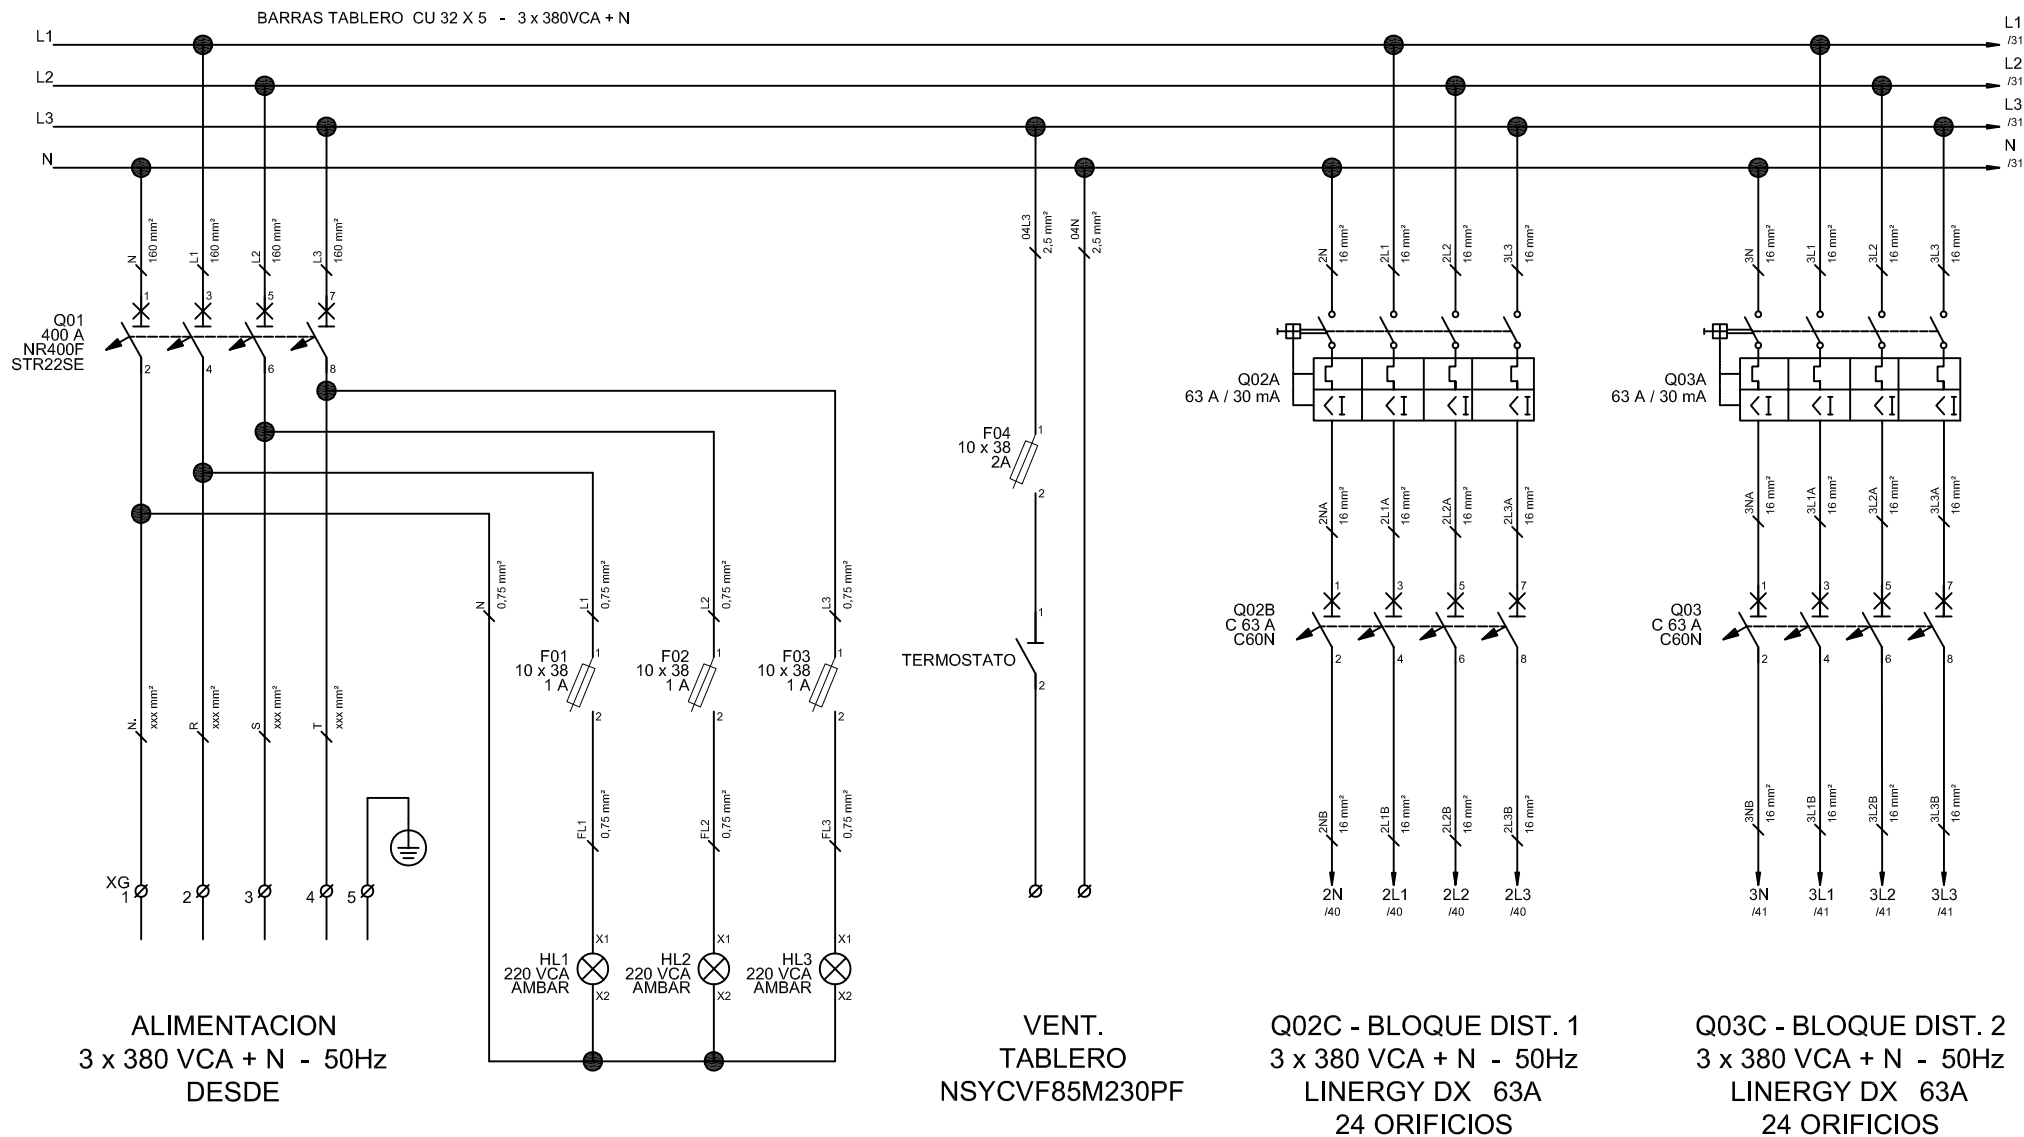


0	EDICION ORIGINAL	—	—	03/03/24
REV	MODIFICACION	DIB	REV	FECHA



TABLERO FEM
PERMEADO



ESC	S / E
HOJA	30
SIGUE	31

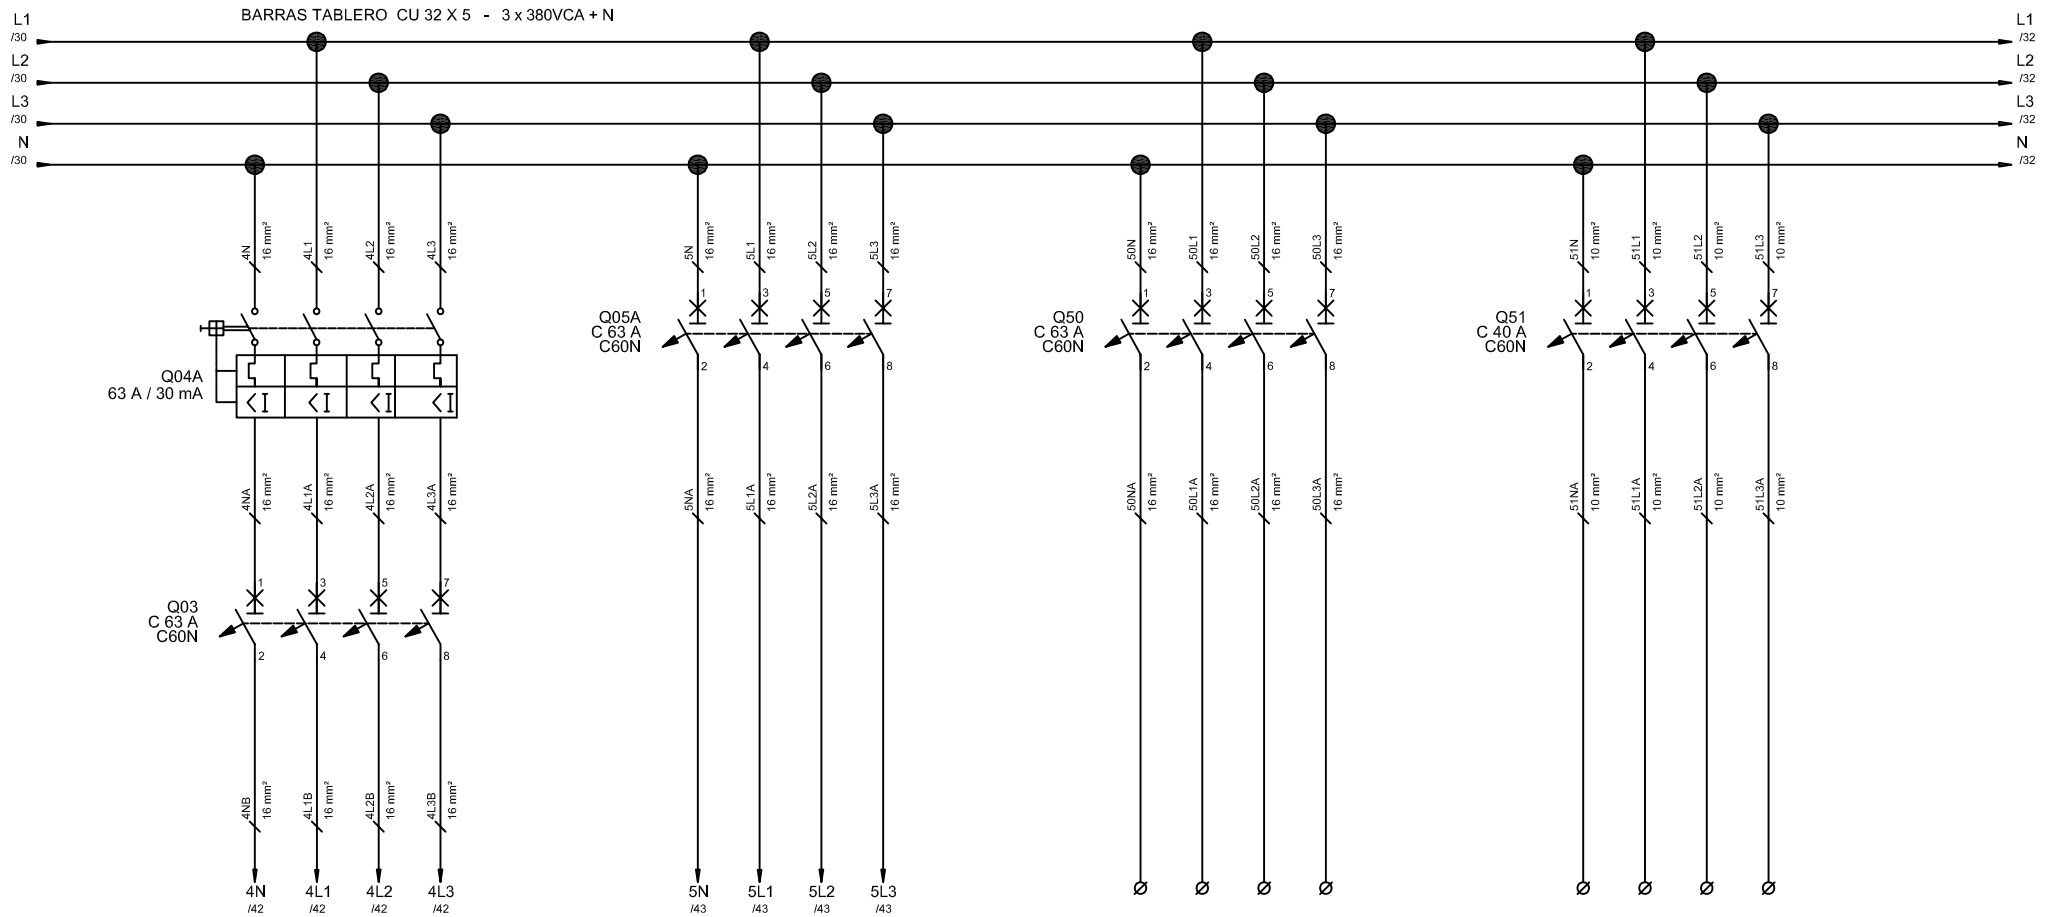

Q04C - BLOQUE DIST. 3
3 x 380 VCA + N - 50Hz
LINERGY DX 63A
24 ORIFICIOS

Q05B - BLOQUE DIST. 4
3 x 380 VCA + N - 50Hz
LINERGY DX 63A
24 ORIFICIOS

VENTILACIÓN DEPO 3

UTA ENV. 2


0	EDICION ORIGINAL	—	—	03/03/24
REV	MODIFICACION	DIB	REV	FECHA



TABLERO FEM
PERMEADO



ESC	S / E
HOJA	31
SIGUE	32

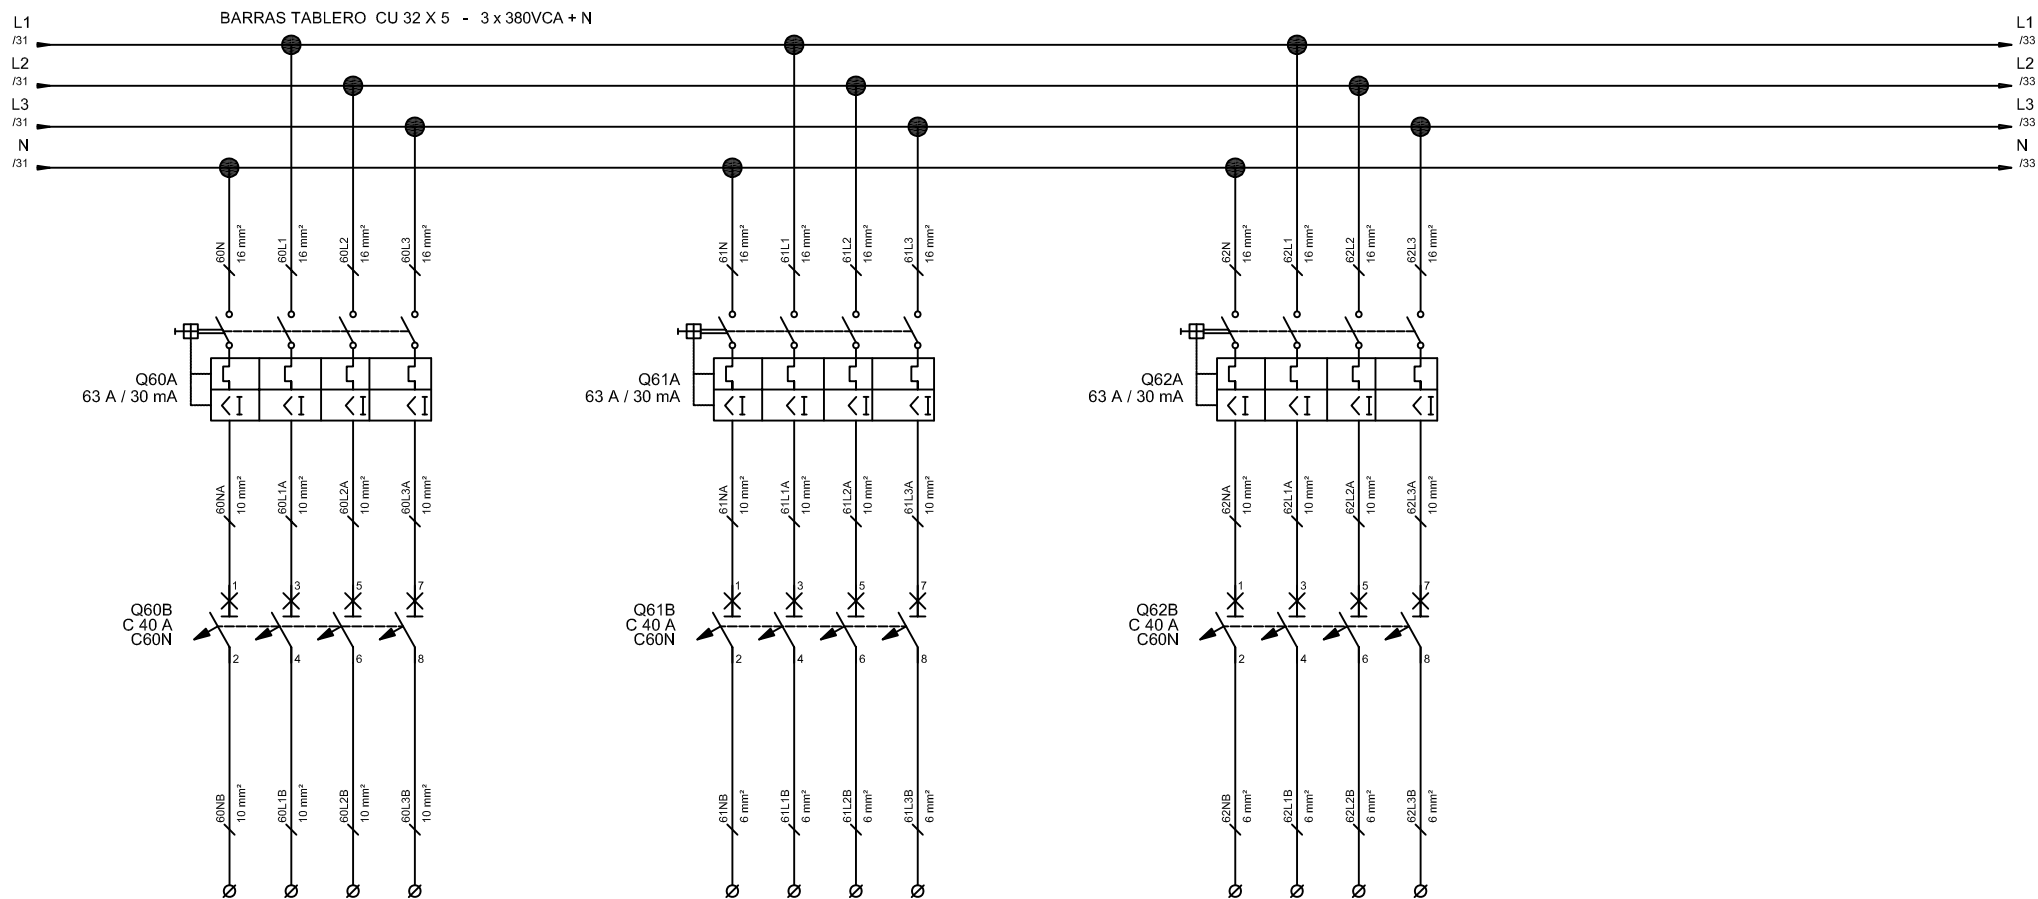

AA MCC PERMEADO POT.

TABLEROS TOMAS EXT.

TABLEROS TOMAS INT.


0	EDICION ORIGINAL	—	—	03/03/24
REV	MODIFICACION	DIB	REV	FECHA



TABLERO FEM
PERMEADO



ESC	S / E
HOJA	32
SIGUE	33

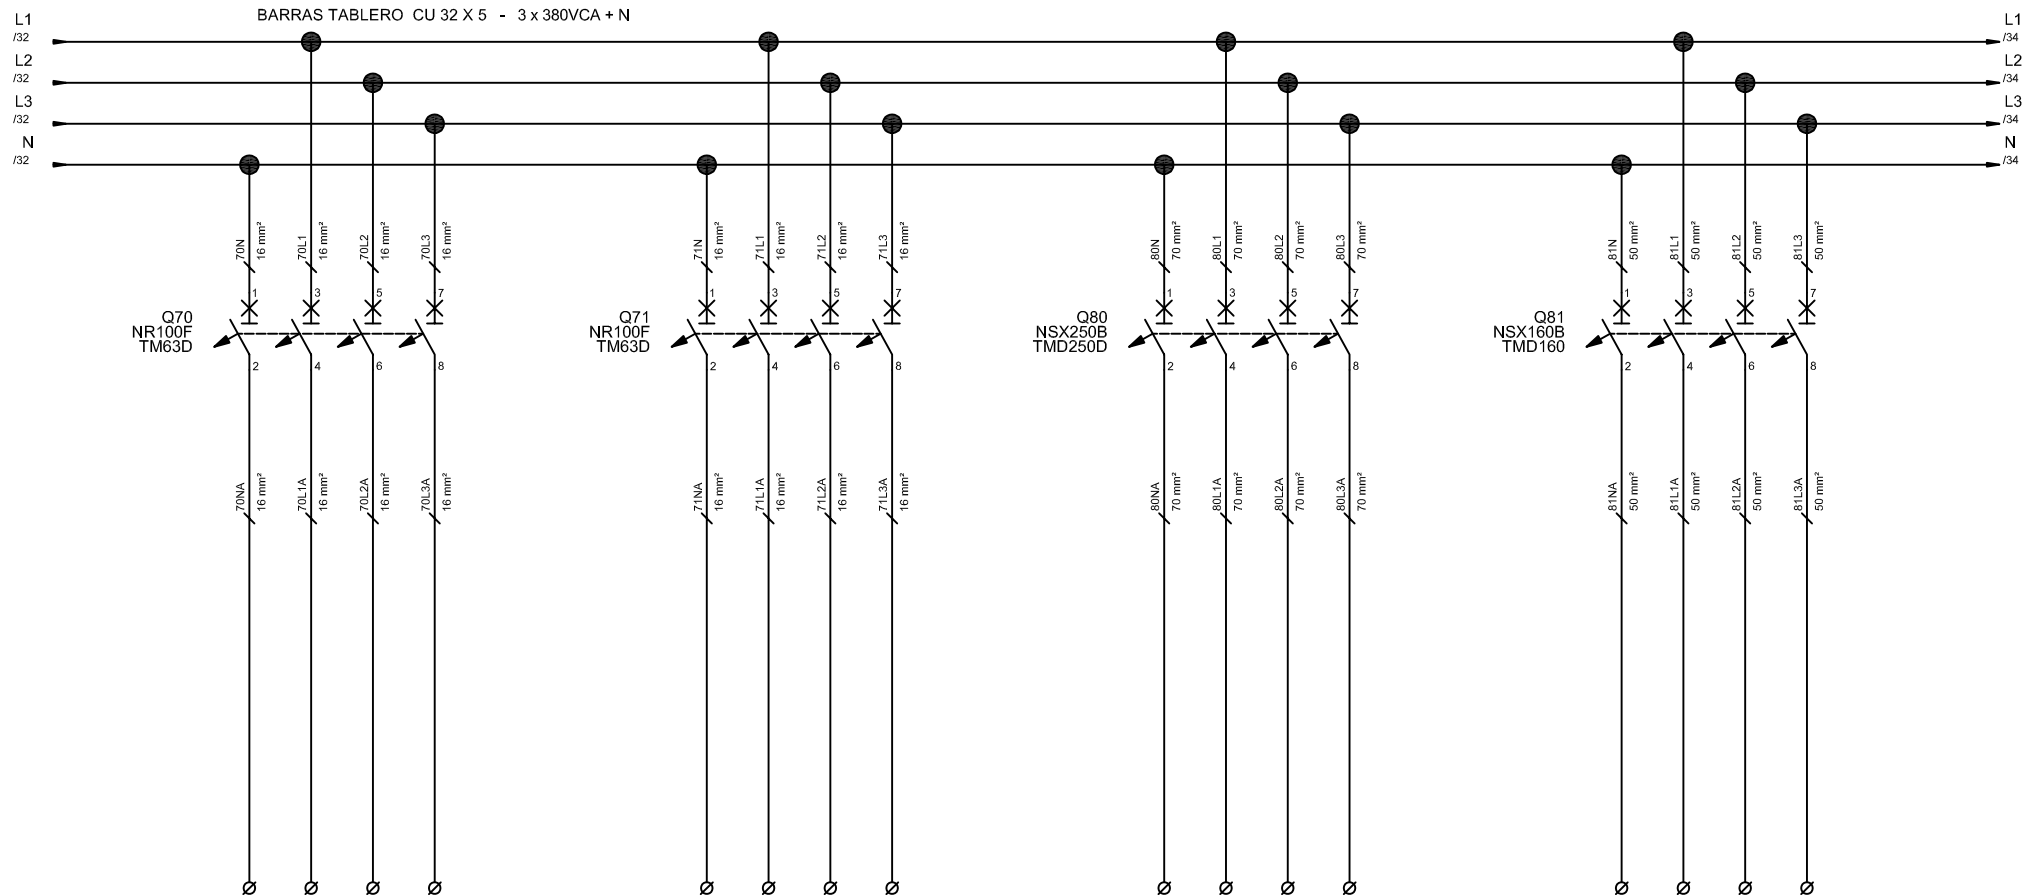

TABLERO
ILUMINACION
T2

TABLERO
ILUMINACION
DEPO 3

TABLERO
DEPOSITO 4

TABLERO
DEPOSITO 5


0	EDICION ORIGINAL	—	—	03/03/24
REV	MODIFICACION	DIB	REV	FECHA



TABLERO FEM
PERMEADO



ESC	S / E
HOJA	33
SIGUE	34

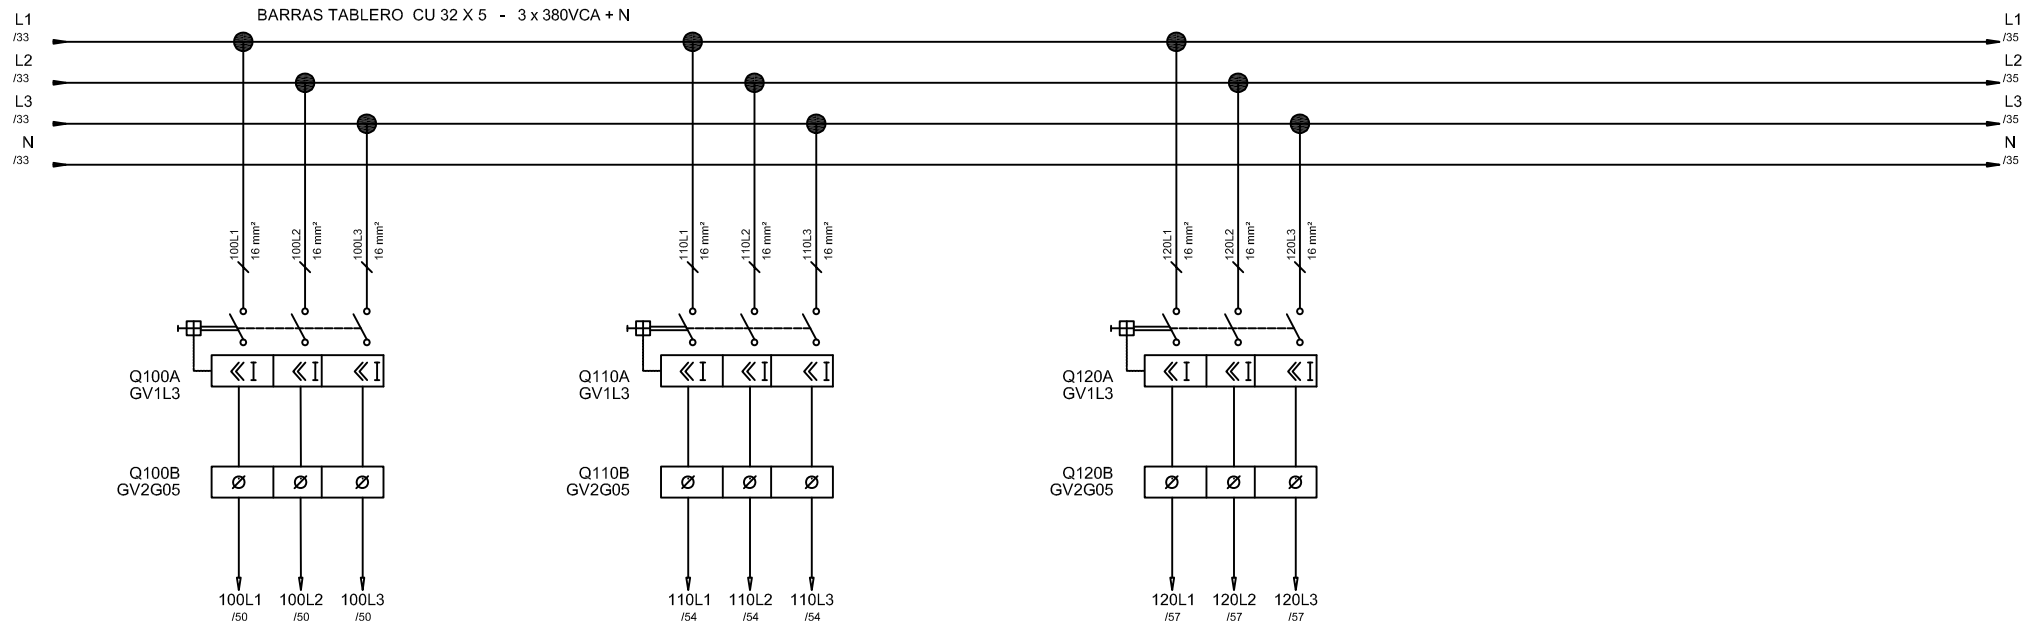

Q100C - PEINE DIST.
GV2G554+GV2G454

Q110C - PEINE DIST.
GV2G554+GV2G354

Q120C - PEINE DIST.
GV2G354


0	EDICION ORIGINAL	—	—	03/03/24
REV	MODIFICACION	DIB	REV	FECHA



TABLERO FEM
PERMEADO



ESC	S / E
HOJA	34
SIGUE	35

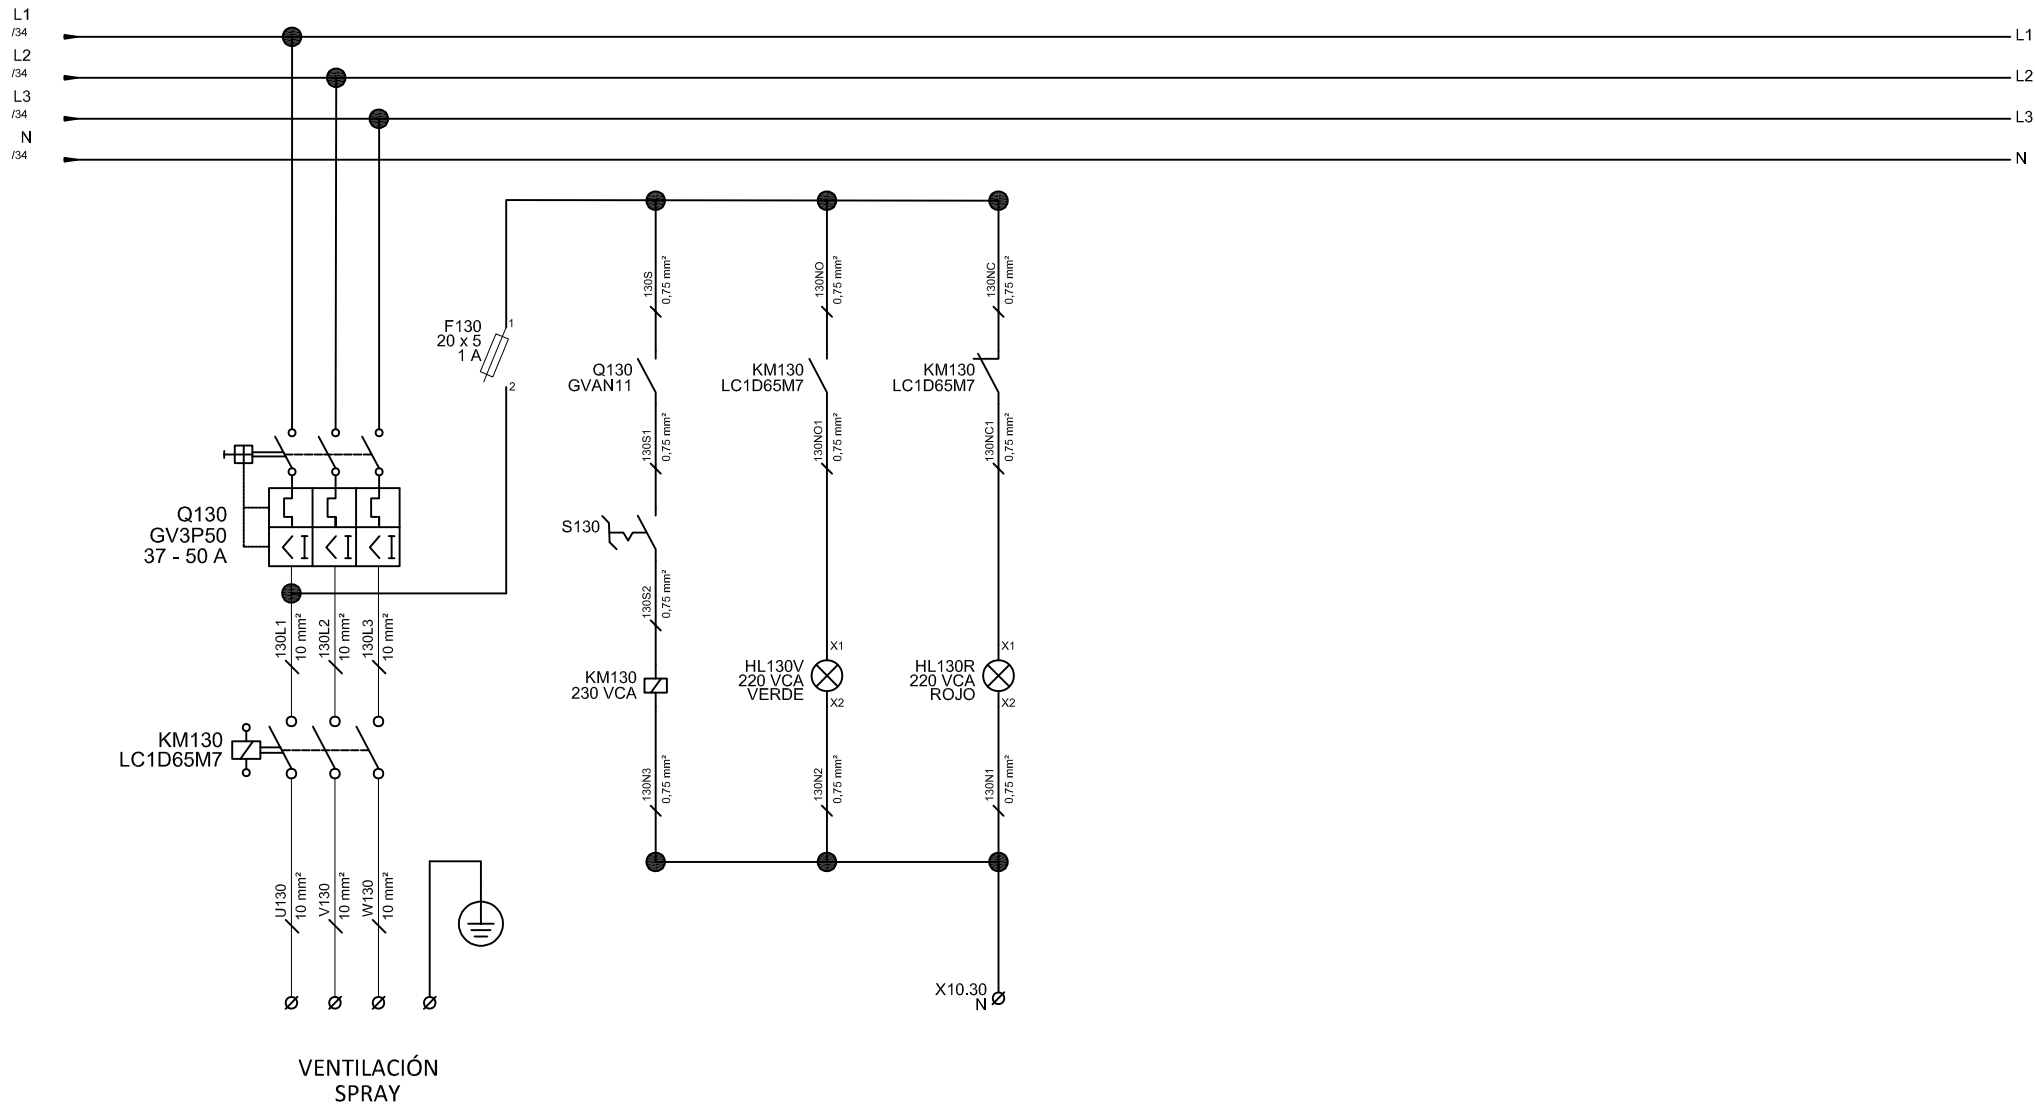


0	EDICION ORIGINAL	—	—	03/03/24
REV	MODIFICACION	DIB	REV	FECHA



TABLERO FEM
PERMEADO



ESC	S / E
HOJA	35
SIGUE	40

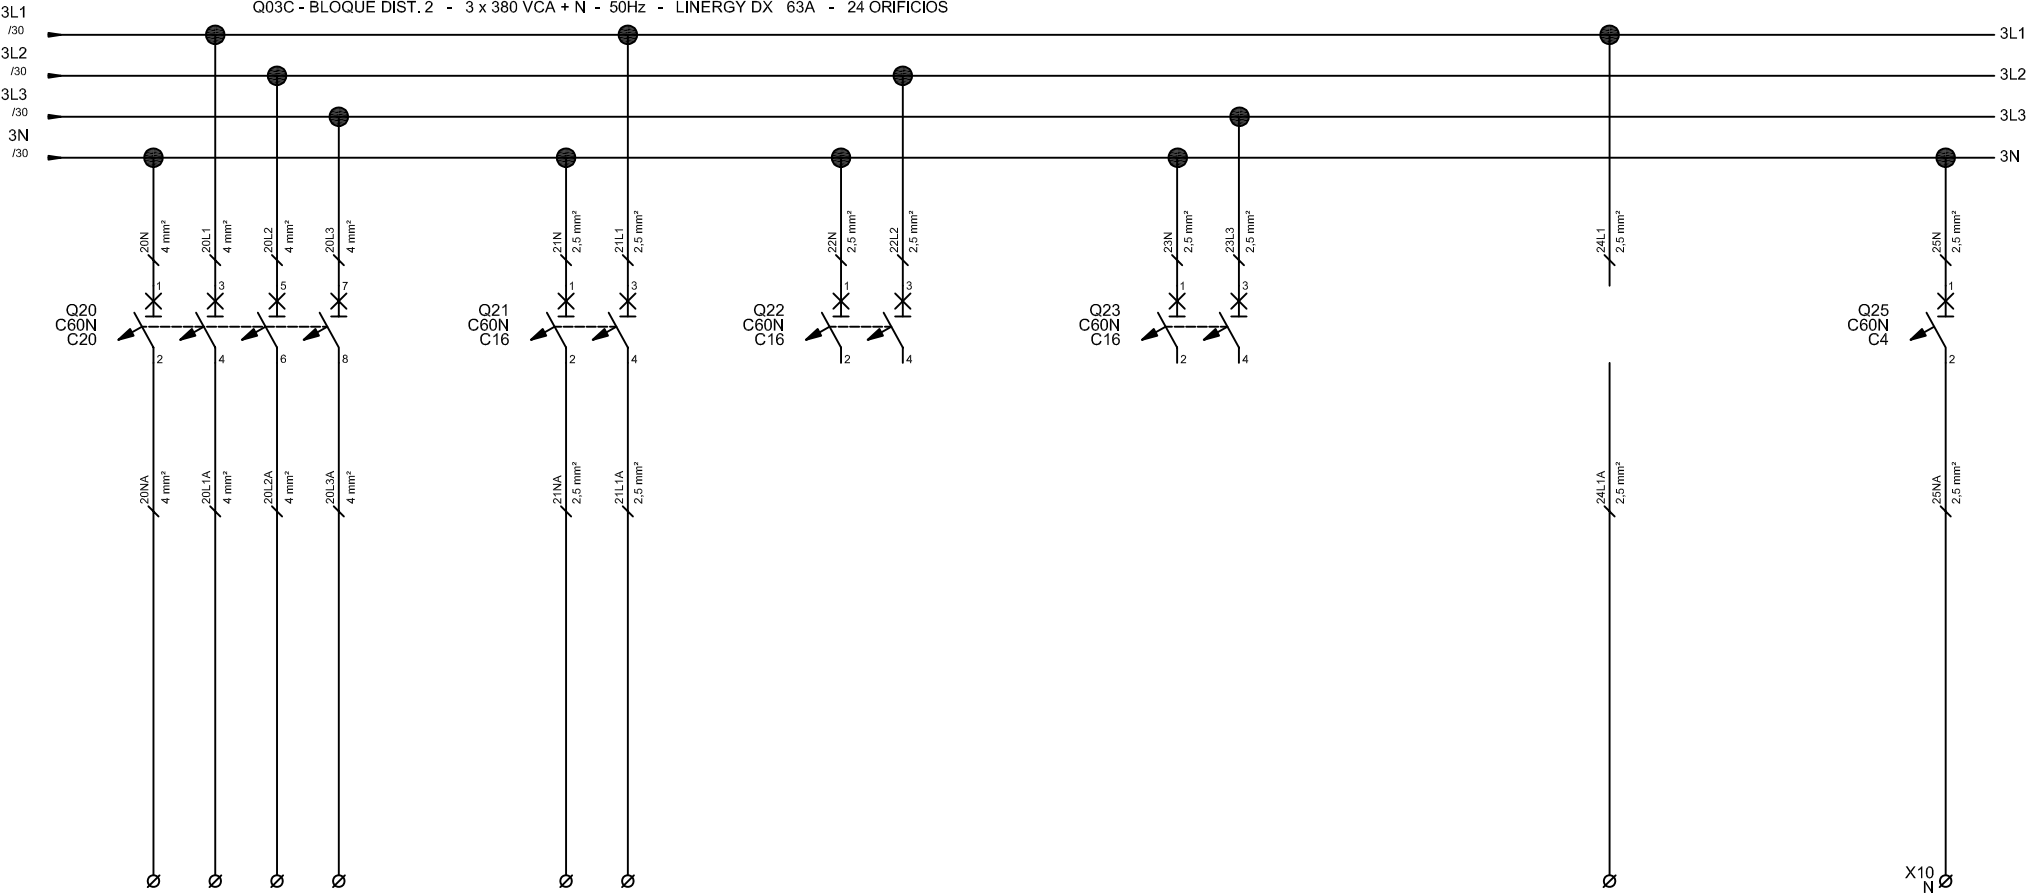

AA
DESHUMIDIFIC
IMP 2

UTA ENV. 2 Y
PLC VENT.
DEPO 3

RESERVA

RESERVA

COMANDO
BBA AGUA

COMANDOS
TABLERO


0	EDICION ORIGINAL	—	—	03/03/24
REV	MODIFICACION	DIB	REV	FECHA




TABLERO FEM
PERMEADO




ESC	S / E
HOJA	41
SIGUE	42

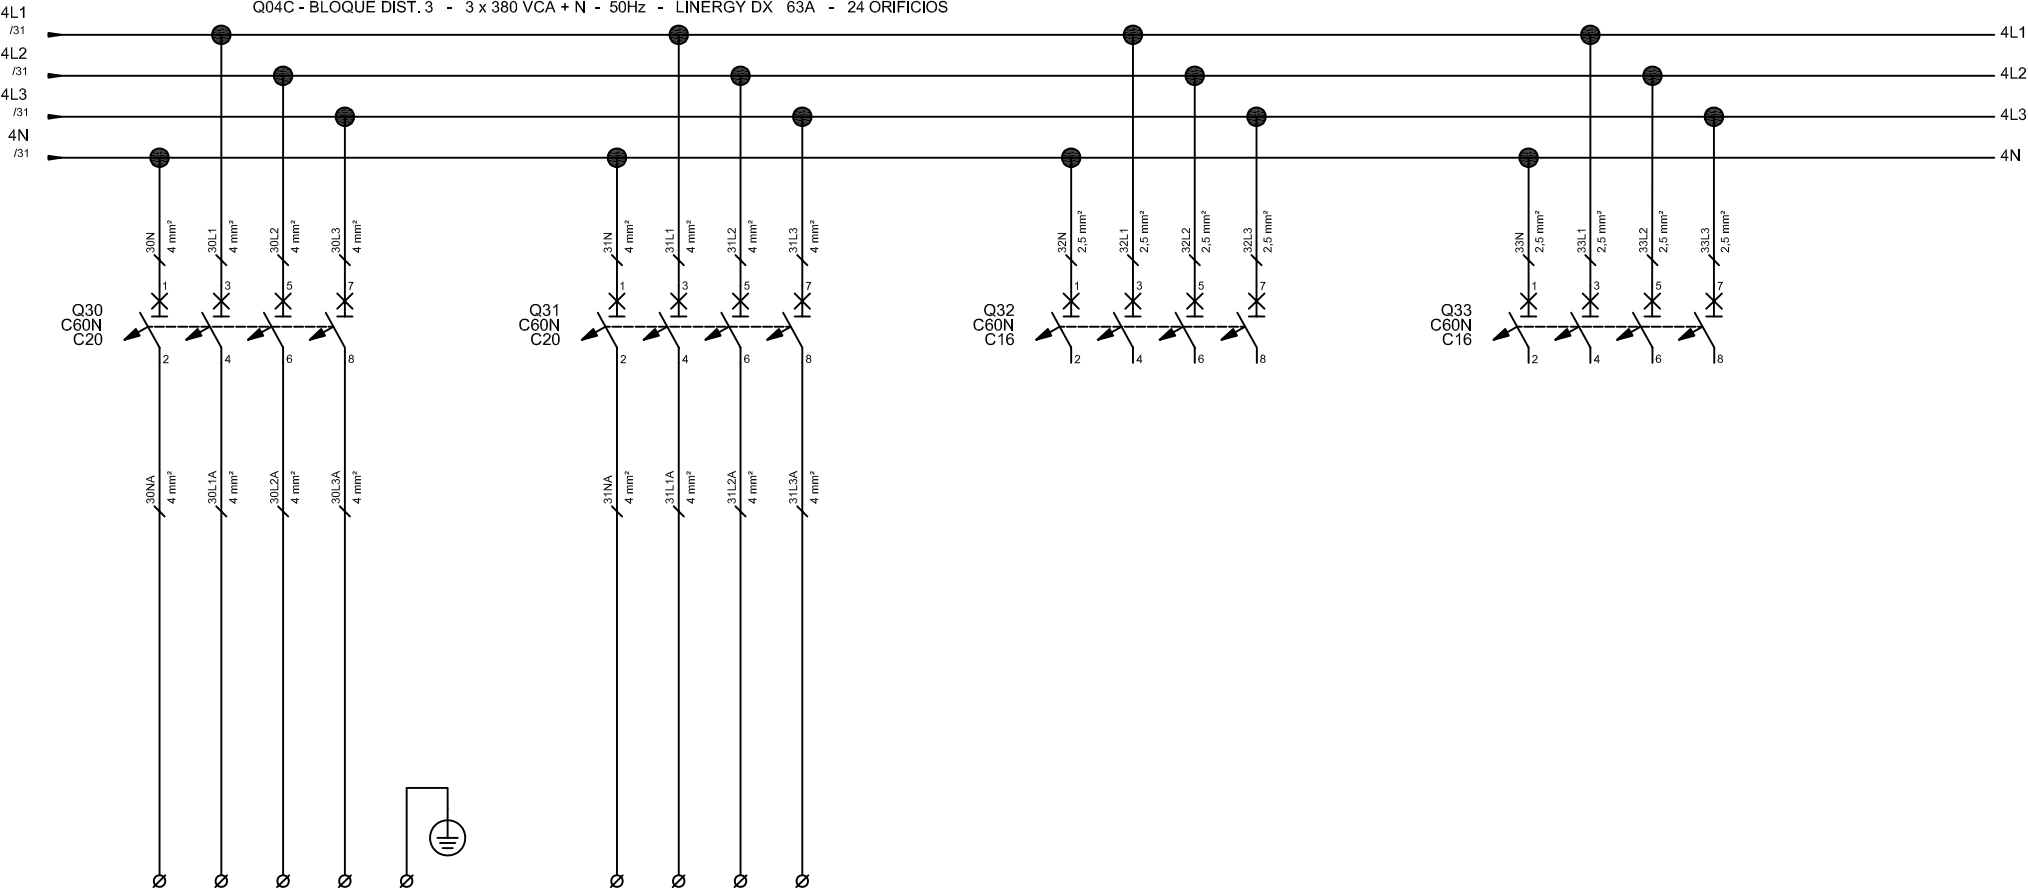

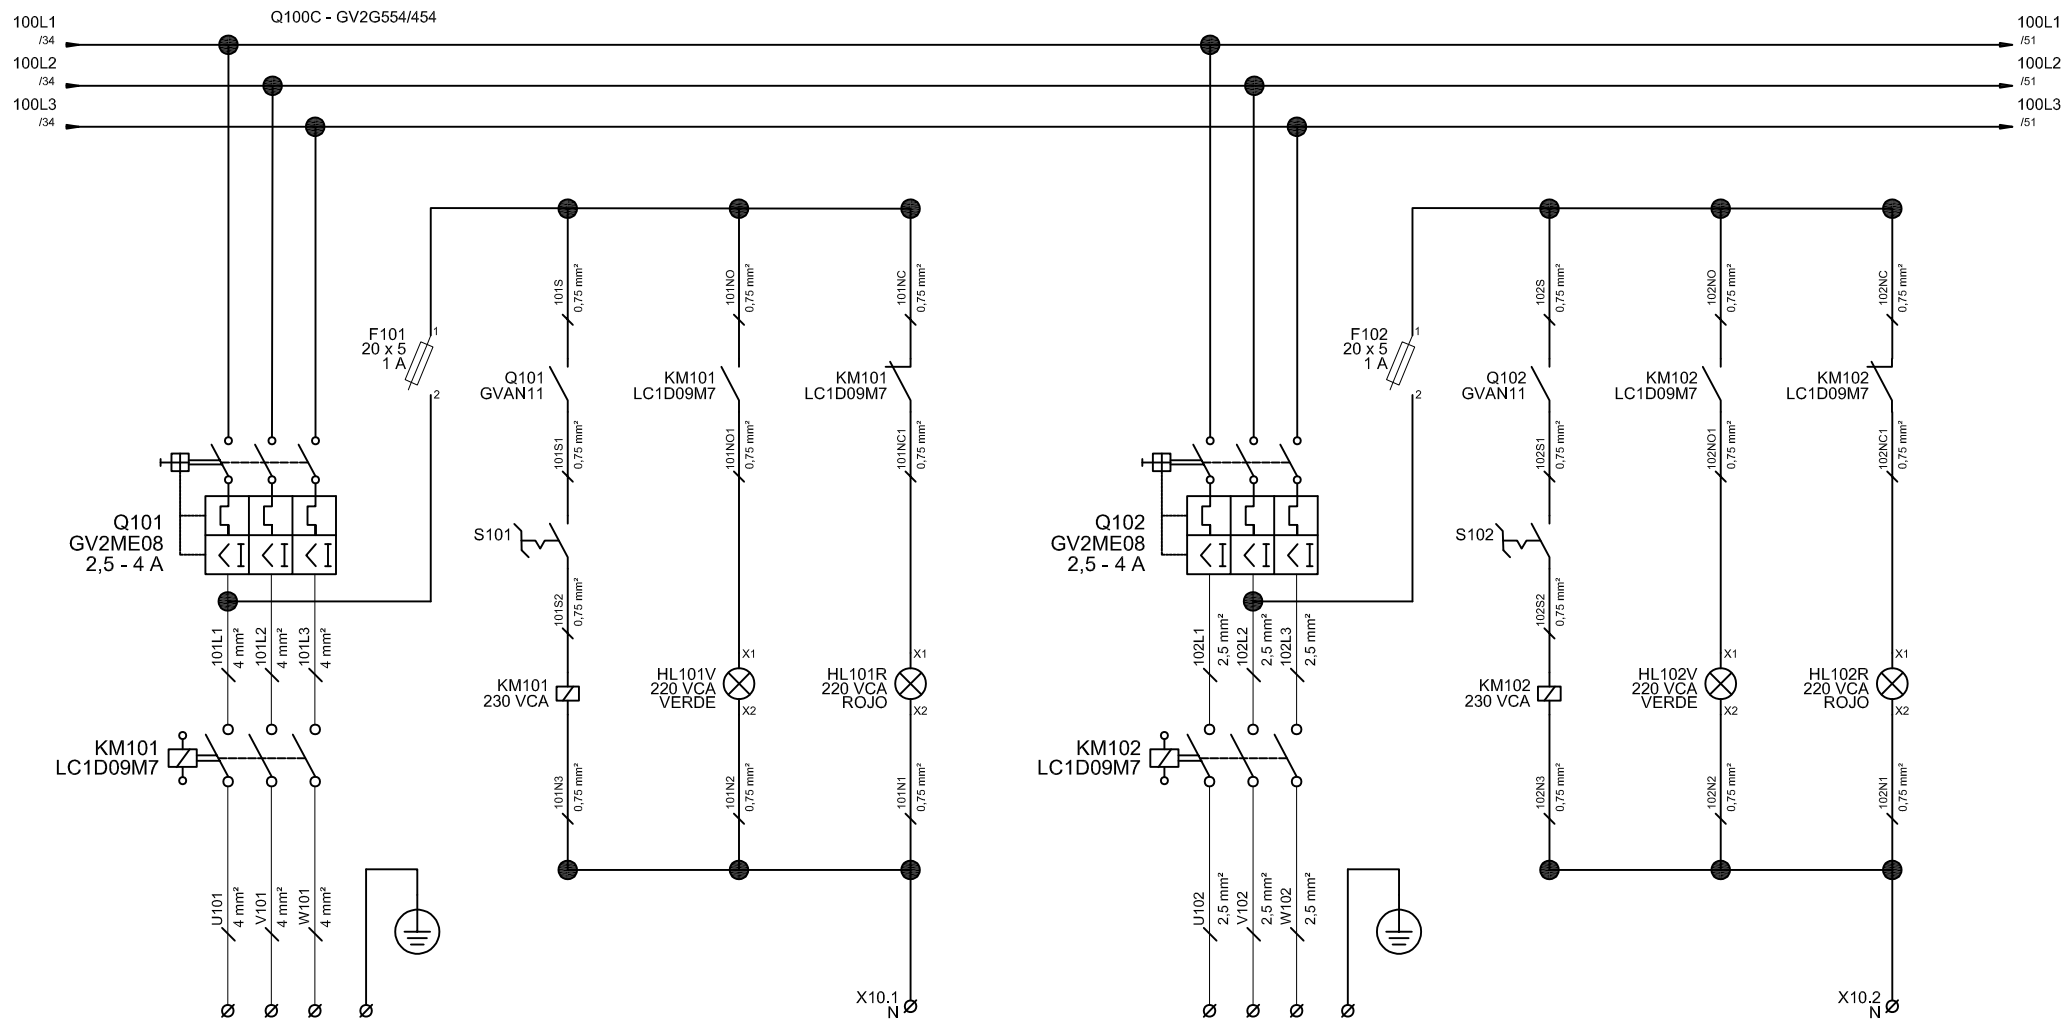

BBA AGUA
PISTOLA
SPRAY


EXTRACTOR DE
AIRE 1
EVAPORADOR

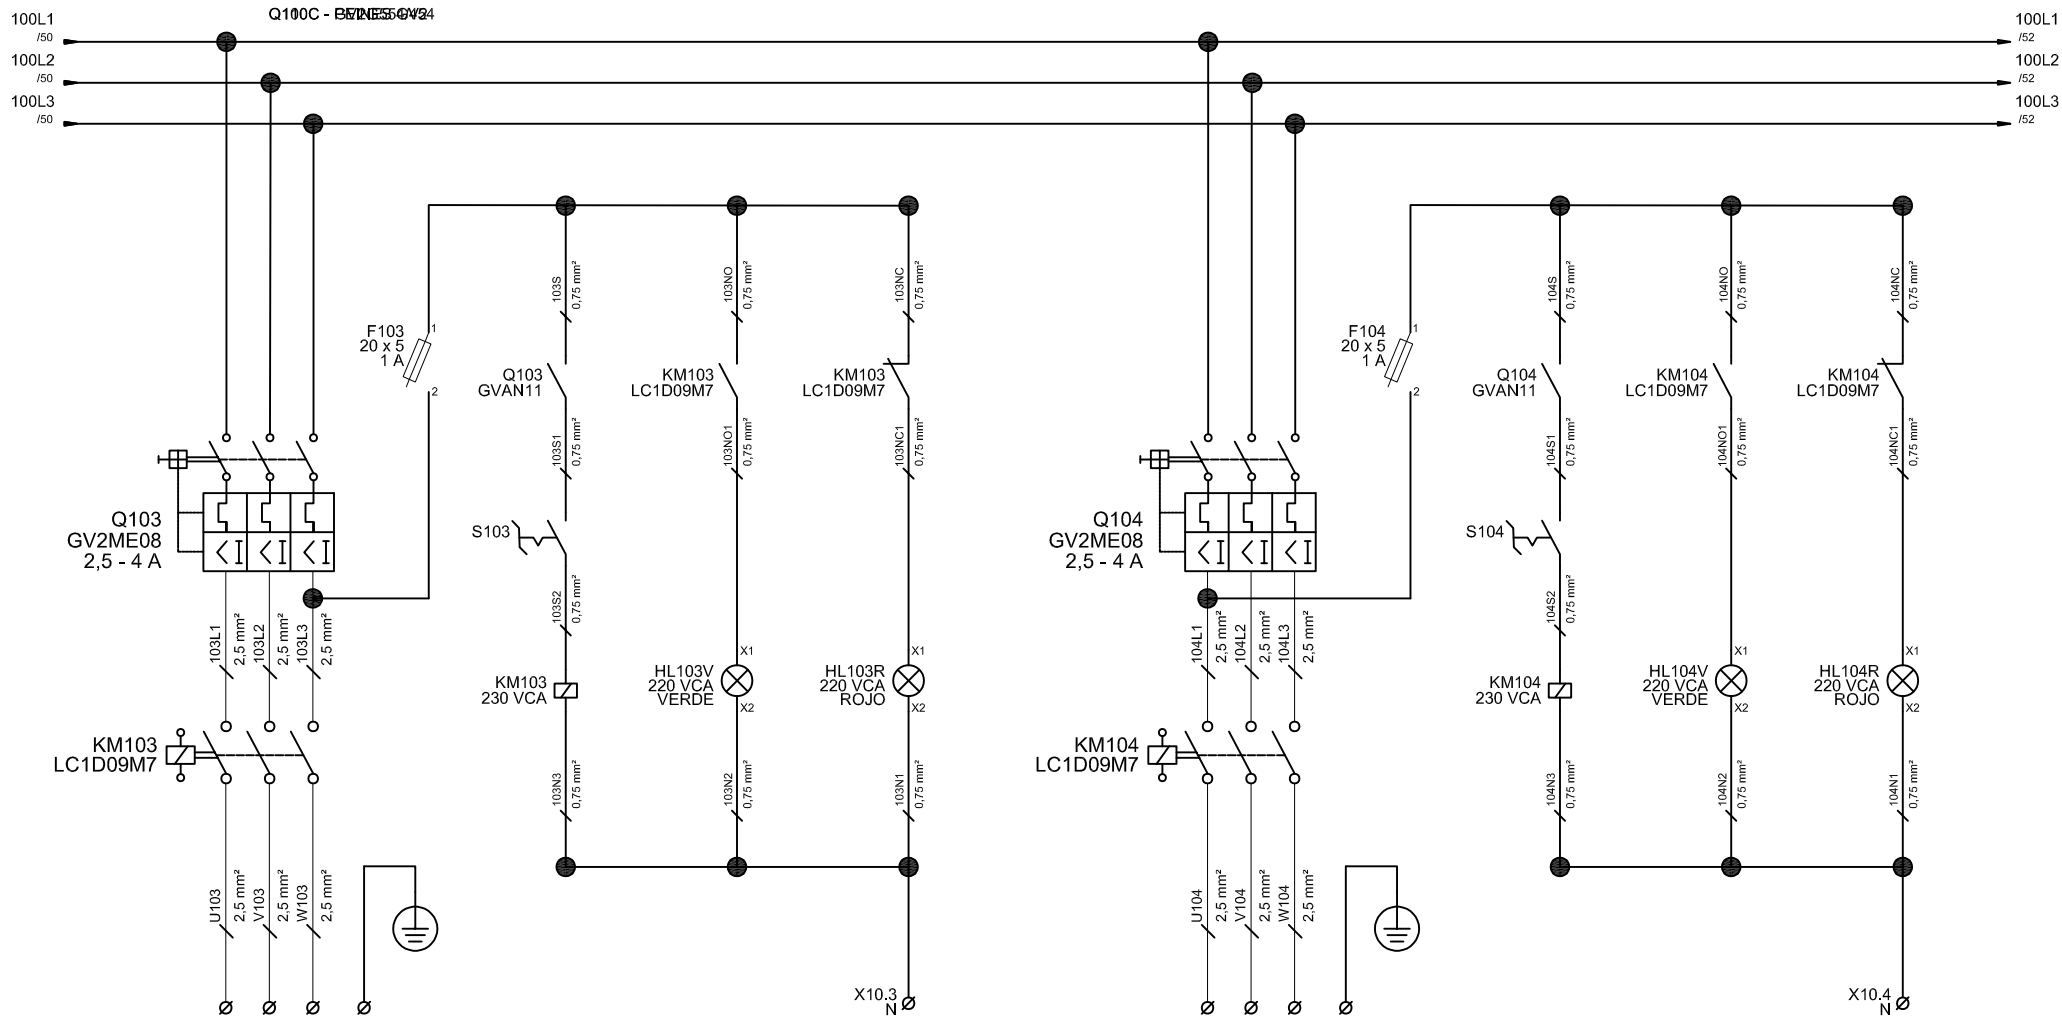

EXTRACTOR DE
AIRE 2
EVAPORADOR

EXTRACTOR DE
AIRE 1
CALENTADOR


						TABLERO FEM PERMEADO	 SERVICIOS DE INGENIERIA	ESC	S / E
0	EDICION ORIGINAL	—	—	03/03/24				HOJA	51
REV	MODIFICACION	DIB	REV	FECHA				SIGUE	52

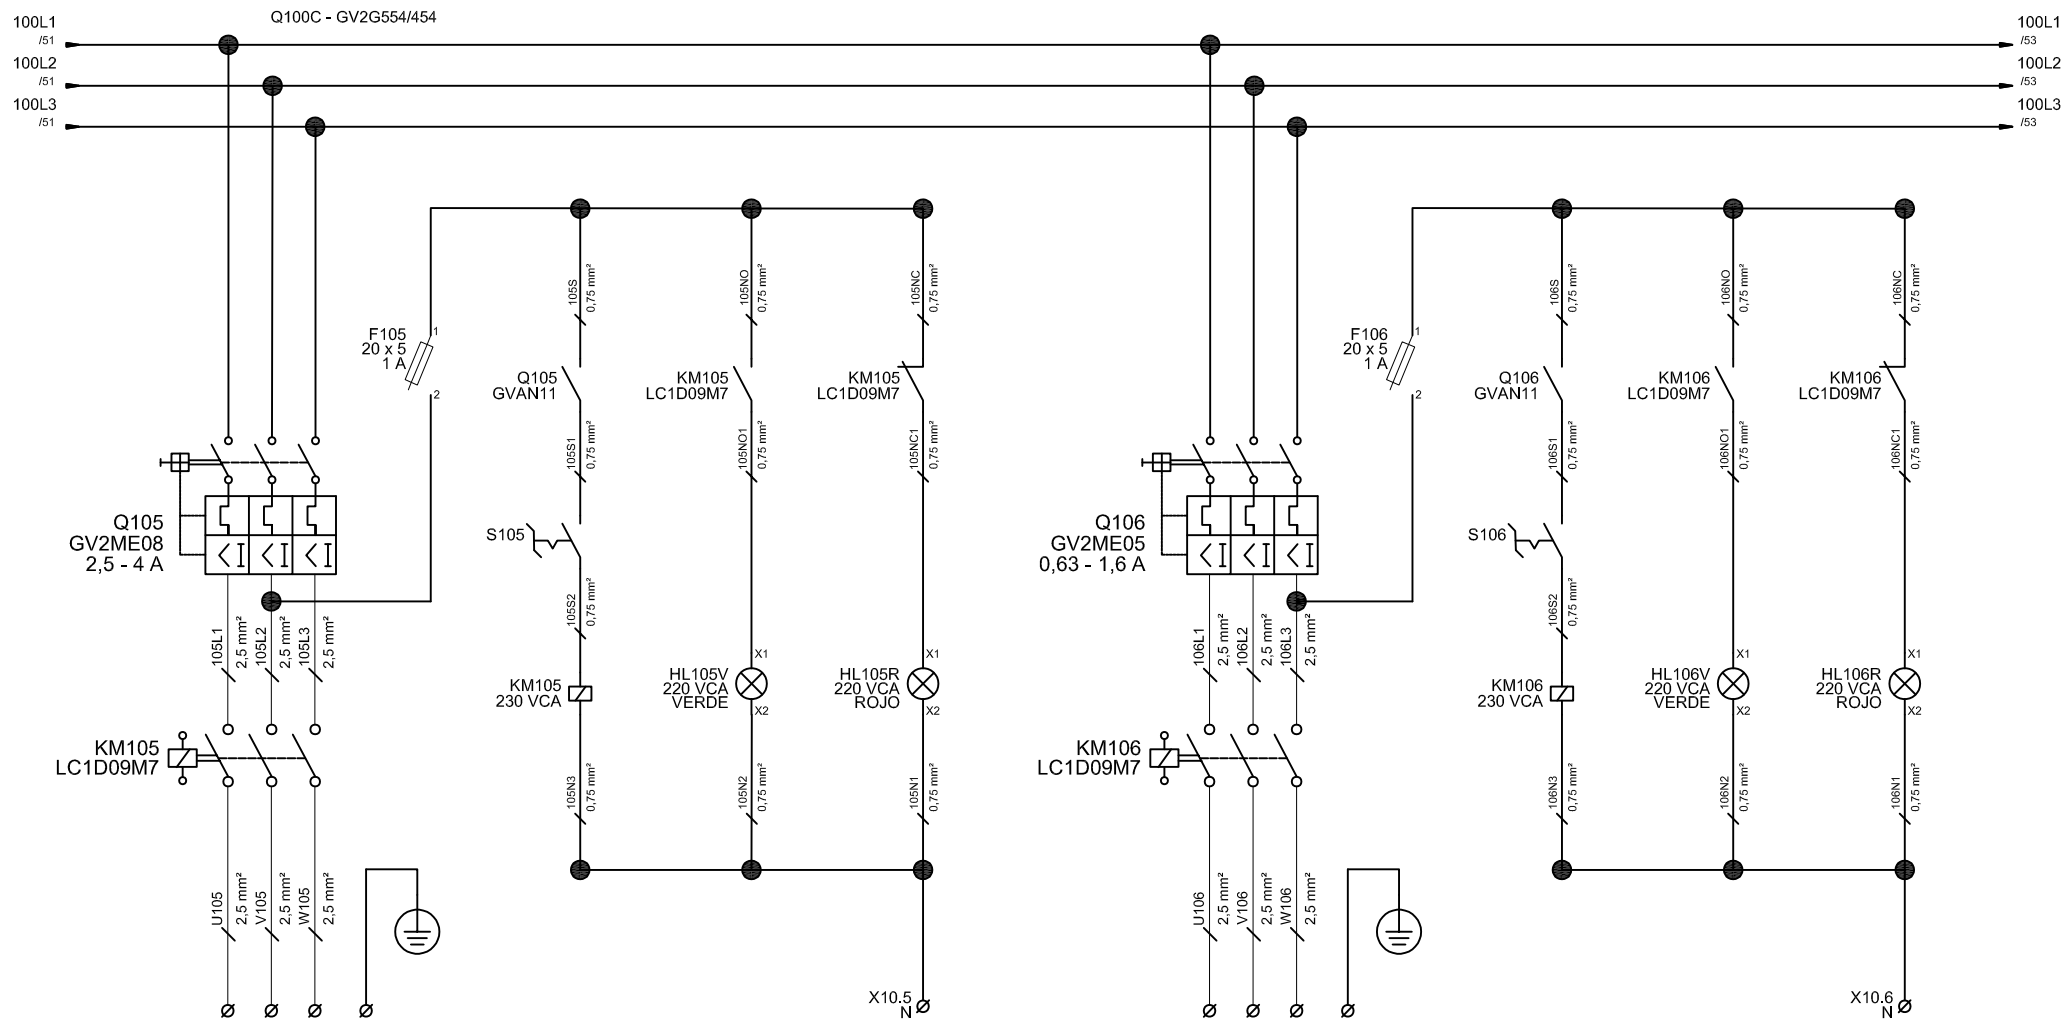

EXTRACTOR DE
AIRE 2
CALENTADOR


EXTRACTOR DE
AIRE CIP
SPRAY

						TABLERO FEM PERMEADO	 SERVICIOS DE INGENIERIA	ESC	S / E
0	EDICION ORIGINAL	—	—	03/03/24				HOJA	52
REV	MODIFICACION	DIB	REV	FECHA				SIGUE	53

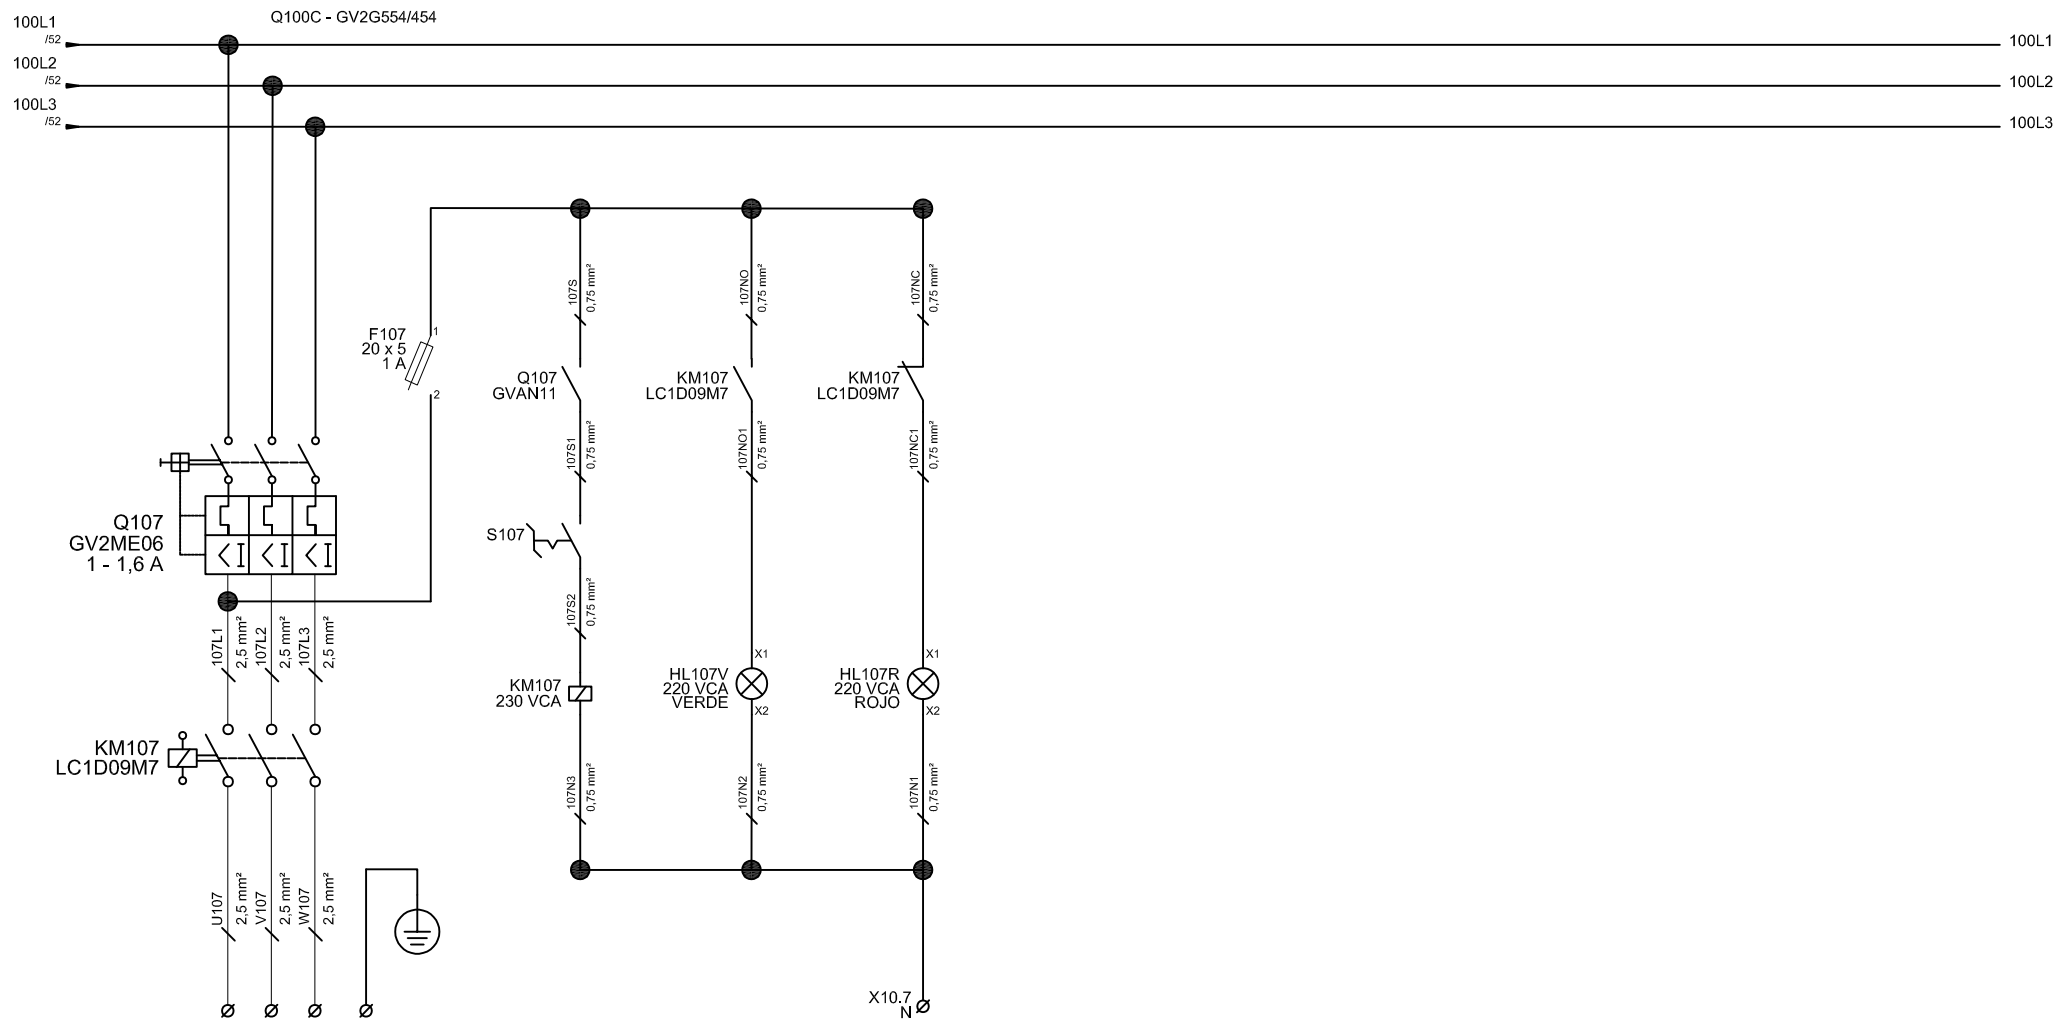


EXTRACTOR
DE AIRE
REPUESTOS

						TABLERO FEM PERMEADO	 SERVICIOS DE INGENIERIA	ESC	S / E
0	EDICION ORIGINAL	—	—	03/03/24				HOJA	53
REV	MODIFICACION	DIB	REV	FECHA				SIGUE	54

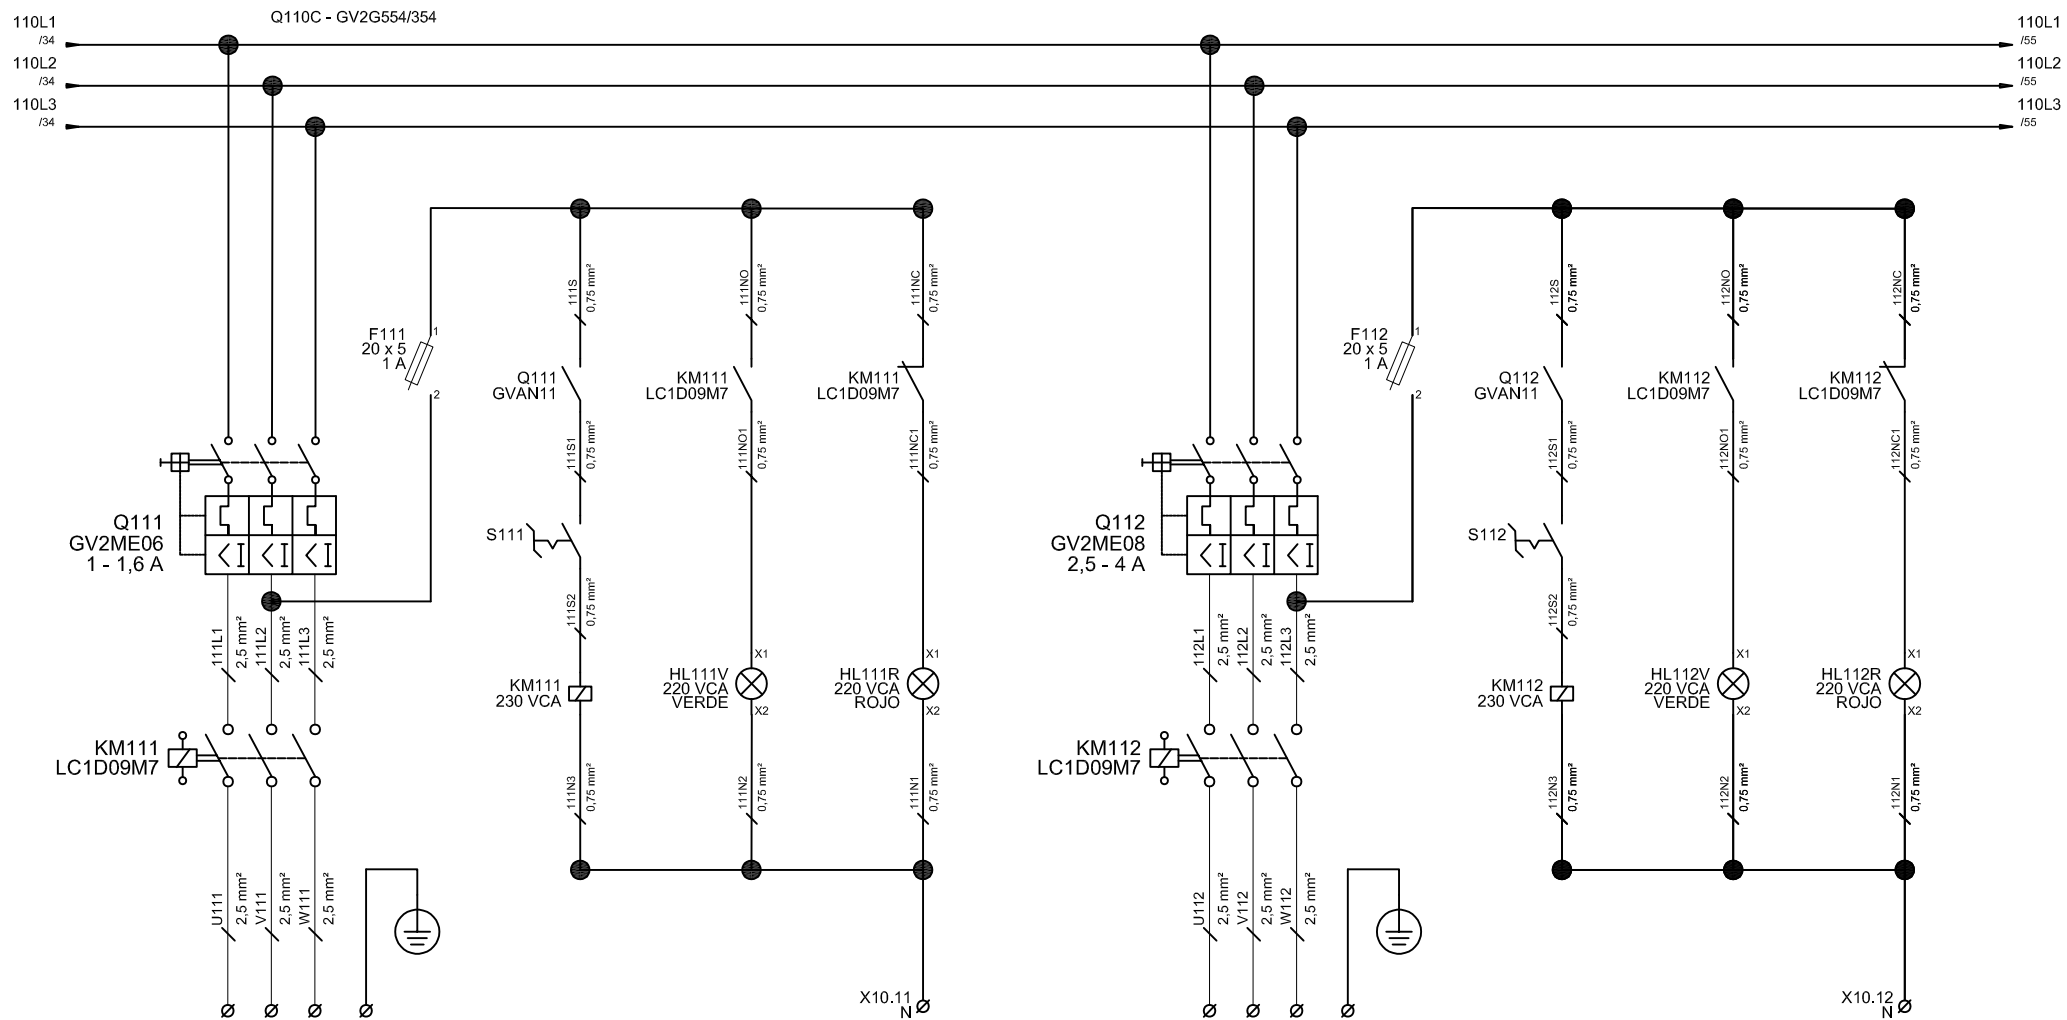


EXTRACTOR
DE AIRE
CIP 547

EXTRACTOR DE
AIRE CHILLERS

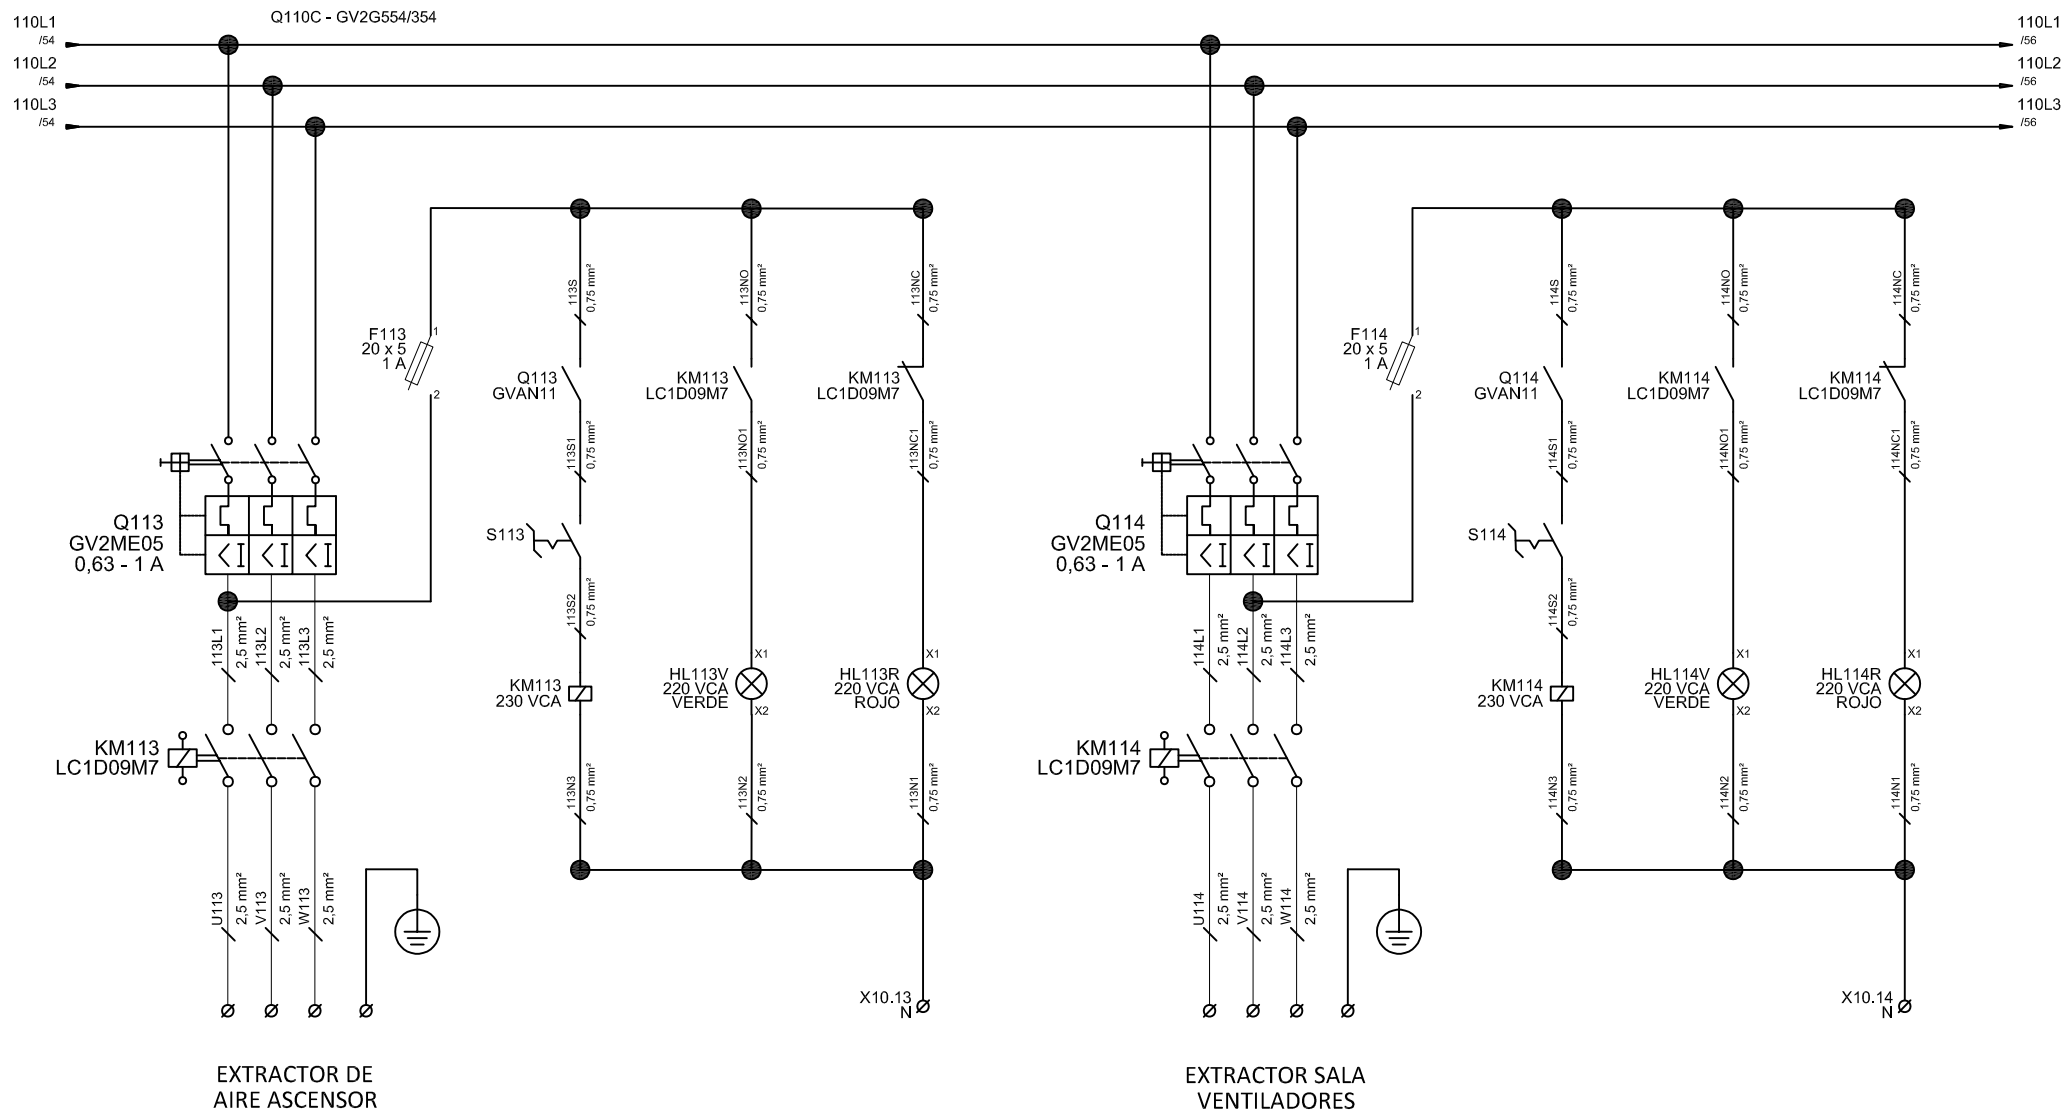

						TABLERO FEM PERMEADO	 SERVICIOS DE INGENIERIA	ESC	S / E
0	EDICION ORIGINAL	—	—	03/03/24				HOJA	55
REV	MODIFICACION	DIB	REV	FECHA				SIGUE	56

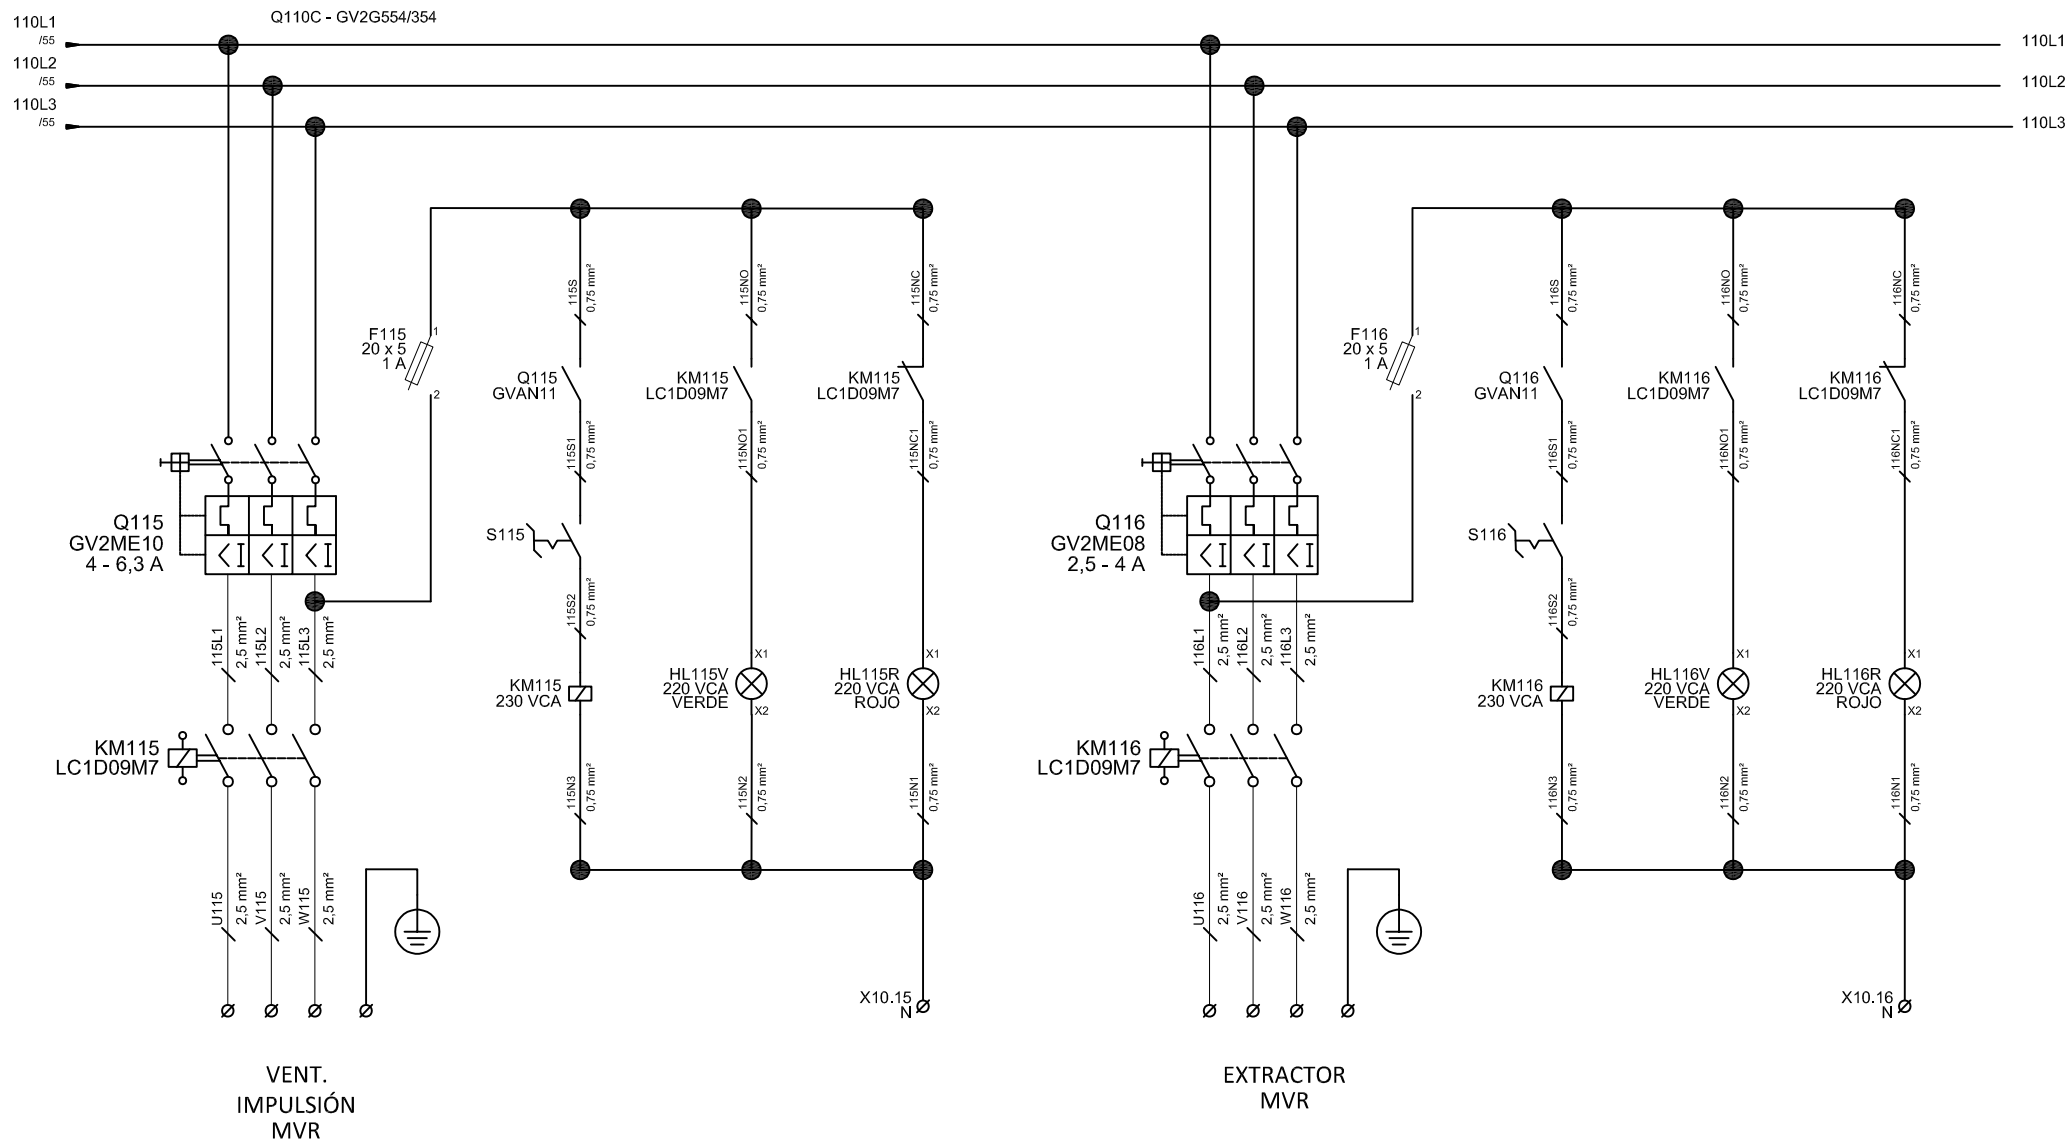


0	EDICION ORIGINAL	—	—	03/03/24
REV	MODIFICACION	DIB	REV	FECHA



TABLERO FEM
PERMEADO




ESC	S / E
HOJA	56
SIGUE	57

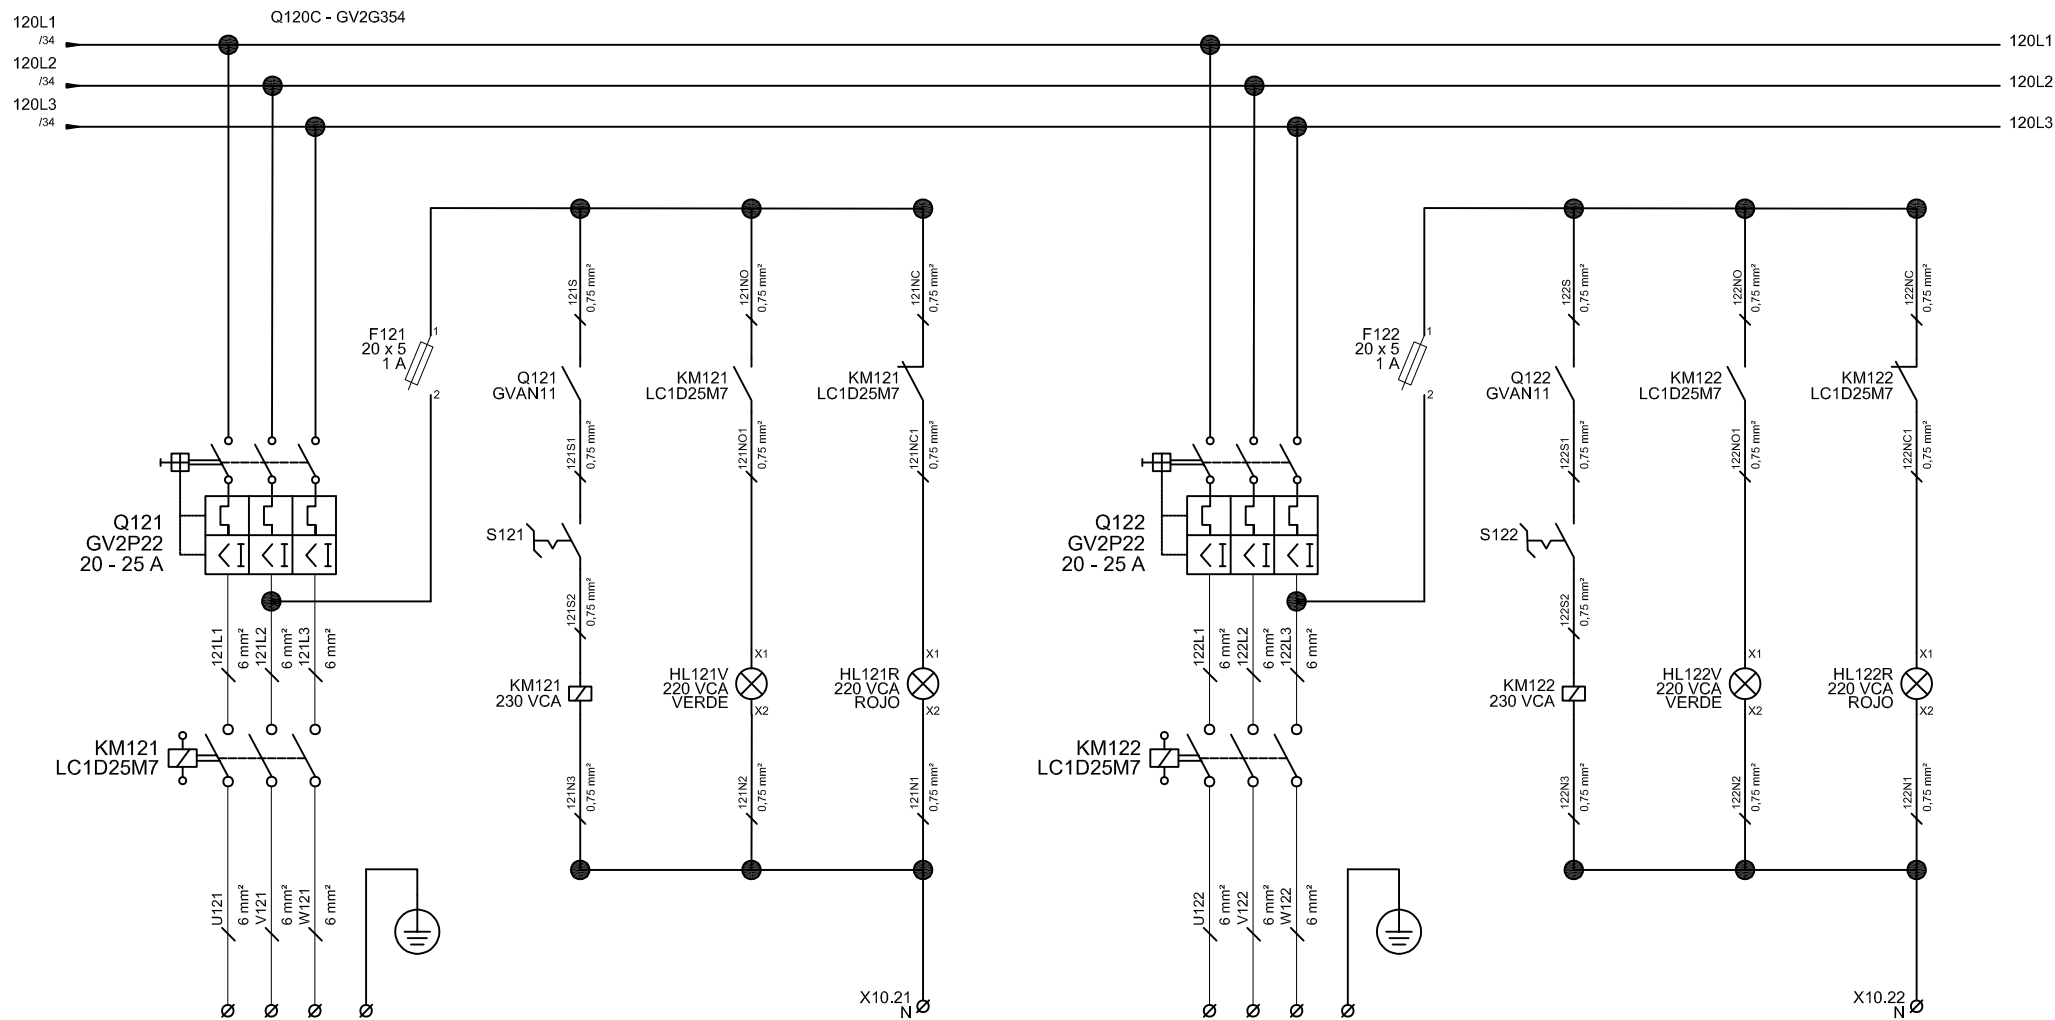

VENT. IMPULSIÓN
AIRE
EVAPORADOR

VENT. IMPULSIÓN
AIRE
CRISTALIZACIÓN

						TABLERO FEM PERMEADO	 SERVICIOS DE INGENIERIA	ESC	S / E
0	EDICION ORIGINAL	—	—	03/03/24				HOJA	57
REV	MODIFICACION	DIB	REV	FECHA				SIGUE	

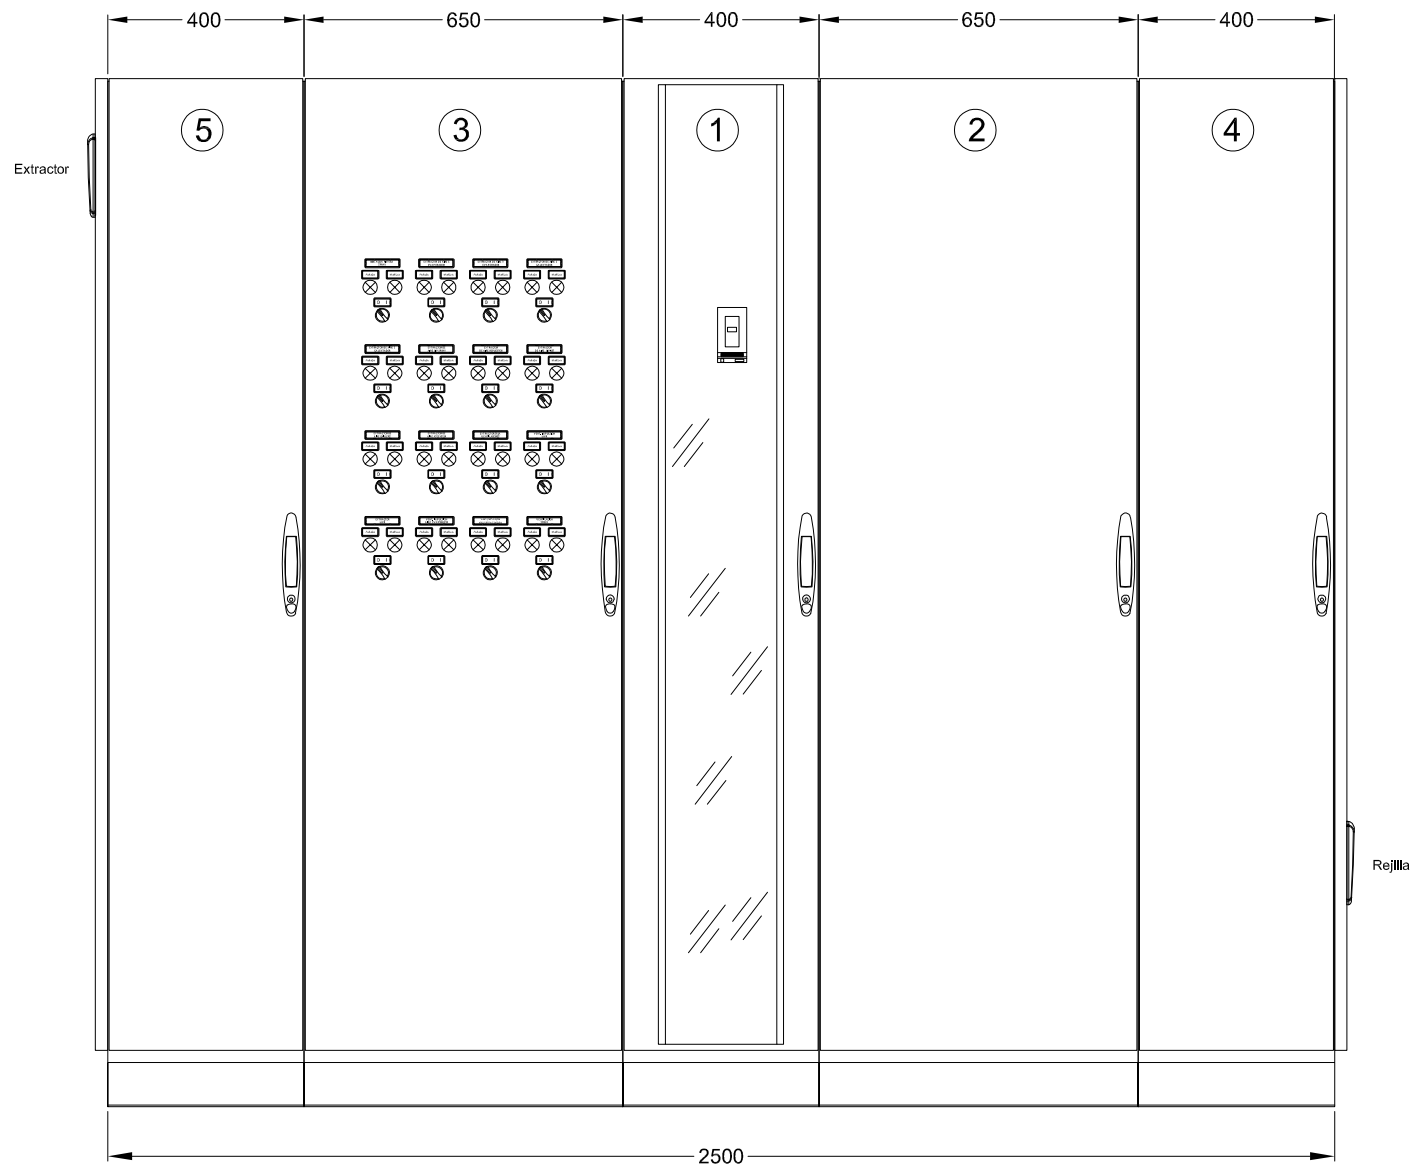

Schneider Electric PrismaSet P - IP30
 1 - Módulo 400x600x2000
 2 - Módulo 650x600x2000
 3 - Módulo 650x600x2000
 4 - Módulo 400x600x2000
 5 - Módulo 400x600x200

0	EDICION ORIGINAL	—	—	03/03/24
REV	MODIFICACION	DIB	REV	FECHA




PUERTAS

TABLERO FEM
PERMEADO



ESC	S / E
HOJA	70
SIGUE	71

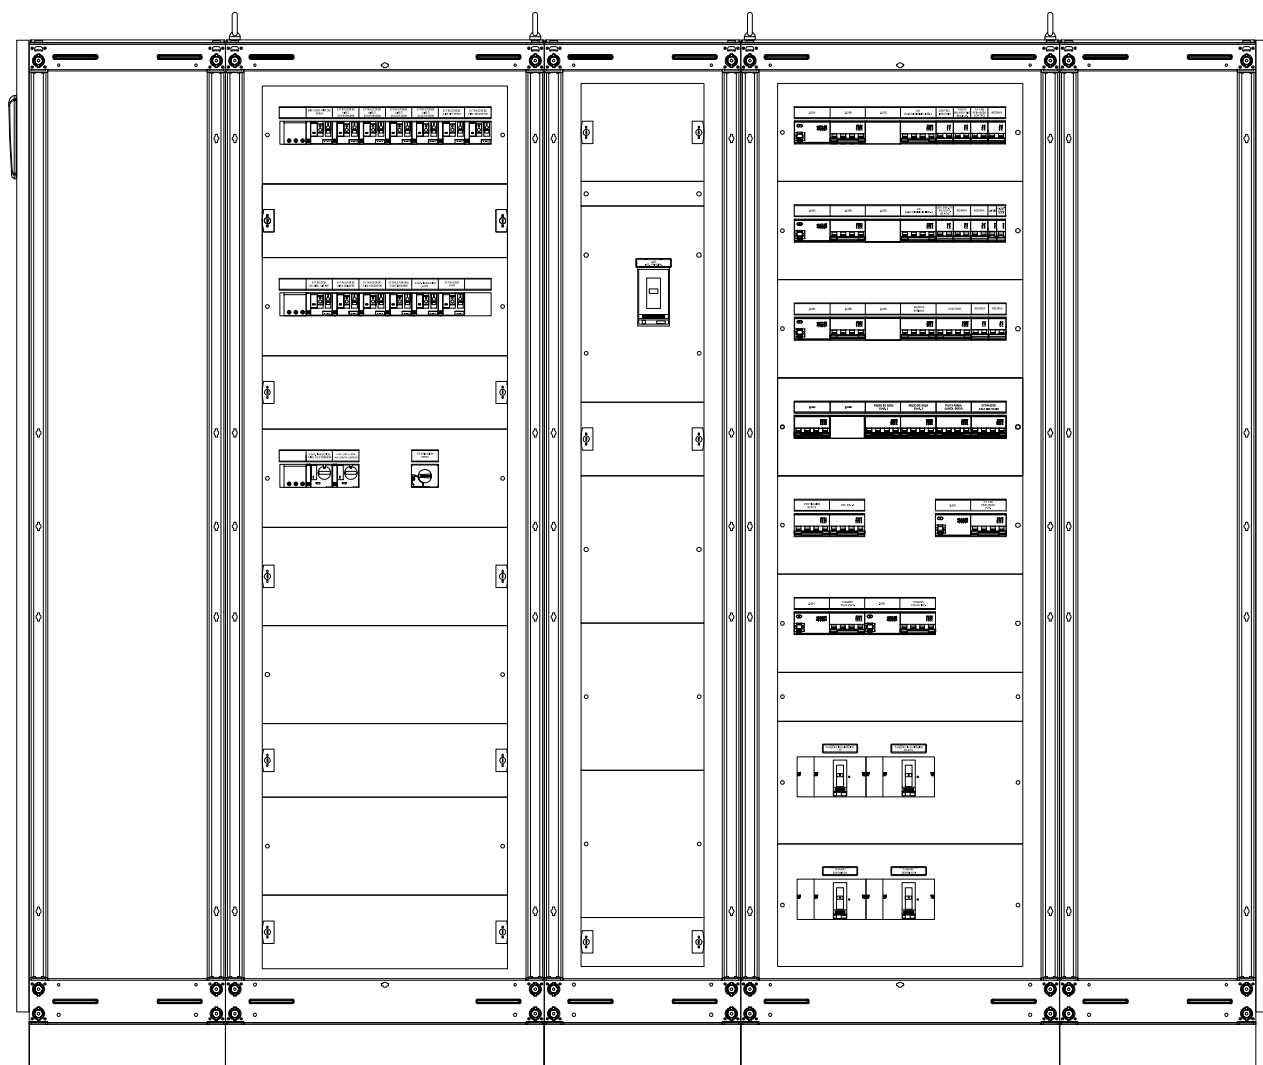

0	EDICION ORIGINAL	—	—	03/03/24
REV	MODIFICACION	DIB	REV	FECHA



CONTRAPUERTAS

TABLERO FEM
PERMEADO

JPI 
SERVICIOS DE INGENIERIA

ESC	S / E
HOJA	71
SIGUE	72



TABLERO FEM
PERMEADO

ESC	S / E
HOJA	72
SIGUE	73

