



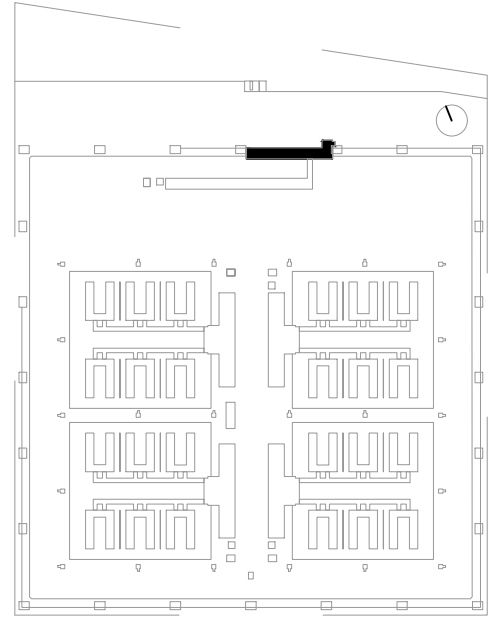


Tablero Seccional
Sector: - Control de Ingreso

ESQUEMA UNIFILAR
"TABLERO INGRESO 1 P.B."
desde T.G.B.T.

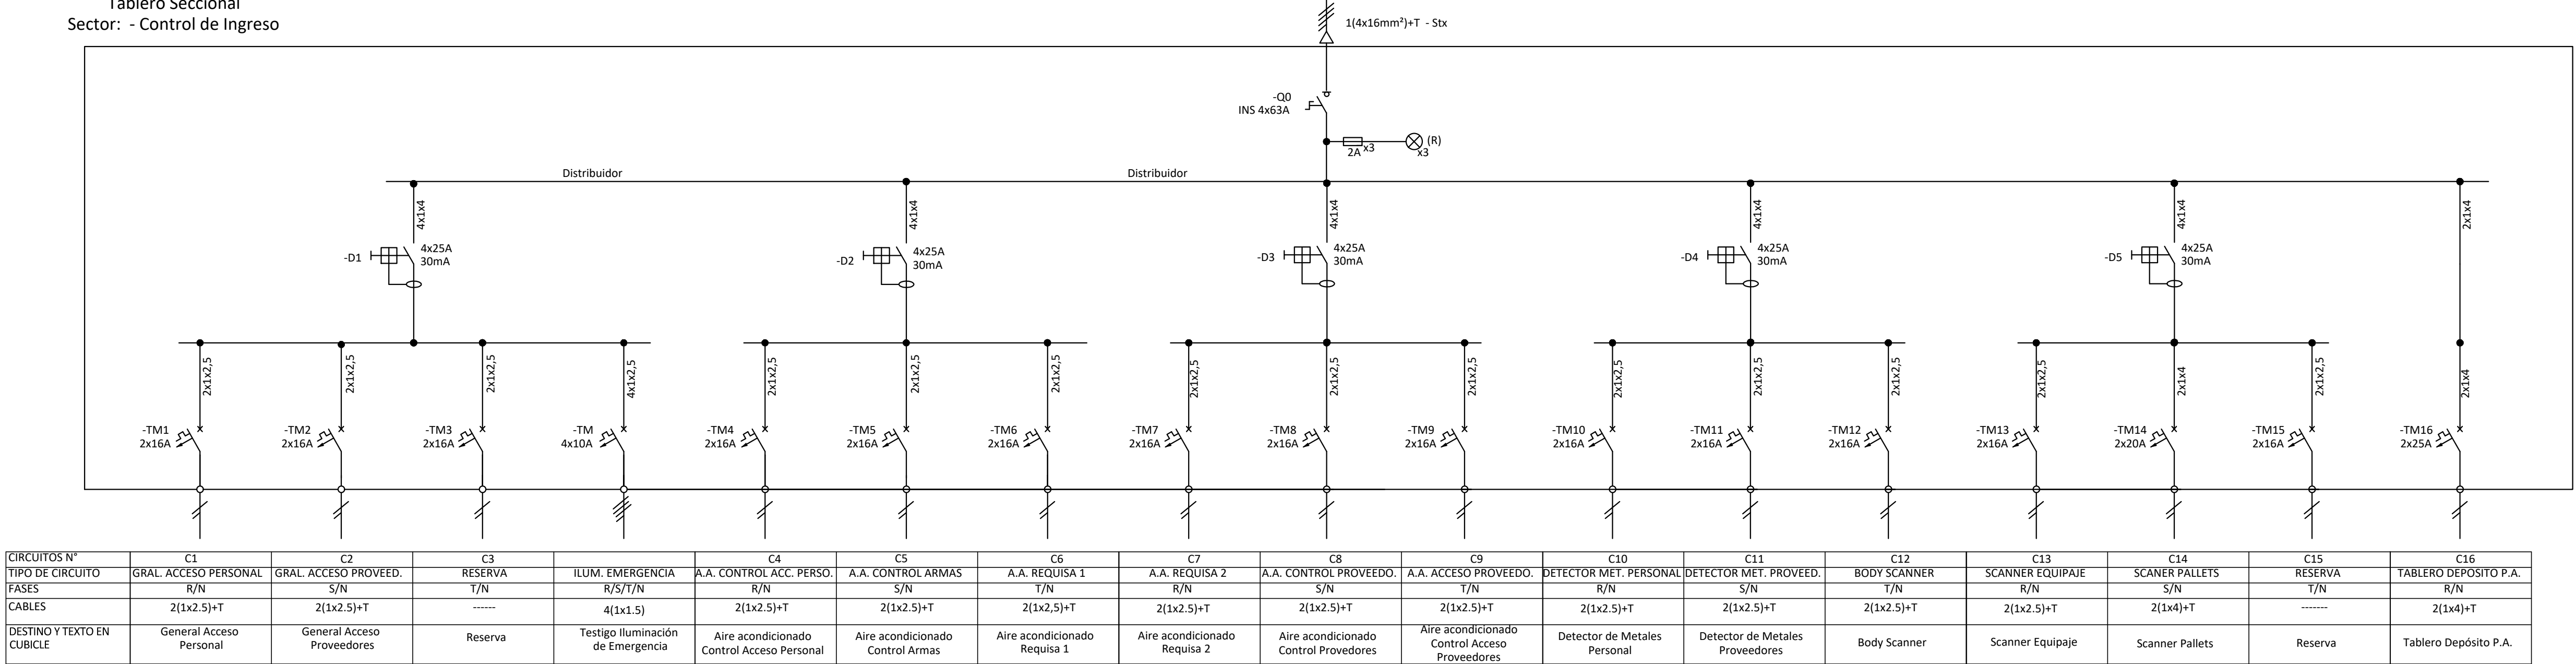

Tablero Seccional
Sector: - Control de Ingreso

ESQUEMA UNIFILAR
"TABLERO INGRESO 2 P.B."
desde T.G.B.T.

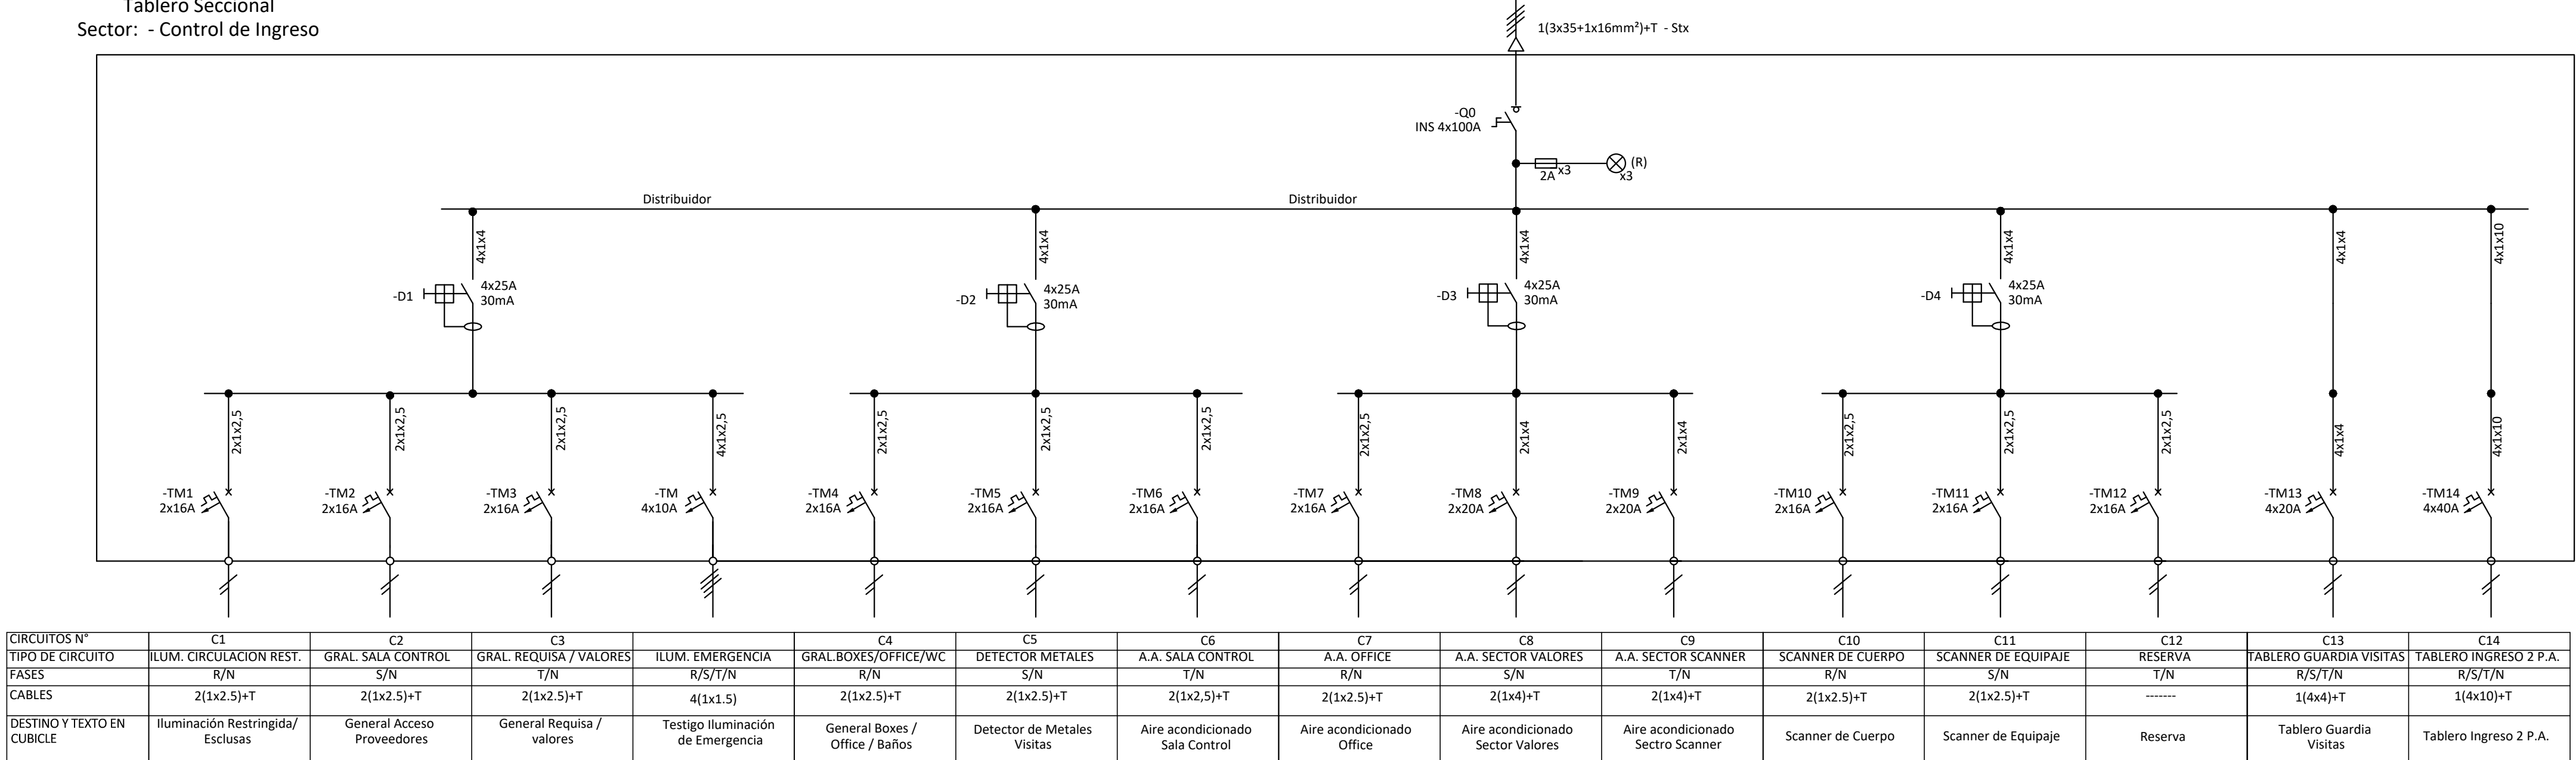

REFERENCIAS

	INTERRUPTOR SECCIONAL INS MANDO ROTATIVO -		INTERRUPTOR DIFERENCIAL 30MMA -		INDICADOR LUMINOSO PRESENCIA DE FASE A LED 220V - D=22 MM		LLAVE SELECTORA DE TRES PUNTOS
	INTERRUPTOR TECNOMAGNETICO C60N -		SECCIONADOR FUSIBLE 20A - CON FUSIBLE 2A -		LLAVE CONMUTADORA		FOTOCONTROL 10A

NOTA:
TODAS LAS MEDIDAS DEBERAN SER VERIFICADAS EN OBRA.

UNIDAD EJECUTORA DE INFRAESTRUCTURA

SUB SECRETARIA TECNICA

ARQ. FRANCISCO QUIJANO

DIRECCION PROVINCIAL DE OBRAS

ING. FEDERICO ZEGNA RATA

DIRECCION PROVINCIAL DE PROYECTOS

ARQ. JORGE GIUNTA

SUBDIRECCION GENERAL TECNICA

MG. ARQ. M.V. LANZARO

OBRA:

UNIDAD PENITENCIARIA N° 8 - CONSTRUCCION DE DOBLE MURO, EDIFICIO CONTROL DE INGRESO, GOBIERNO GENERAL Y EDIFICIOS COMPLEMENTARIOS

EDIFICIO:

CONTROL DE INGRESO

PLANO:

INSTALACION ELECTRICA

ESCALA:

5/E

REVISION:

00

OBSERVACIONES:

FECHA:

21/04/2025