



Tablero Seccional
Sector: - Control de Ingreso

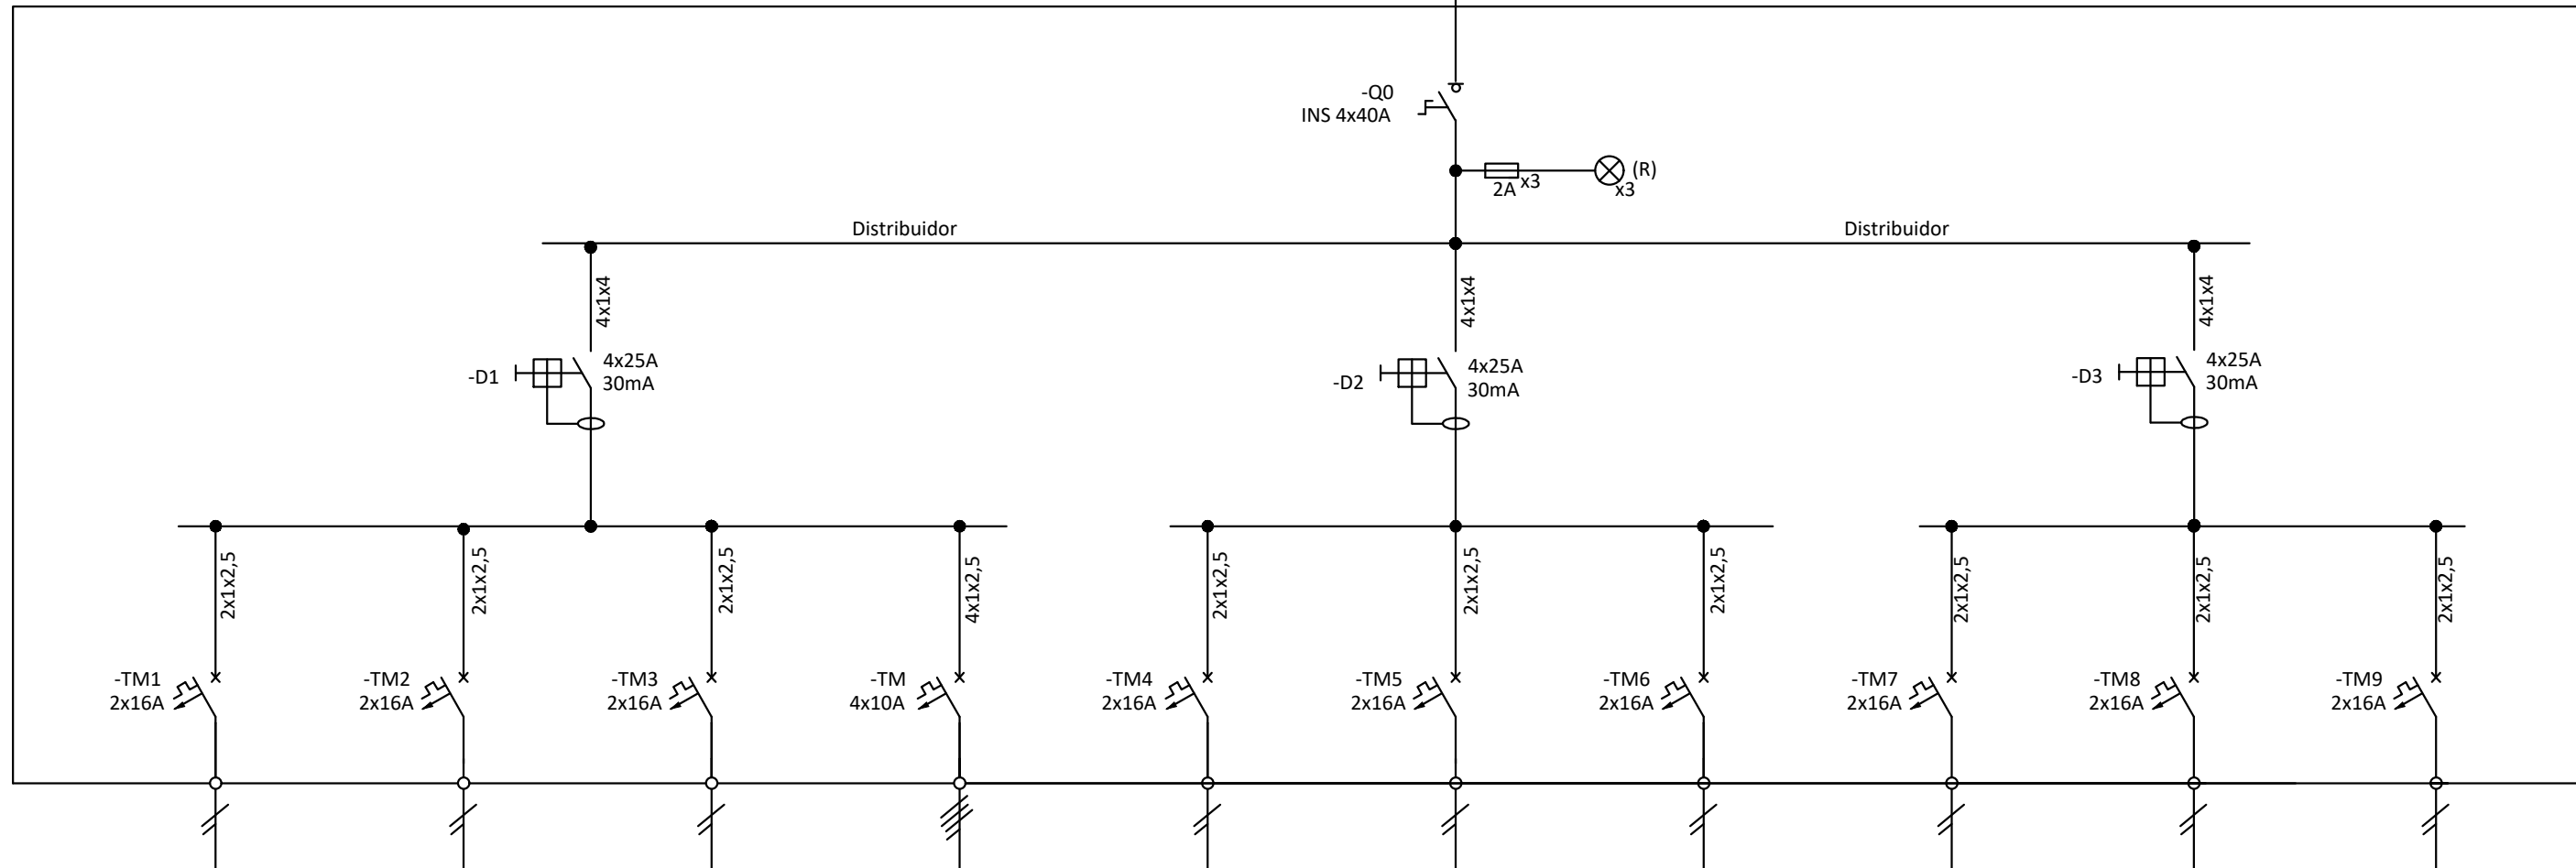


CIRCUITOS N°	C1	C2	C3		C4	C5	C6	C7	C8	C9
TIPO DE CIRCUITO	ILUM. ESPERA VISITAS	ILUM. ACCESO VISITAS	ILUM. EGRESO VISITAS	ILUM. EMERGENCIA	GRAL GUARDIA	GRAL BAÑOS	GRAL VALORES	A.A. GUARDIA	RESERVA	RESERVA
FASES	R/N	S/N	T/N	R/S/T/N	R/N	S/N	T/N	R/N	S/N	T/N
CABLES	2(1x2.5)+T	2(1x2.5)+T	2(1x2.5)+T	4(1x1.5)	2(1x2.5)+T	2(1x2.5)+T	2(1x2.5)+T	2(1x2.5)+T	-----	-----
DESTINO Y TEXTO EN CUBICLE	Iluminación Espera Visitas	Iluminación Acceso Visitas	Iluminación Egreso Visitas	Testigo Iluminación de Emergencia	General Guardia	General Baños	General Valores	Aire acondicionado Office	Reserva	Reserva

Tablero Seccional
Sector: - Control de Ingreso

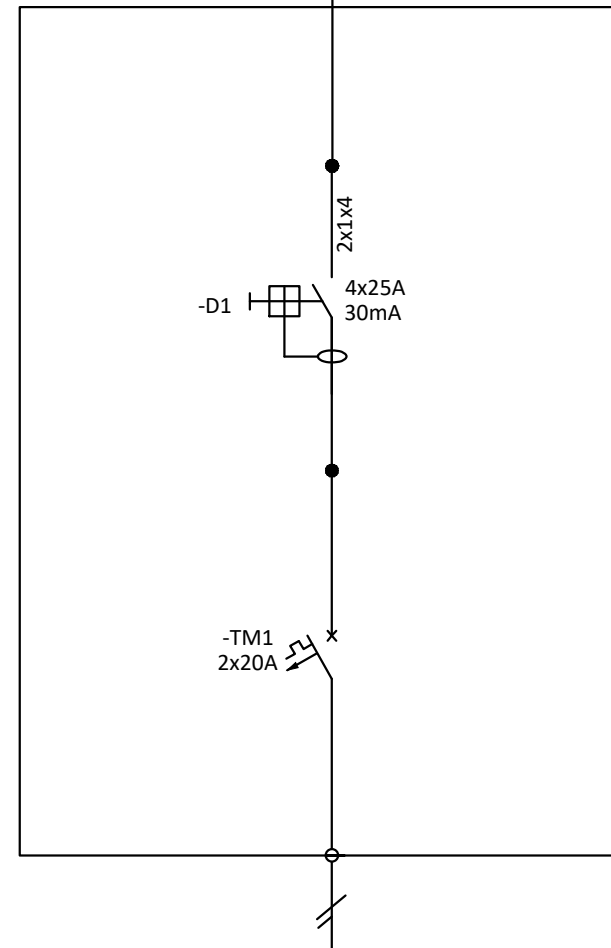

CIRCUITOS N°	C1
TIPO DE CIRCUITO	TABLERO DEPOSITO P.A.
FASES	R/N
CABLES	2(1x4)+T
DESTINO Y TEXTO EN CUBICLE	General Depósito


Tablero Seccional
Sector: - Control de Ingreso

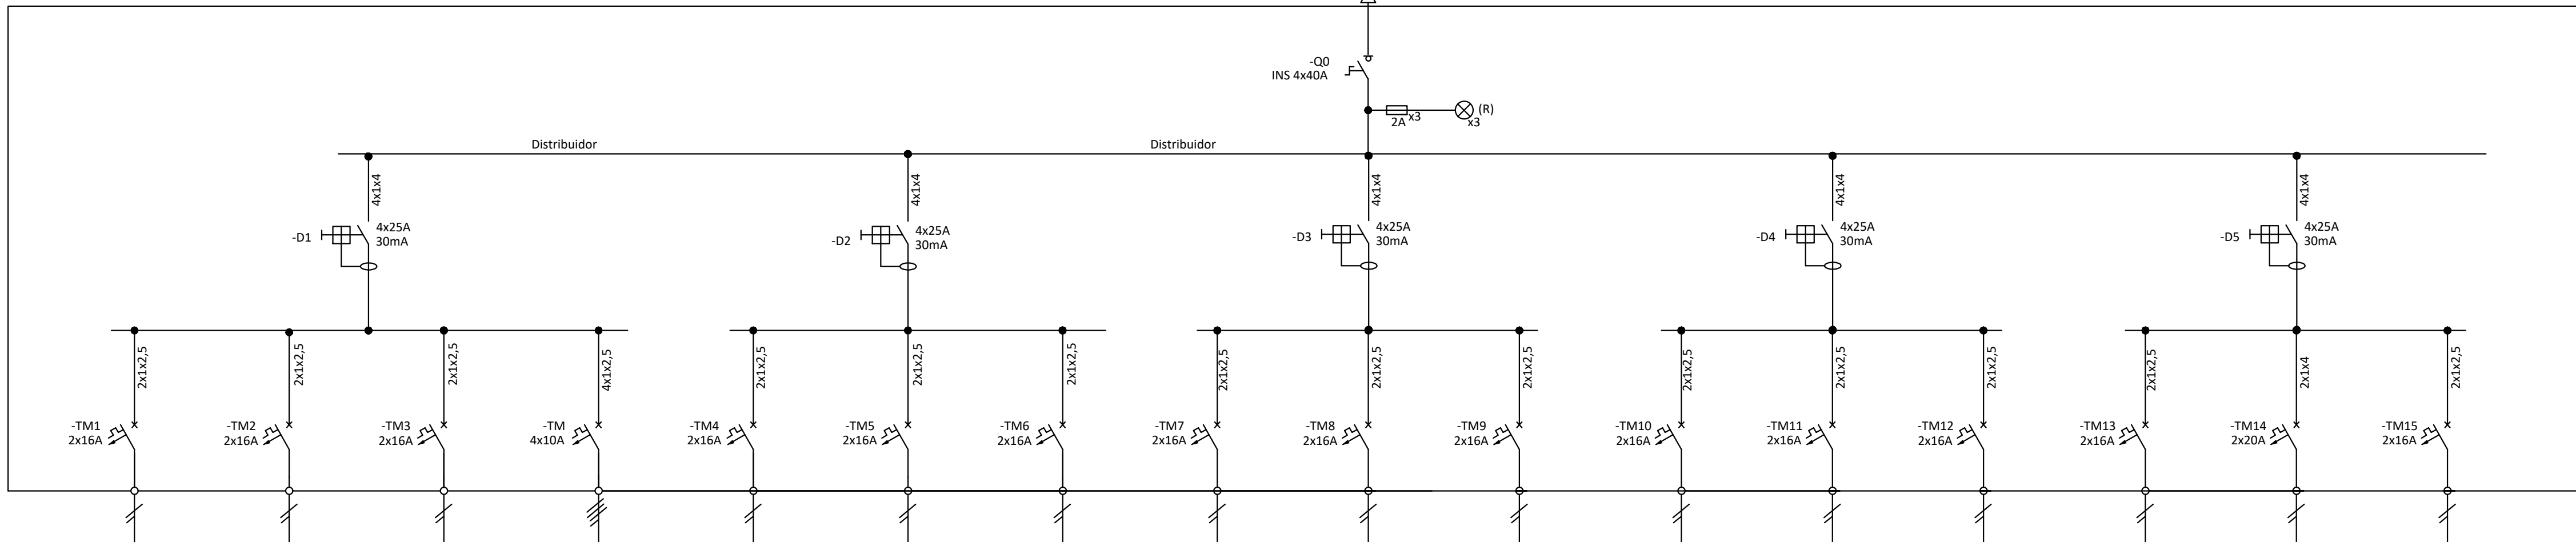

CIRCUITOS N°	C1	C2	C3		C4	C5	C6	C7	C8	C9	C10	C11	C12	C13	C14	C15
TIPO DE CIRCUITO	GRAL. ESTAR/CIRCULACION	GRAL. COCINA/ BAÑO	GRAL. DORMITORIO 1/2/3	ILUM. EMERGENCIA	GRAL. DORMITORIO 4/5/6	GRAL. DORMITORIO 7/8/9	GRAL. DORMI. 10/11/12	A.A. DORMITORIO 1/2	A.A. DORMITORIO 3/4	A.A. DORMITORIO 5/6	A.A. DORMITORIO 7/8	A.A. DORMITORIO 9/10	A.A. DORMITORIO 11/12	A.A. ESTAR / COMEDOR	RESERVA	RESERVA
FASES	R/N	S/N	T/N	R/S/T/N	R/N	S/N	T/N	R/N	S/N	T/N	R/N	S/N	T/N	R/N	S/N	T/N
CABLES	2(1x2.5)+T	2(1x2.5)+T	2(1x2.5)+T	4(1x1.5)	2(1x2.5)+T	2(1x2.5)+T	2(1x2.5)+T	2(1x2.5)+T	2(1x2.5)+T	2(1x2.5)+T	2(1x2.5)+T	2(1x2.5)+T	2(1x2.5)+T	2(1x2.5)+T	-----	-----
DESTINO Y TEXTO EN CUBICLE	General Escalera / Estar / Circulación / Depósito	General Cocina / Baño	General Dormitorio 1 / 2 / 3	Testigo Iluminación de Emergencia	General Dormitorio 4 / 5 / 6	General Dormitorio 7 / 8 / 9	General Dormitorio 10 / 11 / 12	Aire acondicionado Dormitorio 1 / 2	Aire acondicionado Dormitorio 3 / 4	Aire acondicionado Dormitorio 5 / 6	Aire acondicionado Dormitorio 7 / 8	Aire acondicionado Dormitorio 9 / 10	Aire acondicionado Dormitorio 11 / 12	Aire acondicionado Estar / Comedor	Reserva	Reserva

REFERENCIAS

	INTERRUPTOR SECCIONAL INS MANDO ROTATIVO -		INTERRUPTOR DIFERENCIAL 30MMA -		INDICADOR LUMINOSO PRESENCIA DE FASE A LED 220V - D=22 MM		LLAVE SELECTORA DE TRES PUNTOS
	INTERRUPTOR TECNOMAGNETICO C60N -		SECCIONADOR FUSIBLE 20A - CON FUSIBLE 2A -		LLAVE CONMUTADORA		FOTOCONTROL 10A

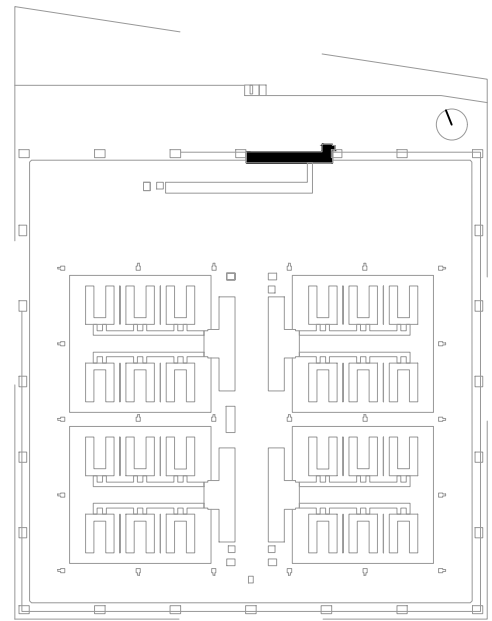

NOTA:
TODAS LAS MEDIDAS DEBERAN SER VERIFICADAS EN OBRA.



UNIDAD EJECUTORA
DE INFRAESTRUCTURA

SUB SECRETARIA TECNICA
ARQ. FRANCISCO QUIJANO

DIRECCION PROVINCIAL DE OBRAS
ING. FEDERICO ZEGNA RATA

DIRECCION PROVINCIAL DE PROYECTOS
ARQ. JORGE GIUNTA

SUBDIRECCION GENERAL TECNICA
MG. ARQ. M.V. LANZARO

OBRA:
UNIDAD PENITENCIARIA N° 8 -
CONSTRUCCION DE DOBLE
MURO, EDIFICIO CONTROL DE
INGRESO, GOBIERNO GENERAL Y
EDIFICIOS COMPLEMENTARIOS

EDIFICIO:
CONTROL DE INGRESO

PLANO:
INSTALACION ELECTRICA

ESCALA:
5/E

REVISION:
00

OBSERVACIONES:
-

FECHA:
21/04/2025

03DM_PE CI-E 04