



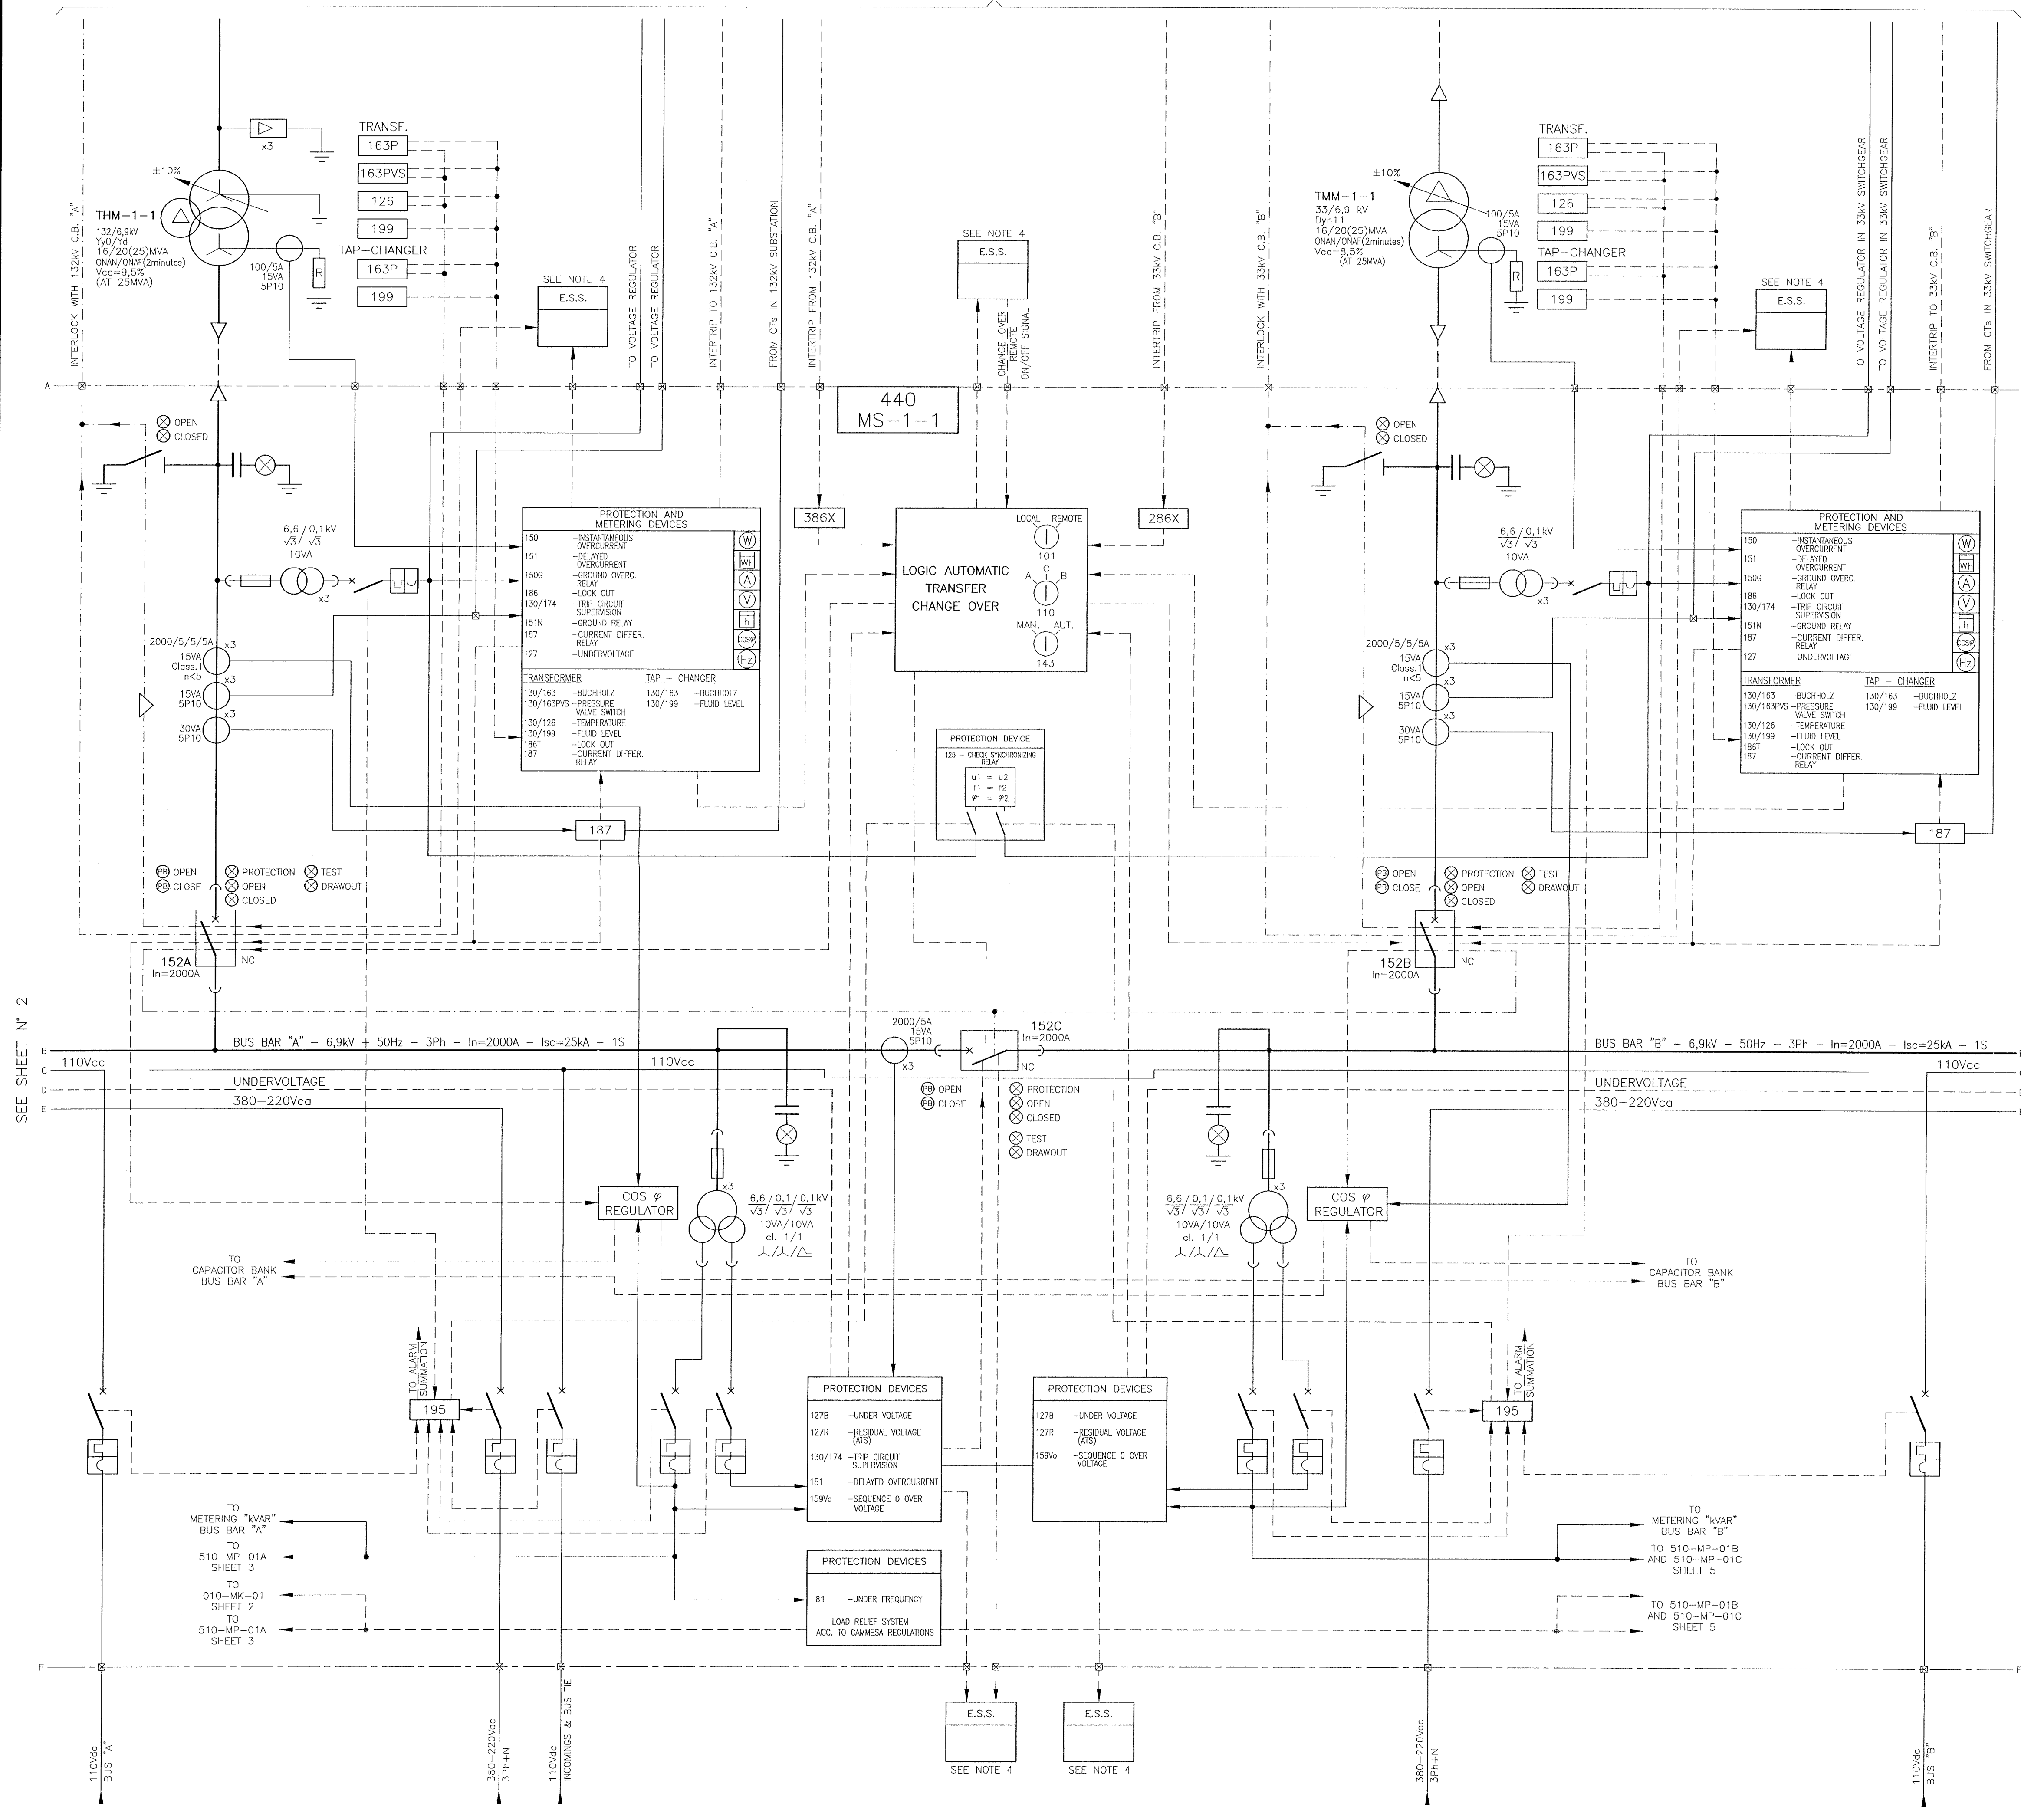

EACH PANEL SHALL BE EQUIPPED WITH ANTICONDENSATION HEATER

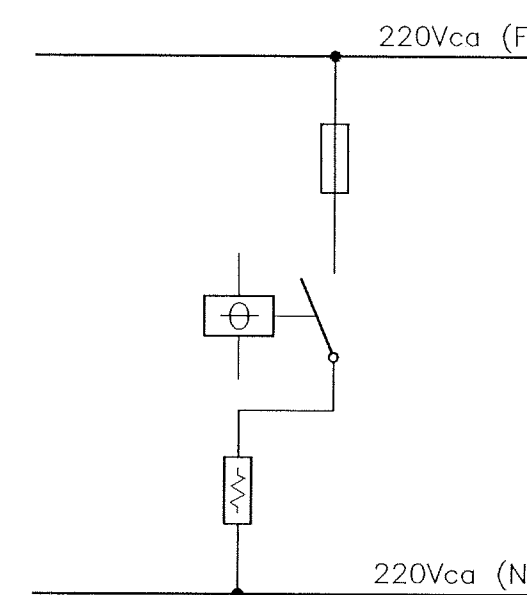

## NOTE:

- 1- FUSE AND CONTACTOR RATINGS HAVE BEEN DETERMINED BY MEDIUM VOLTAGE SWITCHGEAR SUPPLIER.
- 2- AUTOTRANSFORMER FOR MOTOR STARTING HAS BEEN PROVIDED BY MEDIUM VOLTAGE SWITCHGEAR SUPPLIER.
- 3- CAPACITOR BANKS FOR POWER FACTOR IMPROVEMENT HAVE BEEN PROVIDED BY MEDIUM VOLTAGE SWITCHGEAR SUPPLIER.
- 4- E.S.S., D.C.S. AND E.S.D. COMPLETE LIST FOR ALARMS AND STATUS CHANGES SIGNALS SEE DWG. D-001-1381-010.
- 5- METERING TRANSFORMERS' PERFORMANCE HAS BEEN CHECKED WITH THE FEATURES OF THE PROTECTION AND METERING DEVICES.

## REFERENCES:

D.C.S. = DISTRIBUTED CONTROL SYSTEM.  
E.S.D. = EMERGENCY SHUT DOWN.  
E.S.S. = ELECTRICAL SUPERVISION SYSTEM.

## DOCUMENT REVISIONS

| Rev. | 0 | 1 | 2 | 3 | 4 |
|------|---|---|---|---|---|
| 001  | X | X | X | X | X |
| 002  | X | X | X | X | X |
| 003  | X | X | X | X | X |
| 004  |   |   | X | X | X |
| 005  |   |   | X | X | X |

| 4   | 10-APR-01                                       | AS BUILT                                                  | DAC     |         |       |       |
|---|-------------------------------------------------|-----------------------------------------------------------|---------|---------|-------|-------|
| 3   | 19-JAN-99                                       | ISSUED FOR CONSTRUCTION                                   | MAW/DP  | JOM/MON | DIT   | OJIMA |
| 2   | 27-NOV-98                                       | ISSUED FOR CONSTRUCTION                                   | MAW/EDM | JOM/MON | DIT   | OJIMA |
| 1   | 29-SEP-98                                       | ISSUED FOR CONSTRUCTION (GENERAL REVISION)                | MAW/EDM | JOM/MON | DIT   | OJIMA |
| 0   | 20-JUL-98                                       | ISSUED FOR REVIEW                                         | MAW/EDM | JOM     |       |       |
| REV   | DATE                                            | DESCRIPTION                                               | DRAWN   | CHECK   | APPR. | ISSUE |
| V-2181-002-A-121   | 2                                               | LOMA LA LATA DETAILED ONE LINE DIAGRAM SWITCHBOARD 6,6 kV |         |         |       |       |
| D-000-1381-001   | 3                                               | ELECTRICAL SYMBOLS                                        |         |         |       |       |
| S-000-1381-002/AM   | 3                                               | P.S. MEDIUM VOLTAGE SWITCHBOARDS LOMA LA LATA             |         |         |       |       |
| D-001-1381-001   | 2                                               | GENERAL PROTECTION AND METERING DIAGRAM                   |         |         |       |       |
| D-001-1380-010   | 3                                               | GENERAL ONE LINE DIAGRAM                                  |         |         |       |       |
| DOCUMENT N°   | REV                                             | TITLE                                                     |         |         |       |       |
| MEGA PROJECT Argentina   | Owner:                                          | COMPANIA MEGA S.A.                                        |         |         |       |       |
| AREA: 001   | Contract N°:                                    |                                                           |         |         |       |       |
| TITLE:   | LOMA LA LATA<br>DETAILED ONE LINE DIAGRAM 6,6kV |                                                           |         |         |       |       |
| Contractor Doc.N°   | MEGA Doc.N°                                     |                                                           |         |         |       |       |
| D-001-1381-004   |                                                 |                                                           |         |         |       |       |
| This document is the property of COMPANIA MEGA S.A. who will safeguard their rights according to the civil and penal provisions of the law. |                                                 |                                                           |         |         |       |       |





|      |           |                                            |  |         | DAC     |       |  |           |  |
|------|-----------|--------------------------------------------|--|---------|---------|-------|--|-----------|--|
| 4    | 10-APR-01 | AS BUILT                                   |  |         |         |       |  |           |  |
| 3    | 19-JAN-99 | ISSUED FOR CONSTRUCTION                    |  | MAW/DP  | JOM/MON | DIT   |  | OJIMA     |  |
| 2    | 27-NOV-98 | ISSUED FOR CONSTRUCTION                    |  | MAW/EDM | JOM/MON | DIT   |  | OJIMA     |  |
| 1    | 29-SEP-98 | ISSUED FOR CONSTRUCTION (GENERAL REVISION) |  | MAW/EDM | JOM/MON | DIT   |  | OJIMA     |  |
| 0    | 20-JUL-98 | ISSUED FOR REVIEW                          |  | MAW/EDM | JOM     |       |  |           |  |
| REV. | DATE      | DESCRIPTION                                |  | DRAWN   | CHECK   | APPR. |  | ISSUED BY |  |

|                                                                                       |  |   |  |
|---------------------------------------------------------------------------------------|--|---|--|
| MEGA PROJECT<br>Argentina                                                             |  | Owner:<br><br>COMPAÑIA MEGA S.A.                                                              |  |
|  |  |   SAIPEM |  |
| AREA: 001<br>UNIT:                                                                    |  | Contract N°:   |  |
| TITLE: LOMA LA LATA<br>DETAILED ONE LINE DIAGRAM 6,6kv                                |  | REV.                                                                                          |  |
| 250A                                                                                  |  | Sheet<br>2 of   |  |
| Contractor Doc.N°<br>D-001-1381-004                                                   |  | MEGA Doc.N°<br>Scale<br>NONE   |  |
| This document is the property of COMPAÑIA MEGA S.A. who will safeguard their          |  |   |  |







|     |           |                                            |                                                                                           |         |       |                                                                                       |
|-----|-----------|--------------------------------------------|-------------------------------------------------------------------------------------------|---------|-------|---------------------------------------------------------------------------------------|
|     |           |                                            |                                                                                           |         |       |                                                                                       |
| 4   | 10-APR-01 | AS BUILT                                   | DAC  |         |       |  |
| 3   | 19-JAN-99 | ISSUED FOR CONSTRUCTION                    | MAW/DP                                                                                    | JOM/MON | DIT   | OJIMA                                                                                 |
| 2   | 27-NOV-98 | ISSUED FOR CONSTRUCTION                    | MAW/EDM                                                                                   | JOM/MON | DIT   | OJIMA                                                                                 |
| 1   | 23-SEP-98 | ISSUED FOR CONSTRUCTION (GENERAL REVISION) | MAW/EDM                                                                                   | JOM/MON | DIT   | OJIMA                                                                                 |
| 0   | 20-JUL-98 | ISSUED FOR REVIEW                          | MAW/EDM                                                                                   | JOM     |       |                                                                                       |
| REV | DATE      | DESCRIPTION                                | DRAWN                                                                                     | CHECK   | APPR. | ISSUE                                                                                 |

|   |  |                                                                                              |  |
|---|--|----------------------------------------------------------------------------------------------|--|
| MEGA PROJECT<br>Argentina   |  | Owner:  |  |
| COMPAÑIA MEGA S.A.   |  |                                                                                              |  |
|                                                        |  |         |  |
|   |  |  SAIPEM |  |
| AREA: 001<br>UNIT:   |  | Contract N°:                                                                                 |  |
| TITLE: LOMA LA LATA<br>DETAILED ONE LINE DIAGRAM 6,6kV                                                                                      |  |         |  |
|   |  | Sheet<br>3 of 5                                                                              |  |
| Contractor Doc.N°<br>D-001-1381-004   |  | MEGA Doc.N°<br>                                                                              |  |
|   |  | Scale<br>NONE                                                                                |  |
| This document is the property of COMPAÑIA MEGA S.A. who will safeguard their rights according to the civil and penal provisions of the law. |  |                                                                                              |  |



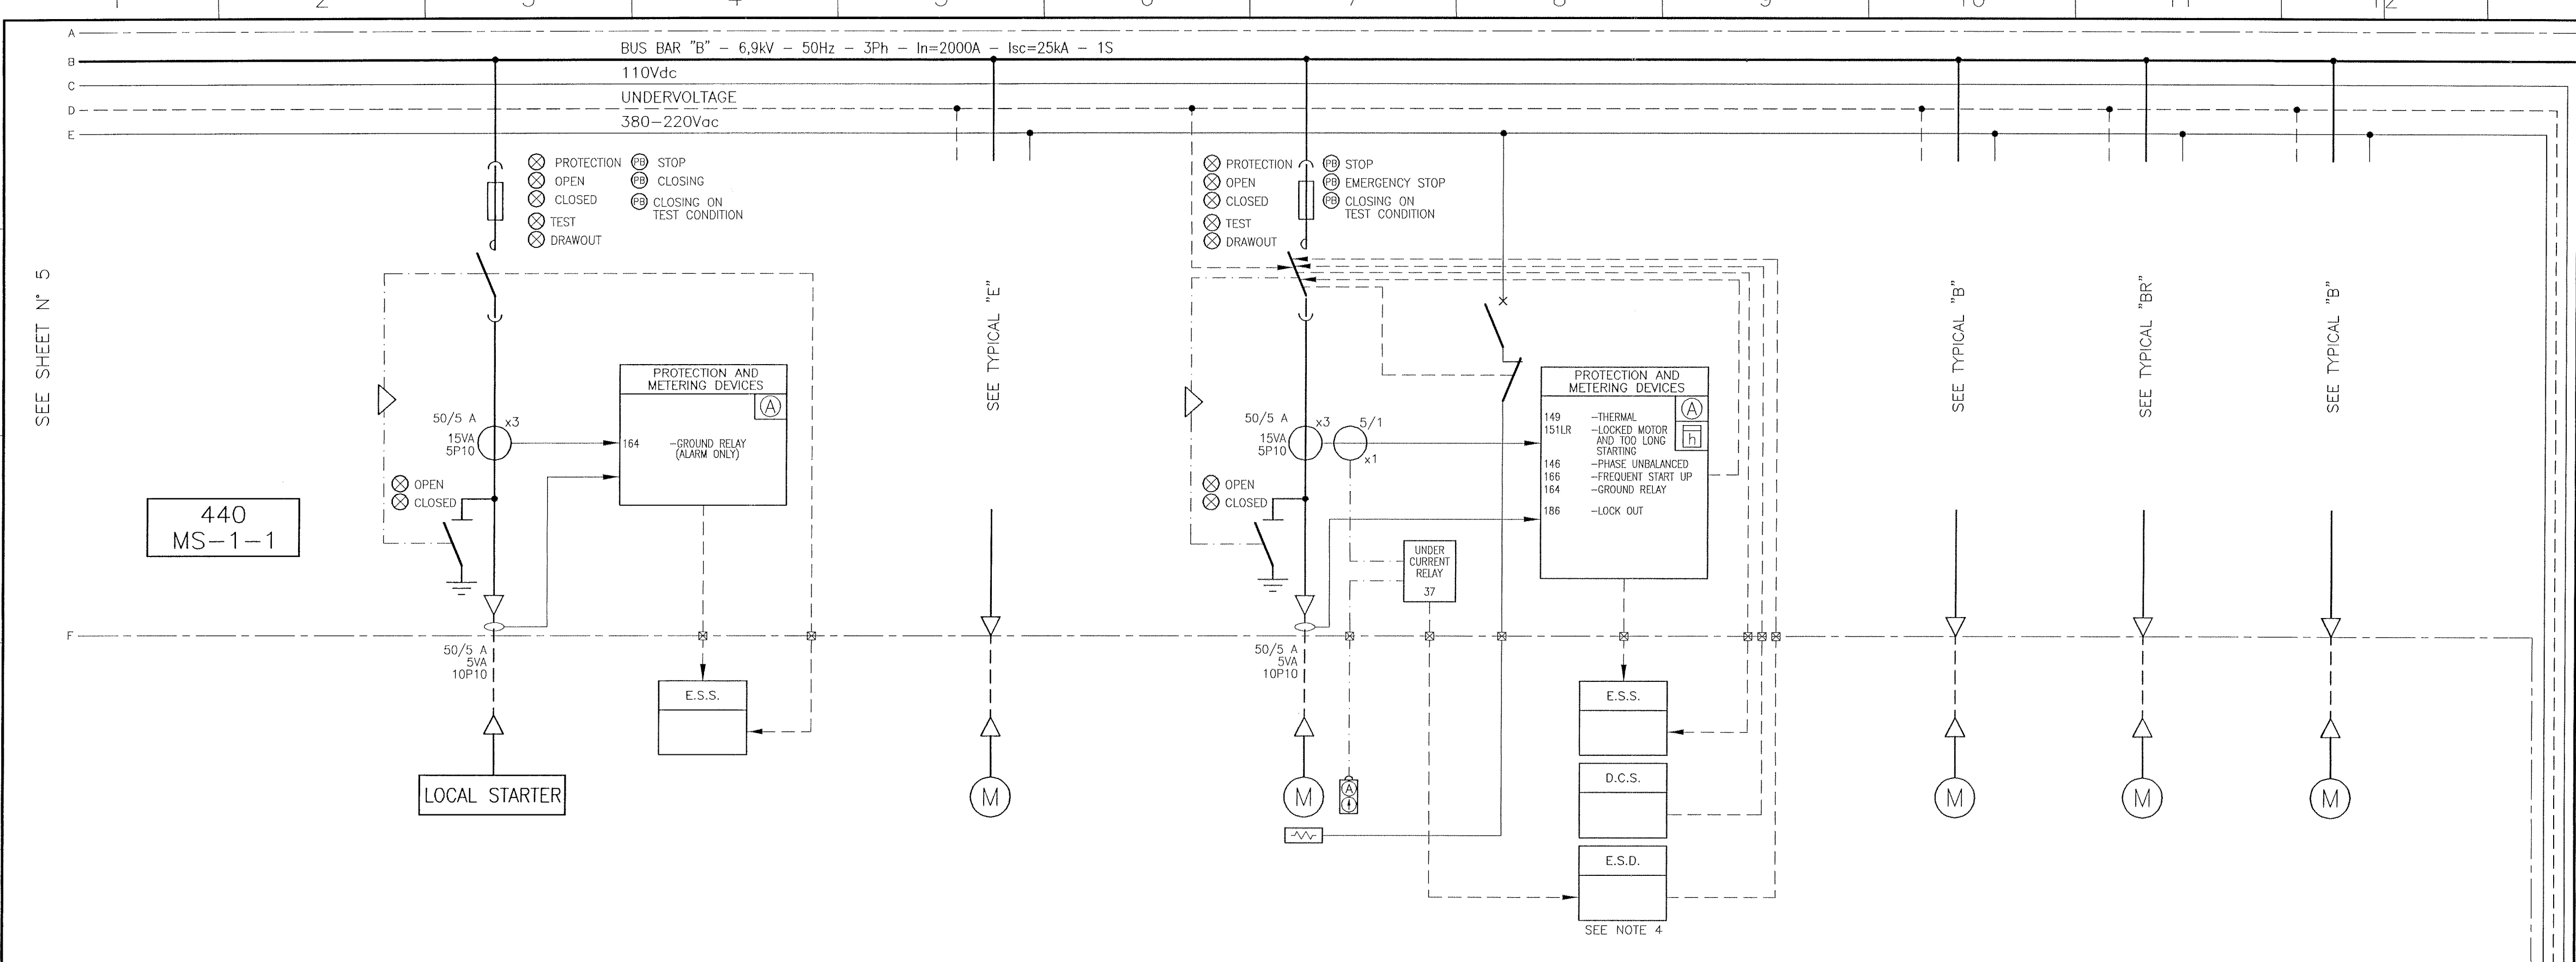

| NAME            | LOCAL PANEL FIRE WATER PUMP<br>TYPICAL "F" | NGL TRANSFER PUMP<br>TYPICAL "E" | NGL TRANSFER PUMP<br>TYPICAL "E" | INST. AND SERVICE<br>AIR COMPRESSOR | NGL<br>RERUN PUMP | MOTOR            |
|-----------------|--------------------------------------------|----------------------------------|----------------------------------|-------------------------------------|-------------------|------------------|
| TAG             | LP-400-P-02                                | 150-MP-02B                       | 140-MP-02B                       | 340-MK-01B                          | 300-MP-02B        | SPARE STARTER    |
| CIRCUIT BREAKER |                                            |                                  |                                  |                                     |                   |                  |
| FUSE            | 100A                                       | 63A                              | 100A                             | 100A                                | 63A               | 100A             |
| C.T. RATIO      | 50/5A                                      | 40/5A                            | 40/5A                            | 50/5A                               | 30/5A             | 50/5A            |
| CONTACTOR       | 400A                                       | 400A                             | 400A                             | 400A                                | 400A              | 400A             |
| CONTROL DIAGRAM | V-2181-002-A-134                           | V-2181-002-A-212                 | V-2181-002-A-212                 | V-2181-002-A-213                    | V-2181-002-A-133  | V-2181-002-A-213 |
| POWER (kW-kVA)  | 410kW                                      | 180kW                            | 180kW                            | 300kW                               | 150kW             | 315kW            |

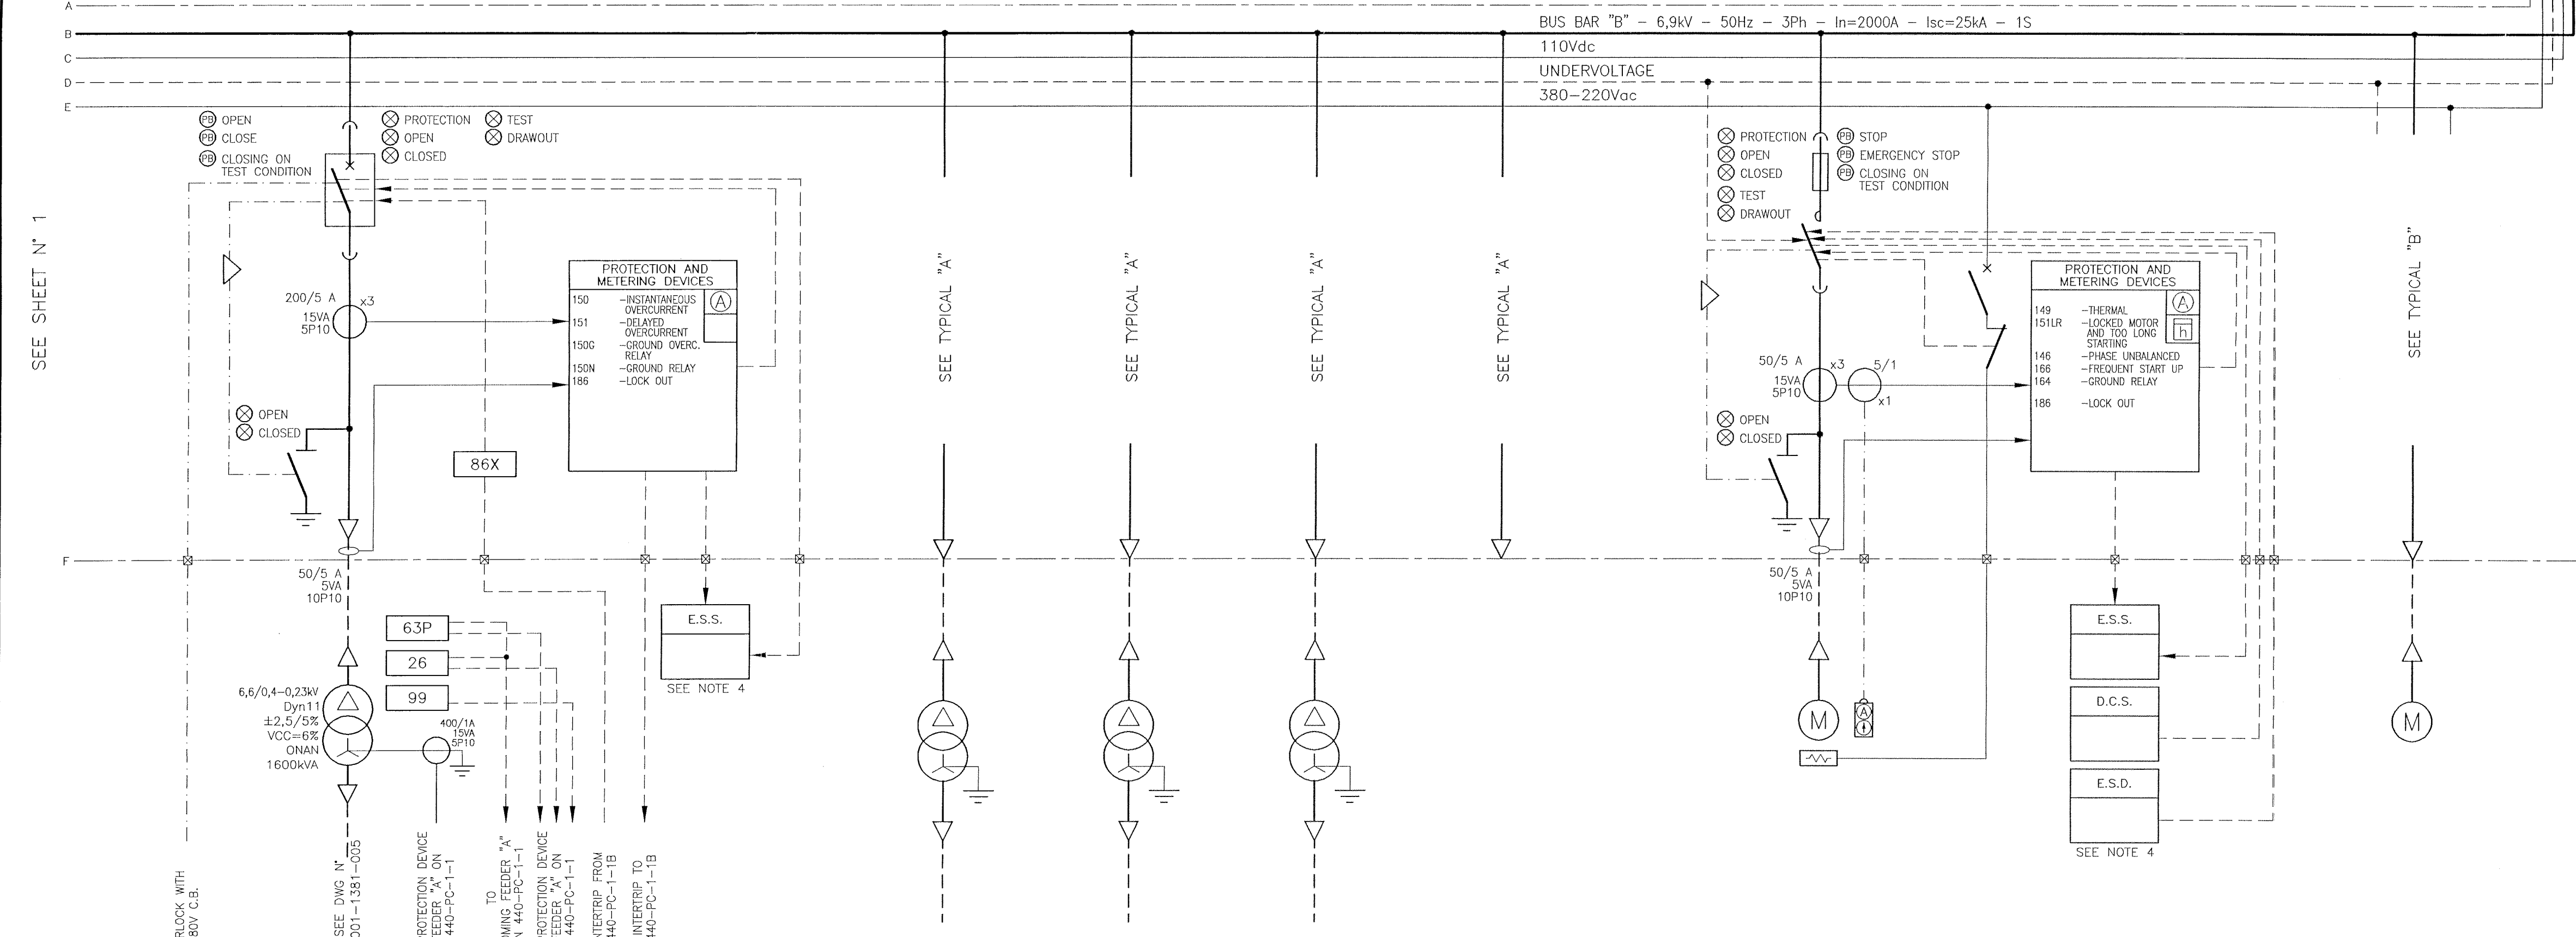

| NAME            | TRANSFORMER<br>(TYPICAL "A") | TRANSFORMER      | TRANSFORMER      | TRANSFORMER      | TRANSFORMER      | REGEN. GAS COMP. "B"<br>(TYPICAL "B") | REGEN. GAS<br>COMPRESSOR "D" |
|-----------------|------------------------------|------------------|------------------|------------------|------------------|---------------------------------------|------------------------------|
| TAG             | 440-TML-1-1B                 | 440-TML-1-2B     | 440-TML-2-1B     | 440-TML-2-2B     | SPARE            | 050-MK-01B                            | 050-MK-01D                   |
| CIRCUIT BREAKER |                              |                  |                  |                  |                  |                                       |                              |
| FUSE            | 1250A                        | 1250A            | 1250A            | 1250A            | 1250A            | 75A                                   | 75A                          |
| C.T. RATIO      | 200/5A                       | 200/5A           | 200/5A           | 200/5A           | 200/5A           | 50/5A                                 | 50/5A                        |
| CONTACTOR       |                              |                  |                  |                  |                  | 400A                                  | 400A                         |
| CONTROL DIAGRAM | V-2181-002-A-139             | V-2181-002-A-139 | V-2181-002-A-139 | V-2181-002-A-139 | V-2181-002-A-139 | V-2181-002-A-213                      | V-2181-002-A-213             |
| POWER (kW-kVA)  | 1600kVA                      | 1600kVA          | 1600kVA          | 1600kVA          | 1600kVA          | 250kW                                 | 250kW                        |

FOR NOTES SEE SHEET 1 OF 5

| REV | DATE      | DESCRIPTION                                | DRAWN   | CHECK   | APPR. | ISSUE |
|-----|-----------|--------------------------------------------|---------|---------|-------|-------|
| 4   | 10-APR-01 | AS BUILT                                   | DAC     |         |       |       |
| 3   | 19-JAN-98 | ISSUED FOR CONSTRUCTION                    | MAW/DP  | JOM/MON | DIT   | OJIMA |
| 2   | 27-NOV-98 | ISSUED FOR CONSTRUCTION                    | MAW/EDM | JOM/MON | DIT   | OJIMA |
| 1   | 29-SEP-98 | ISSUED FOR CONSTRUCTION (GENERAL REVISION) | MAW/EDM | JOM/MON | DIT   | OJIMA |
| 0   | 20-JUL-98 | ISSUED FOR REVIEW                          | MAW/EDM | JOM     |       |       |

| REFERENCE         | DOCUMENT N° | REV | TITLE                                                    |
|-------------------|-------------|-----|----------------------------------------------------------|
| V-2181-002-A-121  | 2           |     | LOMA LA LATA DETAILED ON LINE DIAGRAM SWITCHBOARD 6,6 kV |
| D-000-1381-001    | 3           |     | ELECTRICAL SYMBOLS                                       |
| S-000-1381-002/AM | 3           |     | P.S. MEDIUM VOLTAGE SWITCHBOARDS LOMA LA LATA            |
| D-001-1381-001    | 2           |     | GENERAL PROTECTION AND METERING DIAGRAM                  |
| D-001-1380-010    | 3           |     | GENERAL ONE LINE DIAGRAM                                 |


|                           |                                     |
|---------------------------|-------------------------------------|
| MEGA PROJECT<br>Argentina | Owner:<br><b>COMPAÑIA MEGA S.A.</b> |
|---------------------------|-------------------------------------|

|            |            |               |
|------------|------------|---------------|
| <b>JCC</b> | <b>CPC</b> | <b>SAIPEM</b> |
|------------|------------|---------------|

|                                                           |              |                  |
|-----------------------------------------------------------|--------------|------------------|
| AREA: 001<br>UNIT:                                        | Contract N°: | REV.<br><b>4</b> |
| TITLE:<br>LOMA LA LATA<br>DETAILED ONE LINE DIAGRAM 6,6kV |              |                  |
| Contractor Doc.N°<br><b>D-001-1381-004</b>                | MEGA Doc.N°  | Scale<br>NONE    |

This document is the property of COMPAÑIA MEGA S.A. who will safeguard their rights according to the civil and penal provisions of the law.



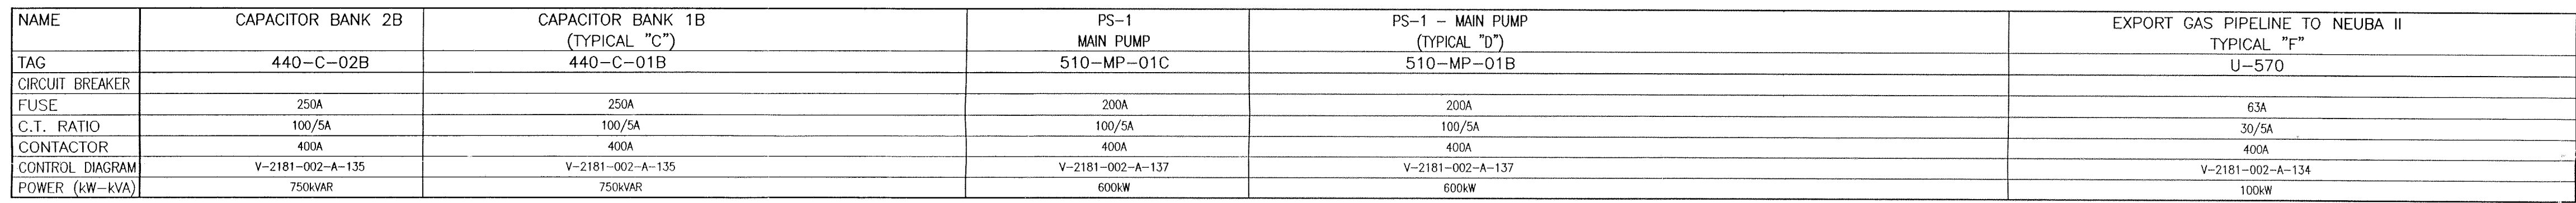

| NAME            | EMPTY SPARE |  |
|-----------------|-------------|--|
| TAG             |             |  |
| CIRCUIT BREAKER |             |  |
| FUSE            |             |  |
| C.T. RATIO      |             |  |
| CONTACTOR       |             |  |
| CONTROL DIAGRAM |             |  |
| POWER (kW-kVA)  |             |  |

|           |                   |     |                                                           |
|-----------|-------------------|-----|-----------------------------------------------------------|
| REFERENCE | V-2181-002-A-121  | 2   | LOMA LA LATA DETAILED ONE LINE DIAGRAM SWITCHBOARD 6,6 kv |
|           | D-000-1381-001    | 3   | ELECTRICAL SYMBOLS                                        |
|           | S-000-1381-002/AM | 3   | P.S. MEDIUM VOLTAGE SWITCHBOARDS LOMA LA LATA             |
|           | D-001-1381-001    | 2   | GENERAL PROTECTION AND METERING DIAGRAM                   |
|           | D-001-1380-010    | 3   | GENERAL ONE LINE DIAGRAM                                  |
|           | DOCUMENT N°       | REV | TITLE                                                     |

JOB No. 0-0888      SIZE 8      CAD File: D-001-1381-004-B-R4-H5.DWG