


ESQUEMA UNIFILAR – TABLERO DE DISTRIBUCIÓN SSAA BT

A	05/02/26	EMISIÓN PARA COTIZACIÓN			E. RODRIGUEZ	E. RODRIGUEZ	CARLOS LONG
REV.	FECHA	DESCRIPCION			DIBUJO	REVISO	APROBO
LISTA DE REVISIONES							
		CLIENTE: SECCO OBRA: --- N° PROY./FAB.: 50000 LUGAR: ROSARIO					
SECTOR: INGENIERÍA		TITULO: TABLERO BT SSAA SUB-TITULO: PORTADA PARTE: ESQUEMA UNIFILAR N° SAP: ---					
Prohibida su reproducción total o parcial sin previa autorización escrita. No pasar sobre el plano. "ANTES DE USAR ESTE PLANO CONSULTE AL DEPARTAMENTO TECNICO POR SU REVISIÓN VIGENTE"		ESC: S/E TOL: N/A		PLANO N°: DES-50000-E-EU-40267		Rev. A	Hoja 01/07

ESQUEMA UNIFILAR – TABLERO DE DISTRIBUCIÓN BT

TABLERO DE DISTRIBUCION SSAA EN BAJA TENSION

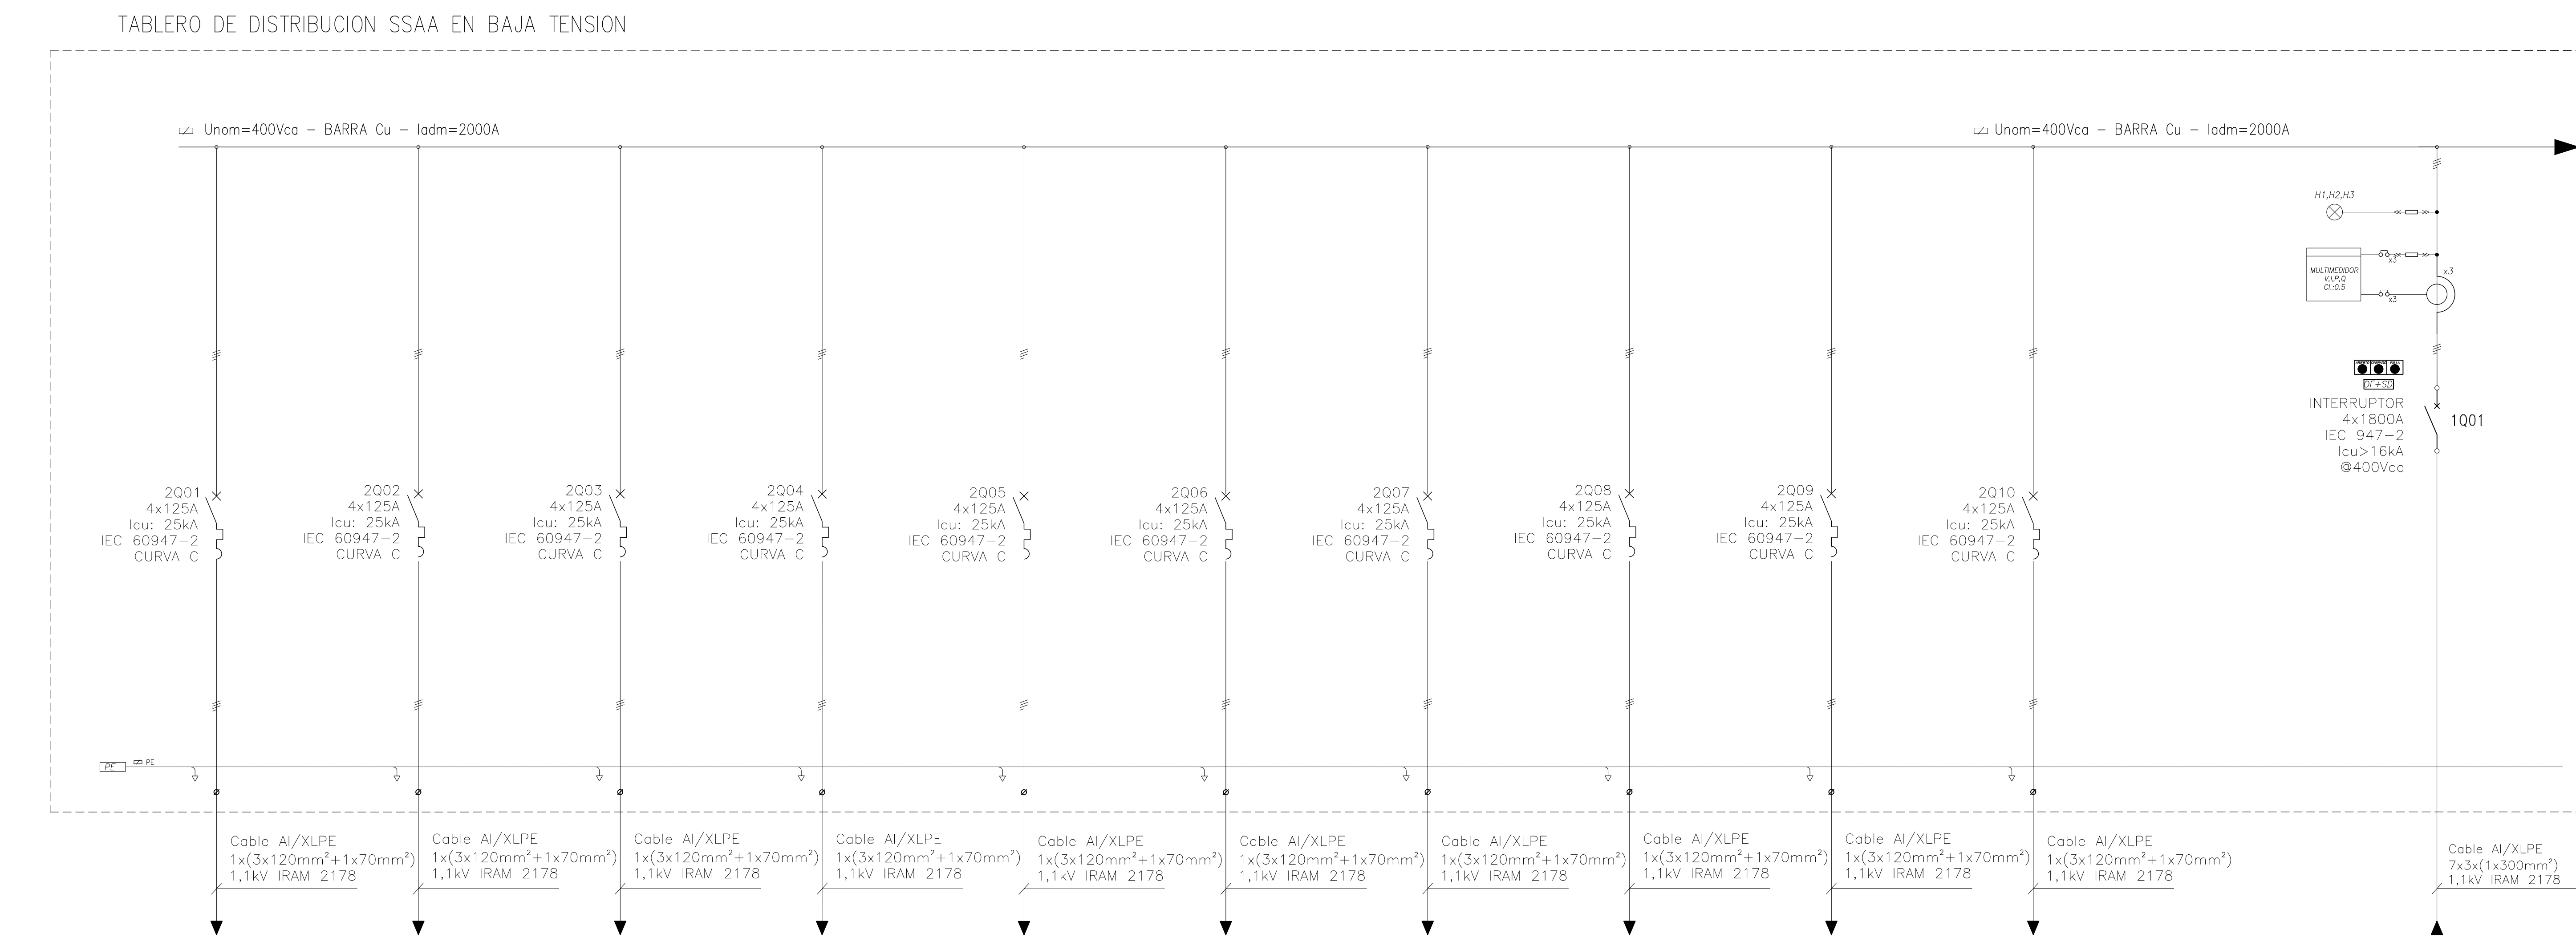

DESIGNACION	SALIDA ALIMENTACIÓN 1	SALIDA ALIMENTACIÓN 2	SALIDA ALIMENTACIÓN 3	SALIDA ALIMENTACIÓN 4	SALIDA ALIMENTACIÓN 5	SALIDA ALIMENTACIÓN 6	SALIDA ALIMENTACIÓN 7	SALIDA ALIMENTACIÓN 8	SALIDA ALIMENTACIÓN 9	SALIDA ALIMENTACIÓN 10		ALIMENTADOR TRANSFORMADOR SSAA
POTENCIA	55 KVA	55 KVA	55 KVA	55 KVA	55 KVA	55 KVA	55 KVA	55 KVA	55 KVA	55 KVA		1250 KVA
TENSION	400 VAC	400 VAC	400 VAC	400 VAC	400 VAC	400 VAC	400 VAC	400 VAC	400 VAC	400 VAC		400 VAC
CORRIENTE	80A	80A	80A	80A	80A	80A	80A	80A	80A	80A		1670A

A	05/02/26	EMISIÓN PARA COTIZACIÓN	E. RODRIGUEZ	E. RODRIGUEZ	CARLOS LONG
REV.	FECHA	DESCRIPCION	DIBUJO	REVISO	APROBO
LISTA DE REVISIONES					
CLIENTE: SECCO		OBRA: ---			
N° PROY./FAB: 50000		LUGAR: ROSARIO			
SECTOR: INGENIERÍA		TITULO: TABLERO BT SSAA			
SUB-TITULO: PORTADA		PARTE: ESQUEMA UNIFILAR			
PLANO N°:		DES-50000-E-EU-40267			
Rev. A		Hoja 02/07			

ESQUEMA UNIFILAR – TABLERO DE DISTRIBUCIÓN BT

TABLERO DE DISTRIBUCION SSAA EN BAJA TENSION

Unom=400Vca – BARRA Cu – Iadm=2000A

Unom=400Vca – BARRA Cu – Iadm=2000A

2Q11
4x125A
Icu: 25kA
IEC 60947-2
CURVA C

2Q12
4x125A
Icu: 25kA
IEC 60947-2
CURVA C

2Q13
4x125A
Icu: 25kA
IEC 60947-2
CURVA C

2Q14
4x125A
Icu: 25kA
IEC 60947-2
CURVA C

2Q15
4x125A
Icu: 25kA
IEC 60947-2
CURVA C

2Q16
4x125A
Icu: 25kA
IEC 60947-2
CURVA C

2Q17
4x125A
Icu: 25kA
IEC 60947-2
CURVA C

2Q18
4x125A
Icu: 25kA
IEC 60947-2
CURVA C

2Q19
4x125A
Icu: 25kA
IEC 60947-2
CURVA C

2Q20
4x125A
Icu: 25kA
IEC 60947-2
CURVA C

Cable Al/XLPE
1x(3x120mm²+1x70mm²)
1,1kV IRAM 2178

Cable Al/XLPE
1x(3x120mm²+1x70mm²)
1,1kV IRAM 2178

Cable Al/XLPE
1x(3x120mm²+1x70mm²)
1,1kV IRAM 2178

Cable Al/XLPE
1x(3x120mm²+1x70mm²)
1,1kV IRAM 2178

Cable Al/XLPE
1x(3x120mm²+1x70mm²)
1,1kV IRAM 2178

Cable Al/XLPE
1x(3x120mm²+1x70mm²)
1,1kV IRAM 2178


Cable Al/XLPE
1x(3x120mm²+1x70mm²)
1,1kV IRAM 2178

Cable Al/XLPE
1x(3x120mm²+1x70mm²)
1,1kV IRAM 2178


Cable Al/XLPE
1x(3x120mm²+1x70mm²)
1,1kV IRAM 2178

Cable Al/XLPE
1x(3x120mm²+1x70mm²)
1,1kV IRAM 2178

DESIGNACION	SALIDA ALIMENTACIÓN 11	SALIDA ALIMENTACIÓN 12	SALIDA ALIMENTACIÓN 13	SALIDA ALIMENTACIÓN 14	SALIDA ALIMENTACIÓN 15	SALIDA ALIMENTACIÓN 16	SALIDA ALIMENTACIÓN 17	SALIDA ALIMENTACIÓN 18	SALIDA ALIMENTACIÓN 19	SALIDA ALIMENTACIÓN 20		
POTENCIA	55 KVA	55 KVA	55 KVA	55 KVA	55 KVA	55 KVA	55 KVA	55 KVA	55 KVA	55 KVA		
TENSION	400 VAC	400 VAC	400 VAC	400 VAC	400 VAC	400 VAC	400 VAC	400 VAC	400 VAC	400 VAC		
CORRIENTE	80A	80A	80A	80A	80A	80A	80A	80A	80A	80A		

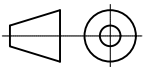A	05/02/26	EMISIÓN PARA COTIZACIÓN	E. RODRIGUEZ	E. RODRIGUEZ	CARLOS LONG
REV.	FECHA	DESCRIPCION	DIBUJO	REVISO	APROBO
LISTA DE REVISIONES					
		CLIENTE: SECCO	OBRA: ---		
		N° PROY./FAB.: 50000	LUGAR: ROSARIO		
SECTOR:	INGENIERÍA		TITULO:	TABLERO BT SSAA	
Prohibida su reproducción total o parcial sin previa autorización escrita. No poder sobre el plano. ANTES DE USAR ESTE PLANO CONSULTE AL DEPARTAMENTO TECNICO POR SU REVISION VIGENTE.		SUB-TITULO: PORTADA			
		PARTE: ESQUEMA UNIFILAR		Nº SAP: ---	
		ESC: S/E	PLANO Nº: DES-50000-E-EU-40267		Rev. Hoja
		TOL: N/A			A 03/07

ESQUEMA UNIFILAR – TABLERO DE DISTRIBUCIÓN BT

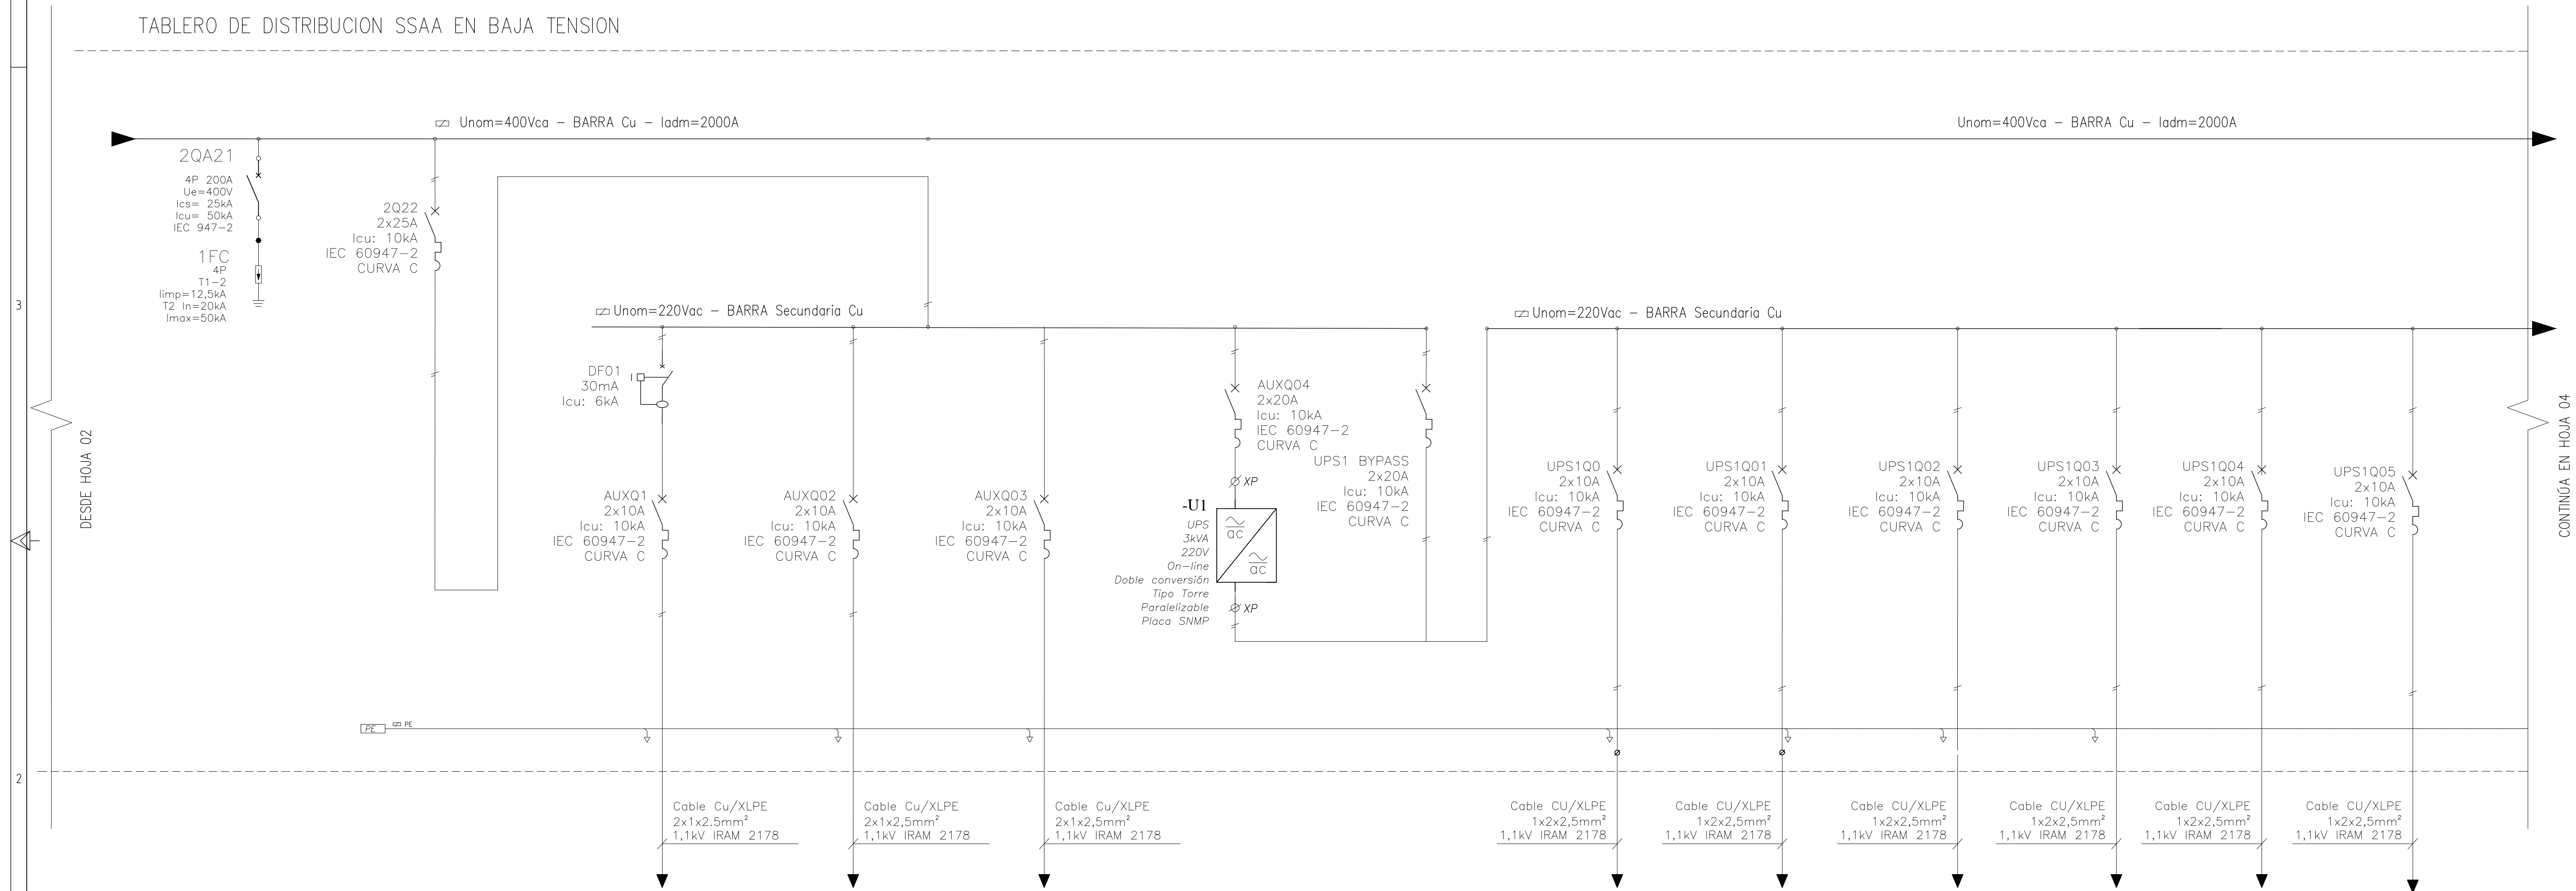


DESIGNACION	DESCARGADOR DE SOBRETENSION	ALIMENTADOR BARRA 220 #1	TOMACORRIENTES	RESERVA	RESERVA	UPS	BY-PASS UPS	MOTOR INTERRUPTOR 1Q1	SALIDA UPS ALIMENTACIÓN 1	SALIDA UPS ALIMENTACIÓN 2	SALIDA UPS ALIMENTACIÓN 3	SALIDA UPS ALIMENTACIÓN 4	SALIDA UPS ALIMENTACIÓN 5
POTENCIA		5,75 kVA	1,4 kVA			3 kVA							
TENSION		230 VAC	220V	400V	400V	220V		220V	220V	220V	220V	220V	220V
CORRIENTE		25A	8 A	8 A	8 A	17 A							

A	05/02/26	EMISIÓN PARA COTIZACIÓN	E. RODRIGUEZ	E. RODRIGUEZ	CARLOS LONG
REV.	FECHA	DESCRIPCIÓN	DIBUJO	REVISO	APROBO
LISTA DE REVISIONES					
		CLIENTE: SECCO	OBRA: ---		
		N° PROY./FAB.: 50000	LUGAR: ROSARIO		
SECTOR:	INGENIERÍA		TITULO:	TABLERO BT SSAA	
Prohibida su reproducción total o parcial sin previa autorización escrita. No medir sobre el plano - ANTES DE USAR ESTE PLANO CONSULTE AL DEPARTAMENTO TÉCNICO POR SU REVISIÓN VIGENTE			SUB-TITULO:	PORTADA	
			PARTÉ:	ESQUEMA UNIFILAR	
	ESC:	S/E	PLANO N°:	Rev.	Hoja
	TOL:	N/A		DES-50000-E-EU-40267	A

ESQUEMA UNIFILAR – TABLERO DE DISTRIBUCIÓN BT

TABLERO DE DISTRIBUCION SSAA EN BAJA TENSION

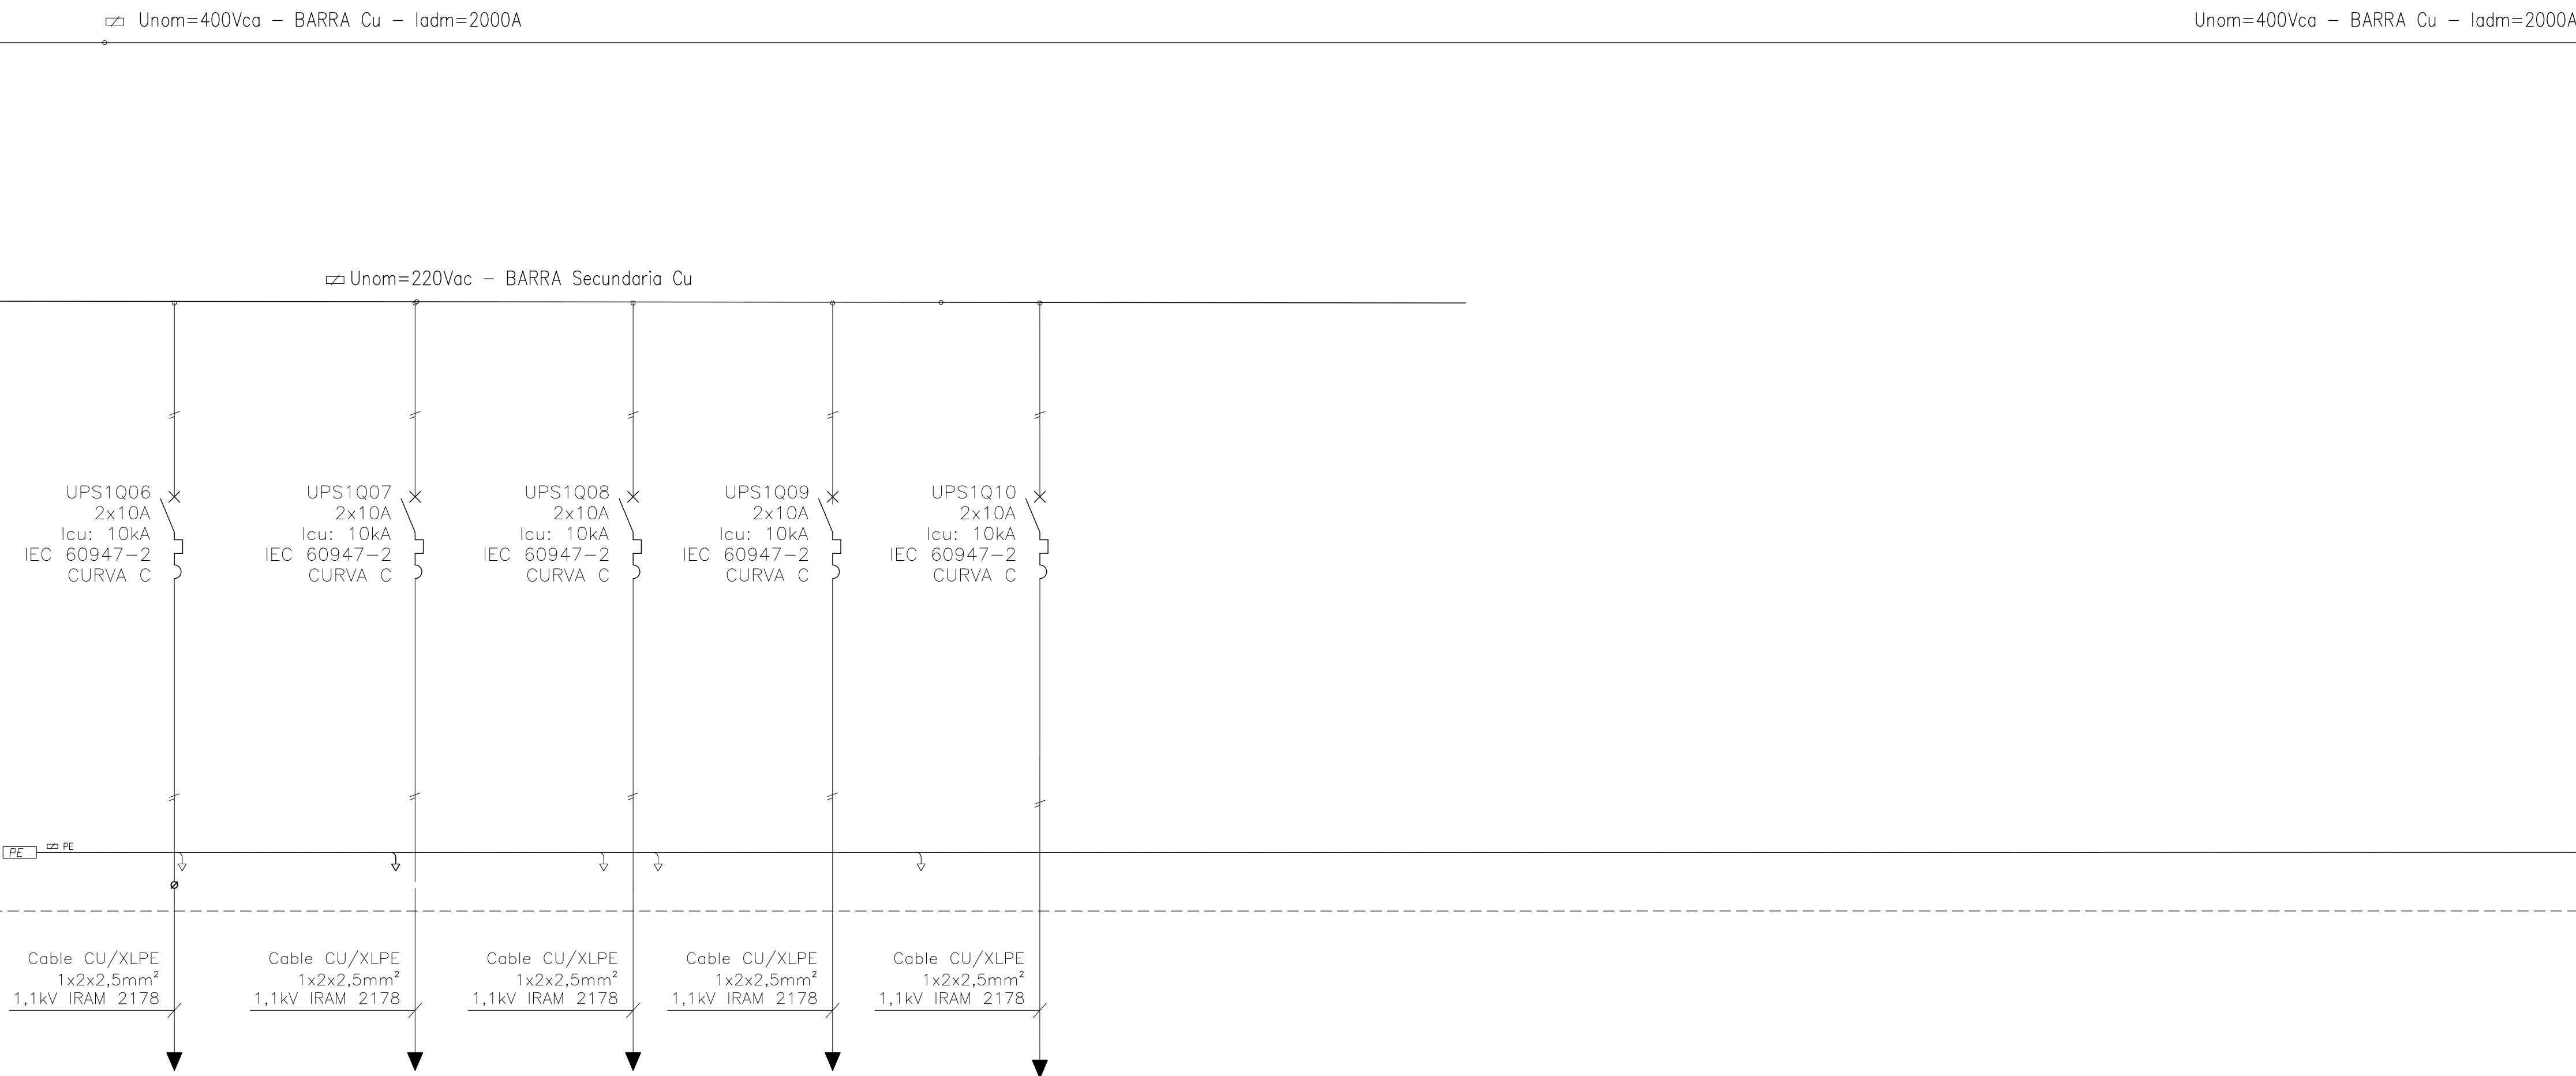


DESIGNACION		SALIDA UPS ALIMENTACIÓN 6	SALIDA UPS ALIMENTACIÓN 7	SALIDA UPS ALIMENTACIÓN 8	SALIDA UPS ALIMENTACIÓN 9	SALIDA UPS ALIMENTACIÓN 10
POTENCIA						
TENSION		220V	220V	220V	220V	220V
CORRIENTE						


A	05/02/26	EMISIÓN PARA COTIZACIÓN	E. RODRIGUEZ	E. RODRIGUEZ	CARLOS LONG
REV.	FECHA	DESCRIPCION	DIBUJO	REVISO	APROBO
LISTA DE REVISIONES					
		CLIENTE: SECCO OBRA: --- N° PROY./FAB.: 50000 LUGAR: ROSARIO			
SECTOR: INGENIERÍA		TITULO: TABLERO BT SSAA SUB-TITULO: PORTADA PARTE: ESQUEMA UNIFILAR N° SAP: ---			
Prohibida su reproducción total o parcial sin previa autorización escrita. No poder usarse el plano sin antes de usar este plano consulte al DEPARTAMENTO TECNICO POR SU REVISIÓN VIGENTE.		ESQ: S/E TOL: N/A		PLANO N°: DES-50000-E-EU-40267	
		Rev. A		Hoja 05/07	

ESQUEMA UNIFILAR – TABLERO DE DISTRIBUCIÓN BT

TABLERO DE DISTRIBUCION SSAA EN BAJA TENSION

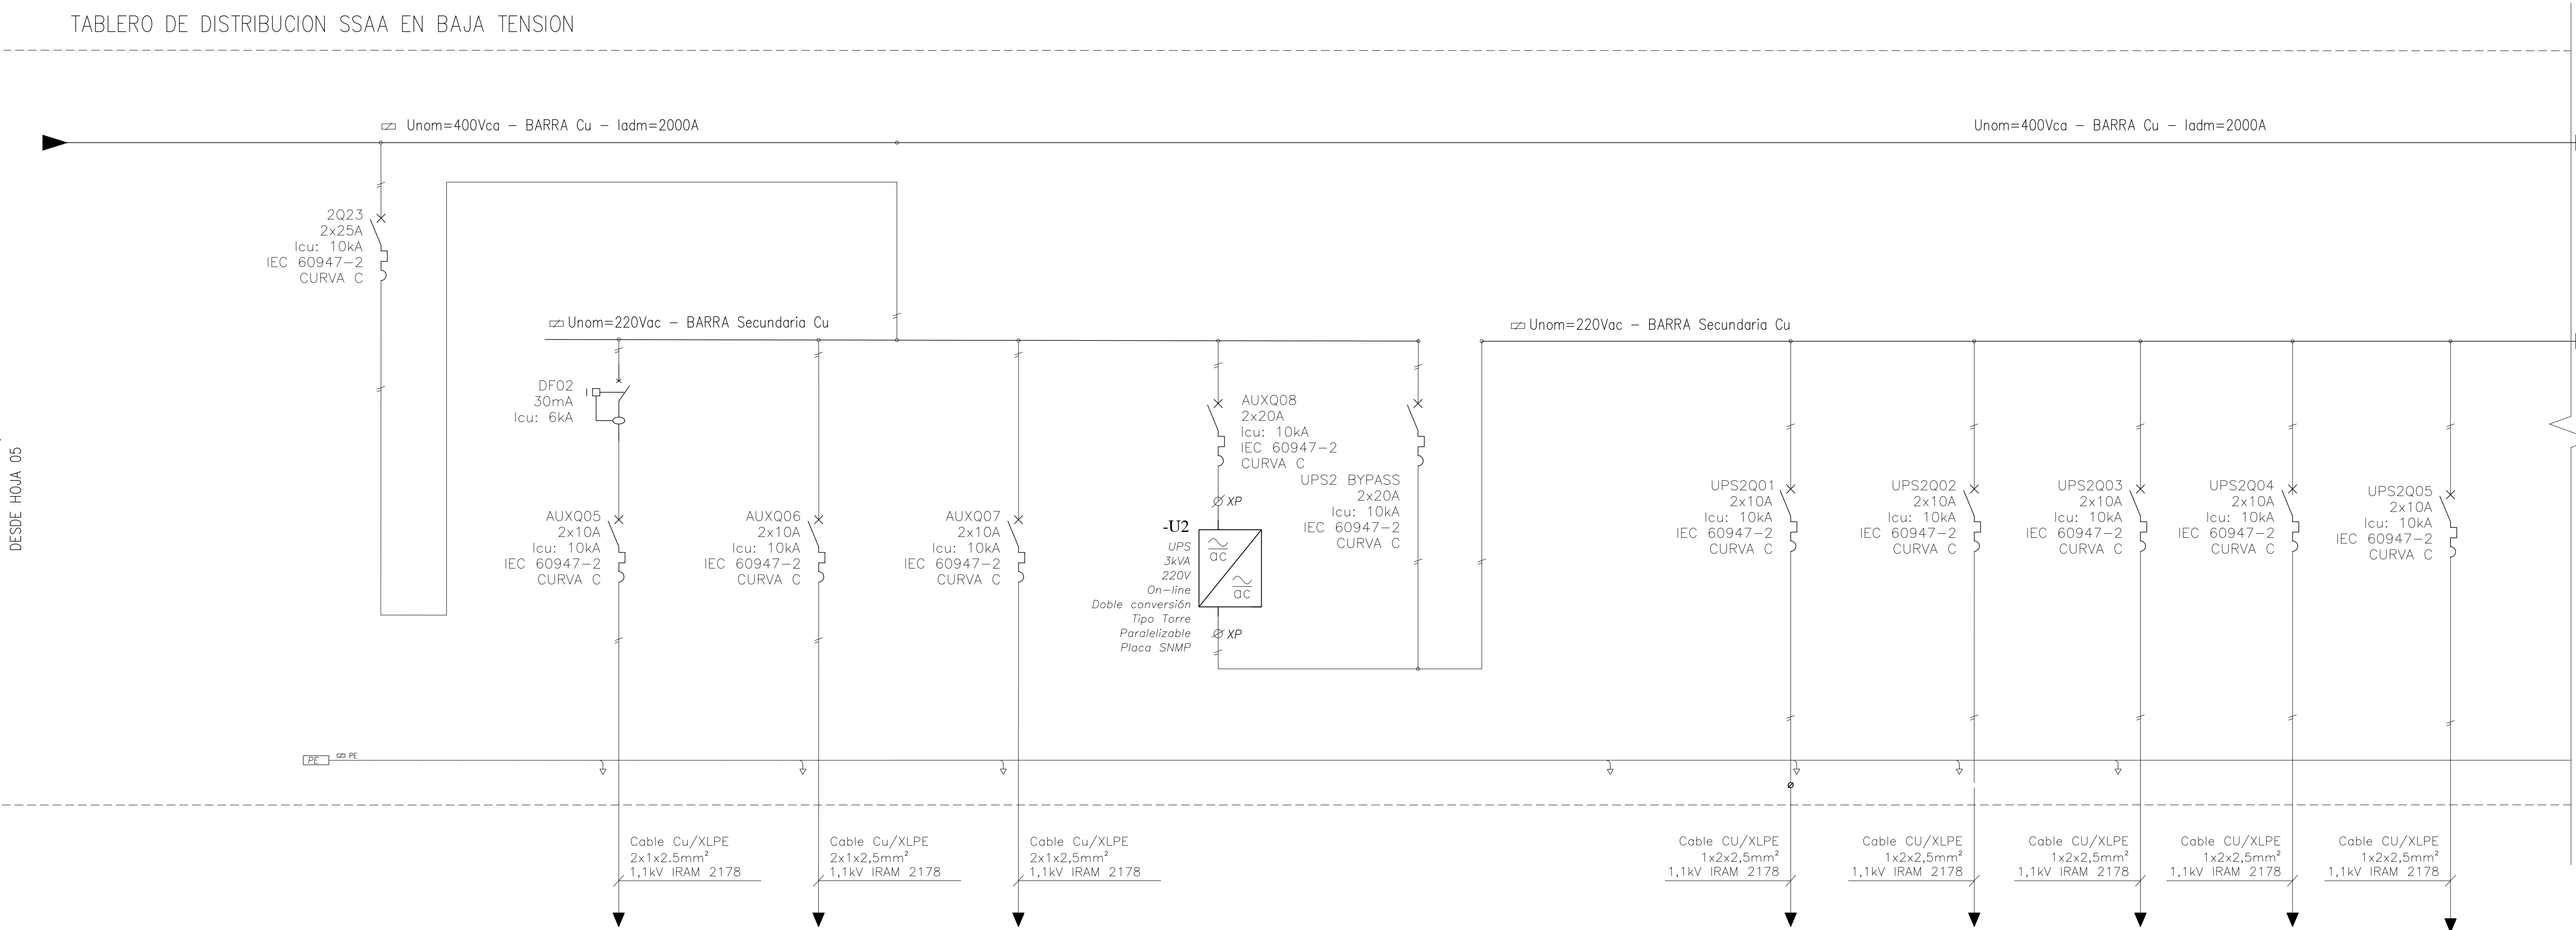

DESIGNACION	DESCARGADOR DE SOBRETENSION	ALIMENTADOR BARRA 220 #1	TOMACORRIENTES	RESERVA	RESERVA	UPS	BY-PASS UPS		SALIDA UPS ALIMENTACIÓN 11	SALIDA UPS ALIMENTACIÓN 12	SALIDA UPS ALIMENTACIÓN 13	SALIDA UPS ALIMENTACIÓN 14	SALIDA UPS ALIMENTACIÓN 15
POTENCIA		5,75 kVA	1,4 kVA			3 kVA							
TENSION		230 VAC	220V	400V	400V	220V			220V	220V	220V	220V	220V
CORRIENTE		25A	8 A	8 A	8 A	17 A							

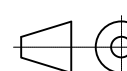A	05/02/26	EMISIÓN PARA COTIZACIÓN		E RODRIGUEZ	E RODRIGUEZ	CARLOS LONG
REV.	FECHA	DESCRIPCION		DIBUJO	REVISO	APROBO
LISTA DE REVISIONES						
		CLIENTE: SECCO		OBRA: ---		
		N° PROY./FAB.: 50000		LUGAR: ROSARIO		
		SECTOR: INGENIERÍA				
		TITULO: TABLERO BT SSAA				
Prohibida su reproducción total o parcial sin previa autorización escrita. No medir sobre el plano - ANTES DE USAR ESTE PLANO CONSULTE AL DEPARTAMENTO TECNICO POR SU REVISIÓN VIGENTE		SUB-TITULO: PORTADA				
		PARTE: ESQUEMA UNIFILAR				
		Nº SAP: ---				
		ESC. S/E			PLANO Nº:	
		TOL. N/A			DES-50000-E-EU-40267	
					Rev. A	Hoja 06/07

ESQUEMA UNIFILAR – TABLERO DE DISTRIBUCIÓN BT

TABLERO DE DISTRIBUCION SSAA EN BAJA TENSION

Unom=400Vca – BARRA Cu – Iadm=2000A

Unom=400Vca – BARRA Cu – Iadm=2000A

Unom=220Vac – BARRA Secundaria Cu

UPS2Q06
2x10A
Icu: 10kA
IEC 60947-2
CURVA C

UPS2Q07
2x10A
Icu: 10kA
IEC 60947-2
CURVA C

UPS2Q08
2x10A
Icu: 10kA
IEC 60947-2
CURVA C

UPS2Q09
2x10A
Icu: 10kA
IEC 60947-2
CURVA C

UPS2Q10
2x10A
Icu: 10kA
IEC 60947-2
CURVA C

PE

Cable CU/XLPE
1x2x2,5mm²
1,1kV IRAM 2178

Cable CU/XLPE
1x2x2,5mm²
1,1kV IRAM 2178

Cable CU/XLPE
1x2x2,5mm²
1,1kV IRAM 2178

Cable CU/XLPE
1x2x2,5mm²
1,1kV IRAM 2178

Cable CU/XLPE
1x2x2,5mm²
1,1kV IRAM 2178

DESIGNACION		SALIDA UPS ALIMENTACIÓN 16	SALIDA UPS ALIMENTACIÓN 17	SALIDA UPS ALIMENTACIÓN 18	SALIDA UPS ALIMENTACIÓN 19	SALIDA UPS ALIMENTACIÓN 20
POTENCIA						
TENSION		220V	220V	220V	220V	220V
CORRIENTE						

A	05/02/26	EMISIÓN PARA COTIZACIÓN	E. RODRIGUEZ	E. RODRIGUEZ	CARLOS LONG
REV.	FECHA	DESCRIPCION	DIBUJO	REVISO	APROBO
LISTA DE REVISIONES					
		CLIENTE: SECCO OBRA: --- N° PROY./FAB: 50000 LUGAR: ROSARIO			
SECTOR: INGENIERÍA		TITULO: TABLERO BT SSAA SUB-TITULO: PORTADA PARTE: ESQUEMA UNIFILAR N° SAP: ---			
Prohibida su reproducción total o parcial sin previa autorización escrita. No pasar sobre el plano - ANTES DE USAR ESTE PLANO CONSULTE AL DEPARTAMENTO TECNICO POR SU REVISIÓN VIGENTE.		ESC: S/E TOL: N/A	PLANO N°: DES-50000-E-EU-40267		Rev. A Hoja 06/07