


ESQUEMA UNIFILAR

CONJUNTO DE CELDAS DE MT 33kV
S/E

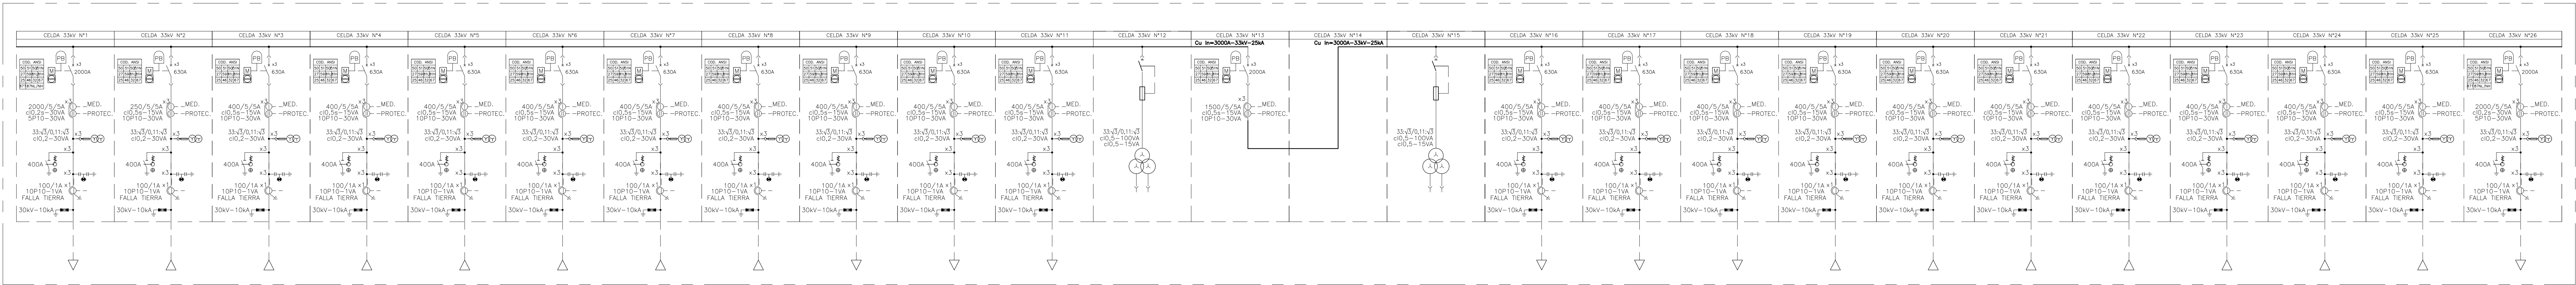

VER ÍTEM: 1 VER ÍTEM: 2 VER ÍTEM: 3 VER ÍTEM: 4 VER ÍTEM: 5 VER ÍTEM: 6 VER ÍTEM: 7 VER ÍTEM: 8 VER ÍTEM: 9 VER ÍTEM: 10 VER ÍTEM: 11 VER ÍTEM: 12 VER ÍTEM: 13 VER ÍTEM: 14 VER ÍTEM: 15 VER ÍTEM: 16 VER ÍTEM: 17 VER ÍTEM: 18 VER ÍTEM: 19 VER ÍTEM: 20 VER ÍTEM: 21 VER ÍTEM: 22 VER ÍTEM: 23 VER ÍTEM: 24 VER ÍTEM: 25 VER ÍTEM: 26

ÍTEM	FORMACIÓN DE TERNAS CAB. MT QUE DEBEN ADMITIR CADA CELDA	RANGO DE APRIETE QUE DEBEN ADMITIR DE LOS CEPOS DE LAS CELDAS	TIPO DE CIRCUITO / CARGA
1	4x(3x1x400mm ²) Cu 33kV IRAM 2178-2	Para cables de diámetro exterior entre Ø32 a Ø56mm	SAIDA DE GENERACIÓN A TRANSFORMADOR 33/132kV
2	2x(3x1x300mm ²) Al 33kV IRAM 2178-2	Para cables de diámetro exterior entre Ø32 a Ø56mm	CIRCUITO COLECTOR DESDE SET'S
3	2x(3x1x300mm ²) Al 33kV IRAM 2178-2	Para cables de diámetro exterior entre Ø32 a Ø56mm	CIRCUITO COLECTOR DESDE SET'S
4	2x(3x1x300mm ²) Al 33kV IRAM 2178-2	Para cables de diámetro exterior entre Ø32 a Ø56mm	CIRCUITO COLECTOR DESDE SET'S
5	2x(3x1x300mm ²) Al 33kV IRAM 2178-2	Para cables de diámetro exterior entre Ø32 a Ø56mm	CIRCUITO COLECTOR DESDE SET'S
6	2x(3x1x300mm ²) Al 33kV IRAM 2178-2	Para cables de diámetro exterior entre Ø32 a Ø56mm	CIRCUITO COLECTOR DESDE SET'S
7	2x(3x1x300mm ²) Al 33kV IRAM 2178-2	Para cables de diámetro exterior entre Ø32 a Ø56mm	CIRCUITO COLECTOR DESDE SET'S
8	2x(3x1x300mm ²) Al 33kV IRAM 2178-2	Para cables de diámetro exterior entre Ø32 a Ø56mm	CIRCUITO COLECTOR DESDE SET'S
9	-	Para cables de diámetro exterior entre Ø32 a Ø56mm	RESERVA #1
10	3x1x50mm ² Al 33kV IRAM 2178-2	Para cables de diámetro exterior entre Ø32 a Ø56mm	TRANSFORMADOR DE SERVICIOS AUXILIARES
11	3x1x50mm ² Al 33kV IRAM 2178-2	Para cables de diámetro exterior entre Ø32 a Ø56mm	BANCO CAPACITORES
12	-	-	CELDA DE MEDICIÓN
13	-	-	CELDA DE ACOPILE
14	-	-	CELDA DE REMONTE
15	-	-	CELDA DE MEDICIÓN
16	3x1x50mm ² Al 33kV IRAM 2178-2	Para cables de diámetro exterior entre Ø32 a Ø56mm	BANCO CAPACITORES
17	3x1x50mm ² Al 33kV IRAM 2178-2	Para cables de diámetro exterior entre Ø32 a Ø56mm	TRANSFORMADOR DE SERVICIOS AUXILIARES
18	-	Para cables de diámetro exterior entre Ø32 a Ø56mm	RESERVA #2
19	2x(3x1x300mm ²) Al 33kV IRAM 2178-2	Para cables de diámetro exterior entre Ø32 a Ø56mm	CIRCUITO COLECTOR DESDE SET'S
20	2x(3x1x300mm ²) Al 33kV IRAM 2178-2	Para cables de diámetro exterior entre Ø32 a Ø56mm	CIRCUITO COLECTOR DESDE SET'S
21	2x(3x1x300mm ²) Al 33kV IRAM 2178-2	Para cables de diámetro exterior entre Ø32 a Ø56mm	CIRCUITO COLECTOR DESDE SET'S
22	2x(3x1x300mm ²) Al 33kV IRAM 2178-2	Para cables de diámetro exterior entre Ø32 a Ø56mm	CIRCUITO COLECTOR DESDE SET'S
23	2x(3x1x300mm ²) Al 33kV IRAM 2178-2	Para cables de diámetro exterior entre Ø32 a Ø56mm	CIRCUITO COLECTOR DESDE SET'S
24	2x(3x1x300mm ²) Al 33kV IRAM 2178-2	Para cables de diámetro exterior entre Ø32 a Ø56mm	CIRCUITO COLECTOR DESDE SET'S
25	2x(3x1x300mm ²) Al 33kV IRAM 2178-2	Para cables de diámetro exterior entre Ø32 a Ø56mm	CIRCUITO COLECTOR DESDE SET'S
26	4x(3x1x400mm ²) Cu 33kV IRAM 2178-2	Para cables de diámetro exterior entre Ø32 a Ø56mm	SAIDA DE GENERACIÓN A TRANSFORMADOR 33/132kV

A	27-10-25	EMISIÓN PARA COTIZACIÓN		F.CALZONE	A.MARTINEZ	G.VALOR
REV	FECHA	DESCRIPCION		DIBUJO	REVISO	APROBO
LISTA DE REVISIONES						
		CLIENTE :	OBRA: PS SAN CARLOS CENTRO			
		Nº PROY./FAB: 50706	LUGAR: SAN CARLOS CENTRO - SANTA FE			
SECTOR:	INGENIERÍA		TITULO CONJUNTO DE CELDAS MT 33kV			
		SUB-TITULO ESQUEMA UNIFILAR				
		PARTE				
		PLANO Nº: ING-50000-E-EU-43739				
		Rev: A				
		Hoja: 1/1				