


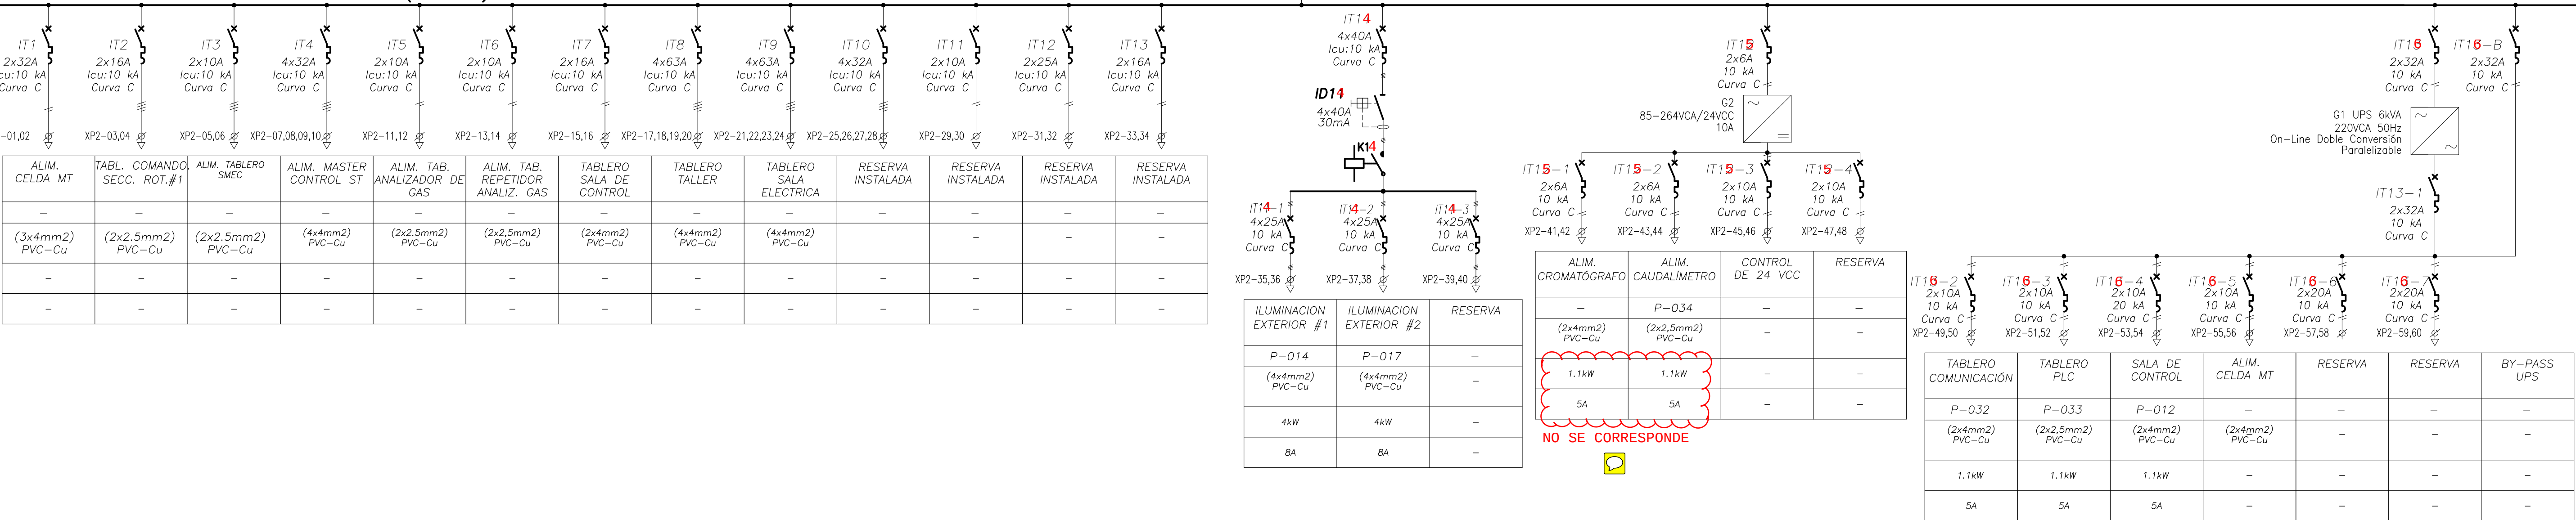
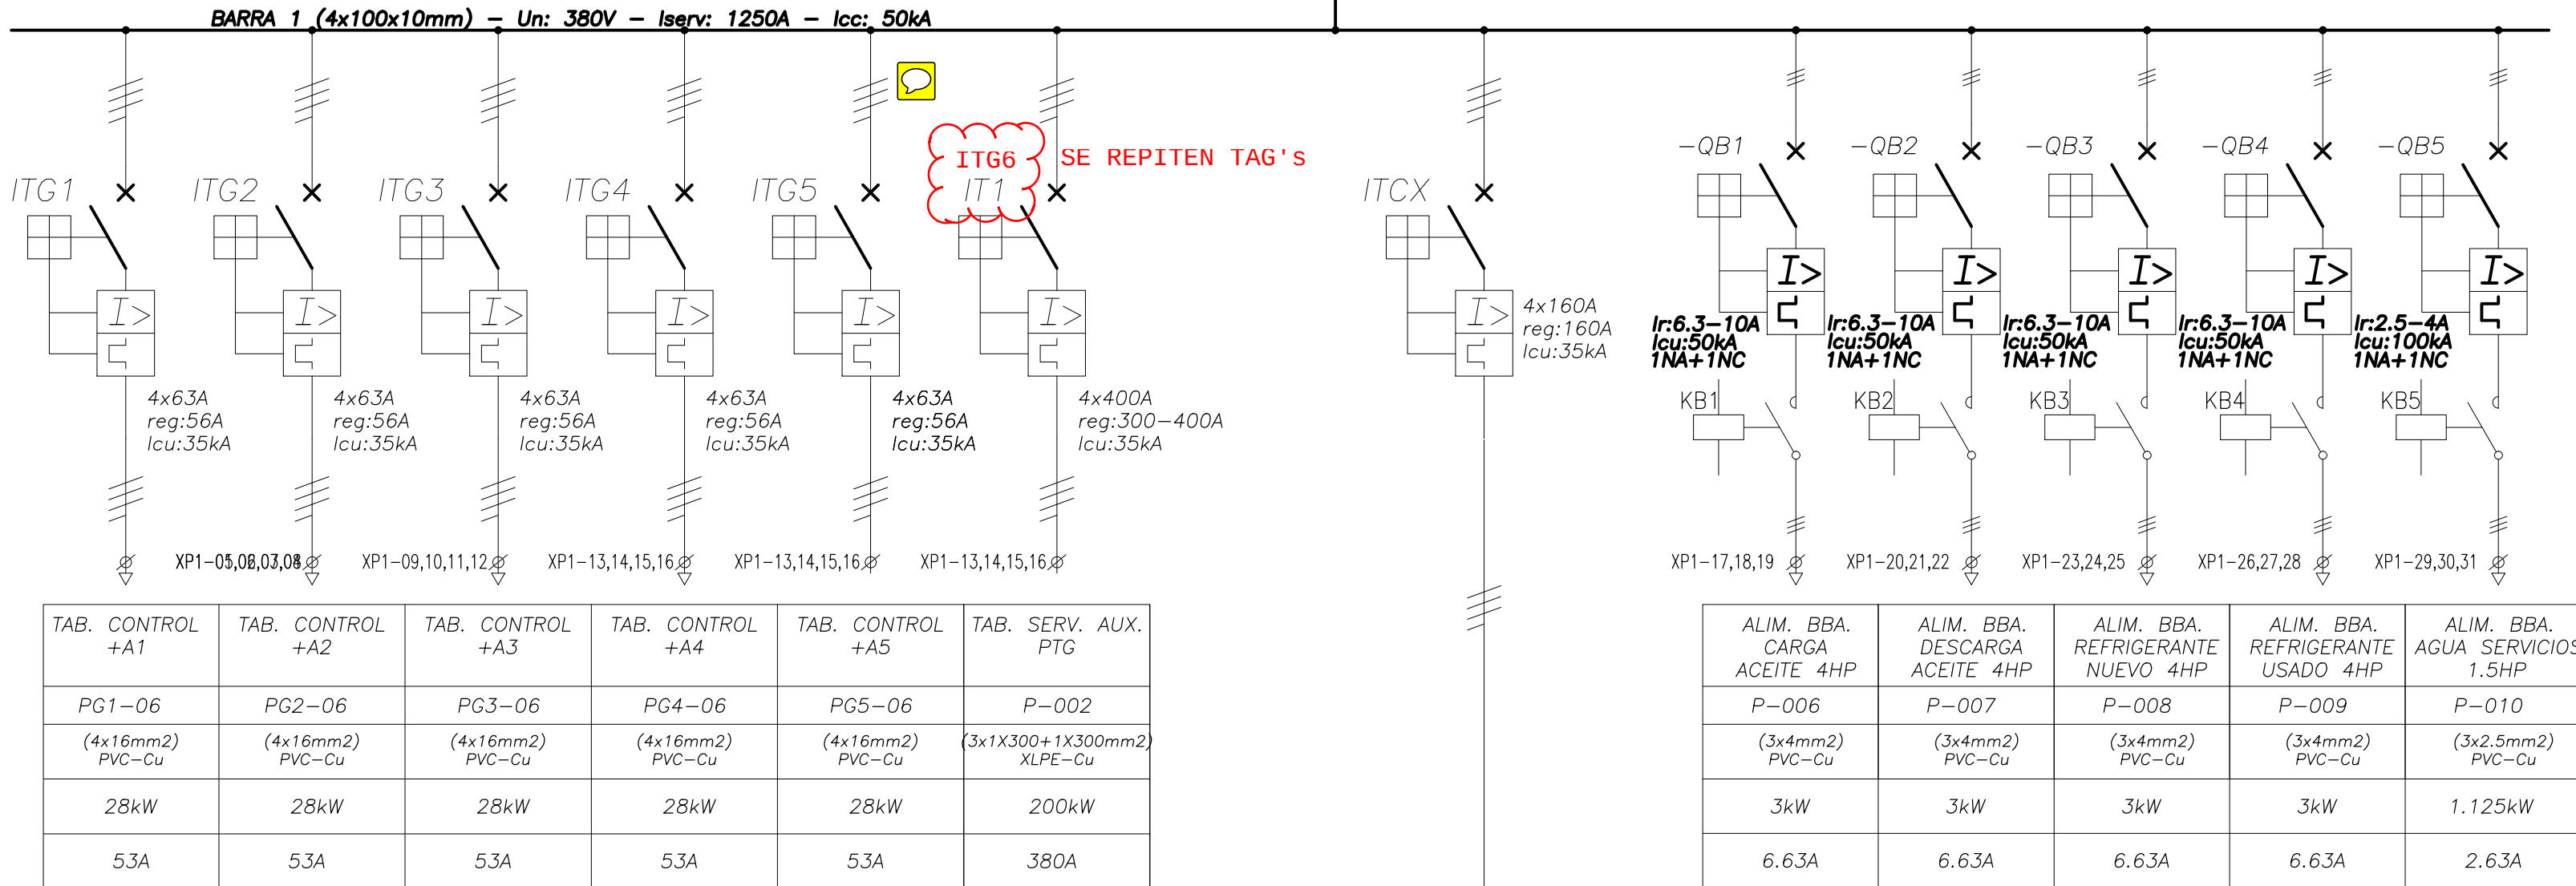


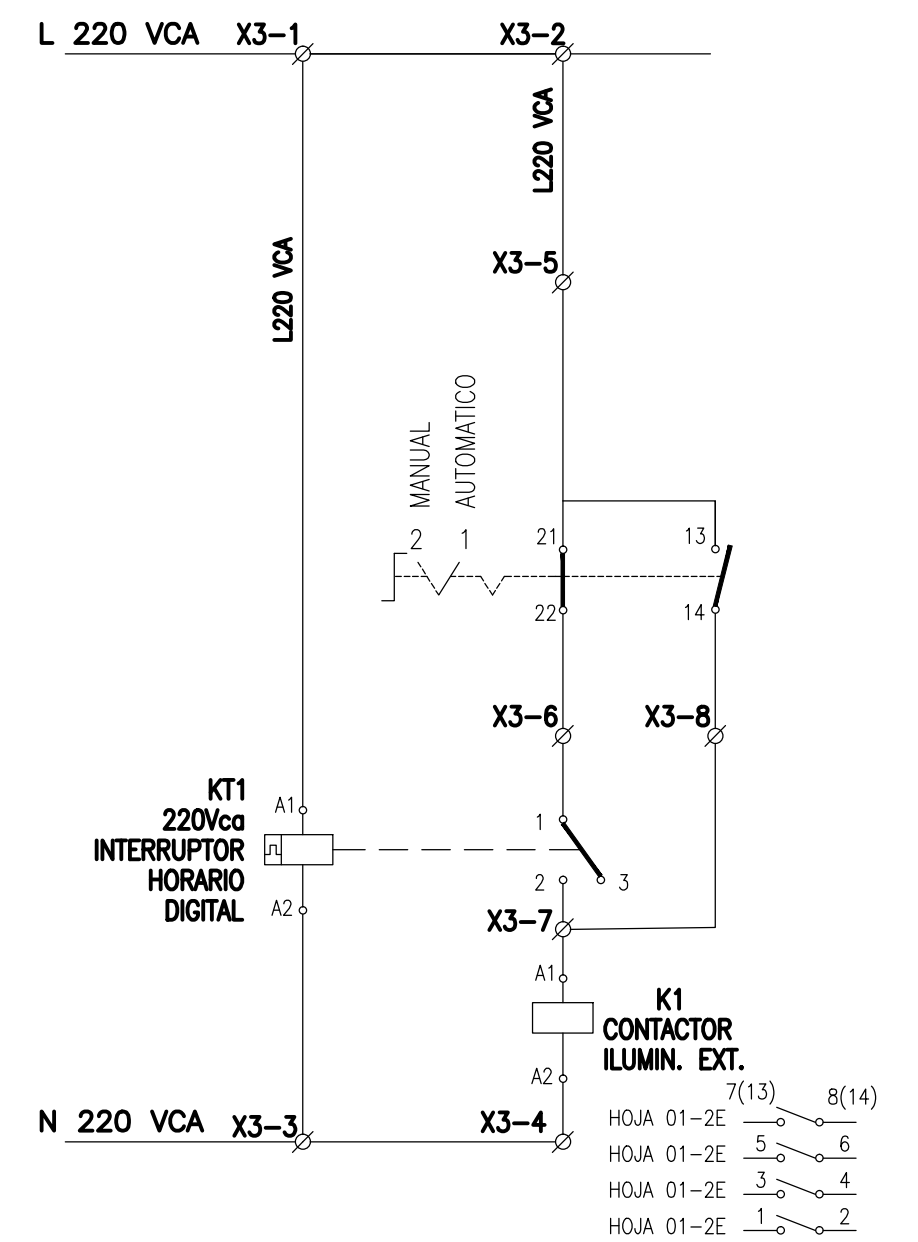


A	26-02-18	EMISIÓN PARA COTIZACIÓN	DIMARABELLA	SORLANDO	M. YANZON
REV.	FECHA	DESCRIPCION	DIBUJO	REVISO	APROBO
LISTA DE REVISIONES					
 SECCO ENERGÍAS RENOVABLES S.A.			CLIENTE: CAMMESA	OBRA: RENOVAR	
			N° PROY./FAB.: 50000	LUGAR: CEAMSE	
SECTOR: INGENIERÍA			TÍTULO: CENTRAL DE GENERACIÓN		
SUB-TÍTULO:			PARTE: TABLERO DE SERV. AUX. N° SAP: -		
Prohibida su reproducción total o parcial sin previa autorización escrita. Su uso está limitado al plano de ingeniería técnica por su exclusiva validez.			PLANO N°:		Rev. Hoja
 ESC: S/E TOL:			ING-50000E-PT-24175		A 1

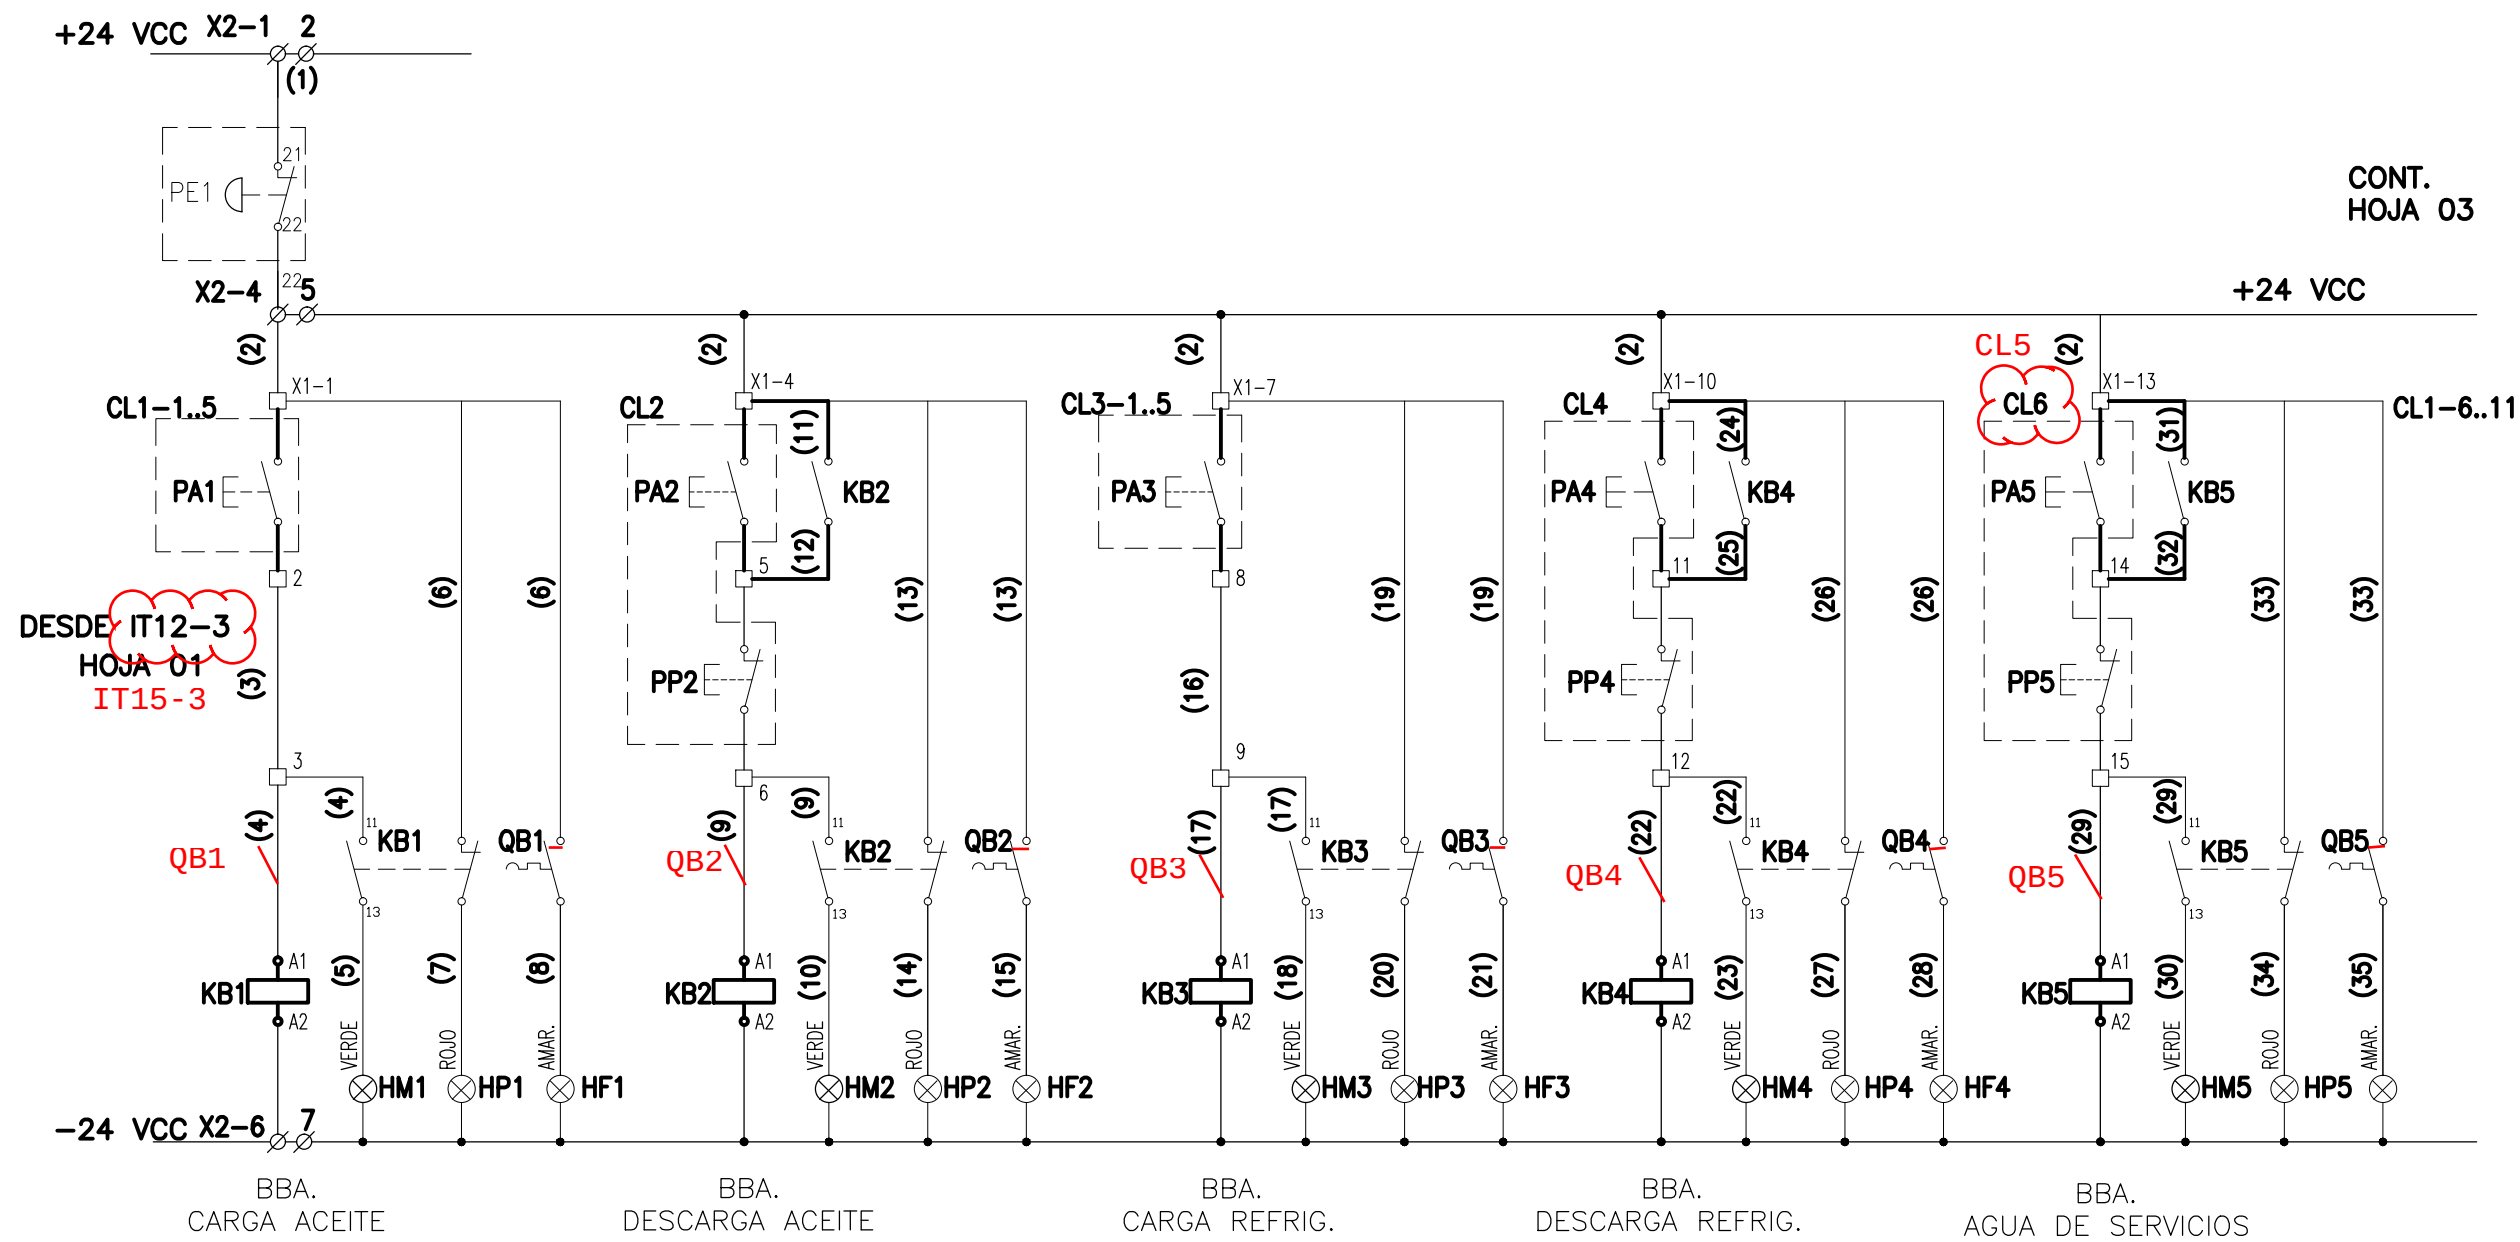

SECCO ENERGÍAS RENOVABLES S.A.		TITULO: TABLERO DE SERV. AUX. SUB-TITULO: CT - RENOVAR PARTE: FUNCIONAL Nº SAP:			
	ESC: S/E	PLANO Nº: ING-50000-E-PT-24175		Rev. A	Hoja 02
	TOL:				

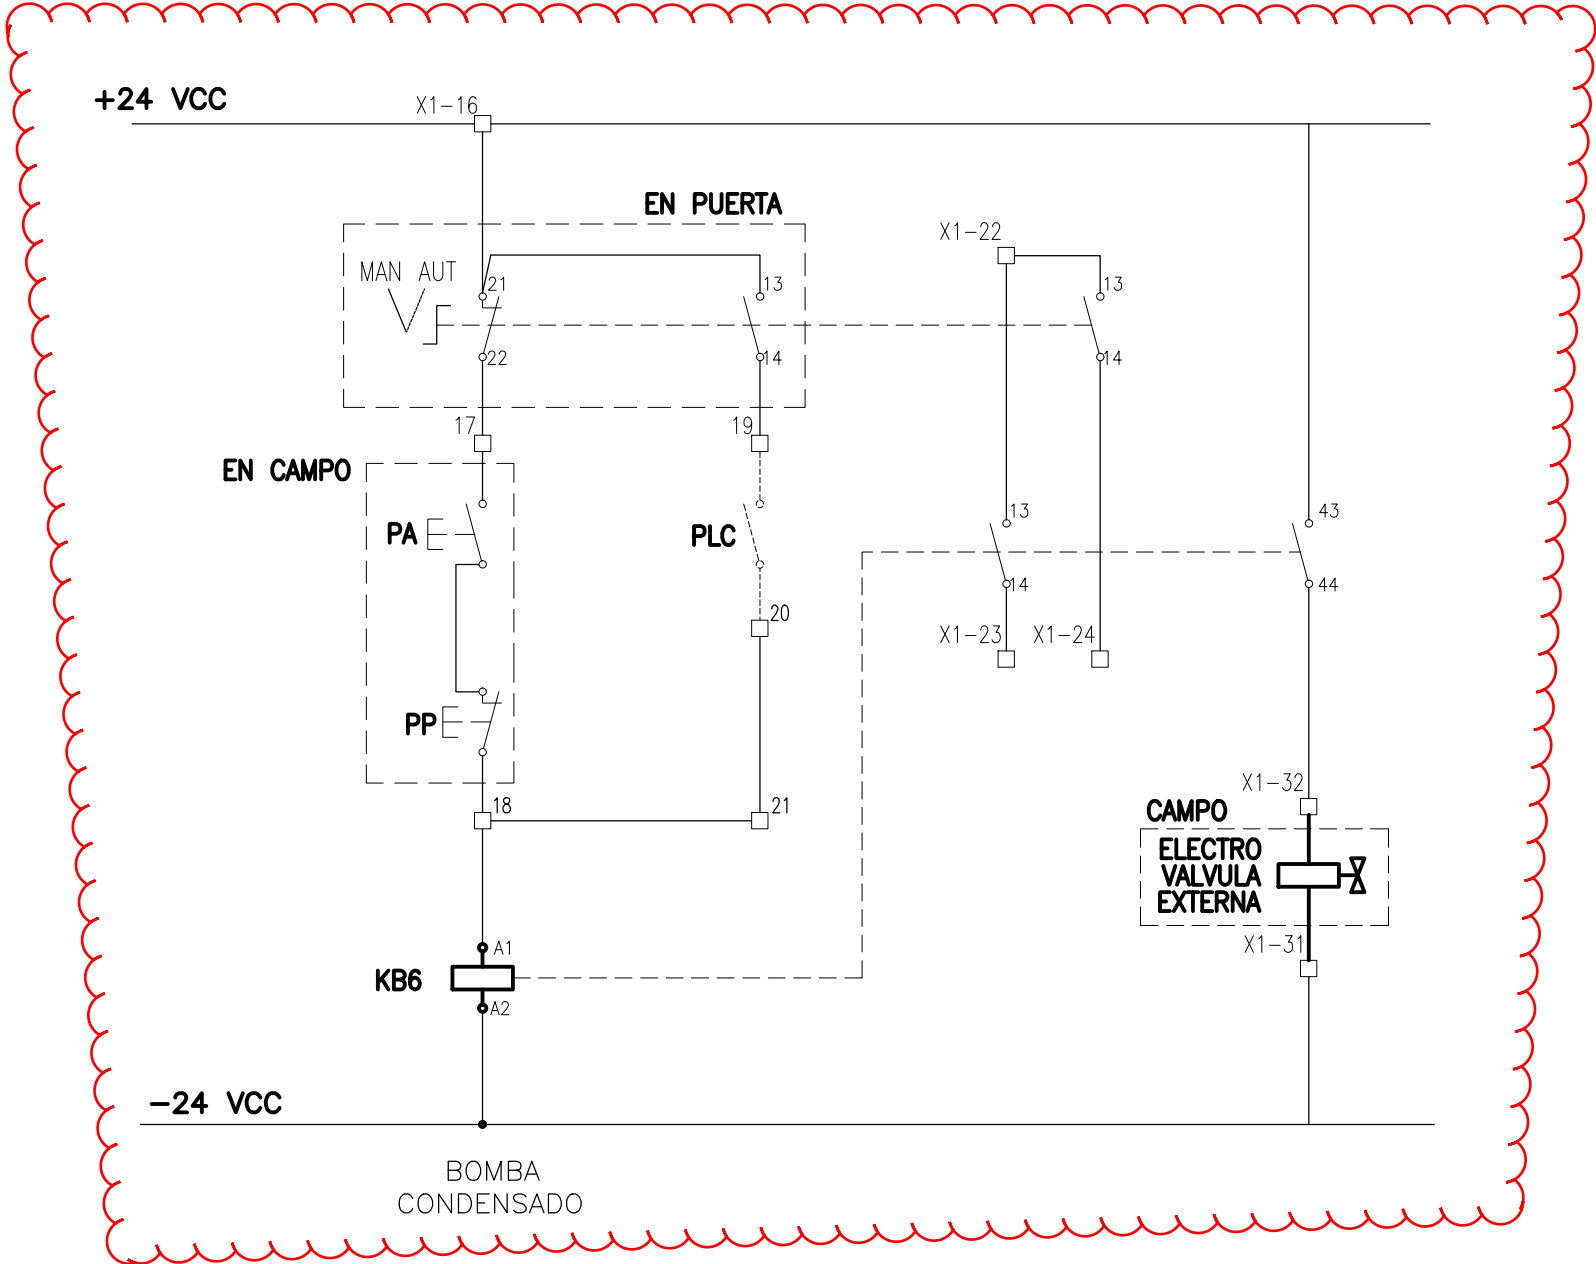

NO SE ENCUENTRA EN EL CIRCUITO UNIFILAR LA BOMBA CONDENSADO.

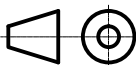 ENERGÍAS RENOVABLES S.A.	TITULO: TABLERO DE SERV. AUX.		
	SUB-TITULO: CT - RENOVAR		
	PARTE: FUNCIONAL		
	ESC:	S/E	Rev. A
	TOL:		03
PLANO Nº:		ING-50000-E-PT-24175	
Nº SAP:			