


1

7

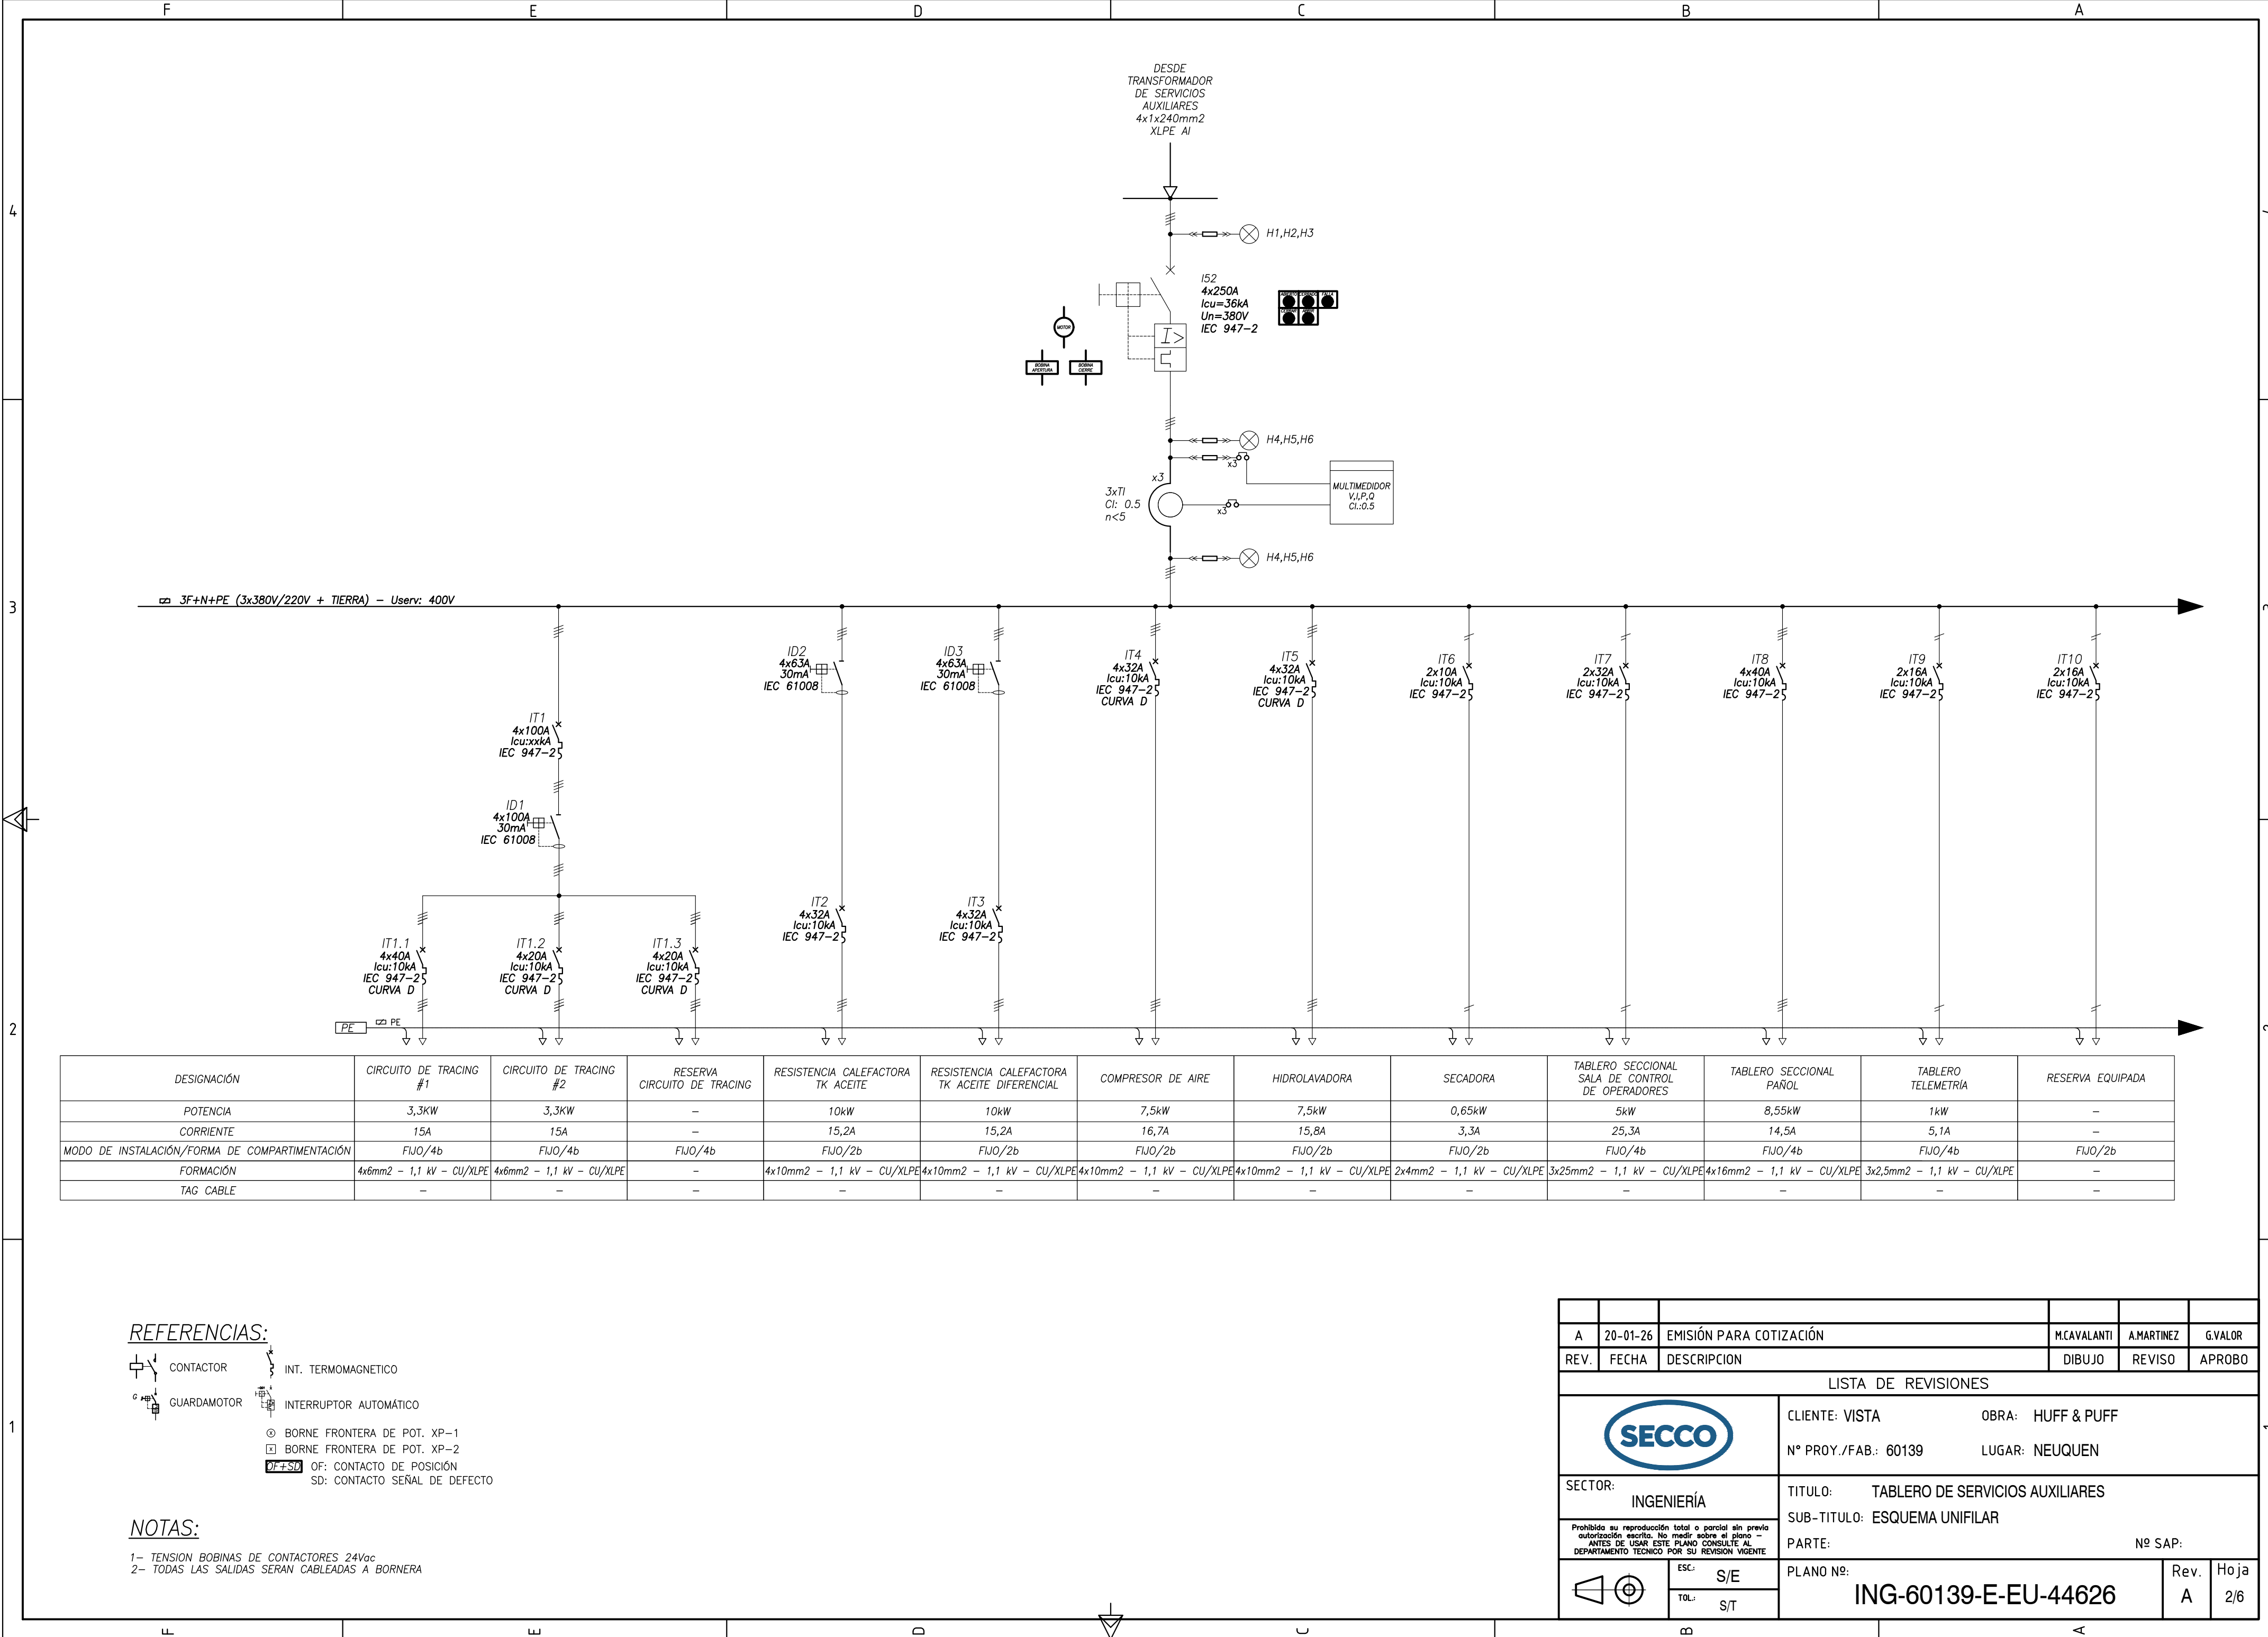


DESIGNACIÓN	CIRCUITO DE TRACING #1	CIRCUITO DE TRACING #2	RESERVA CIRCUITO DE TRACING	RESISTENCIA CALEFACTORA TK ACEITE	RESISTENCIA CALEFACTORA TK ACEITE DIFERENCIAL	COMPRESOR DE AIRE	HIDROLAVADORA	SECADORA	TABLERO SECCIONAL SALA DE CONTROL DE OPERADORES	TABLERO SECCIONAL PAÑOL	TABLERO TELEMETRÍA	RESERVA EQUIPADA
POTENCIA	3,3KW	3,3KW	-	10kW	10kW	7,5kW	7,5kW	0,65kW	5kW	8,55kW	1kW	-
CORRIENTE	15A	15A	-	15,2A	15,2A	16,7A	15,8A	3,3A	25,3A	14,5A	5,1A	-
MODO DE INSTALACIÓN/FORMA DE COMPARTIMENTACIÓN	FIJO/4b	FIJO/4b	FIJO/4b	FIJO/2b	FIJO/2b	FIJO/2b	FIJO/2b	FIJO/2b	FIJO/4b	FIJO/4b	FIJO/4b	FIJO/2b
FORMACIÓN	4x6mm2 - 1,1 kV - CU/XLPE	4x6mm2 - 1,1 kV - CU/XLPE	-	4x10mm2 - 1,1 kV - CU/XLPE	4x10mm2 - 1,1 kV - CU/XLPE	4x10mm2 - 1,1 kV - CU/XLPE	4x10mm2 - 1,1 kV - CU/XLPE	2x4mm2 - 1,1 kV - CU/XLPE	3x25mm2 - 1,1 kV - CU/XLPE	4x16mm2 - 1,1 kV - CU/XLPE	3x2,5mm2 - 1,1 kV - CU/XLPE	-
TAG CABLE	-	-	-	-	-	-	-	-	-	-	-	-


REFERENCIAS:

-  CONTACTOR
-  INT. TERMOMAGNETICO
-  GUARDAMOTOR
-  INTERRUPTOR AUTOMÁTICO
-  BORNE FRONTERA DE POT. XP-1
-  BORNE FRONTERA DE POT. XP-2
-  OF+SD OF: CONTACTO DE POSICIÓN
SD: CONTACTO SEÑAL DE DEFECTO

NOTAS:


- 1- TENSION BOBINAS DE CONTACTORES 24V_{ac}
2- TODAS LAS SALIDAS SERAN CABLEADAS A BORNERA

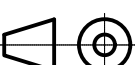A	20-01-26	EMISIÓN PARA COTIZACIÓN	M.CAVALANTI	A.MARTINEZ	G.VALOR
REV.	FECHA	DESCRIPCION	DIBUJO	REVISO	APROBO
LISTA DE REVISIONES					
		CLIENTE: VISTA OBRA: HUFF & PUFF			
		N° PROJ./FAB.: 60139 LUGAR: NEUQUEN			
SECTOR: INGENIERÍA		TITULO: TABLERO DE SERVICIOS AUXILIARES			
		SUB-TITULO: ESQUEMA UNIFILAR			
		PARTE: N° SAP:			
		ESC: S/E	PLANO N°:		
		TOL: S/T	ING-60139-E-EU-44626		
			Rev. A	Hoja 2/6	

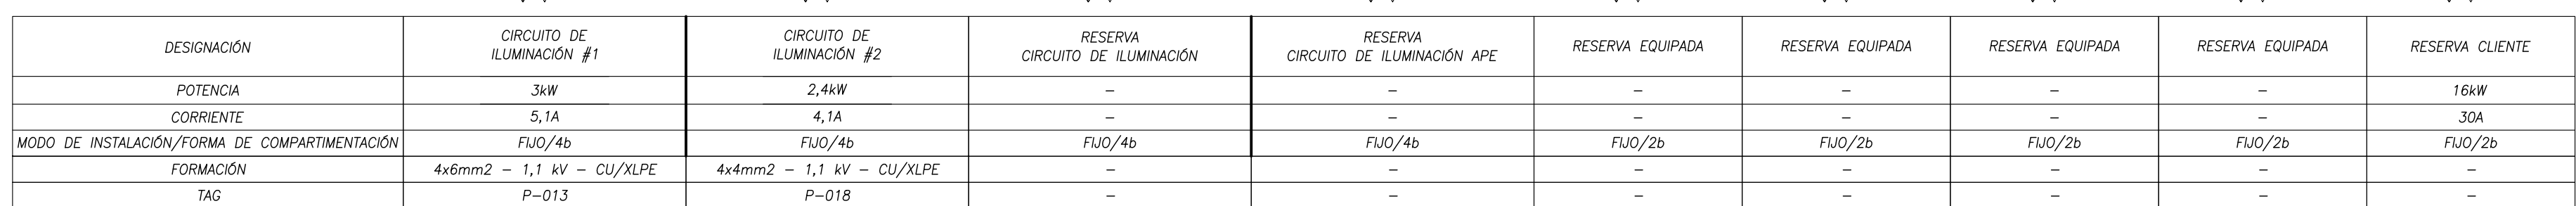

 CONTACTOR
 INT. TERMOMAGNETICO
 GUARDAMOTOR
 INTERRUPTOR AUTOMÁTICO
 ☉ BORNE FRONTERA DE POT. XP-1
 ☒ BORNE FRONTERA DE POT. XP-2
OP+S/O OF: CONTACTO DE POSICIÓN
 SD: CONTACTO SEÑAL DE DEFECTO

A2 IRAM 4504

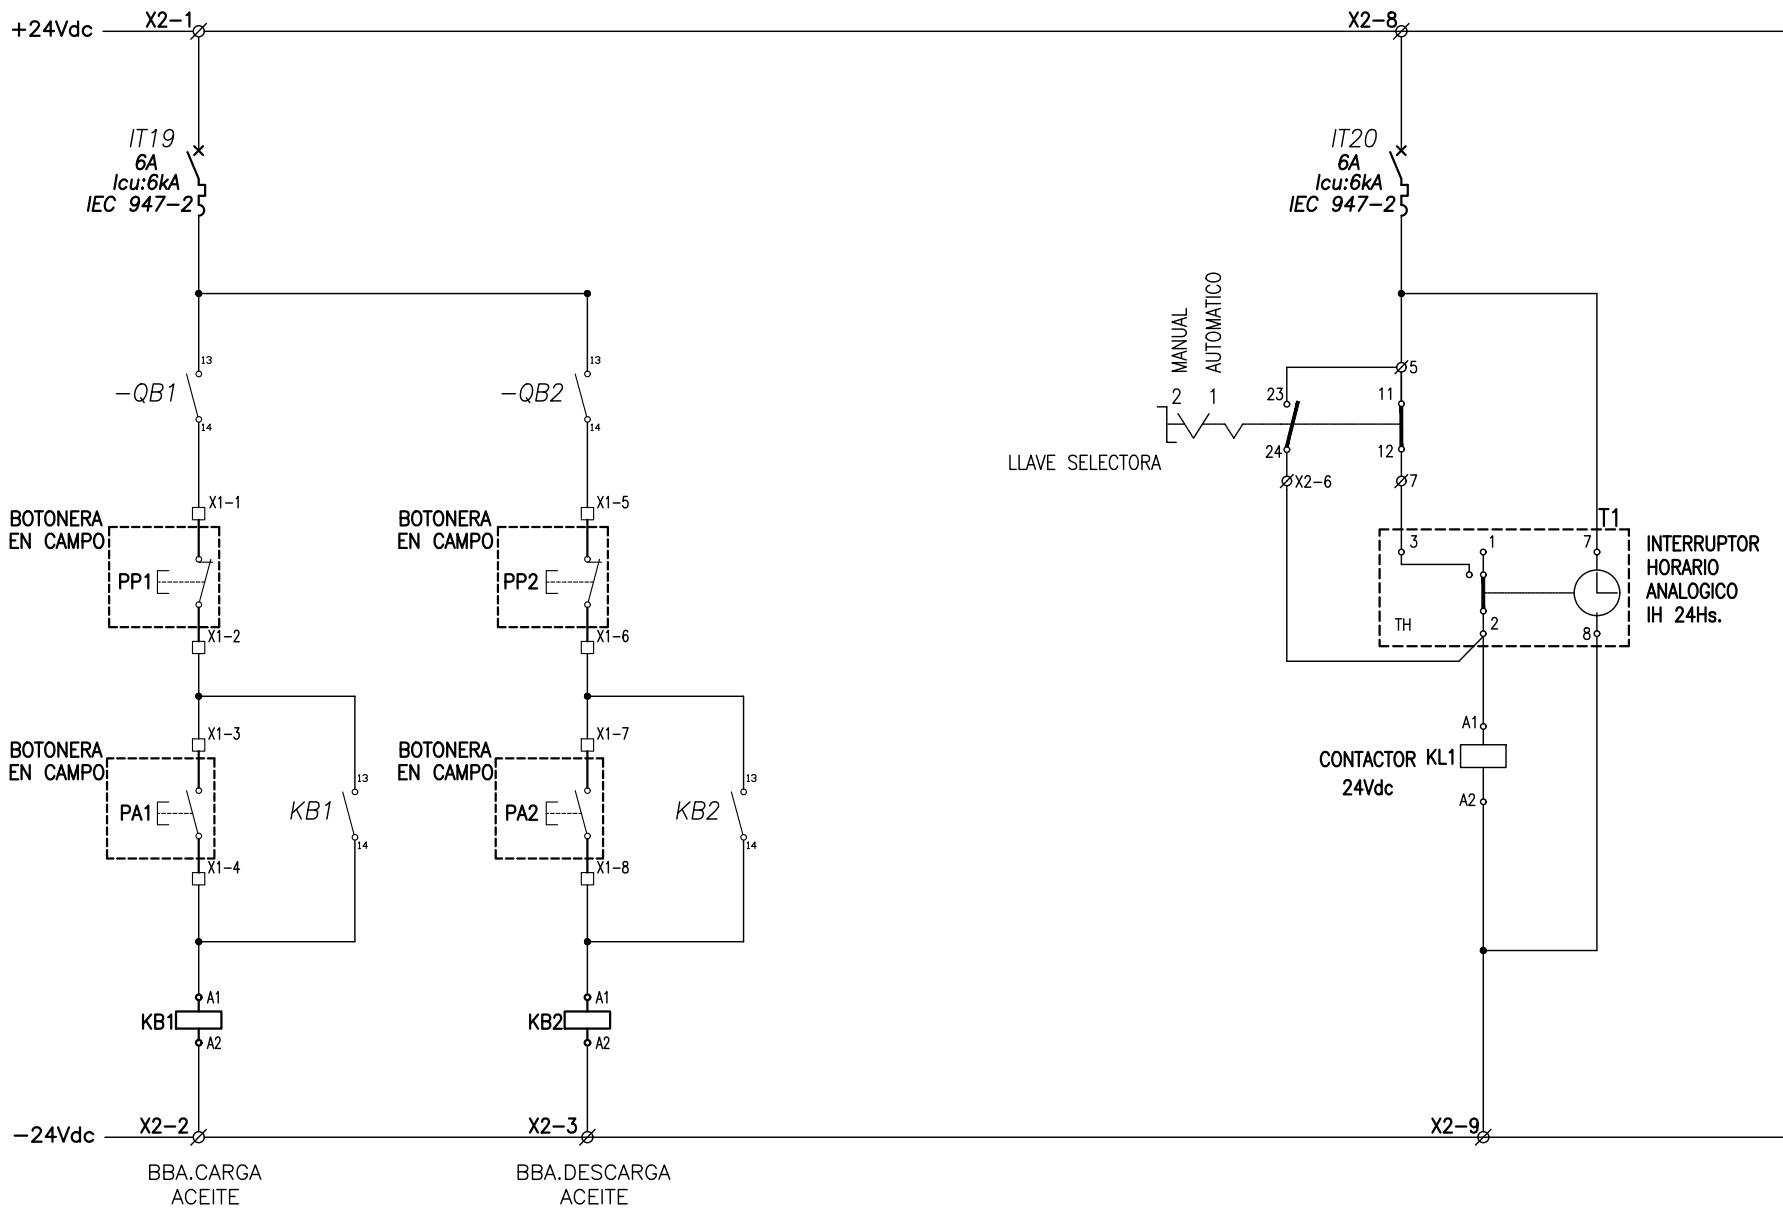

REFERENCIAS:

X1: BORNE FRONTERA DE COMANDO
X2: BORNE INTERNO

A	20-01-26	EMISIÓN PARA COTIZACIÓN	M.CAVALANTI	A.MARTINEZ	G.VALOR
REV.	FECHA	DESCRIPCION	DIBUJO	REVISO	APROBO
LISTA DE REVISIONES					
		CLIENTE: VISTA OBRA: HUFF & PUFF			
N° PROY./FAB.: 60139		LUGAR: NEUQUEN			
SECTOR: INGENIERÍA		TITULO: TABLERO DE SERVICIOS AUXILIARES			
SUB-TITULO: ESQUEMA UNIFILAR		PARTE: N° SAP:			
Prohibida su reproducción total o parcial sin previa autorización escrita. No medir sobre el plano - ANTES DE USAR ESTE PLANO CONSULTE AL DEPARTAMENTO TECNICO POR SU REVISION VIGENTE		PLANO N°: ING-60139-E-EU-44626		Rev. A	Hoja 6/6
		ESC: S/E			
		TOL: S/T			