

TAB 1CMSD 1CF xxx CB xMRO

LEYENDA:

1CM: UNA CAMARA DE MEDIA TEMPERATURA
SD: SIN DESCONGELAMIENTO
1CF: PARA UNA CENTRAL DE FRIO
x: MARCA DE MATERIALES ELECTRICOS. S=SIEMENS, H=SCHNEIDER, A=ABB
x: CON O SIN CORTE EN NEUTRO. SE REPRESENTA CON LA LETRA "N"
x: CON O SIN CONTRAFRENTE. SE REPRESENTA CON LA LETRA "C"
CB: CON CONTROLADOR CAREL VERSION B
xM: CANTIDAD DE EVAPORADORES MONOFASICO
RO: SIN CIRCUITOS DE RESISTENCIAS DE DESCONGELAMIENTO.

NOTAS GENERALES:

- 1) GABINETES FABRICADOS S/IEC60670-24 Y ARMADOS S/IEC60639-3.
- 2) GRADO DE PROTECCION IP42 O SUPERIOR. PUERTAS CON BURLETES INYECTADOS Y CIERRE LABERINTICO.
- 3) CONTRA FRENTE METALICO.
- 4) COMPONENTES ELECTRICOS MONTADOS EN RIEL DIN SOBRE PLACA DE MONTAJE.
- 5) TODOS LOS MATERIALES UTILIZADOS DEBEN SER AUTOEXTINGIBLES , DE ALTA RIGIDEZ DIELÉCTRICA Y NO HIGROSCÓPICOS.
- 6) LAS BORNERAS DE SALIDA PARA ALIMENTACION DE CIRCUITOS SERAN DE UN DIAMETRO MAYOR QUE EL CABLE UTILIZADO EN EL CIRCUITO.
- 7) PINTURA EXTERIOR COLOR RAL 7035.
- 8) TUERCAS, ARANDELAS Y TORNILLOS DEBERAN SER GALVANIZADOS O CADMIADOS.



Juan Pablo II 8050
S2011PWA - Rosario

Tel: +54(0) 341 410 6100
Fax: +54(0) 341 410 6100

MODELO:

TITULO: TAB 1CMSD 1CF xxx CB xMRO REV 2

DESCRIPCION: CARATULA

DESARROLLO: -

SISTEMA DE PROY.

PESO: -KG

TOLERANCIA: +/- X

N° DE HOJA: 1 CONT. 2

DIBUJO: L.PERNA

FECHA: 31/10/2025


APROBO: N.DYKE

CODIGO: 0195XXXX

ESTE DISEÑO NO PUEDE SER REPRODUCIDO O UTILIZADO POR TERCEROS SIN AUTORIZACIÓN PREVIA

D		C									B				A								
PAG.	DESIGNACION	INDICE DE MODIFICACION									PAG.	DESIGNACION	INDICE DE MODIFICACION										
		A	B	C	D	E	0	1	2	3			A	B	C	D	E	0	1	2	3		
01/01E	CARATULA	X					X	X	X		19/18E	DETALLE MONTAJE DE TABLERO	X					X	X	X			
02/02E	INDICE Y REVISIONES	X					X	X	X		20/19E	DETALLE SOPORTE DE MONTAJE	X					X	X	X			
03/03E	CARACTERISTICAS DE FABRICACION	X					X	X	X														
04	DISTRIB. DE POTENCIA Y CONTROL	X					X	X	X														
04E	DISTRIB. DE POTENCIA Y CONTROL (E)	X					X	X	X														
05	CONEXIONADO DE CIRCUITOS AUXILIARES	X					X	X	X														
05E	CONEXIONADO DE CIRCUITOS AUXILIARES (E)	X					X	X	X														
06	CONEXIONADO DE FORZADORES	X					X	X	X														
06E	CONEXIONADO DE FORZADORES (E)	X					X	X	X														
07	TOPOGRAFICO: VISTA EXTERIOR (3 EVAP./2 EVAP.)	X					X	X	X														
07E	TOPOGRAFICO: VISTA EXTERIOR (3 EVAP./2 EVAP./1 EVAP) (E)	X					X	X	X														
08	TOPOGRAFICO: VISTA EXTERIOR (1 EVAP.)	X					X	X	X														
09	TOPOGRAFICO: VISTA INTERIOR (3 EVAP.)	X					X	X	X														
08E	TOPOGRAFICO: VISTA INTERIOR (3 EVAP.) (E)	X					X	X	X														
10	TOPOGRAFICO: VISTA INTERIOR (2 EVAP.)	X					X	X	X														
09E	TOPOGRAFICO: VISTA INTERIOR (2 EVAP.) (E)	X					X	X	X														
11	TOPOGRAFICO: VISTA INTERIOR (1 EVAP.)	X					X	X	X														
10E	TOPOGRAFICO: VISTA INTERIOR (1 EVAP.) (E)	X					X	X	X														
12	TOPOGRAFICO: VISTA INTERIOR C/CONTRAF.(3 EVAP.)	X					X	X	X														
11E	TOPOGRAFICO: VISTA INTERIOR C/CONTRAF.(3 EVAP.) (E)	X					X	X	X														
13	TOPOGRAFICO: VISTA INTERIOR C/CONTRAF.(2 EVAP.)	X					X	X	X														
12E	TOPOGRAFICO: VISTA INTERIOR C/CONTRAF.(2 EVAP.) (E)	X					X	X	X														
14	TOPOGRAFICO: VISTA INTERIOR C/CONTRAF.(1 EVAP.)	X					X	X	X														
13E	TOPOGRAFICO: VISTA INTERIOR C/CONTRAF.(1 EVAP.) (E)	X					X	X	X														
15	DETALLE DE CARTELES ACRILICOS	X					X	X	X														
14E	DETALLE DE CARTELES ACRILICOS (E)	X					X	X	X														
16	DETALLE DE BORNERA (3 EVAP.)	X					X	X	X														
15E	DETALLE DE BORNERA (3 EVAP.) (E)	X					X	X	X														
17	DETALLE DE BORNERA (2 EVAP.)	X					X	X	X														
16E	DETALLE DE BORNERA (2 EVAP.) (E)	X					X	X	X														
18	DETALLE DE BORNERA (1 EVAP.)	X					X	X	X														
17E	DETALLE DE BORNERA (1 EVAP.) (E)	X					X	X	X														
NOTAS: LA LETRA "E" IDENTIFICA LAS HOJAS CORRESPONDIENTE A LA INGENIERIA SIN CORTE EN NEUTRO. EN CASO DE SOLICITAR UN TABLERO CON ESA CONDICION DE FABRICACION SON ESTAS MISMAS HOJAS CON LA QUE SE DEBERA ARMAR EL DOCUMENTO EN FORMATO NO EDITABLE. EN CASO DE SOLICITAR LA FABRICACION "SIN CONFRENTE" DEBERA OMITIRSE LA IMPRESION DE LAS HOJAS 13E, 14E, 15E Y 16. LA HOJA 16 APLICA TANTO PARA LA INGENIERIA CON CORTE EN NEUTRO O SIN CORTE EN NEUTRO.																							
PROYECTO: L.PERNA		16/04/24		TABLERO DE CAMARAS DIAGRAMA DE CONEXIONADO DISTRIBUCION DE ALIMENTACION Y CONTROLADOR								 Juan Pablo II 8050 Tel: +54(0) 341 410 6100 S2011PWA - Rosario Fax: +54(0) 341 410 6100				ARNEG				PAGINA: 02/02E			
DIBUJO: L.PERNA		16/04/24														TAB 1CMSD 1CF xxx CB xMR0				CONTINUA: 03/03E			
APROBO: N.DYKE		22/04/24														— — — — —				REVISION: 2			
																ARCHIVO: REF-ARNEG-E-EU-XXXXXXXX-2-0195XXX							

D			C		B		A	
MEDIDAS DEL TABLERO			BORNE DE ENTRADA XP: R,S,T,N,Pe		CAPACIDAD DE LA TERMOMAGNETICA "TMGP"			
1M	2M	3M		R0		R0		
VER HOJA: 8,11,14,18	VER HOJA: 8,10,13,17	VER HOJA: 8,9,12,16	1M	4mm2	1M	16A		
450X600X210	600X600X210	600X600X210	2M	4mm2	2M	16A		
			3M	6mm2	3M	20A		
SECCION DE CABLE ASOCIADOS A "TMGP"								
	R0							
1M	2,5mm2							
2M	2,5mm2							
3M	4mm2							

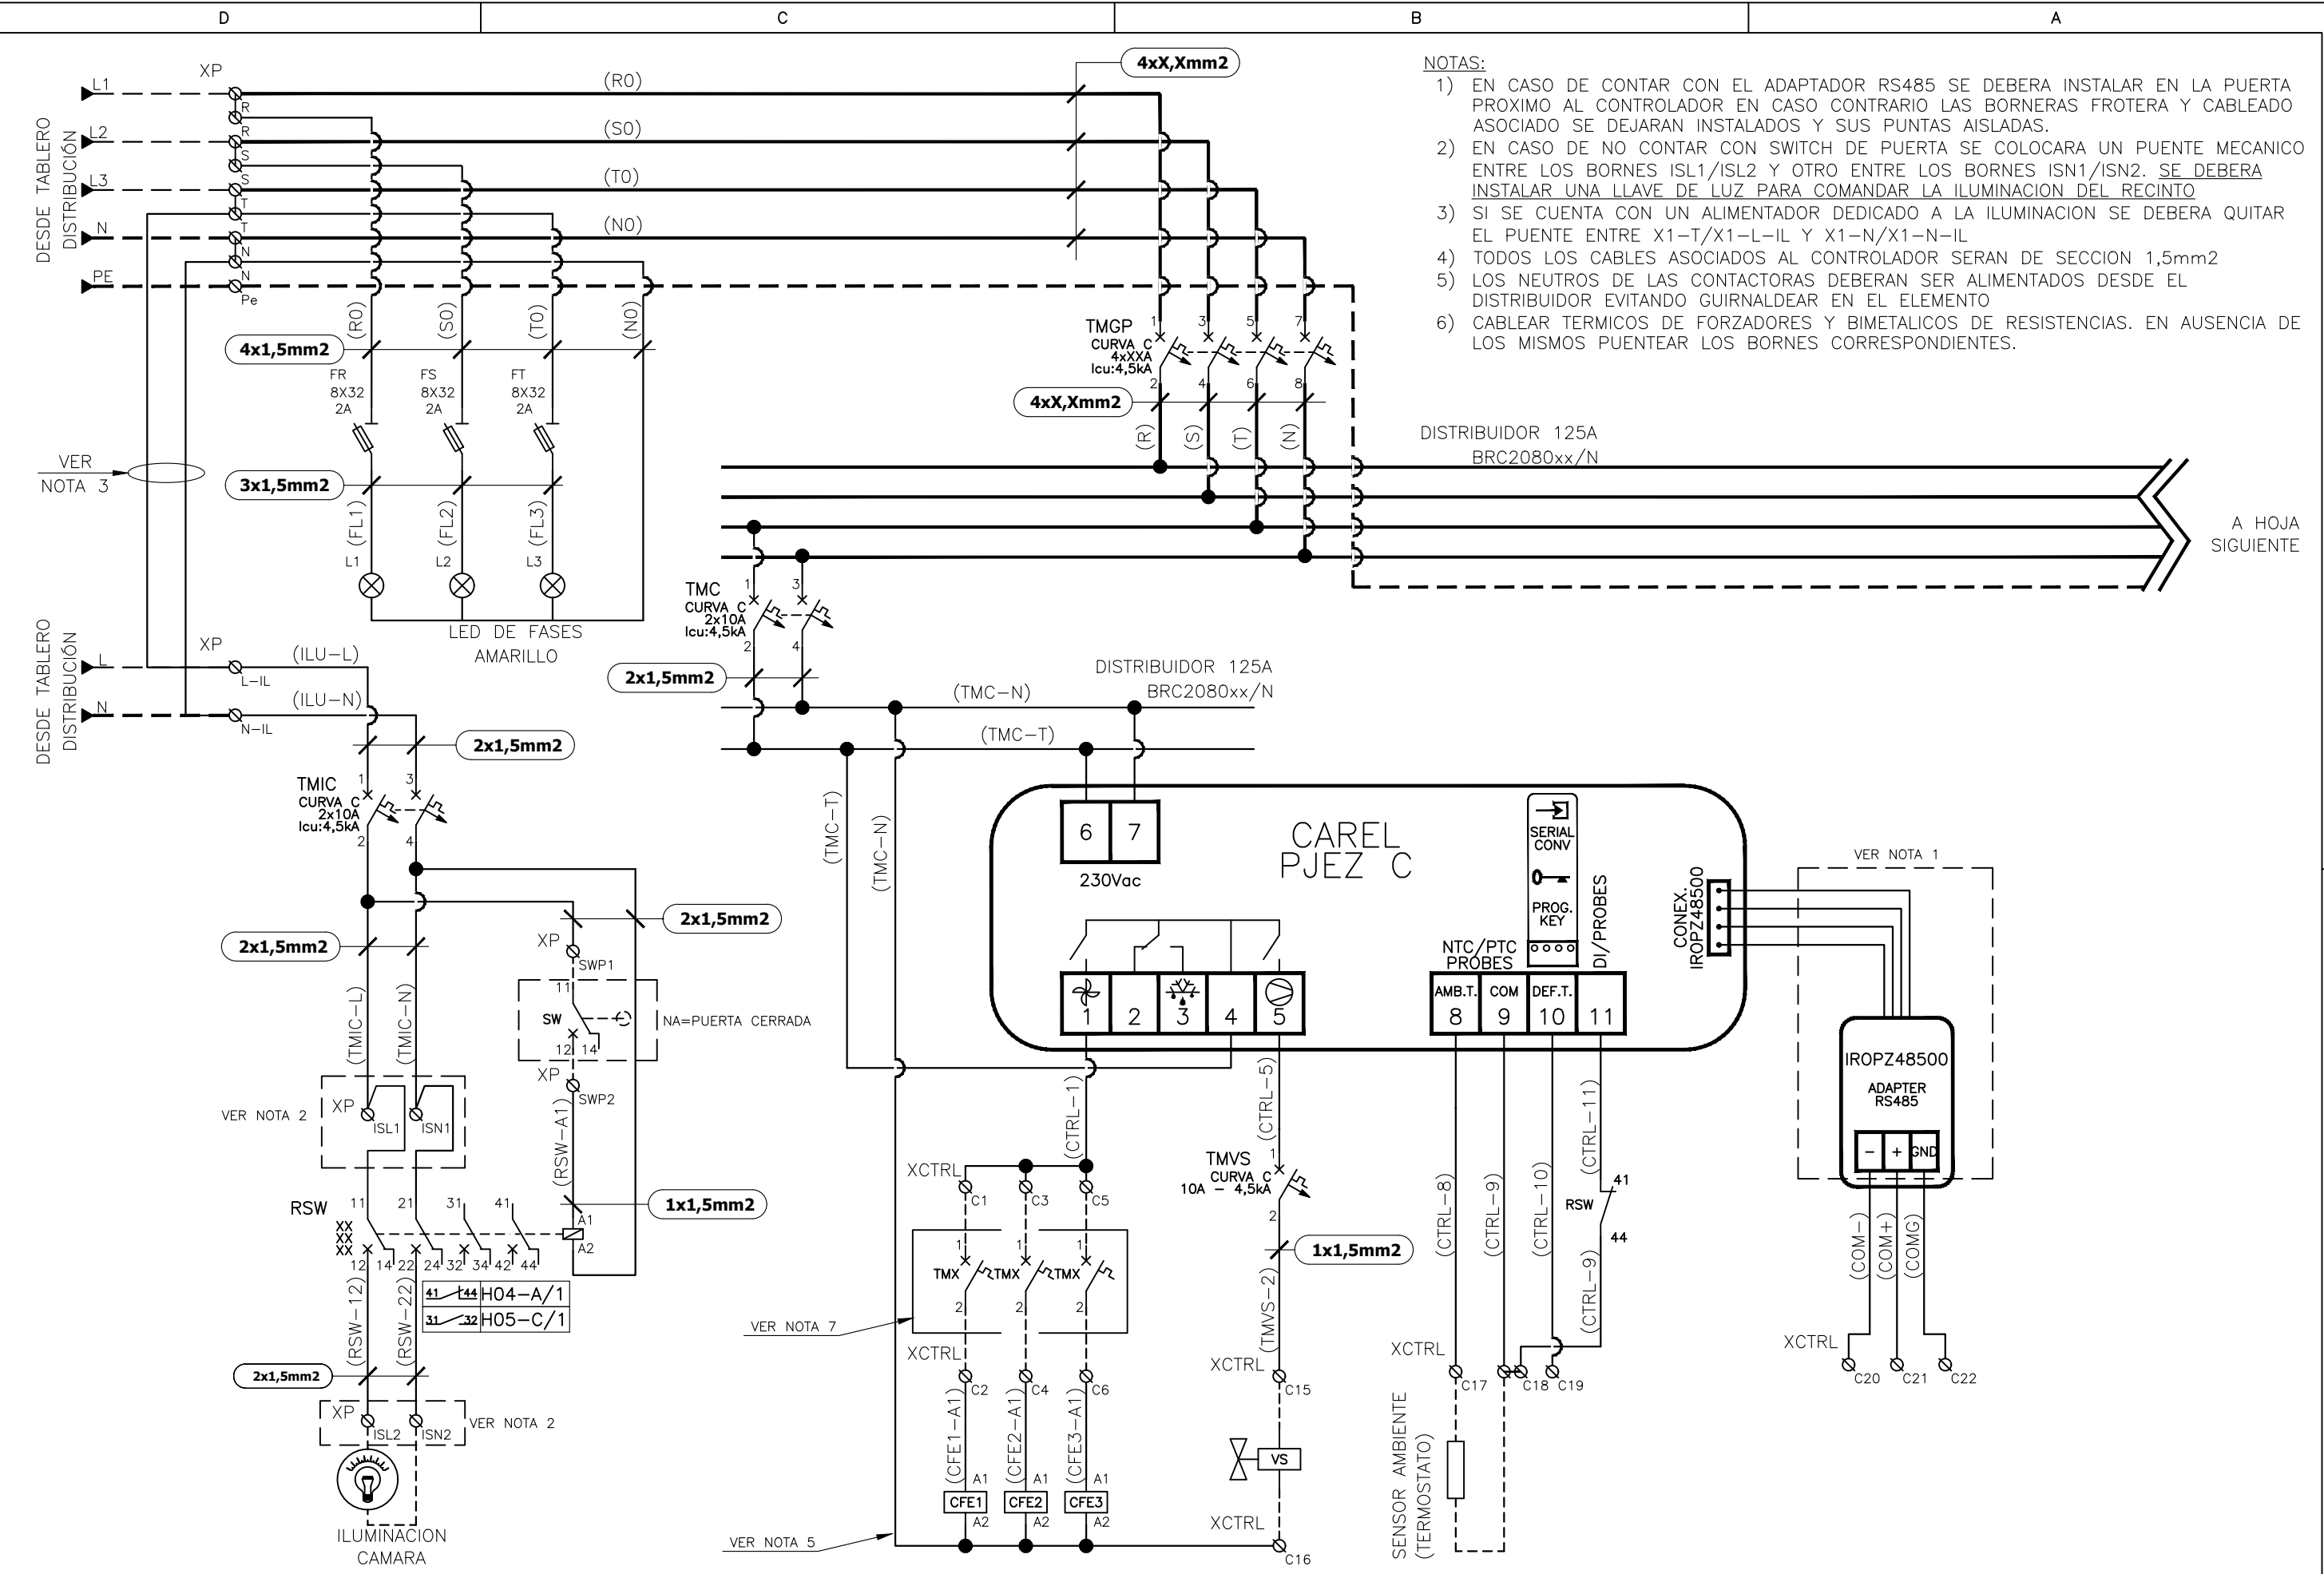


PROYECTO: L.PERNA	16/04/24
DIBUJO: L.PERNA	16/04/24
APROBO: N.DYKE	22/04/24

TABLERO DE CAMARAS
DIAGRAMA DE CONEXIONADO
DISTRIBUCION DE ALIMENTACION Y CONTROLADOR

arneg
Juan Pablo II 8050 Tel: +54(0) 341 410 6100
S2011PWA - Rosario Fax: +54(0) 341 410 6100

ARNEG TAB 1CMSD 1CF xxx CB xMR0	PAGINA: 04
	CONTINUA: 05
	REVISION: 2
ARCHIVO: REF-ARNEG-E-EU-XXXXXXX-2-0195XXX	

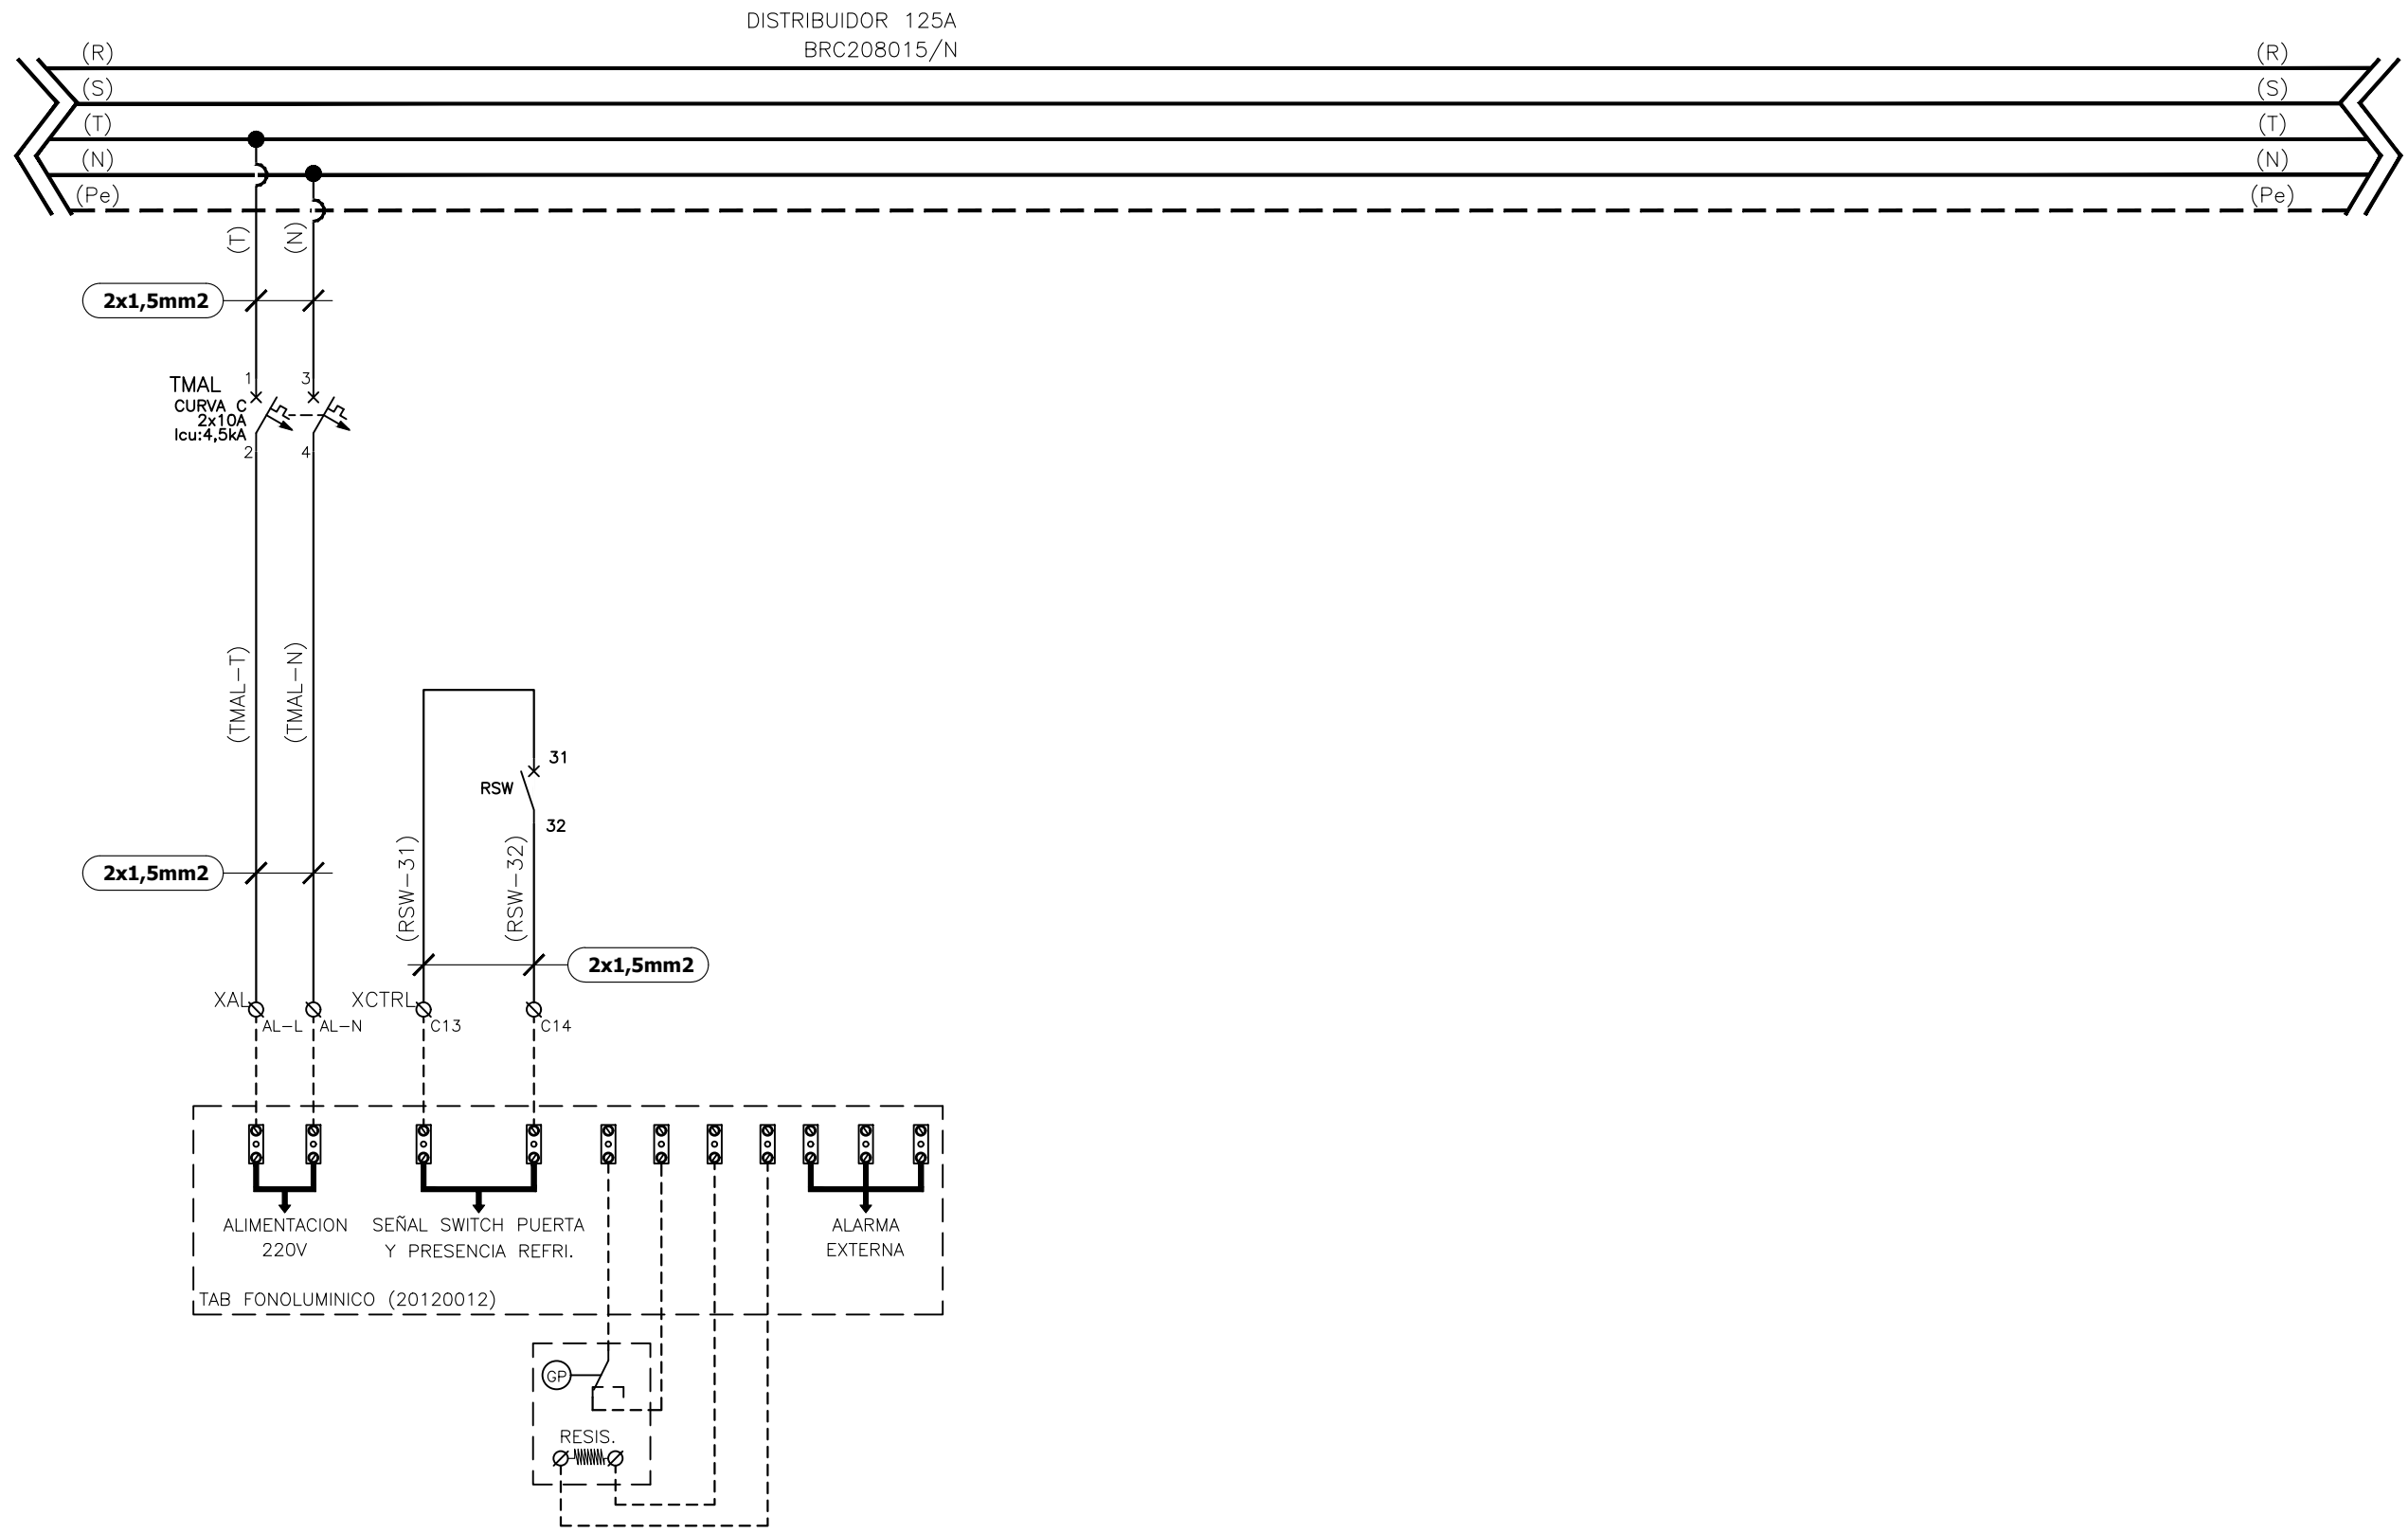

PROYECTO: L.PERNA	16/04/24
DIBUJO: L.PERNA	16/04/24
APROBO: N.DYKE	22/04/24


TABLERO DE CAMARAS
DIAGRAMA DE CONEXIONADO
DISTRIBUCION DE ALIMENTACION CIRCUITOS AUXILIARES



Juan Pablo II 8050 Tel: +54(0) 341 410 6100
S2011PWA - Rosario Fax: +54(0) 341 410 6100

ARNEG
TAB 1CMSD 1CF xxx CB xMRO
ARCHIVO: REF-ARNEG-E-EU-XXXXXXX-2-0195XXX

PAGINA: 05
CONTINUA: 06
REVISION: 2

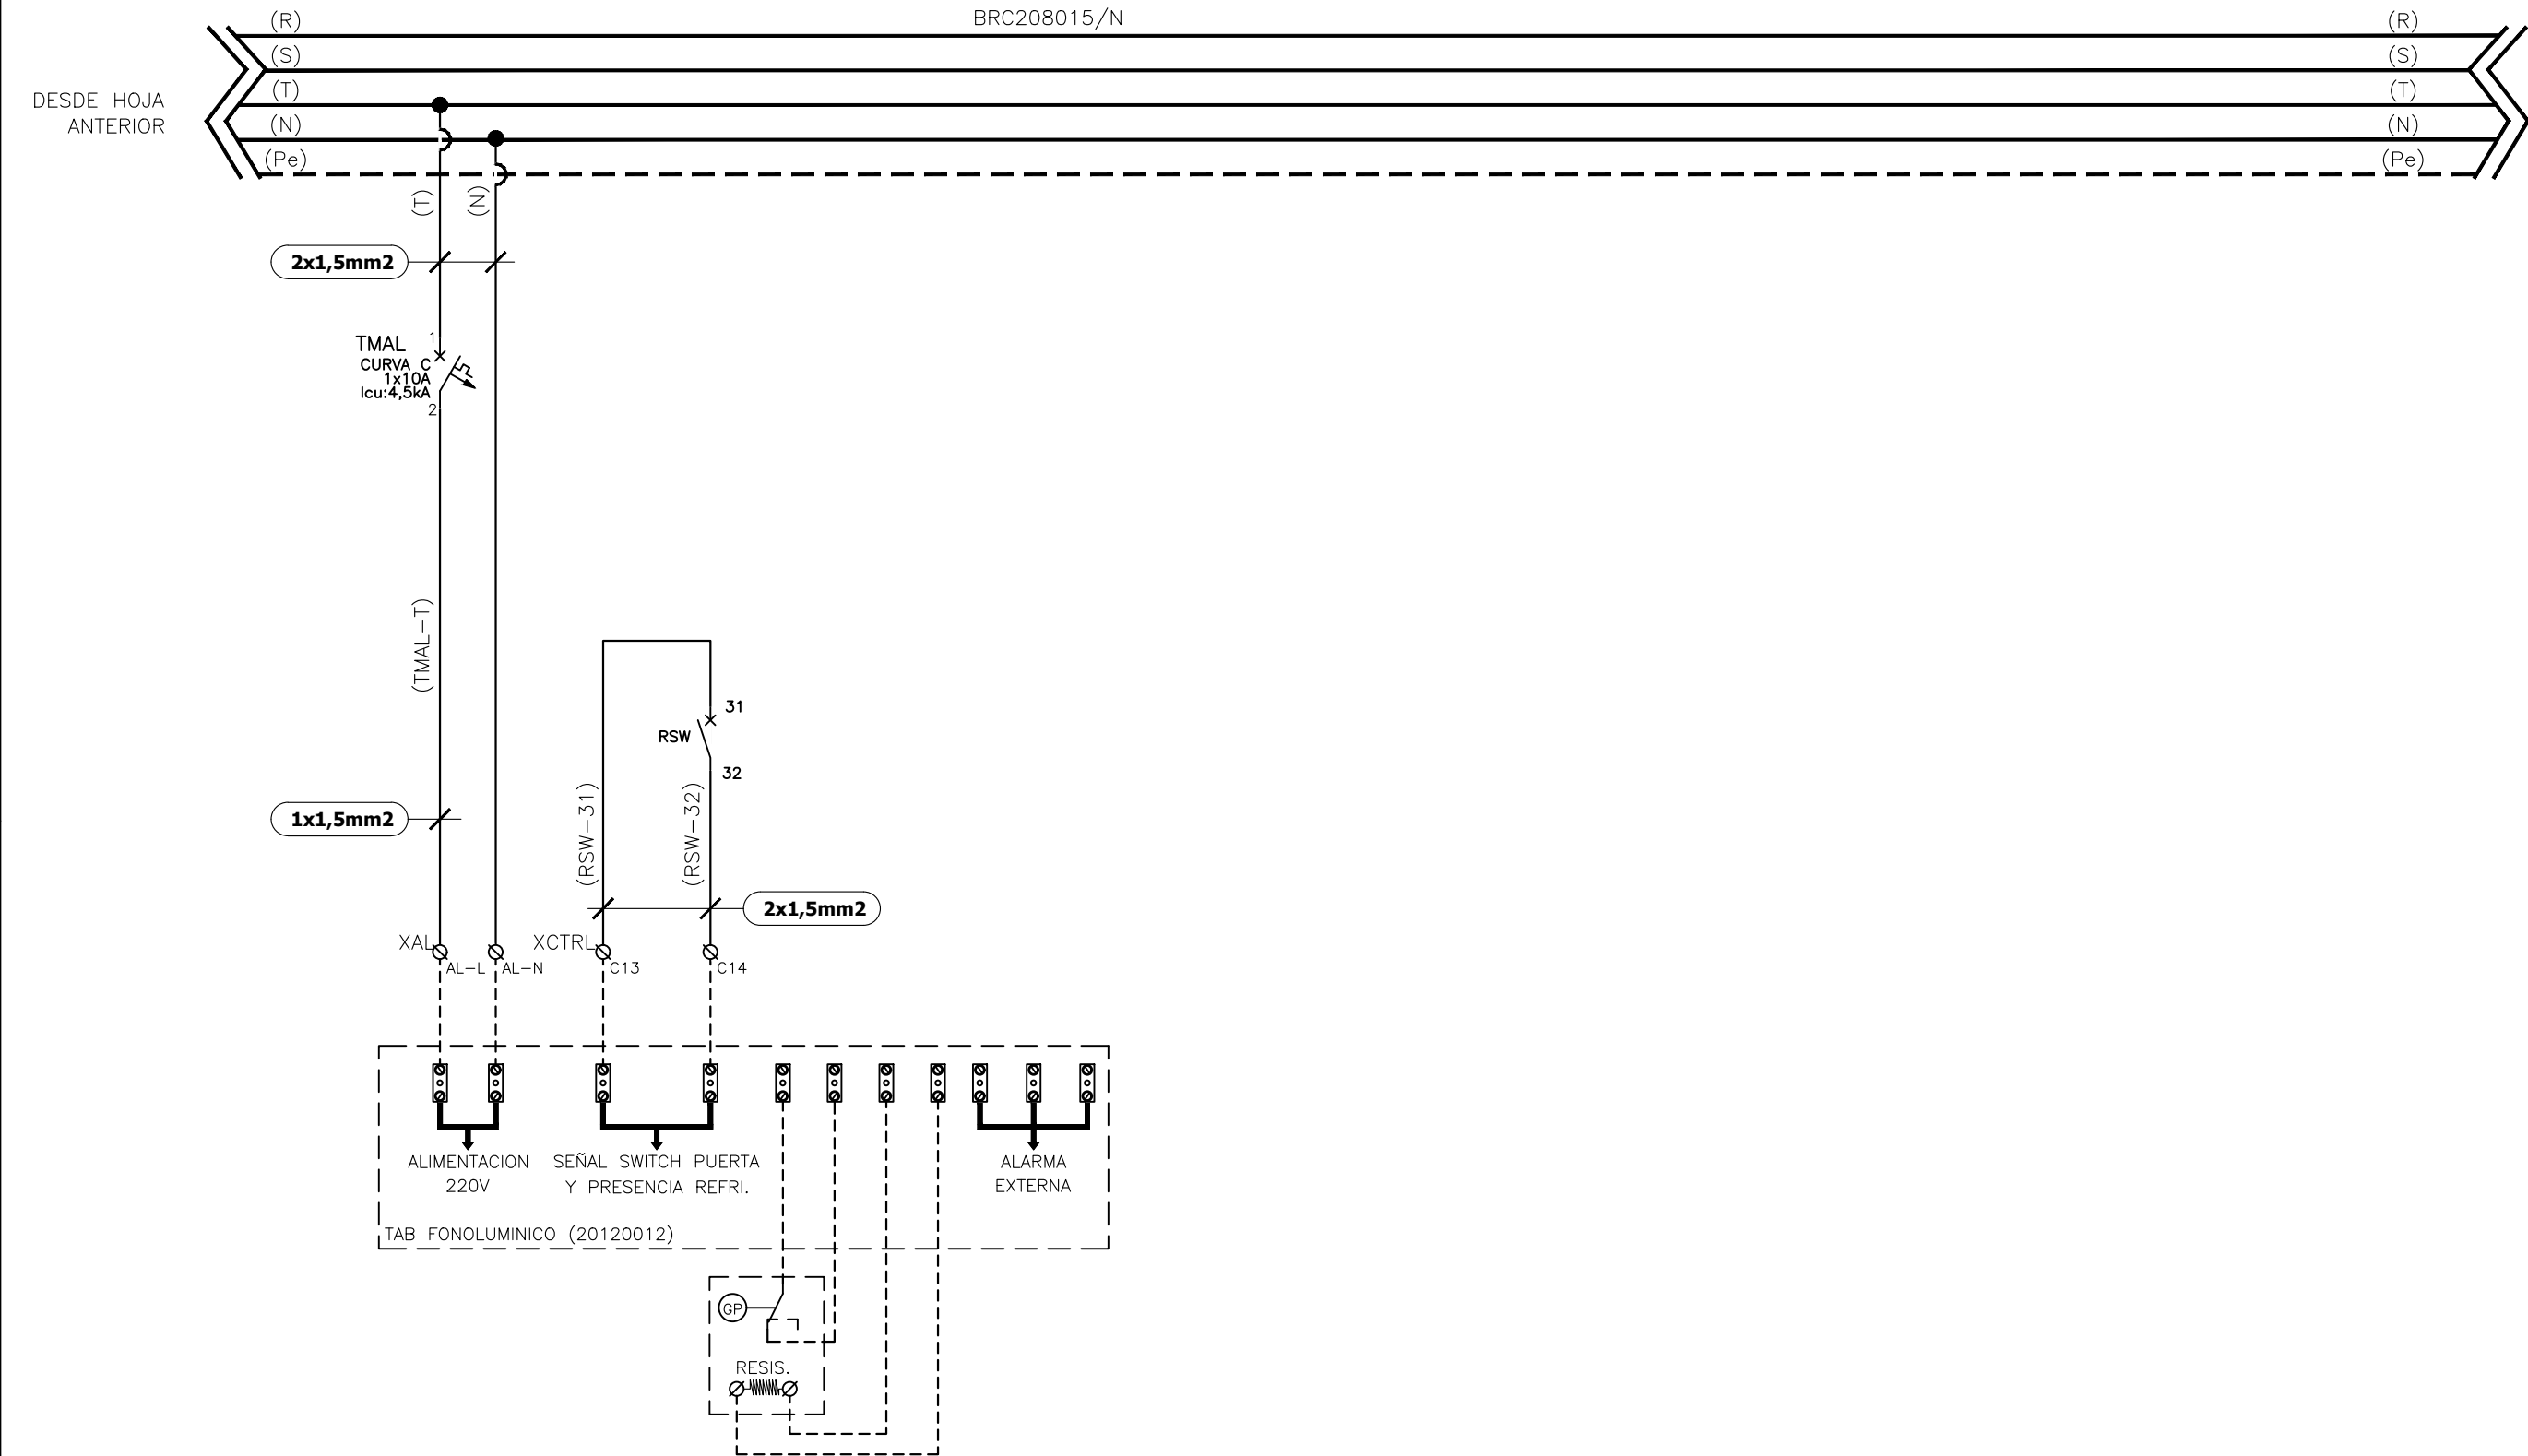


PROYECTO: L.PERNA	16/04/24
DIBUJO: L.PERNA	16/04/24
APROBO: N.DYKE	22/04/24

TABLERO DE CAMARAS
DIAGRAMA DE CONEXIONADO
DISTRIBUCION DE ALIMENTACION CIRCUITOS AUXILIARES

arneg

Juan Pablo II 8050 Tel: +54(0) 341 410 6100
S2011PWA - Rosario Fax: +54(0) 341 410 6100

ARNEG TAB 1CMSD 1CF xxx CB xMR0 - - - - -	PAGINA: 05E
	CONTINUA: 06E
	REVISION: 2
ARCHIVO: REF-ARNEG-E-EU-XXXXXXX-2-0195XXX	

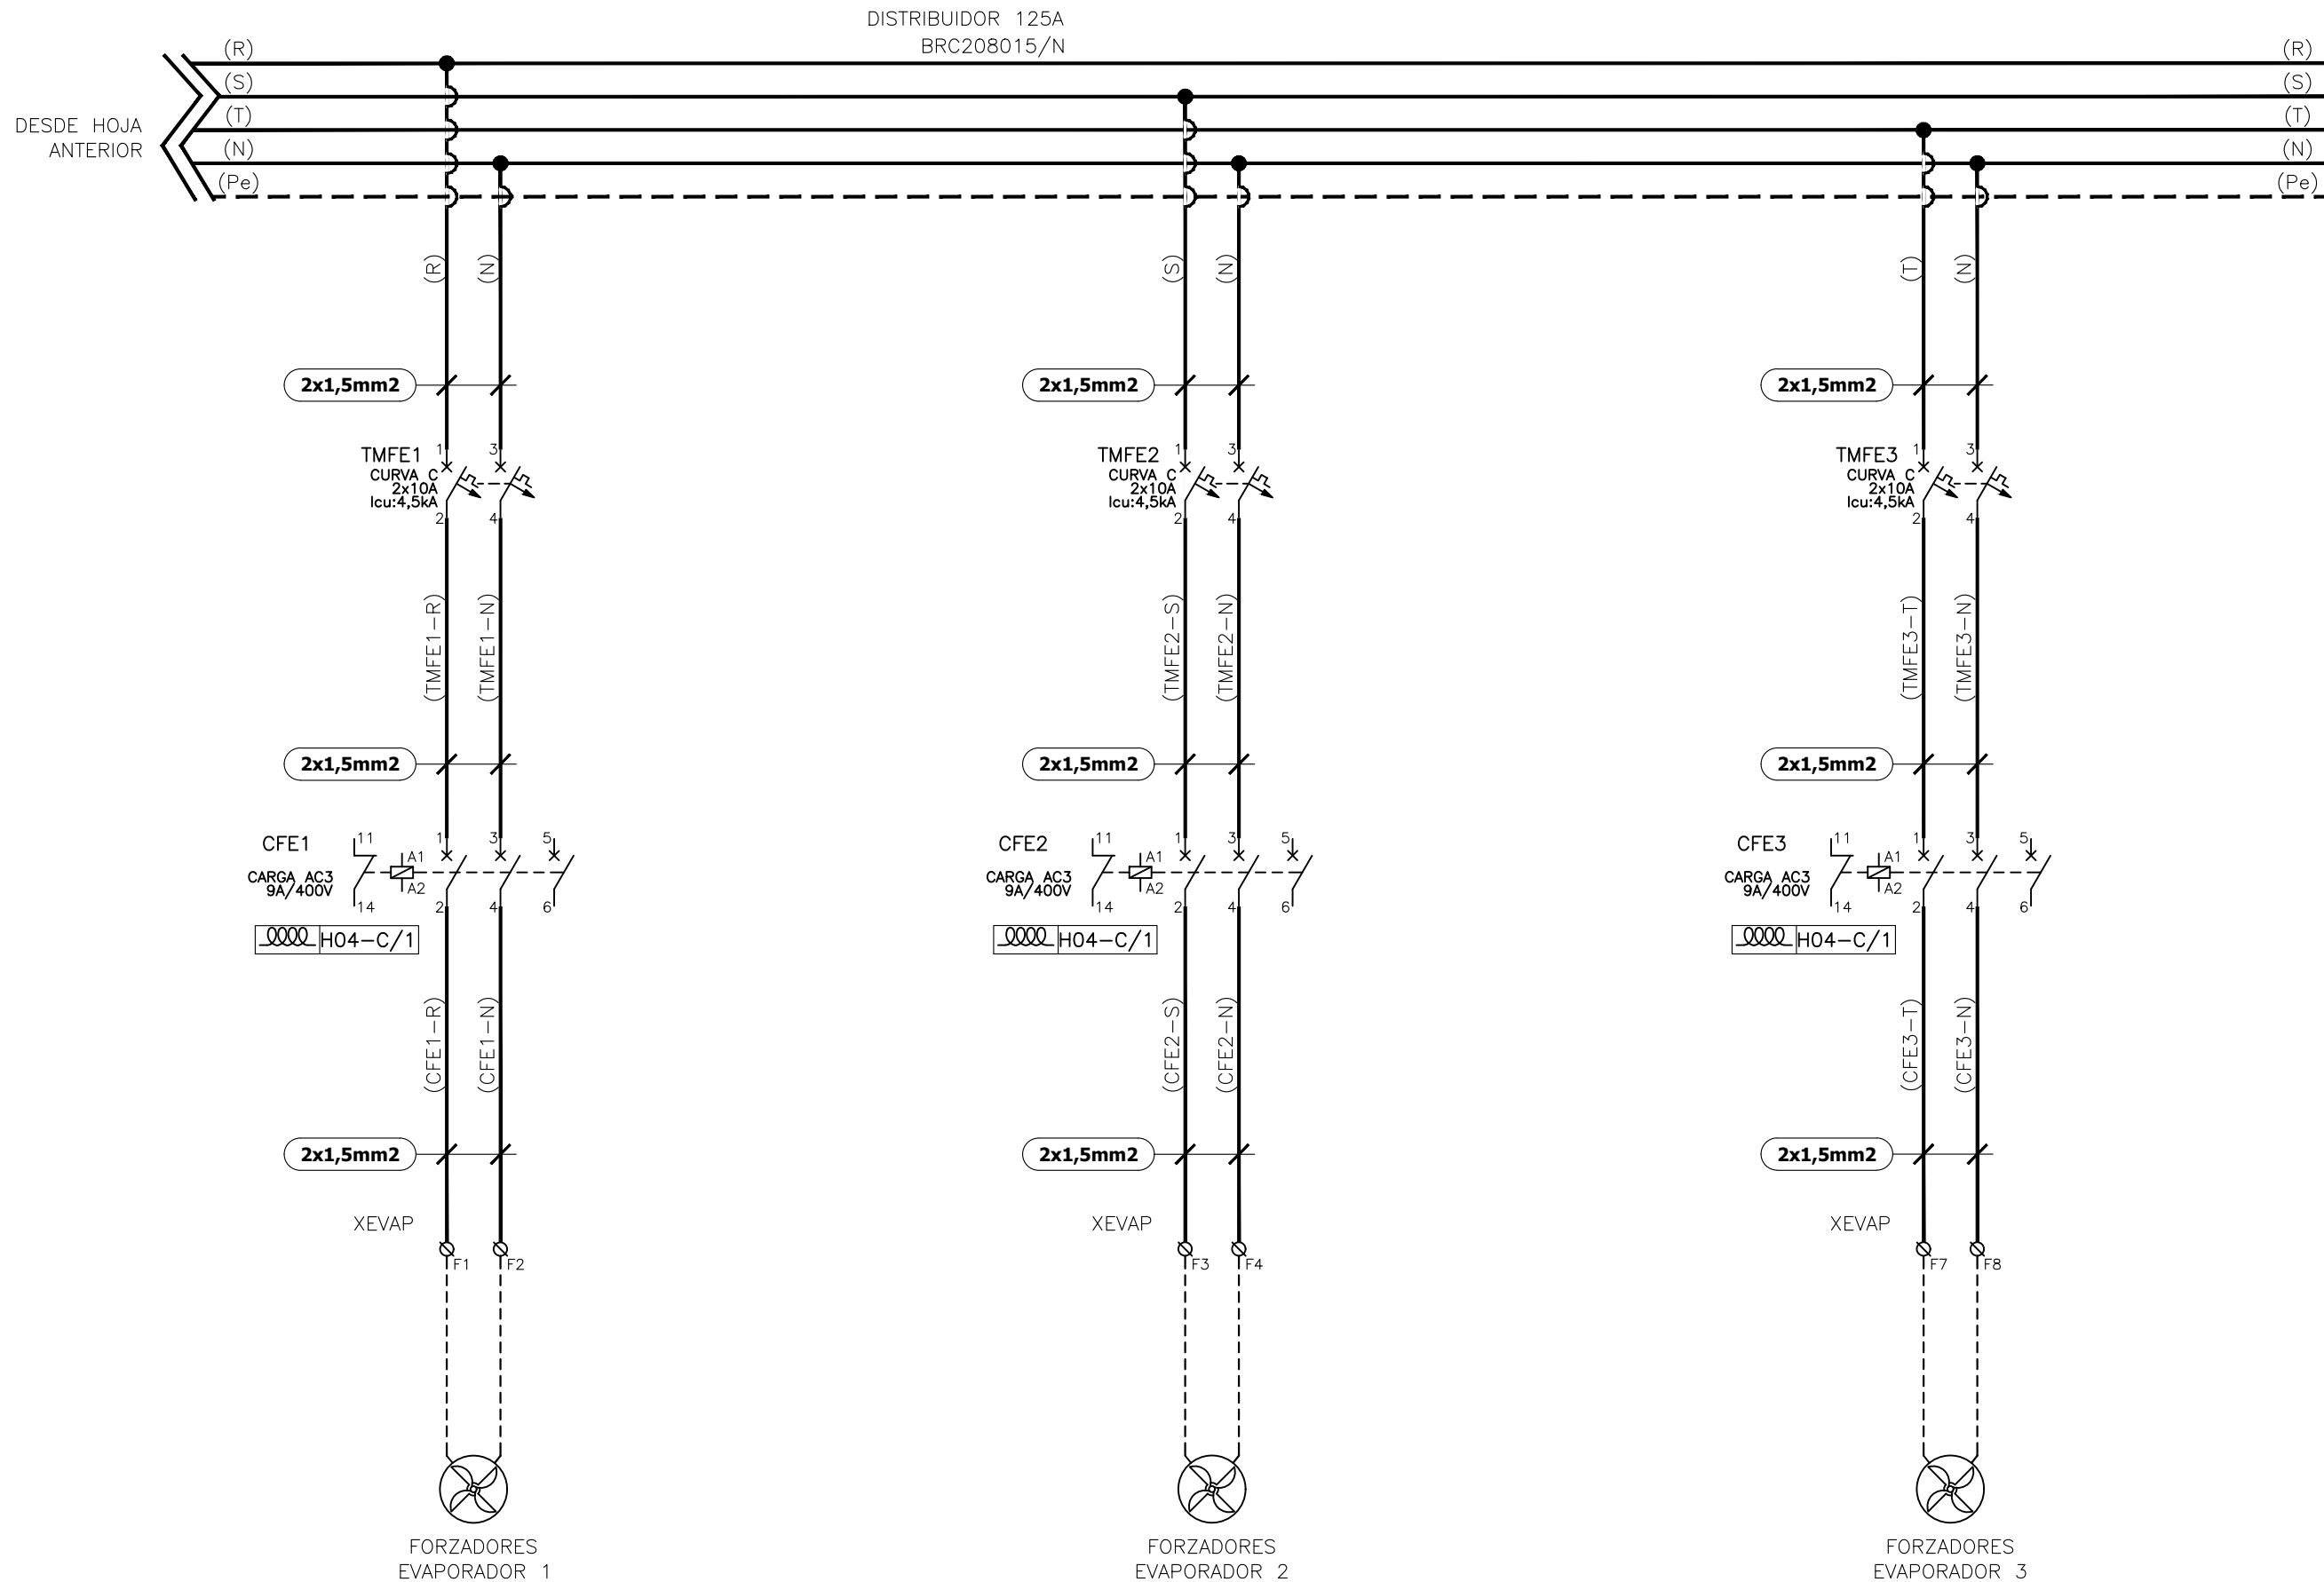

PROYECTO: L.PERNA	16/04/24
DIBUJO: L.PERNA	16/04/24
APROBO: N.DYKE	22/04/24


TABLERO DE CAMARAS
DIAGRAMA DE CONEXIONADO
CONEXIONADO DE FORZADORES

arneg

Juan Pablo II 8050
S2011PWA - Rosario

Tel: +54(0) 341 410 6100
Fax: +54(0) 341 410 6100

ARNEG	PAGINA: 06
TAB 1CMSD 1CF xxx CB xMR0	CONTINUA: 07
ARCHIVO: REF-ARNEG-E-EU-XXXXXXX-2-0195XXX	REVISION: 2

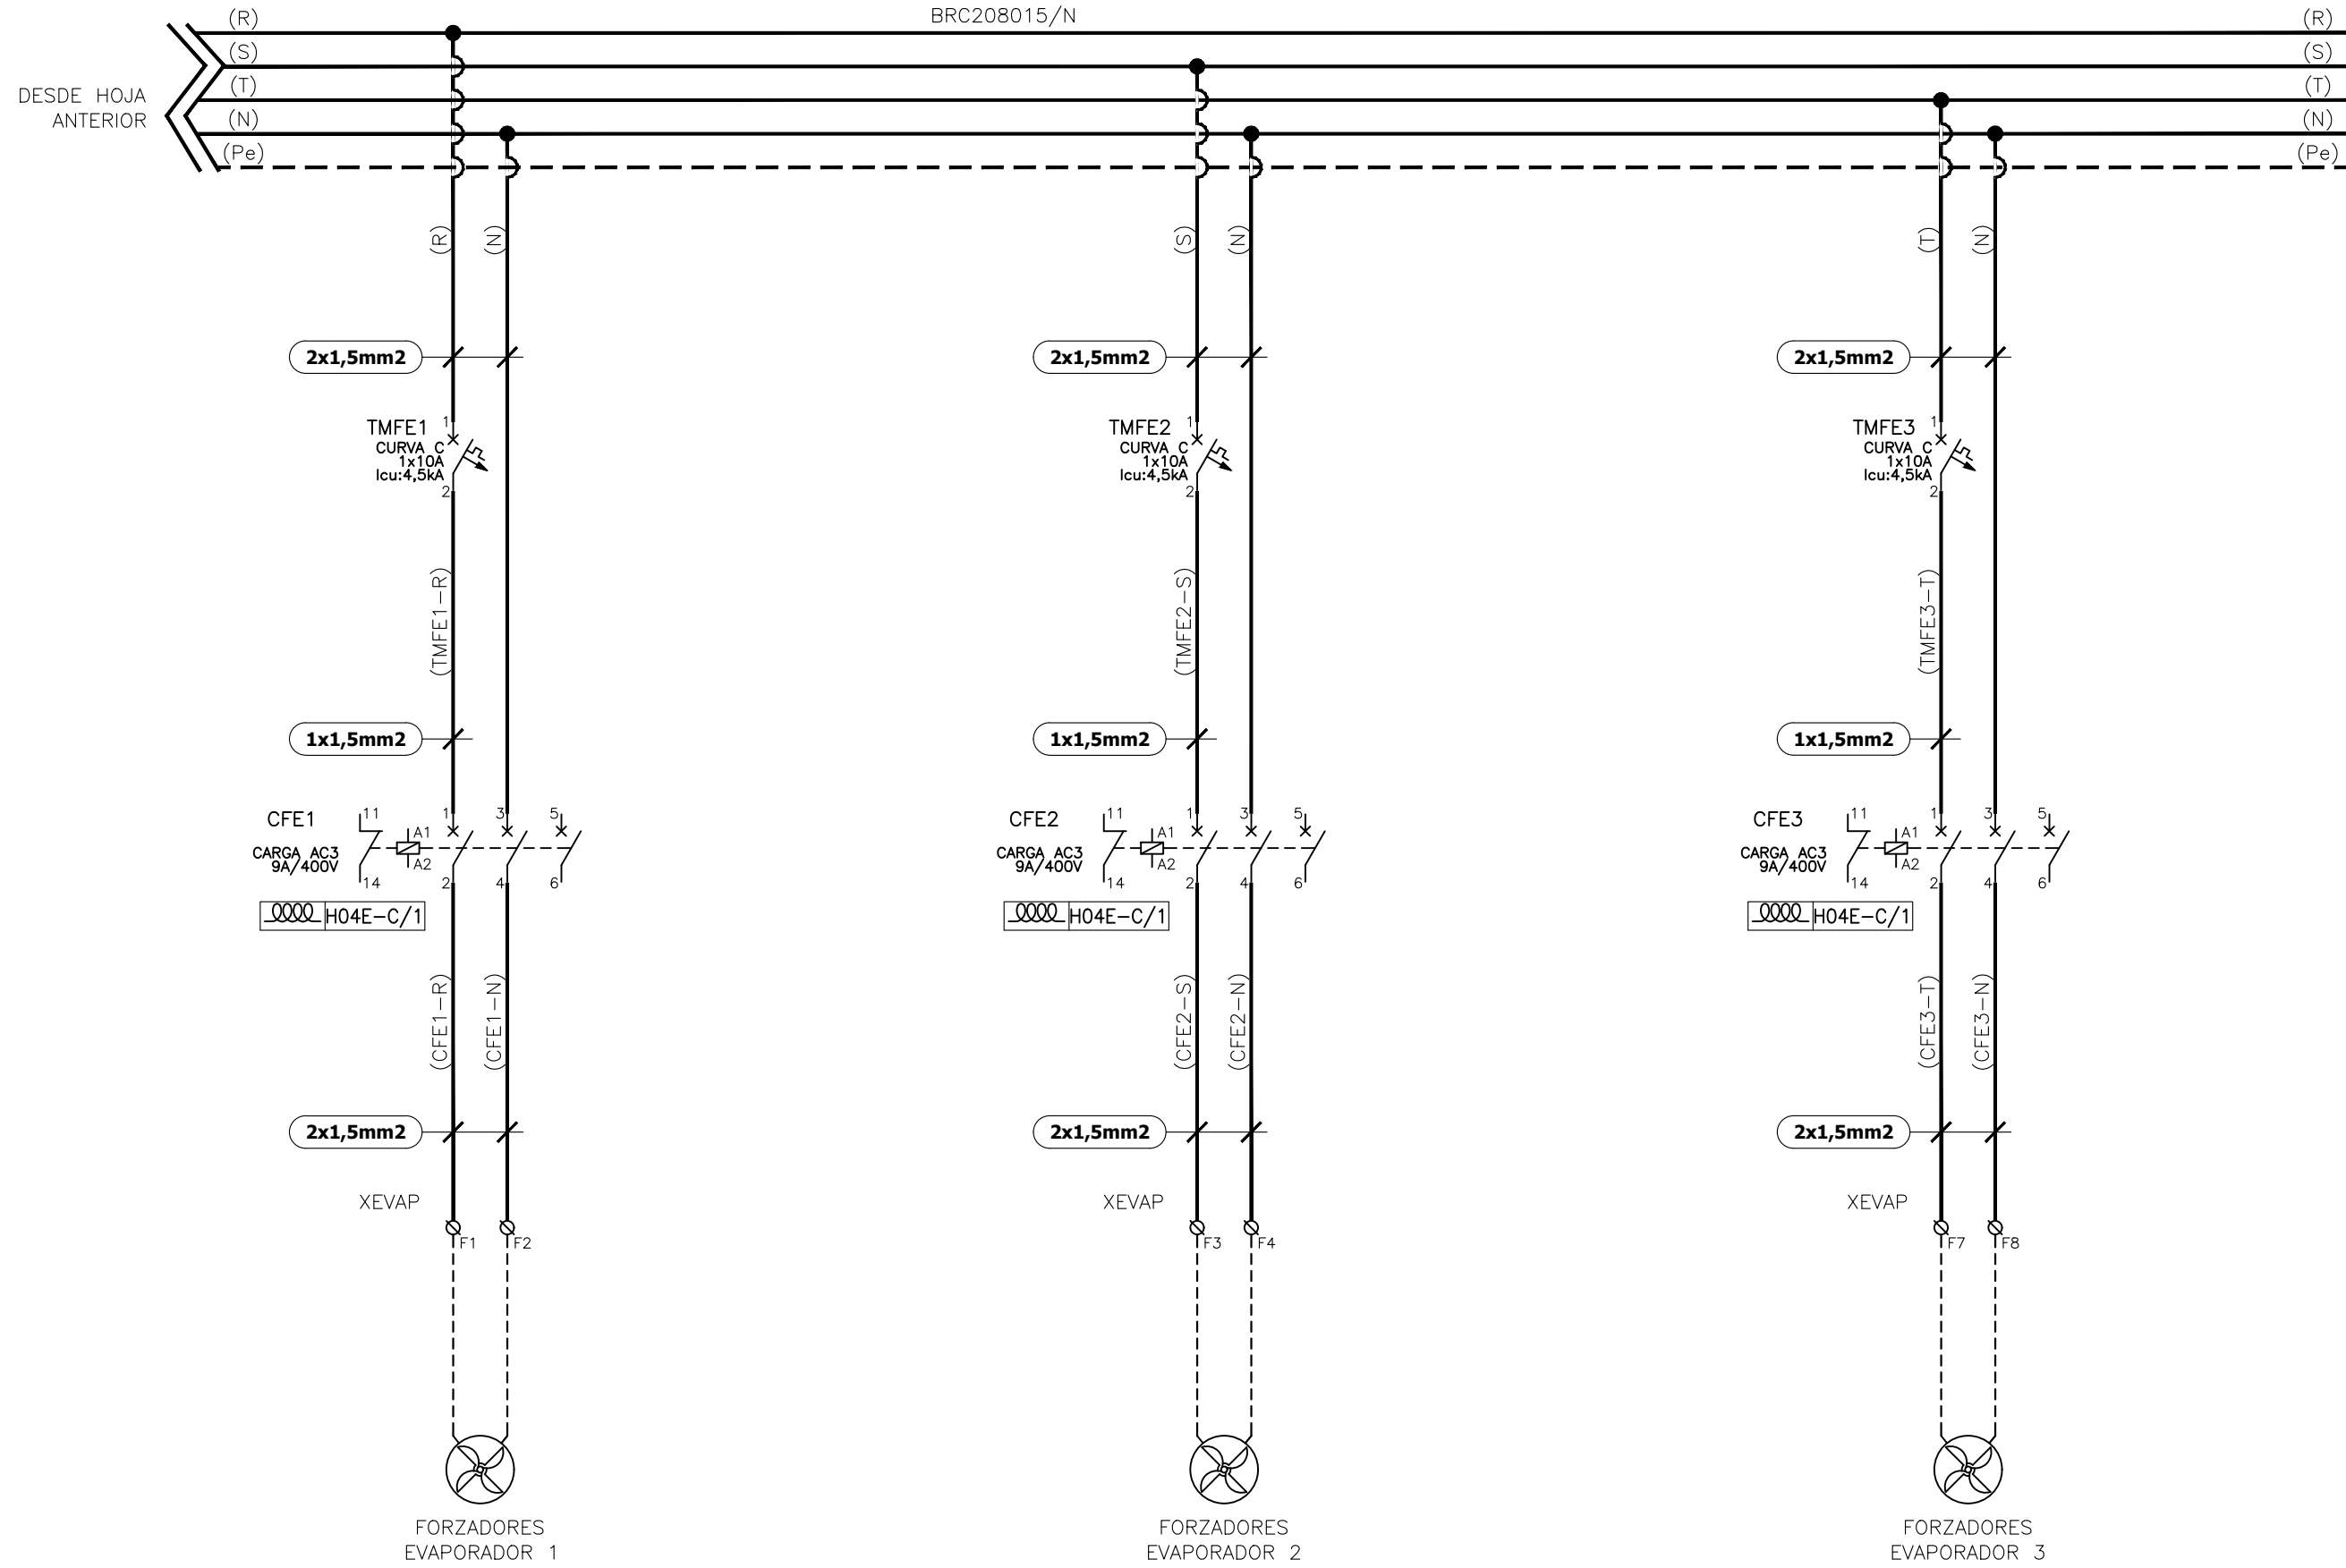

PROYECTO: L.PERNA	16/04/24
DIBUJO: L.PERNA	16/04/24
APROBO: N.DYKE	22/04/24

TABLERO DE CAMARAS
DIAGRAMA DE CONEXIONADO
CONEXIONADO DE FORZADORES




Juan Pablo II 8050
S2011PWA - Rosario

Tel: +54(0) 341 410 6100
Fax: +54(0) 341 410 6100

ARNEG TAB 1CMSD 1CF xxx CB xMR0 — — — — —	PAGINA: 06E
	CONTINUA: 07E
	REVISION: 2
ARCHIVO: REF-ARNEG-E-EU-XXXXXXX-2-0195XXX	

A3 IRAM 4 508

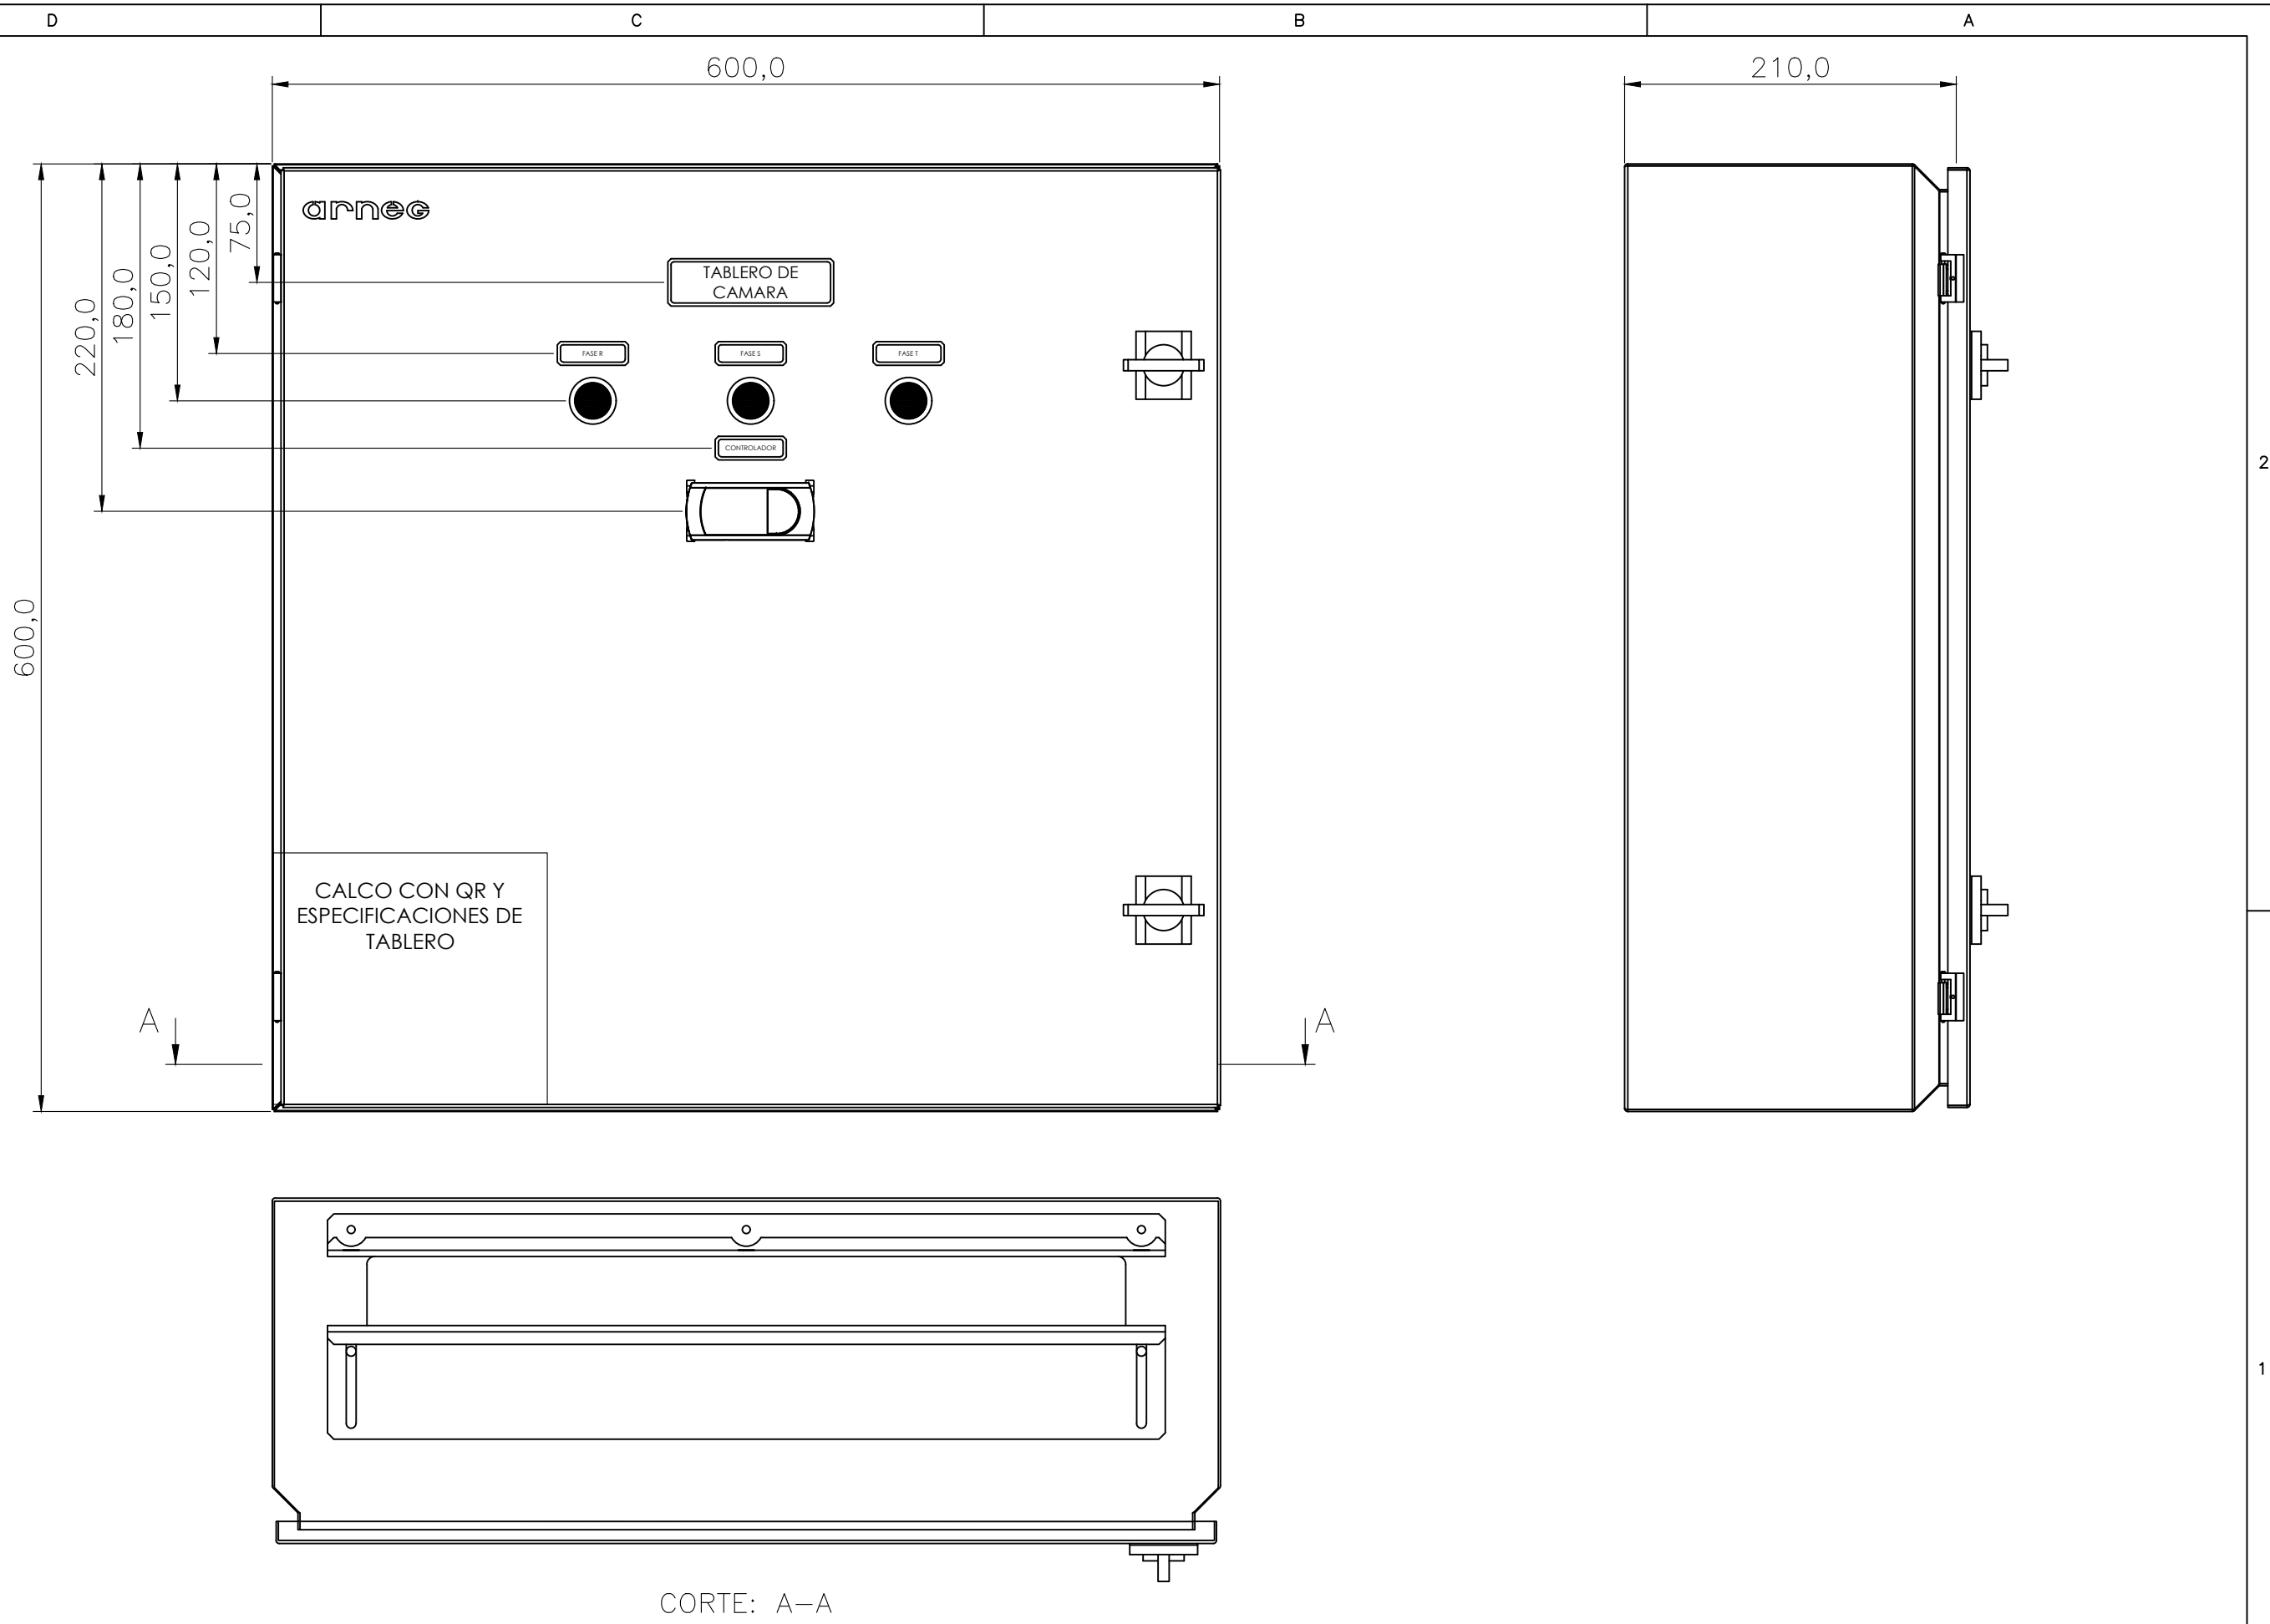


TABLERO DE CAMARAS
TOPOGRAFICO
VISTA EXTERIOR (3 EVAP./ 2EVAP.)

arneg
Juan Pablo II 8050 Tel: +54(0) 341 410 6100
S2011PWA - Rosario Fax: +54(0) 341 410 6100

ARNEG TAB 1CMSD 1CF xxx CB xMR0 - - - - -	PAGINA: 07
	CONTINUA: 08
	REVISION: 2
ARCHIVO: REF-ARNEG-E-EU-XXXXXXX-2-0195XXX	

A3 IRAM 4 508



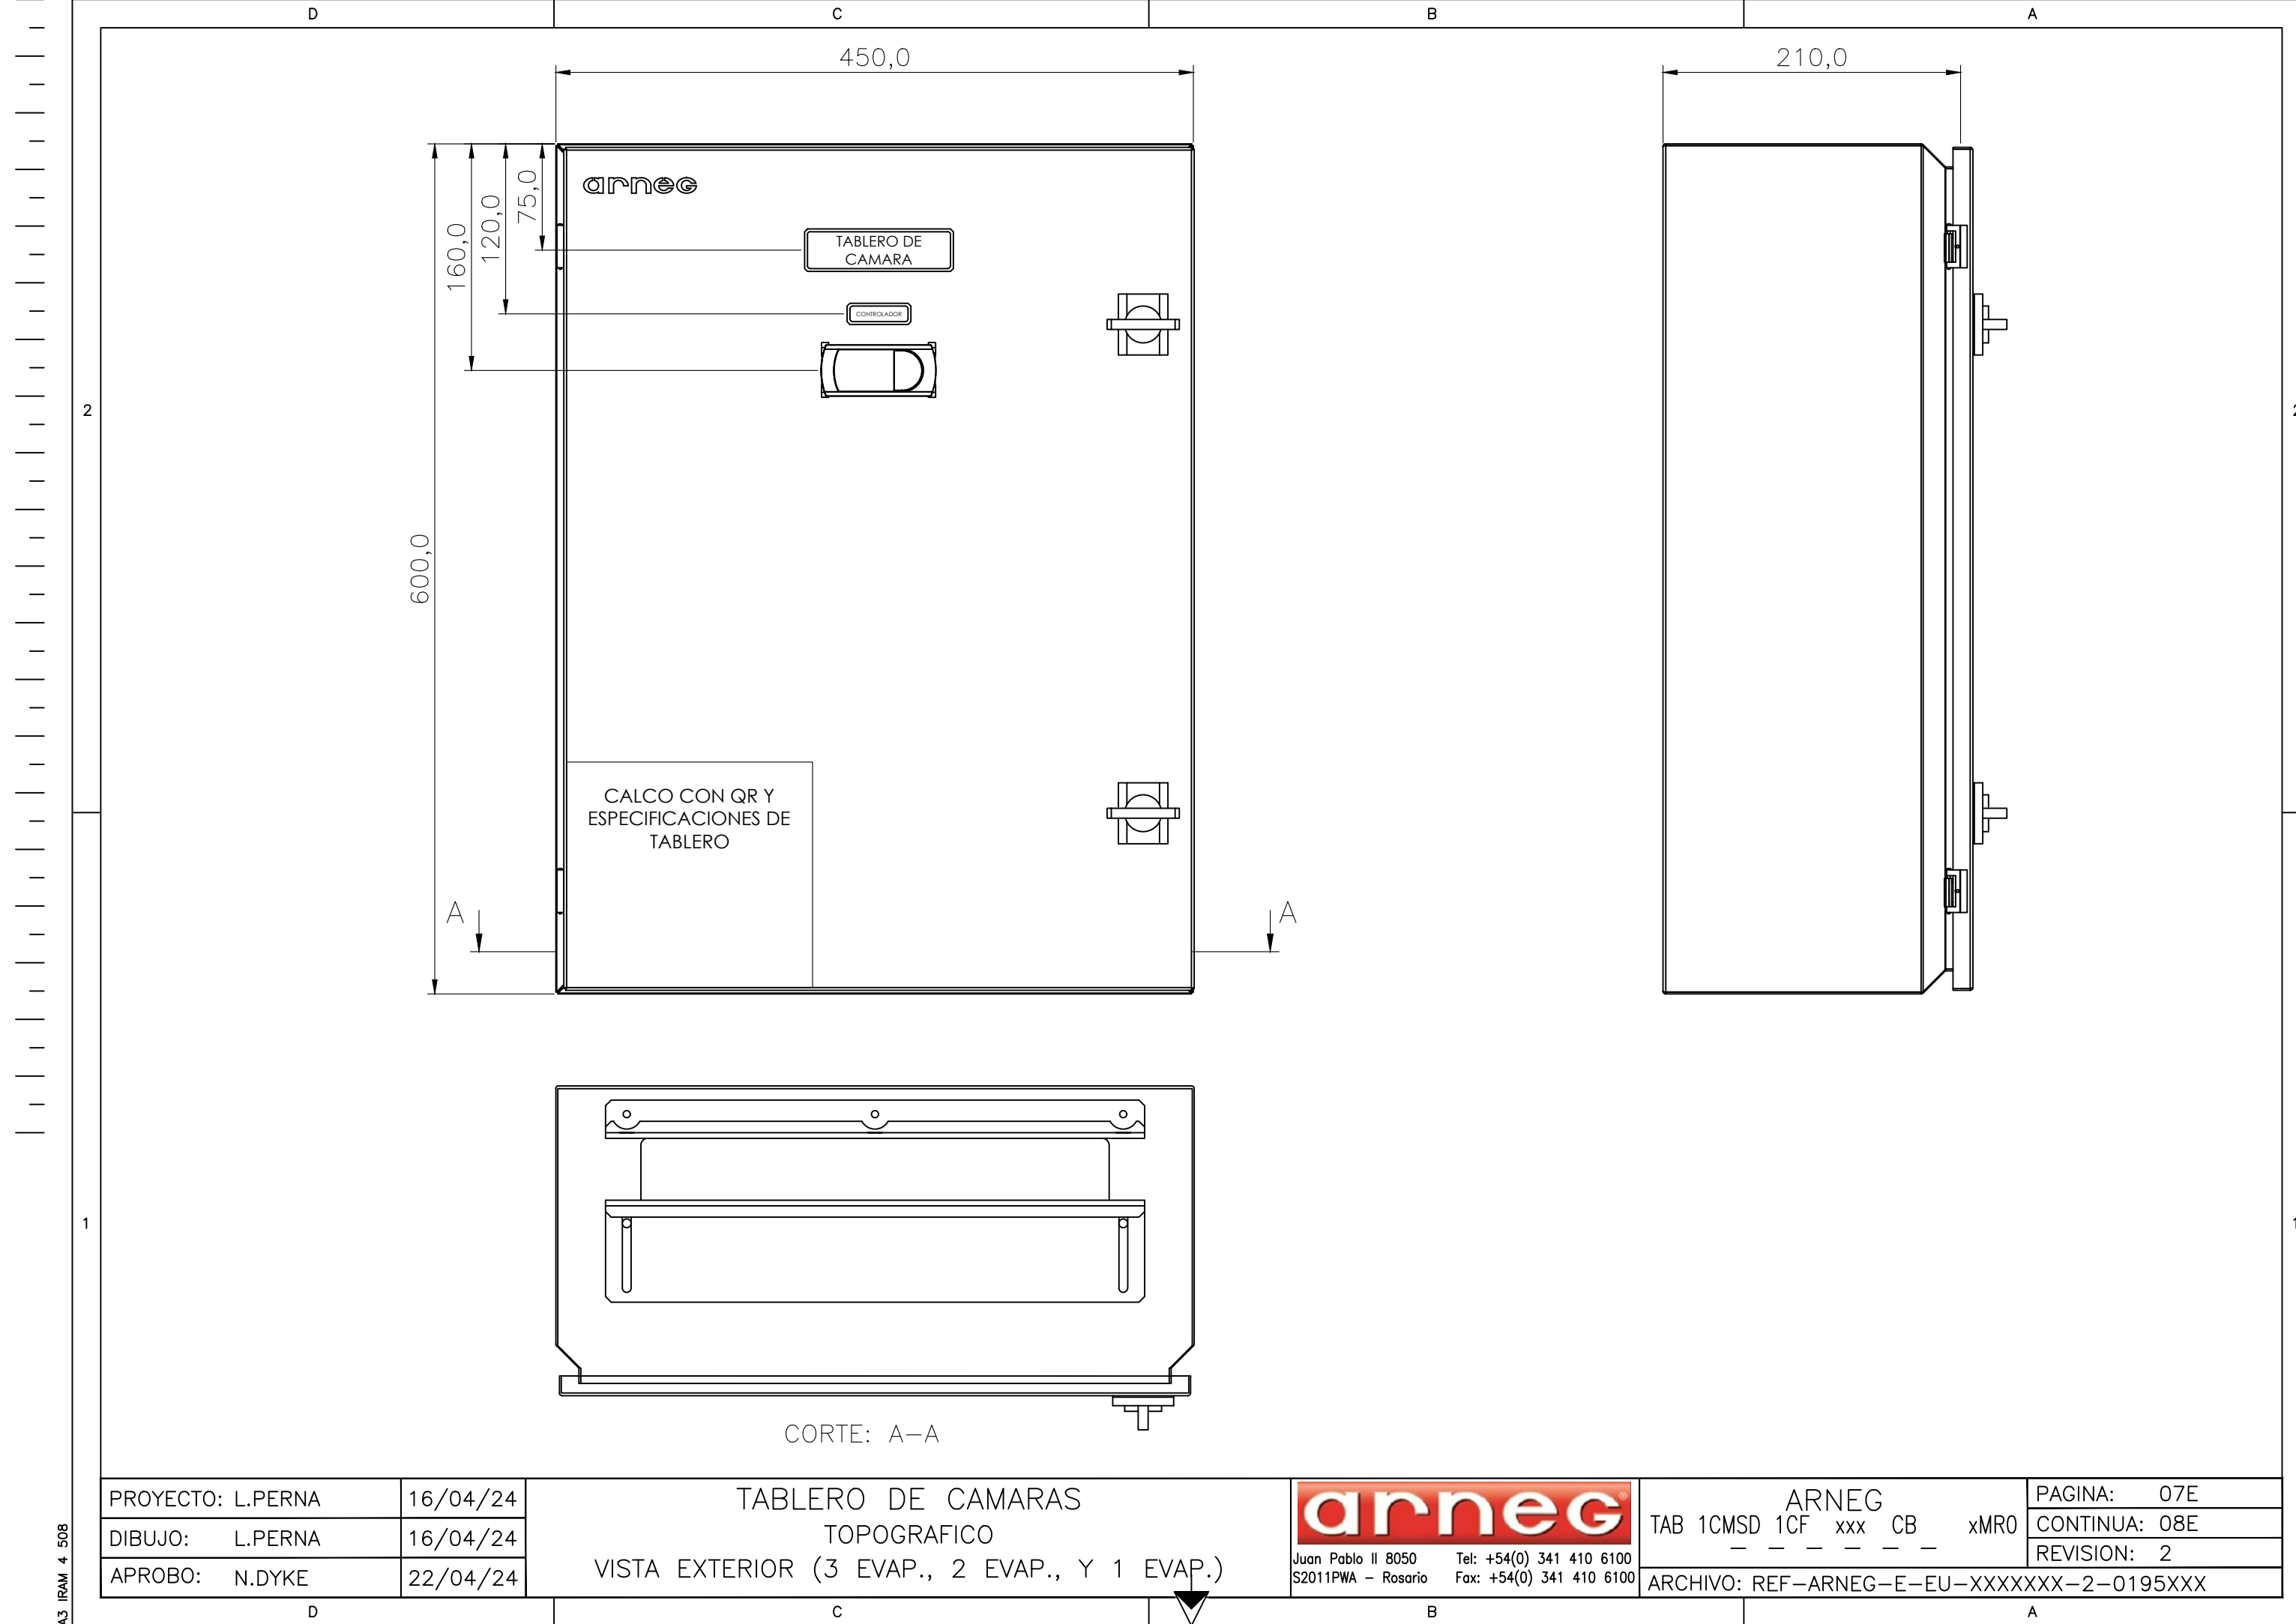

A3 IRAM 4 508

PROYECTO: L.PERNA	16/04/24
DIBUJO: L.PERNA	16/04/24
APROBO: N.DYKE	22/04/24


TABLERO DE CAMARAS
TOPOGRAFICO
VISTA EXTERIOR (3 EVAP., 2 EVAP., Y 1 EVAP.)



Juan Pablo II 8050 Tel: +54(0) 341 410 6100
S2011PWA - Rosario Fax: +54(0) 341 410 6100

ARNEG
TAB 1CMSD 1CF xxx CB xMR0
- - - - -
ARCHIVO: REF-ARNEG-E-EU-XXXXXXX-2-0195XXX

PAGINA: 07E
CONTINUA: 08E
REVISION: 2

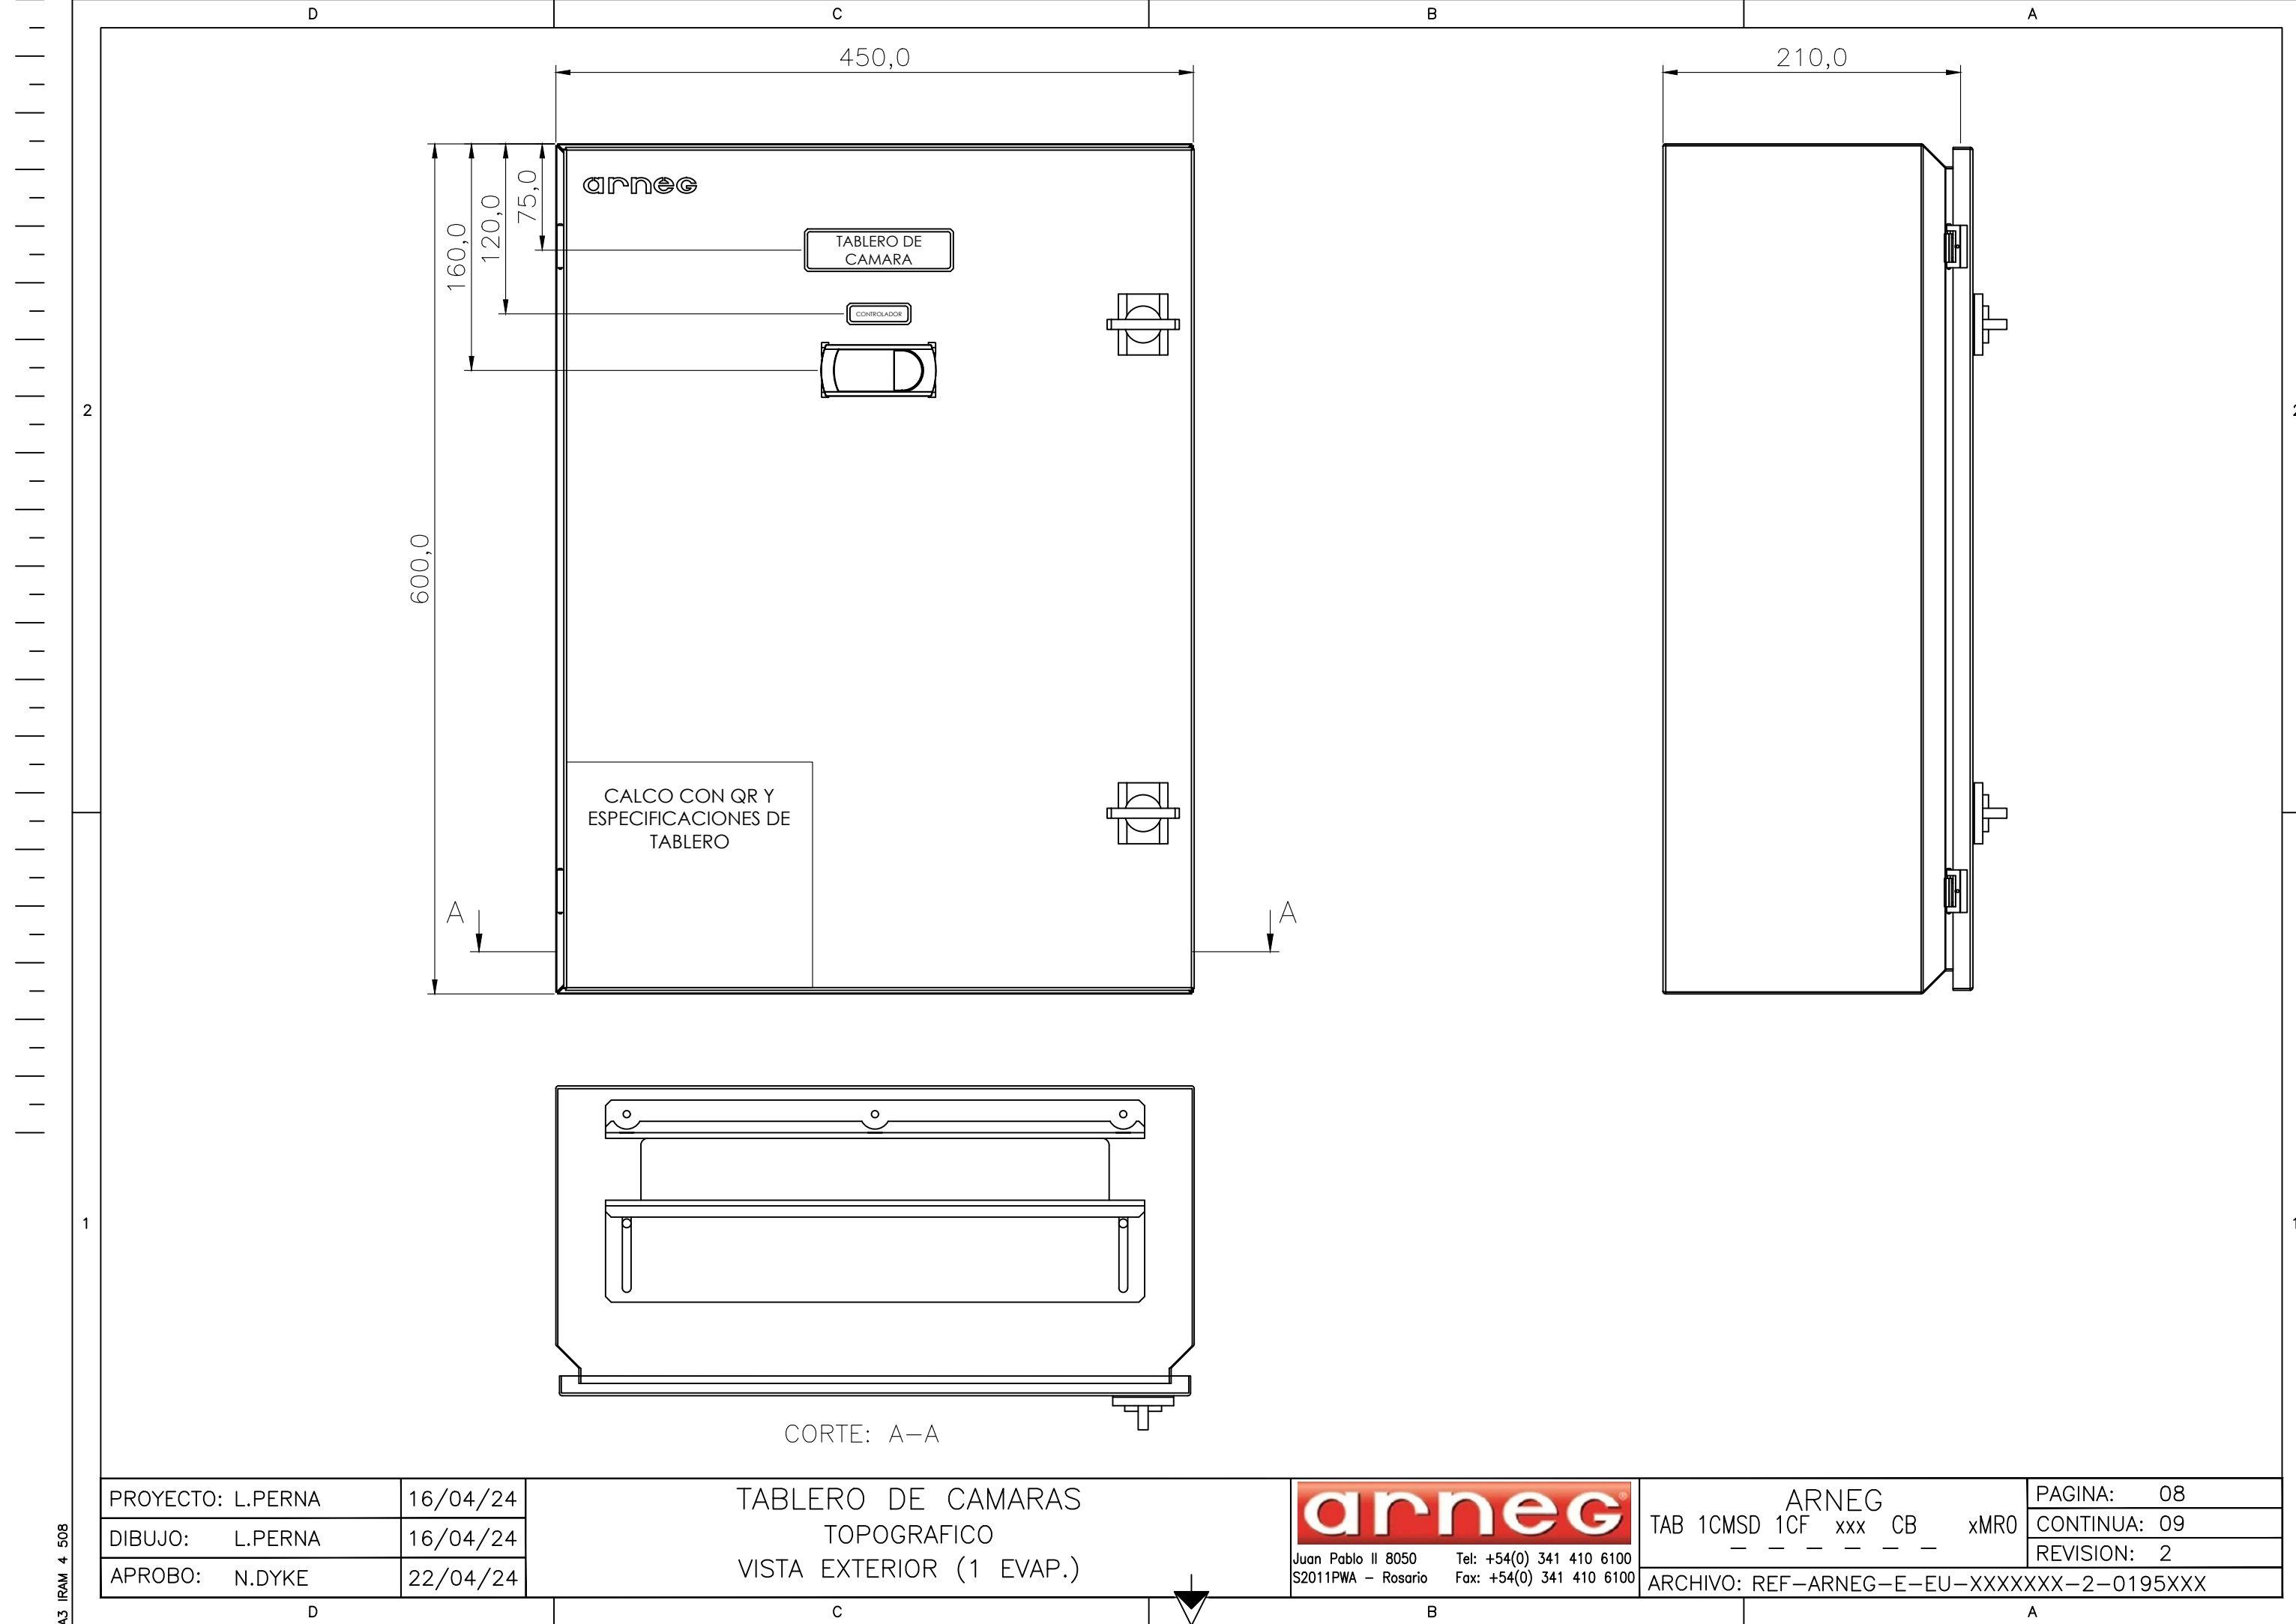

PROYECTO: L.PERNA	16/04/24
DIBUJO: L.PERNA	16/04/24
APROBO: N.DYKE	22/04/24

TABLERO DE CAMARAS
TOPOGRAFICO
VISTA EXTERIOR (1 EVAP.)



arneg

Juan Pablo II 8050
S2011PWA - Rosario

Tel: +54(0) 341 410 6100
Fax: +54(0) 341 410 6100

ARNEG TAB 1CMSD 1CF xxx CB xMR0	PAGINA: 08
	CONTINUA: 09
	REVISION: 2
ARCHIVO: REF-ARNEG-E-EU-XXXXXXX-2-0195XXX	

DETALLE PLACA MONTAJE

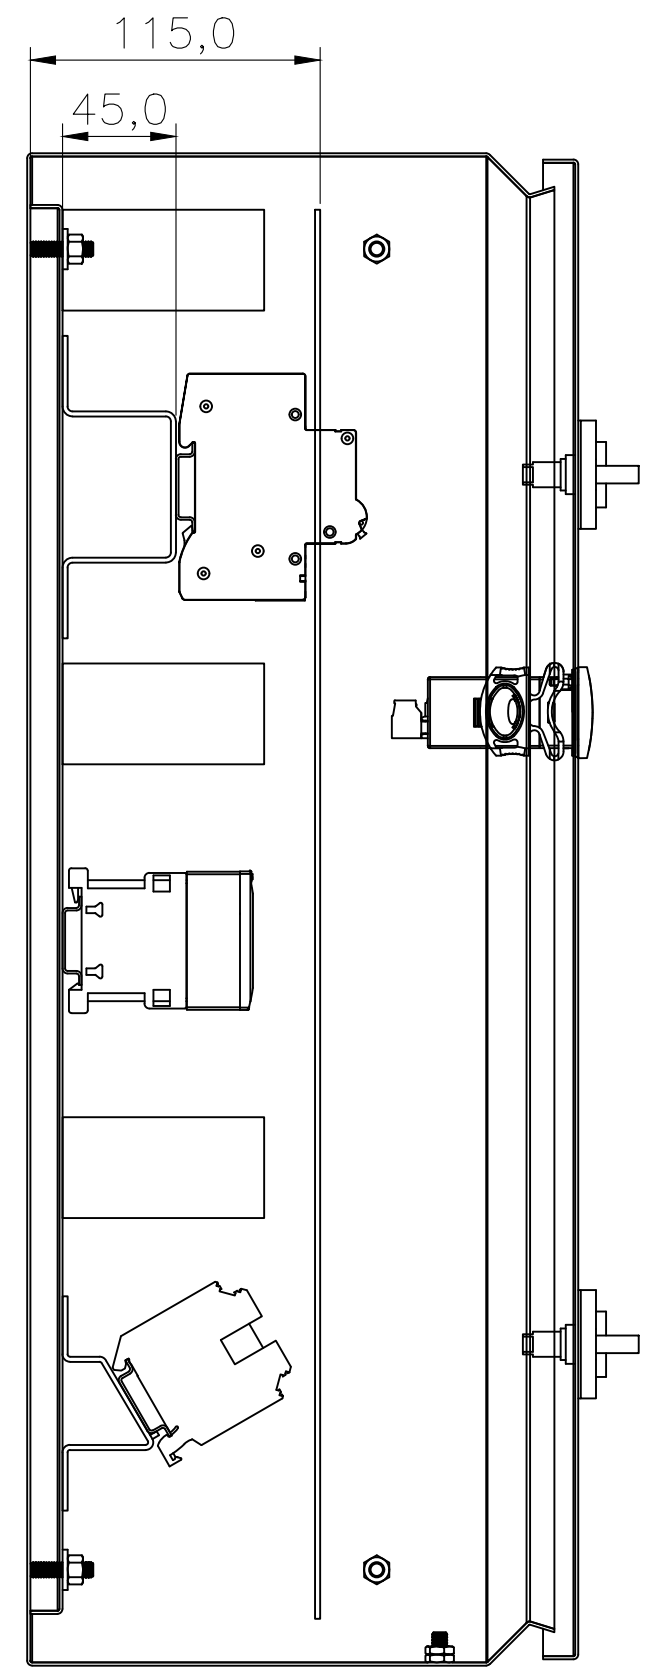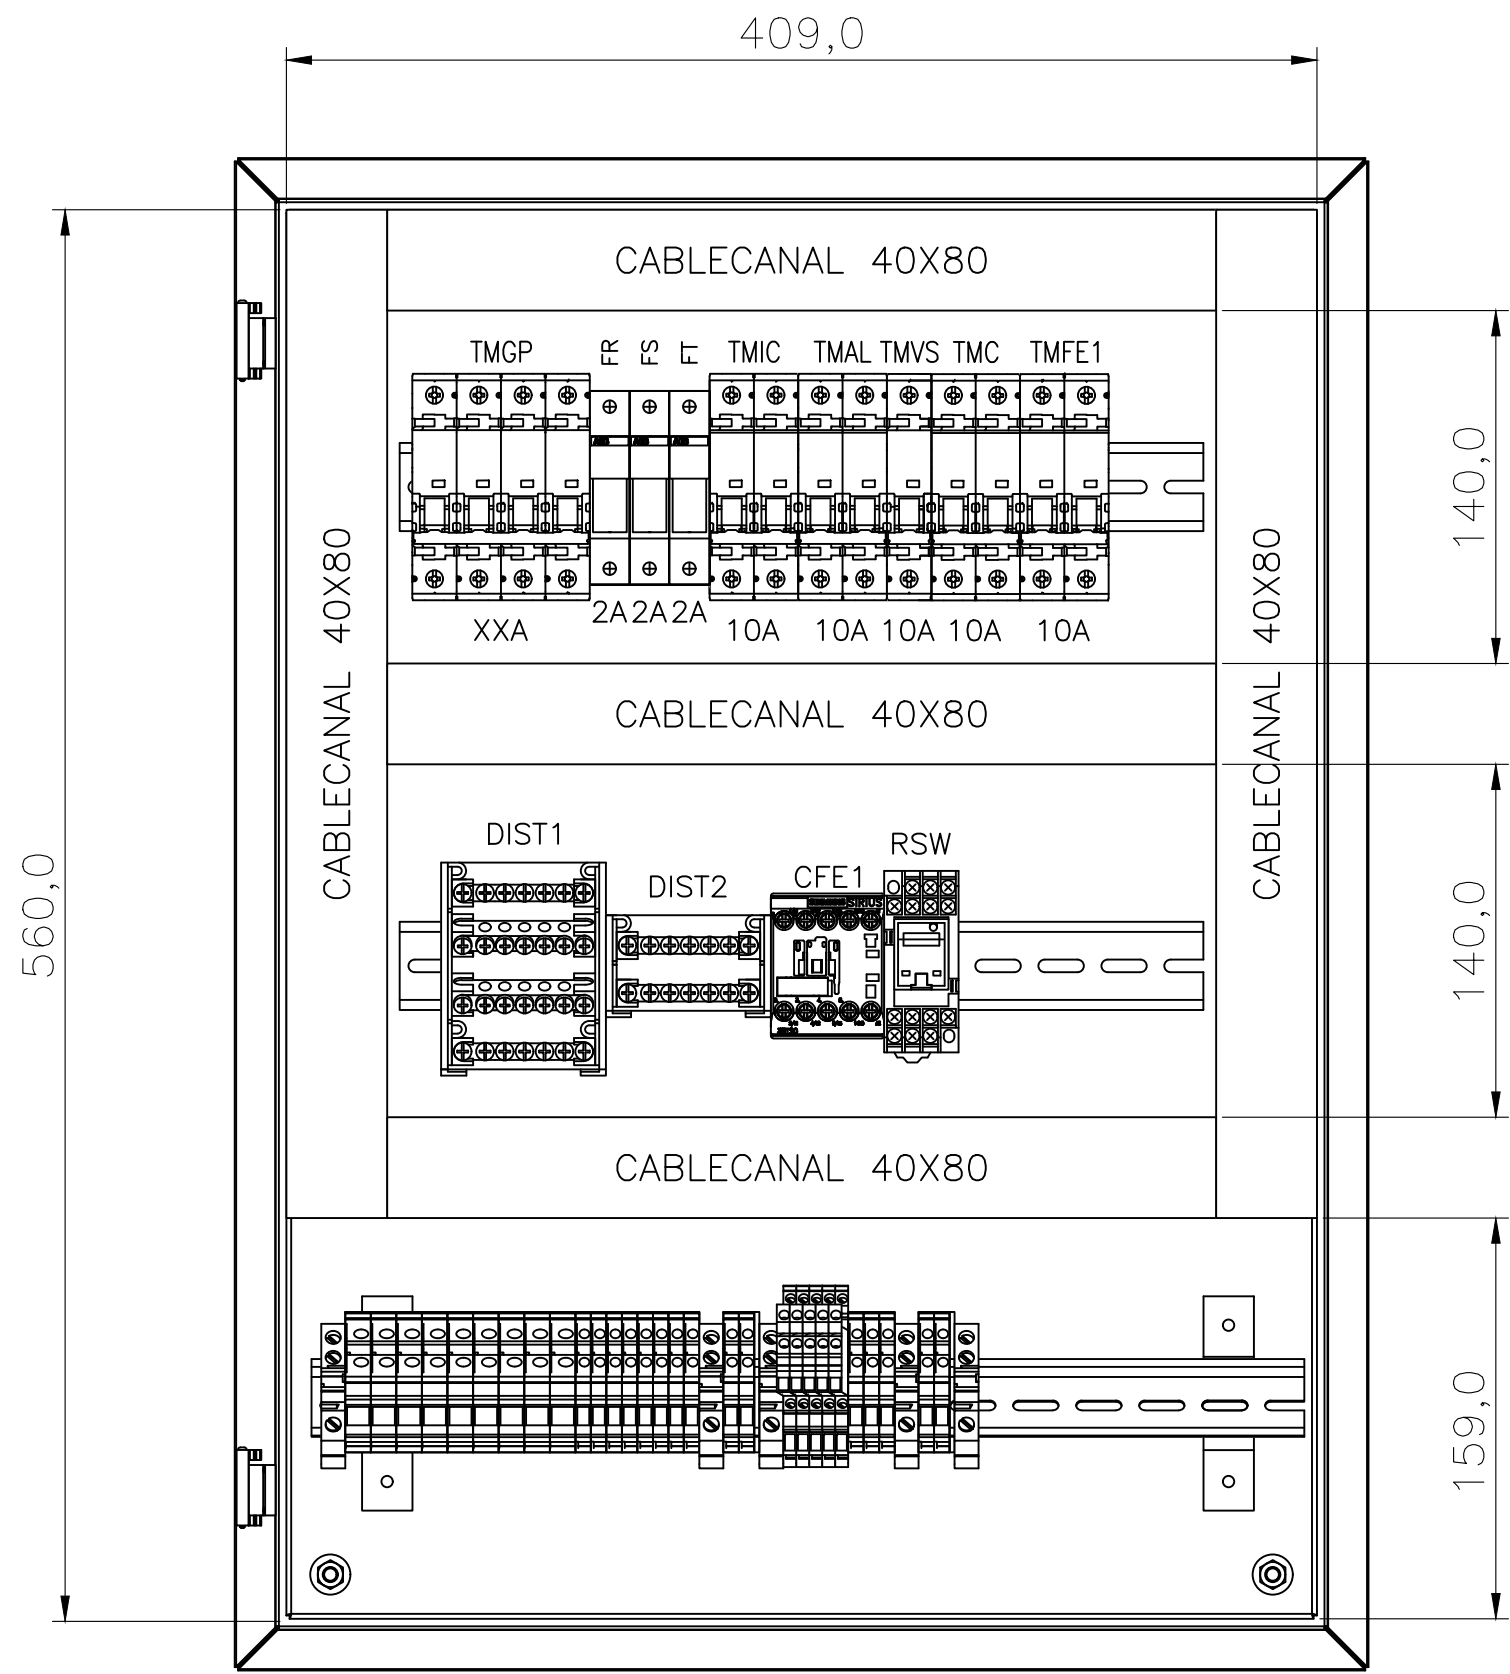

PROYECTO: L.PERNA	16/04/24
DIBUJO: L.PERNA	16/04/24
APROBO: N.DYKE	22/04/24



TABLERO DE CAMARAS
TOPOGRAFICO
VISTA INTERIOR (3 EVAP.)

arneg
Juan Pablo II 8050 Tel: +54(0) 341 410 6100
S2011PWA - Rosario Fax: +54(0) 341 410 6100

ARNEG
TAB 1CMSD 1CF xxx CB xMR0
ARCHIVO: REF-ARNEG-E-EU-XXXXXXX-2-0195XXX

PAGINA: 09
CONTINUA: 10
REVISION: 2

DETALLE PLACA MONTAJE

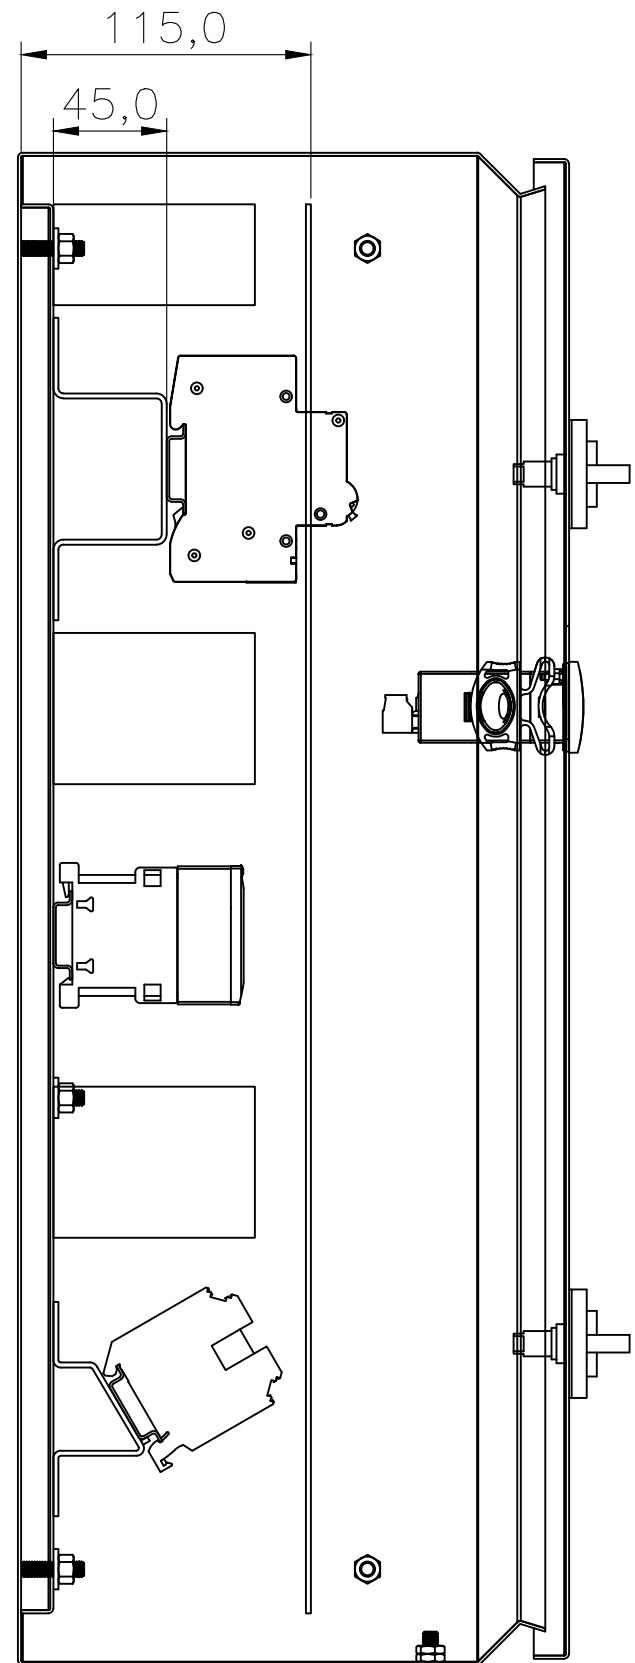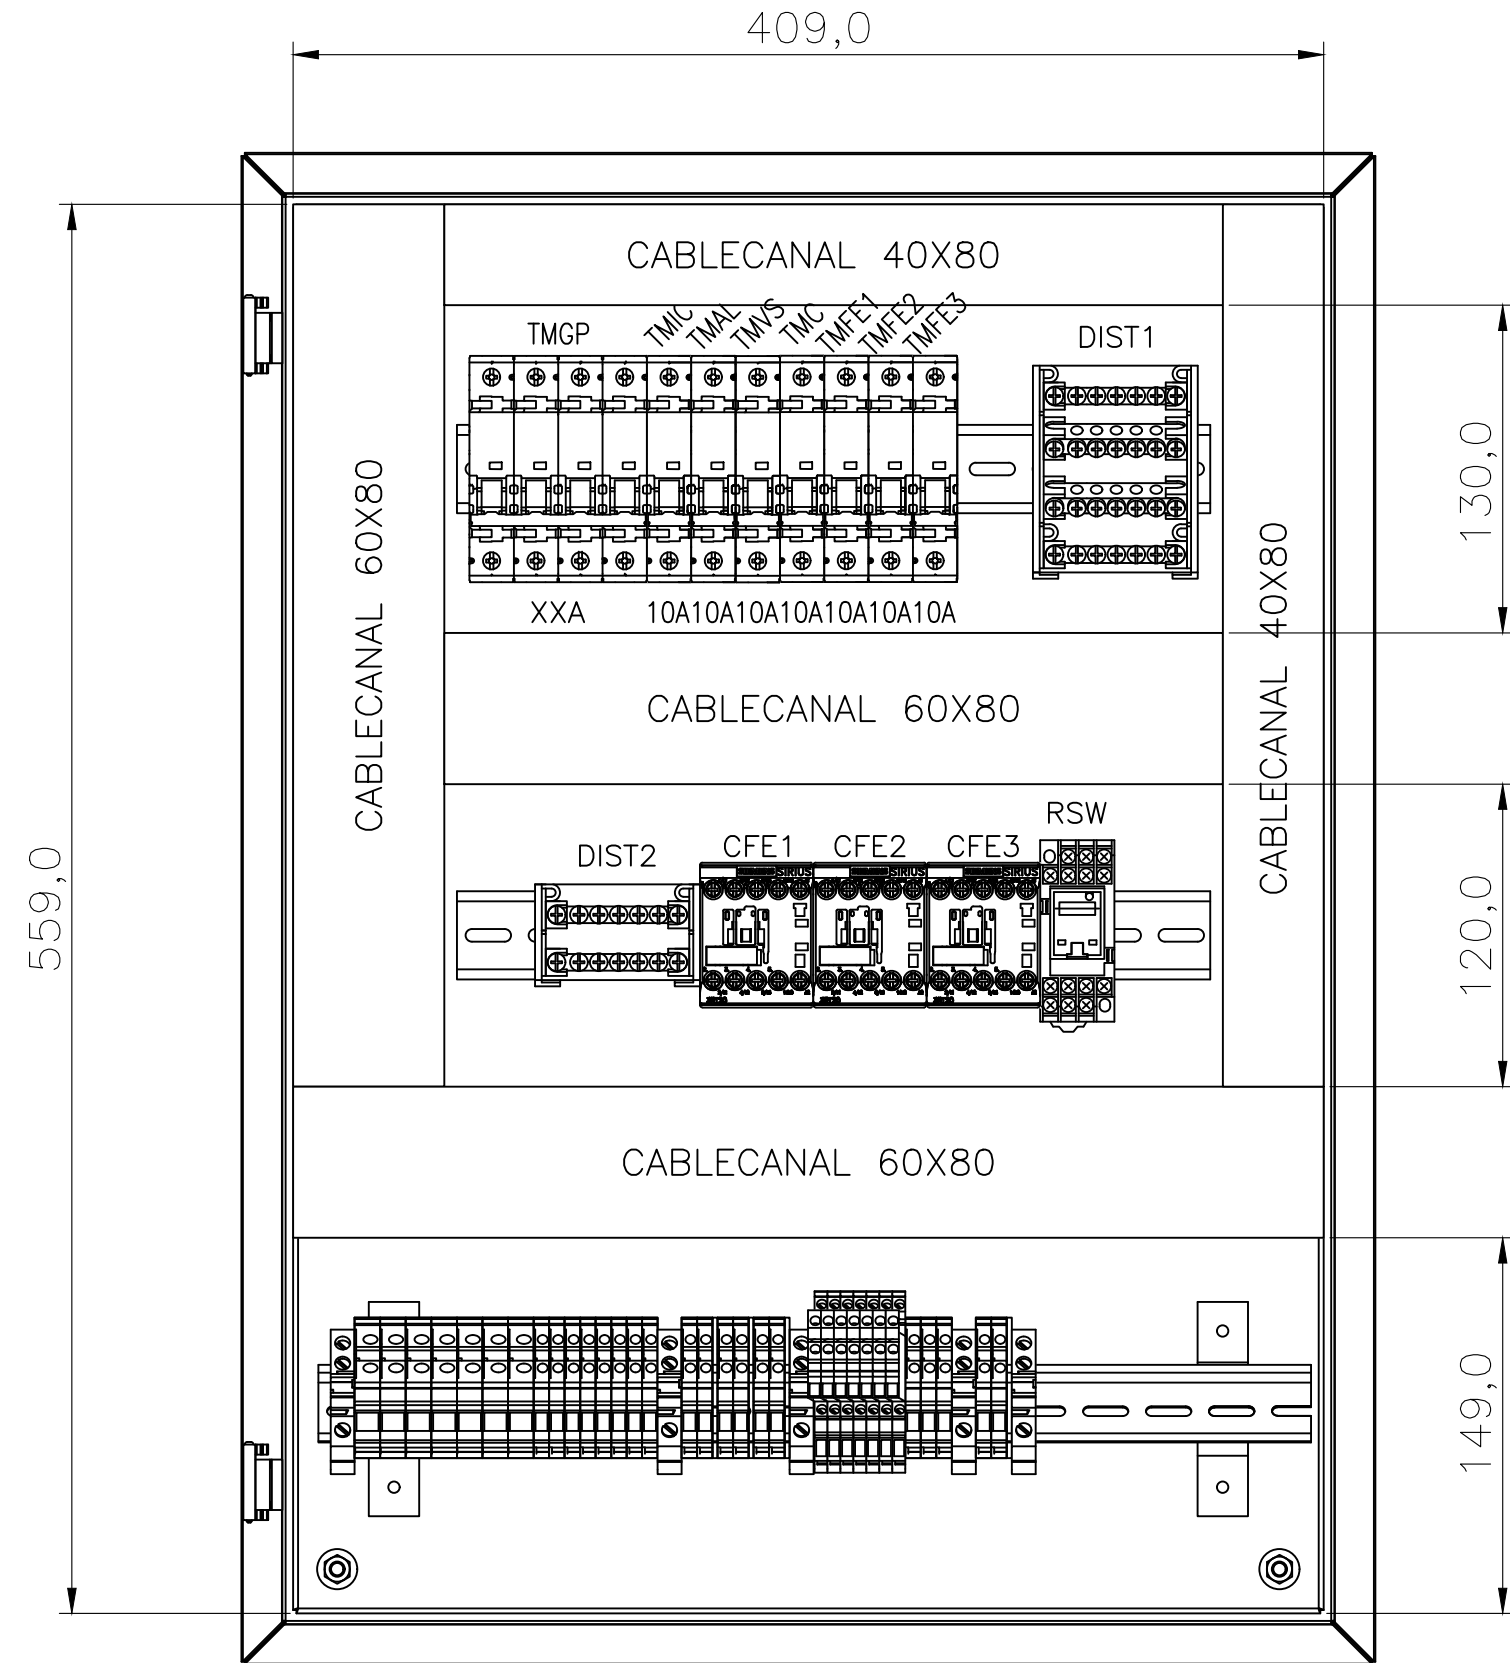

PROYECTO: L.PERNA	16/04/24
DIBUJO: L.PERNA	16/04/24
APROBO: N.DYKE	22/04/24

TABLERO DE CAMARAS
TOPOGRAFICO
VISTA INTERIOR (3 EVAP.)





Juan Pablo II 8050
S2011PWA - Rosario

Tel: +54(0) 341 410 6100
Fax: +54(0) 341 410 6100

ARNEG	PAGINA: 08E
TAB 1CMSD 1CF xxx CB xMR0	CONTINUA: 09E
ARCHIVO: REF-ARNEG-E-EU-XXXXXXX-2-0195XXX	REVISION: 2

DETALLE PLACA MONTAJE

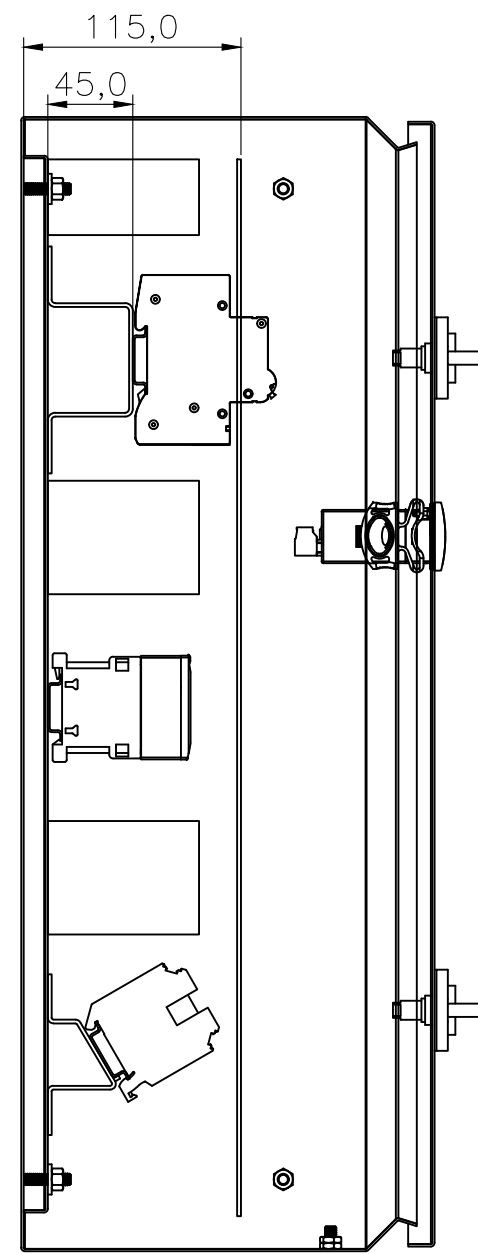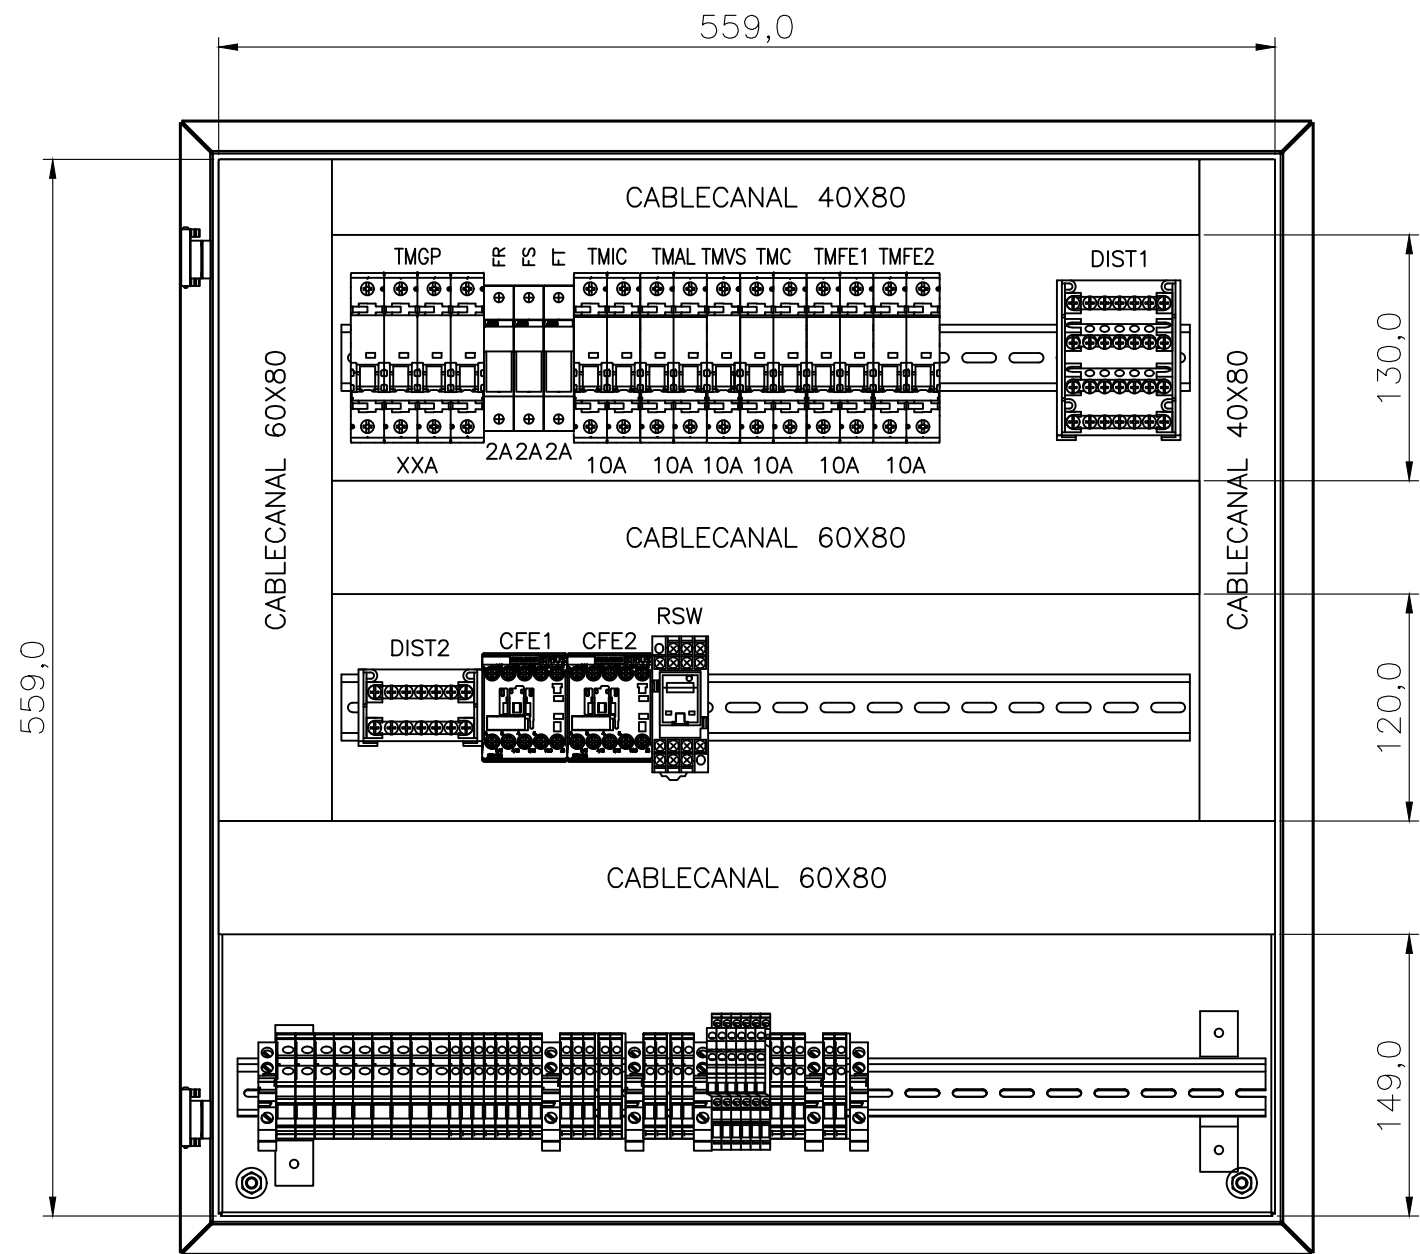


PROYECTO: L.PERNA	16/04/24
DIBUJO: L.PERNA	16/04/24
APROBO: N.DYKE	22/04/24

TABLERO DE CAMARAS
TOPOGRAFICO
VISTA INTERIOR (2 EVAP.)

arneg
Juan Pablo II 8050 Tel: +54(0) 341 410 6100
S2011PWA - Rosario Fax: +54(0) 341 410 6100

ARNEG
TAB 1CMSD 1CF xxx CB xMR0
ARCHIVO: REF-ARNEG-E-EU-XXXXXXX-2-0195XXX

PAGINA: 10
CONTINUA: 11
REVISION: 2

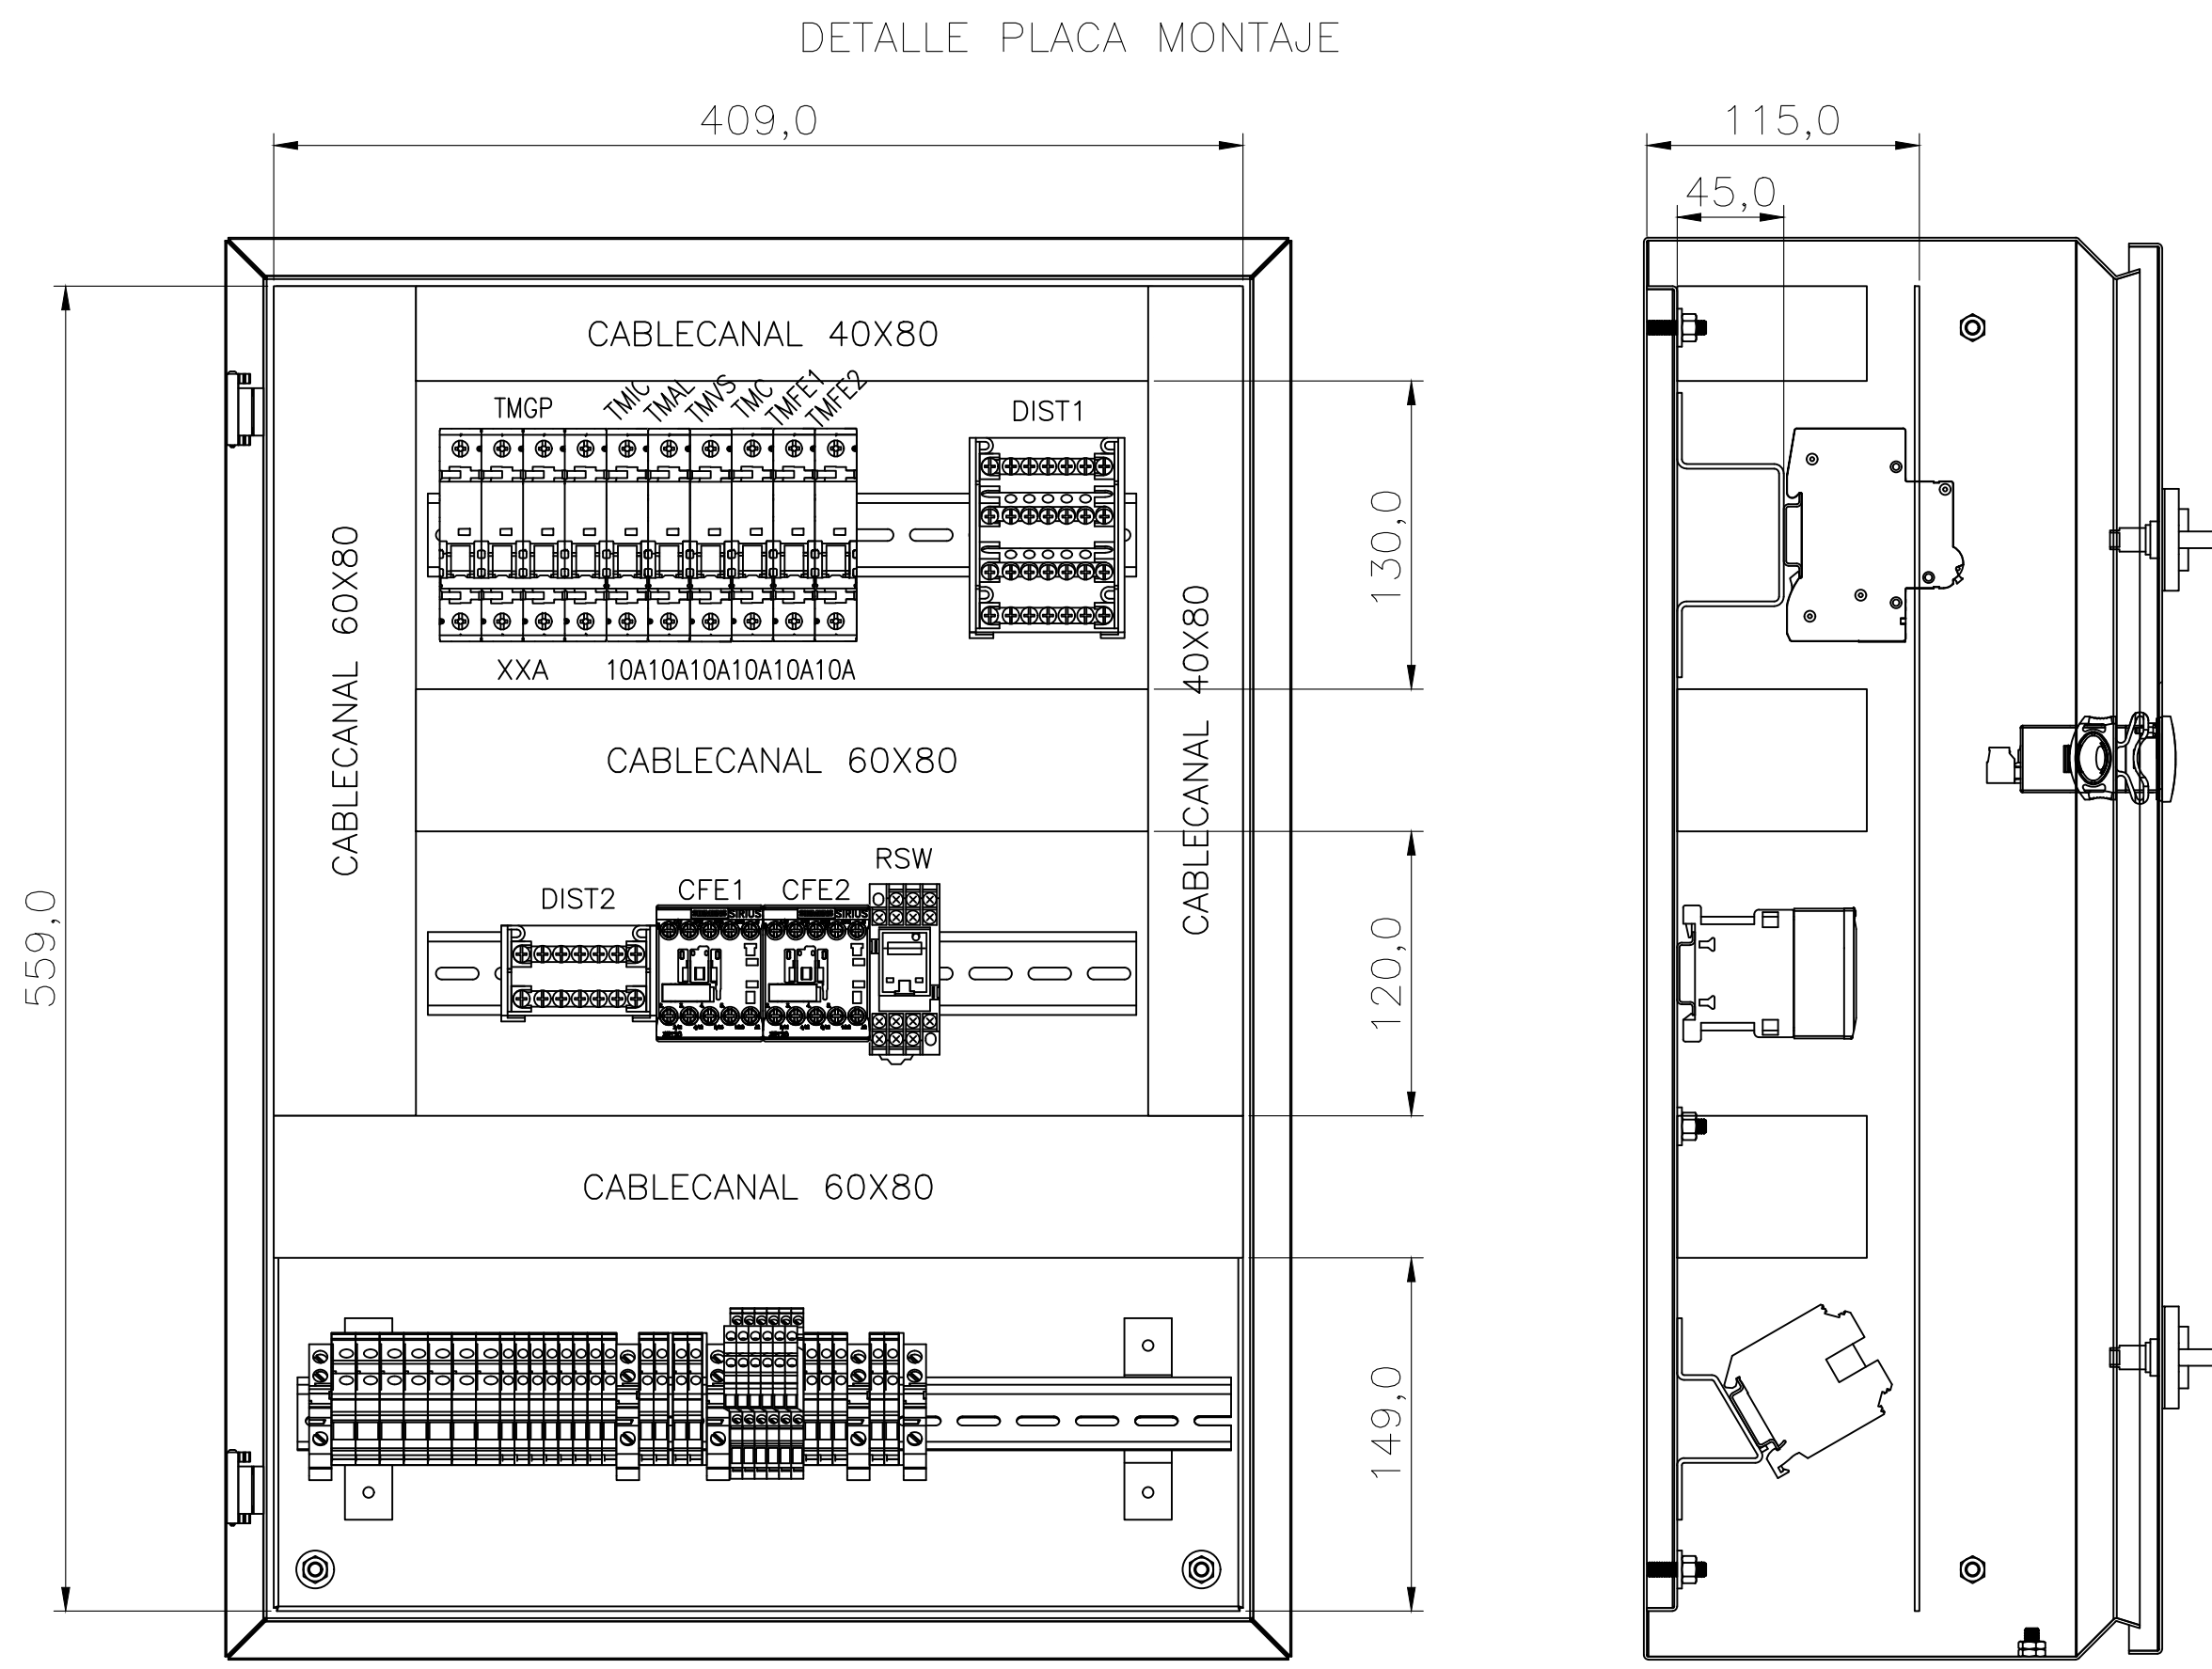

PROYECTO: L.PERNA	16/04/24
DIBUJO: L.PERNA	16/04/24
APROBO: N.DYKE	22/04/24

TABLERO DE CAMARAS
TOPOGRAFICO
VISTA INTERIOR (2 EVAP.)





Juan Pablo II 8050
S2011PWA - Rosario

Tel: +54(0) 341 410 6100
Fax: +54(0) 341 410 6100

ARNEG	PAGINA: 09E
TAB 1CMSD 1CF xxx CB xMR0	CONTINUA: 10E
ARCHIVO: REF-ARNEG-E-EU-XXXXXXX-2-0195XXX	REVISION: 2

DETALLE PLACA MONTAJE

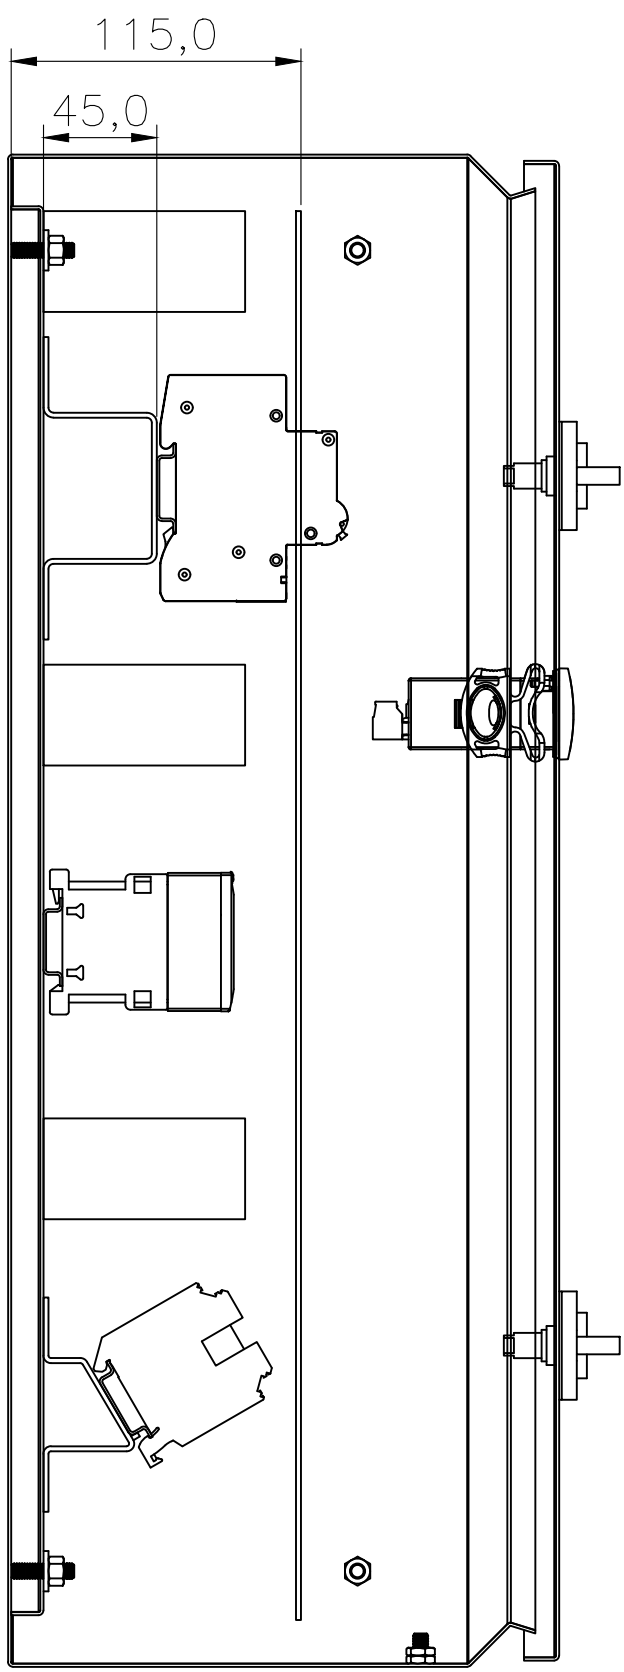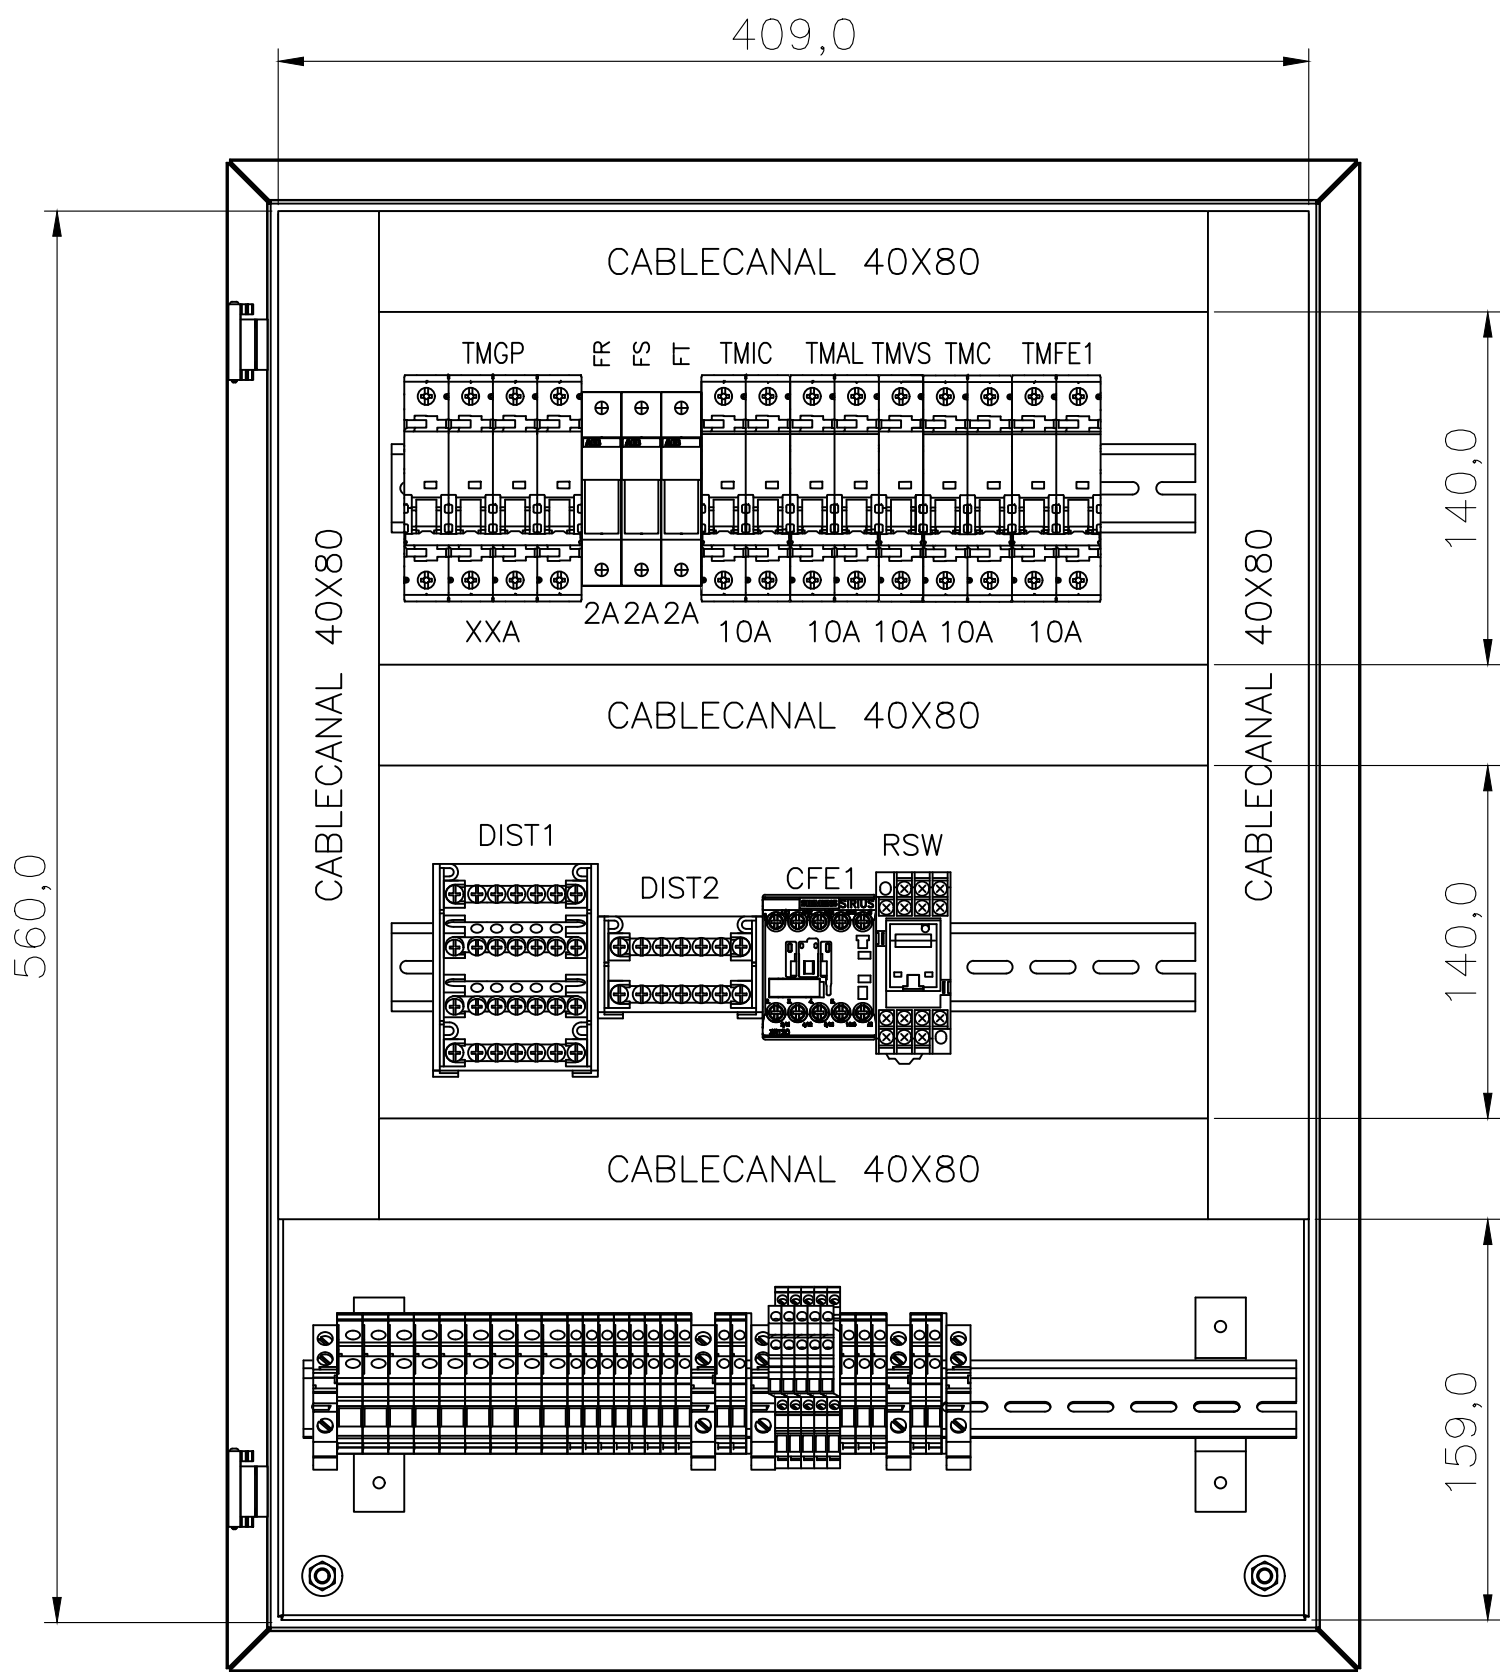


PROYECTO: L.PERNA	16/04/24
DIBUJO: L.PERNA	16/04/24
APROBO: N.DYKE	22/04/24

TABLERO DE CAMARAS
TOPOGRAFICO
VISTA INTERIOR (1 EVAP.)

arneg
Juan Pablo II 8050 Tel: +54(0) 341 410 6100
S2011PWA - Rosario Fax: +54(0) 341 410 6100

ARNEG	PAGINA: 11
TAB 1CMSD 1CF xxx CB xMR0	CONTINUA: 12
	REVISION: 2
ARCHIVO: REF-ARNEG-E-EU-XXXXXXX-2-0195XXX	

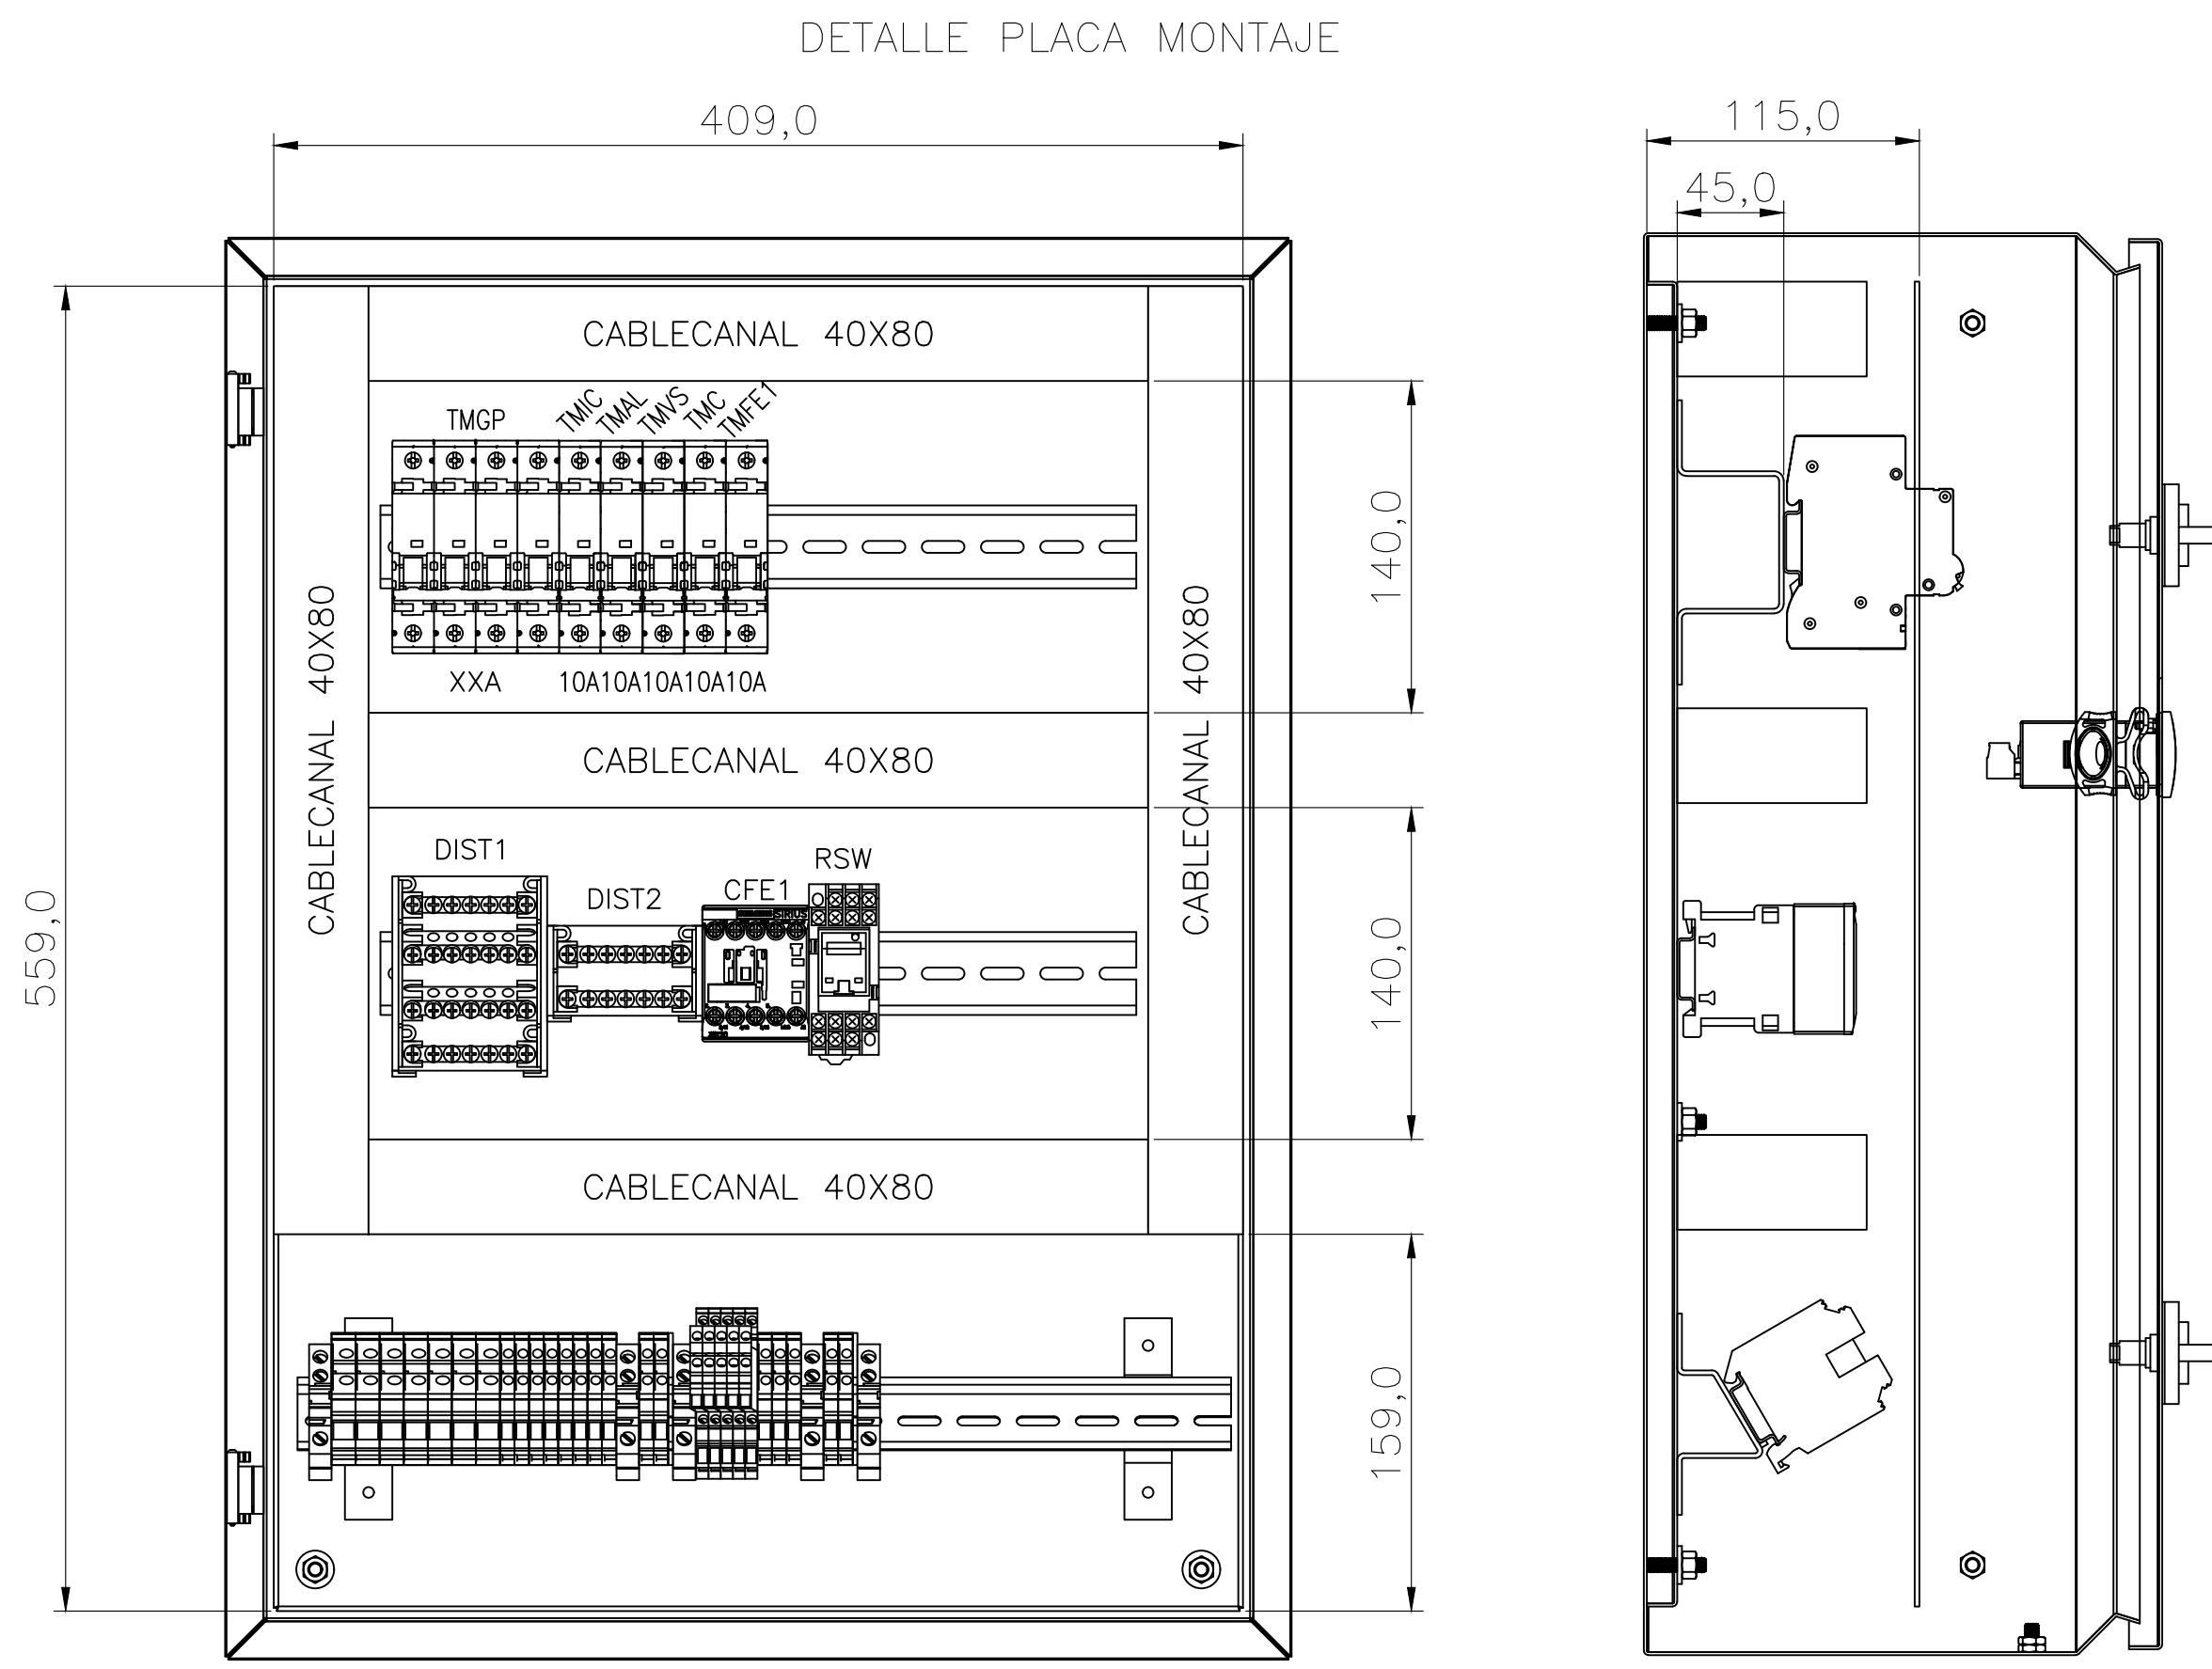

PROYECTO: L.PERNA	16/04/24
DIBUJO: L.PERNA	16/04/24
APROBO: N.DYKE	22/04/24

TABLERO DE CAMARAS
TOPOGRAFICO
VISTA INTERIOR (1 EVAP.)



Juan Pablo II 8050
S2011PWA - Rosario

Tel: +54(0) 341 410 6100
Fax: +54(0) 341 410 6100

ARNEG	PAGINA: 10E
TAB 1CMSD 1CF xxx CB xMR0	CONTINUA: 11E
ARCHIVO: REF-ARNEG-E-EU-XXXXXXX-2-0195XXX	REVISION: 2


D

C

B

A

DETALLE CONTRATAPA

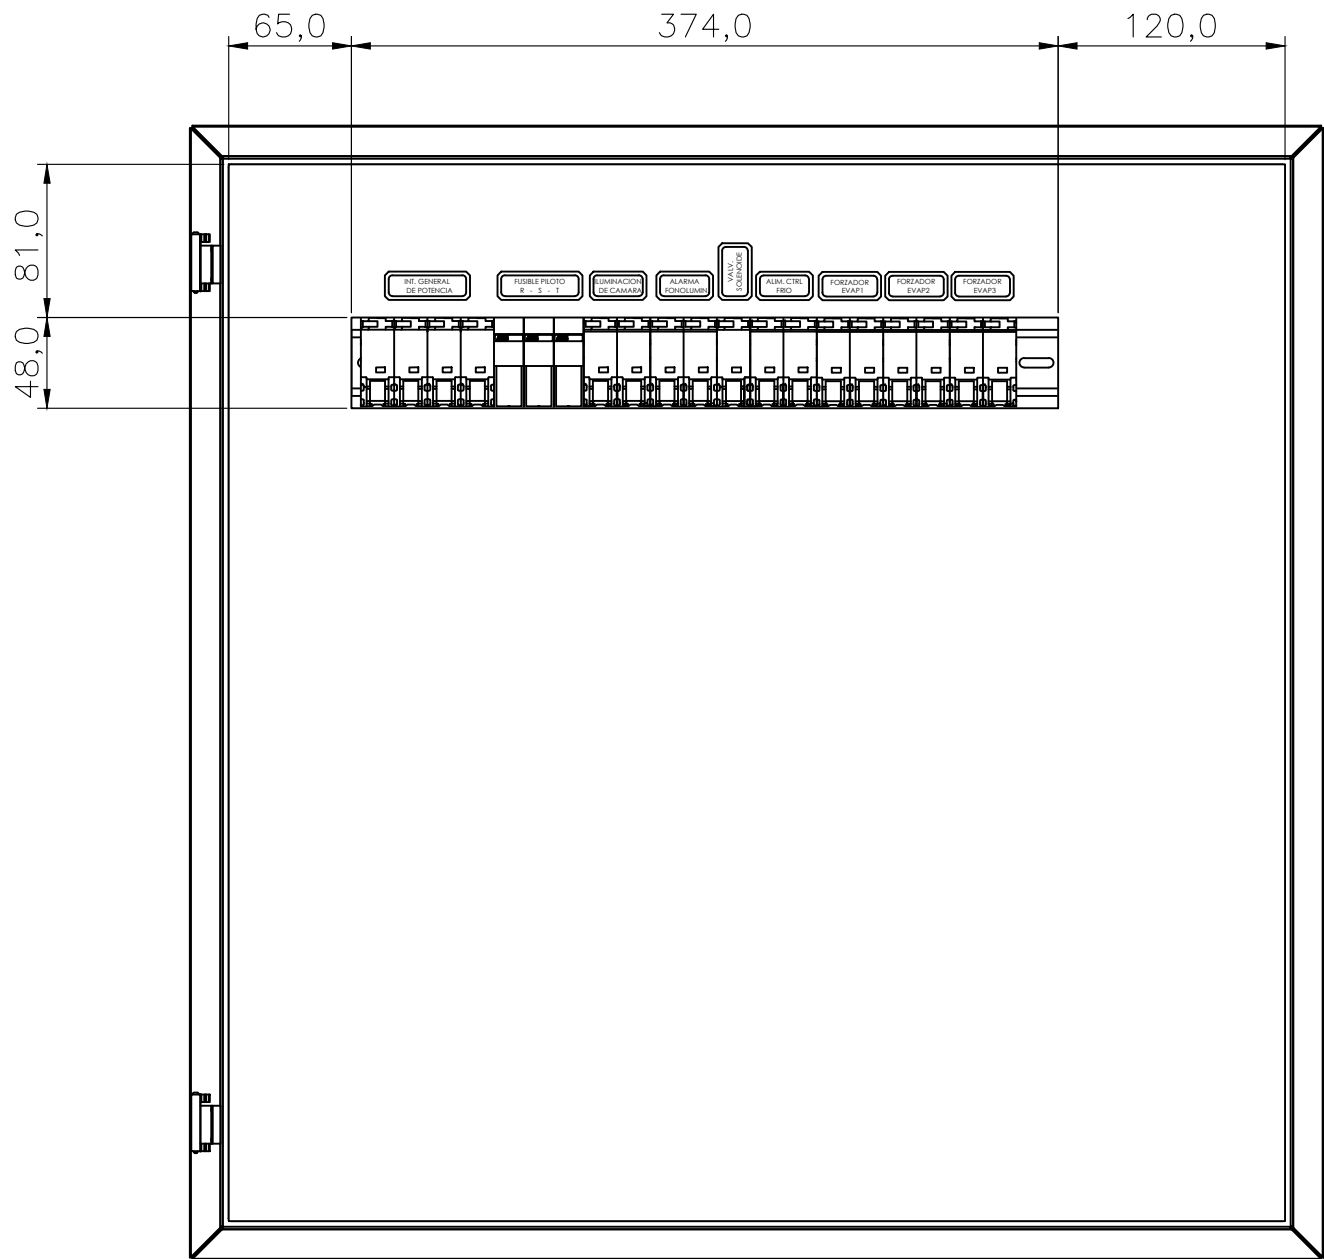


PROYECTO: L.PERNA	16/04/24
DIBUJO: L.PERNA	16/04/24
APROBO: N.DYKE	22/04/24

TABLERO DE CAMARAS
TOPOGRAFICO
VISTA INTERIOR CON CONTRAFRENTE (3 EVAP.)

arneg
Juan Pablo II 8050 Tel: +54(0) 341 410 6100
S2011PWA - Rosario Fax: +54(0) 341 410 6100

ARNEG
TAB 1CMSD 1CF xxx CB xMRO
- - - - -
ARCHIVO: REF-ARNEG-E-EU-XXXXXXX-2-0195XXX

PAGINA: 12
CONTINUA: 13
REVISION: 2

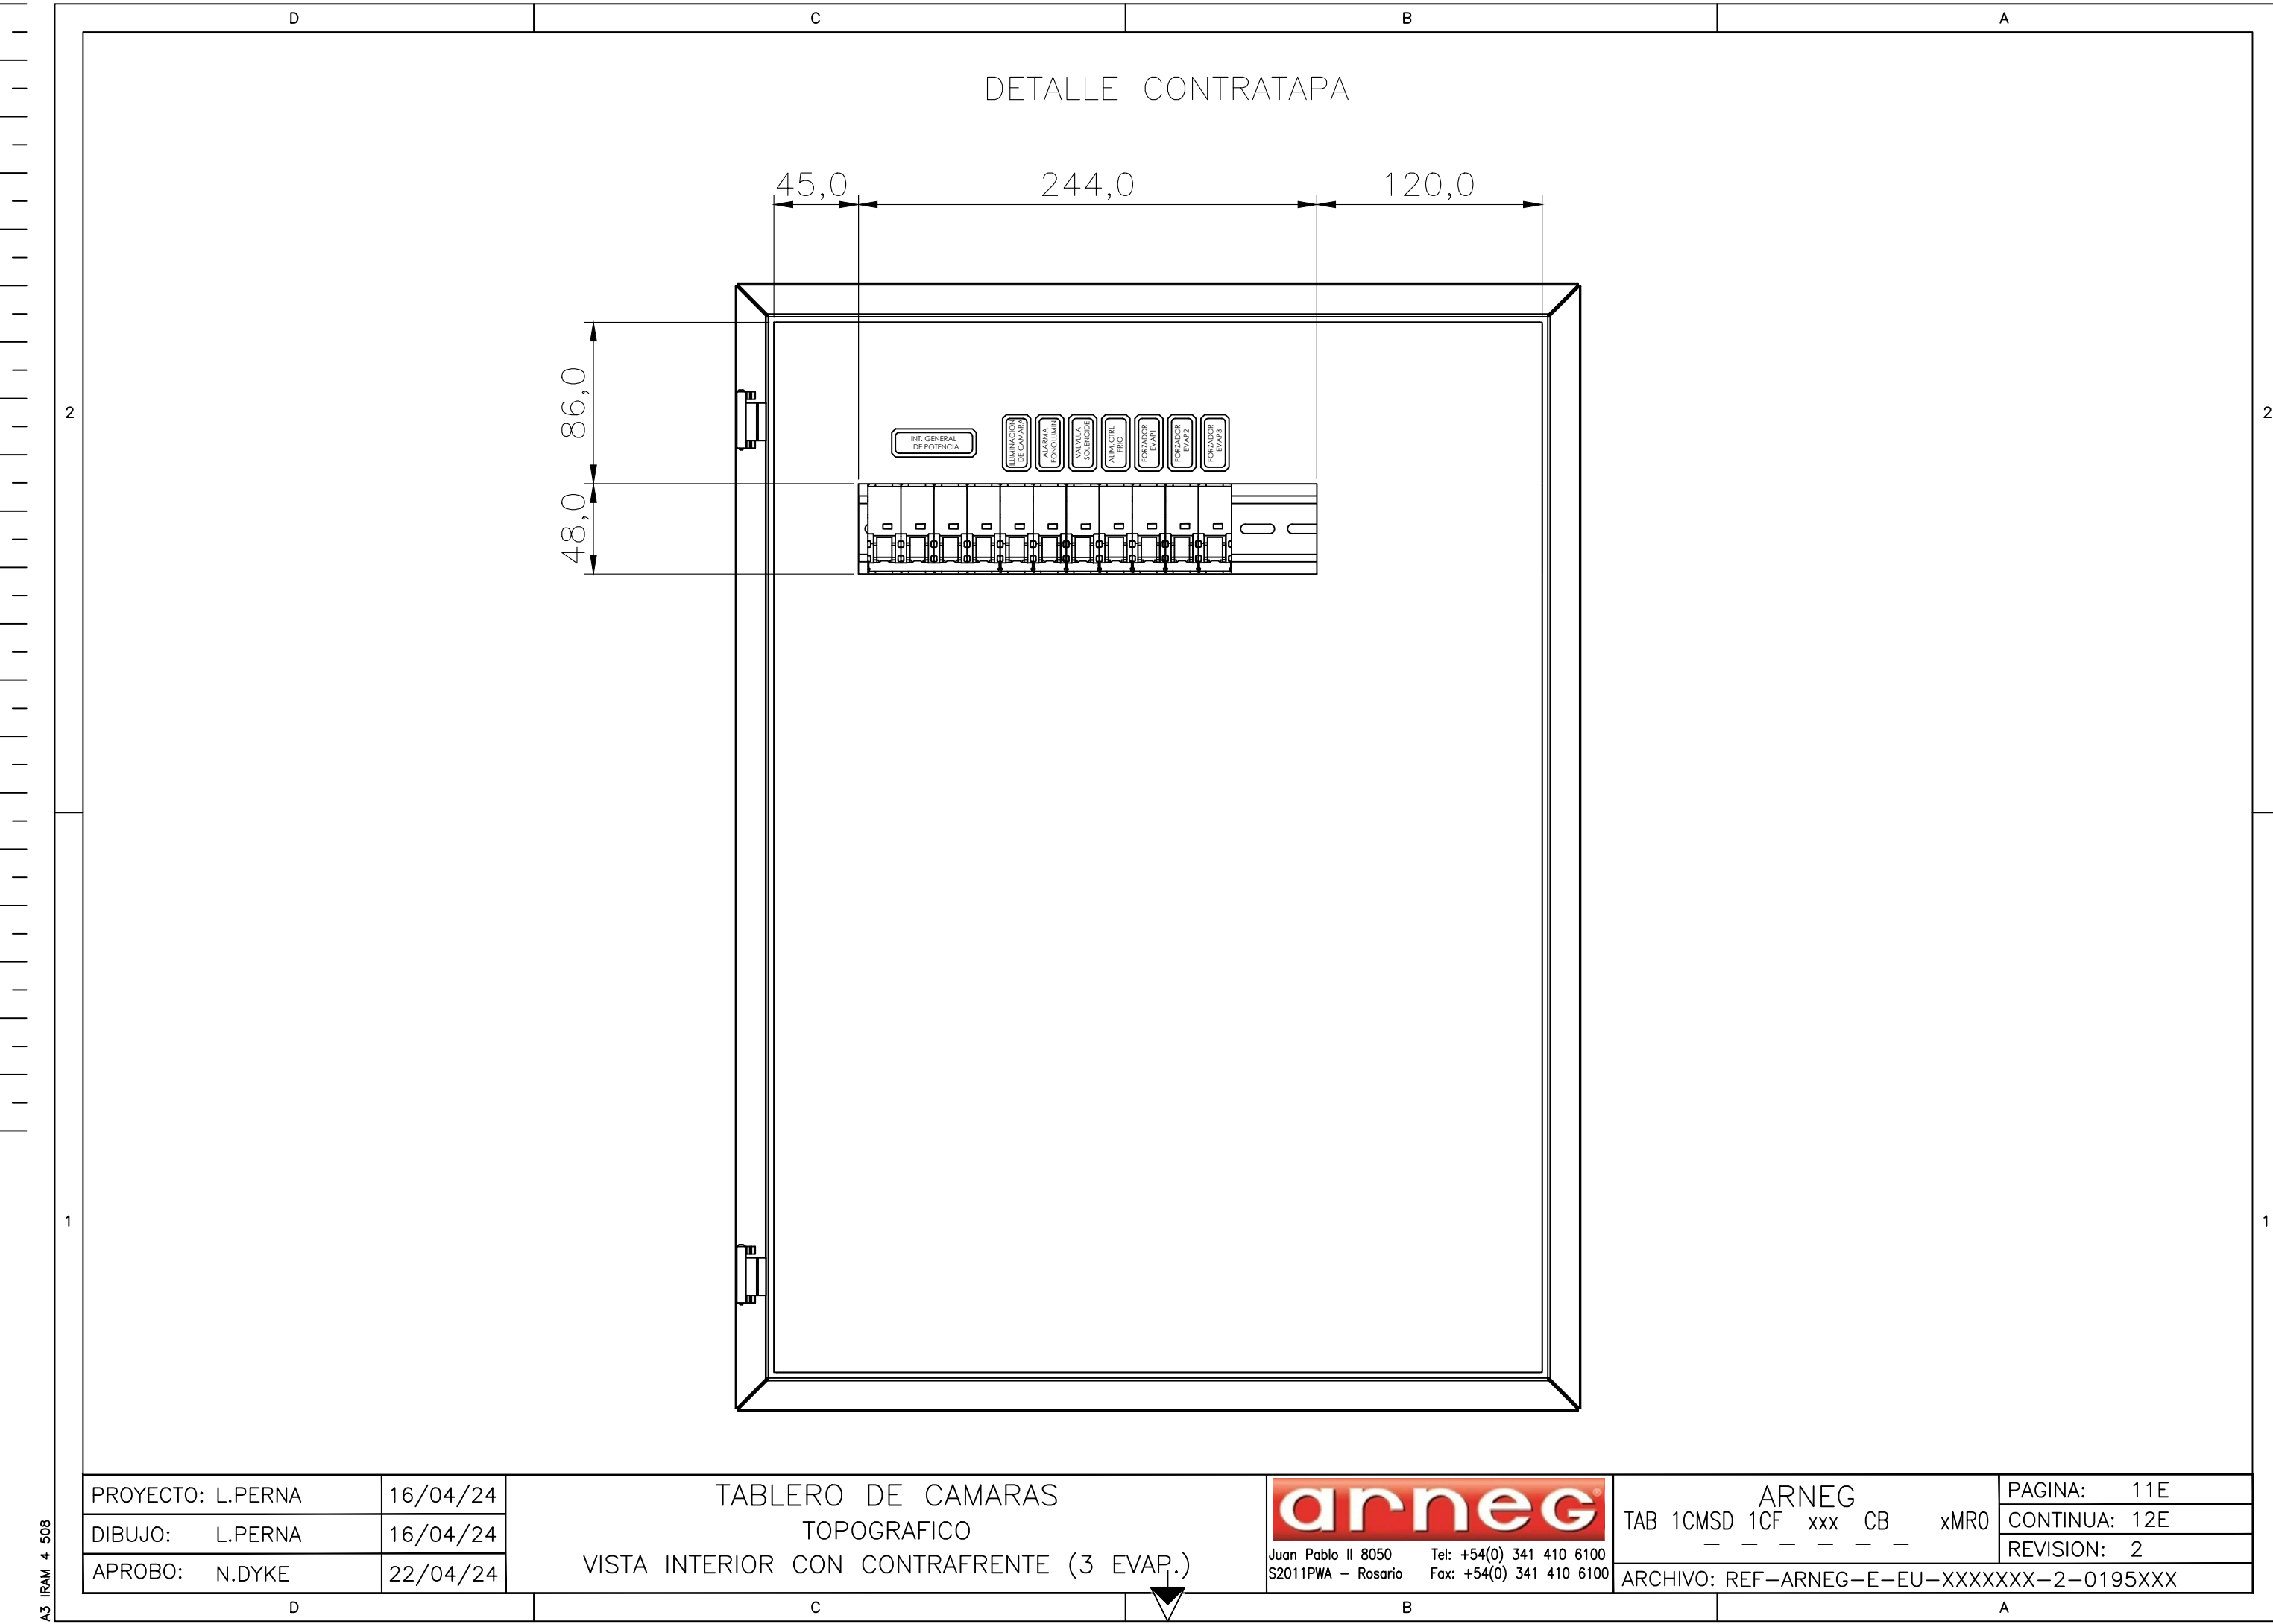

A3 IRAM 4 508

PROYECTO: L.PERNA	16/04/24
DIBUJO: L.PERNA	16/04/24
APROBO: N.DYKE	22/04/24

TABLERO DE CAMARAS
TOPOGRAFICO
VISTA INTERIOR CON CONTRAFRENTE (3 EVAP.)



Juan Pablo II 8050 Tel: +54(0) 341 410 6100
S2011PWA - Rosario Fax: +54(0) 341 410 6100


ARNEG
TAB 1CMSD 1CF xxx CB xMR0
— — — — —
ARCHIVO: REF-ARNEG-E-EU-XXXXXXX-2-0195XXX

PAGINA: 11E
CONTINUA: 12E
REVISION: 2

2 |

A3 IRAM 4 508

244,0 120,0

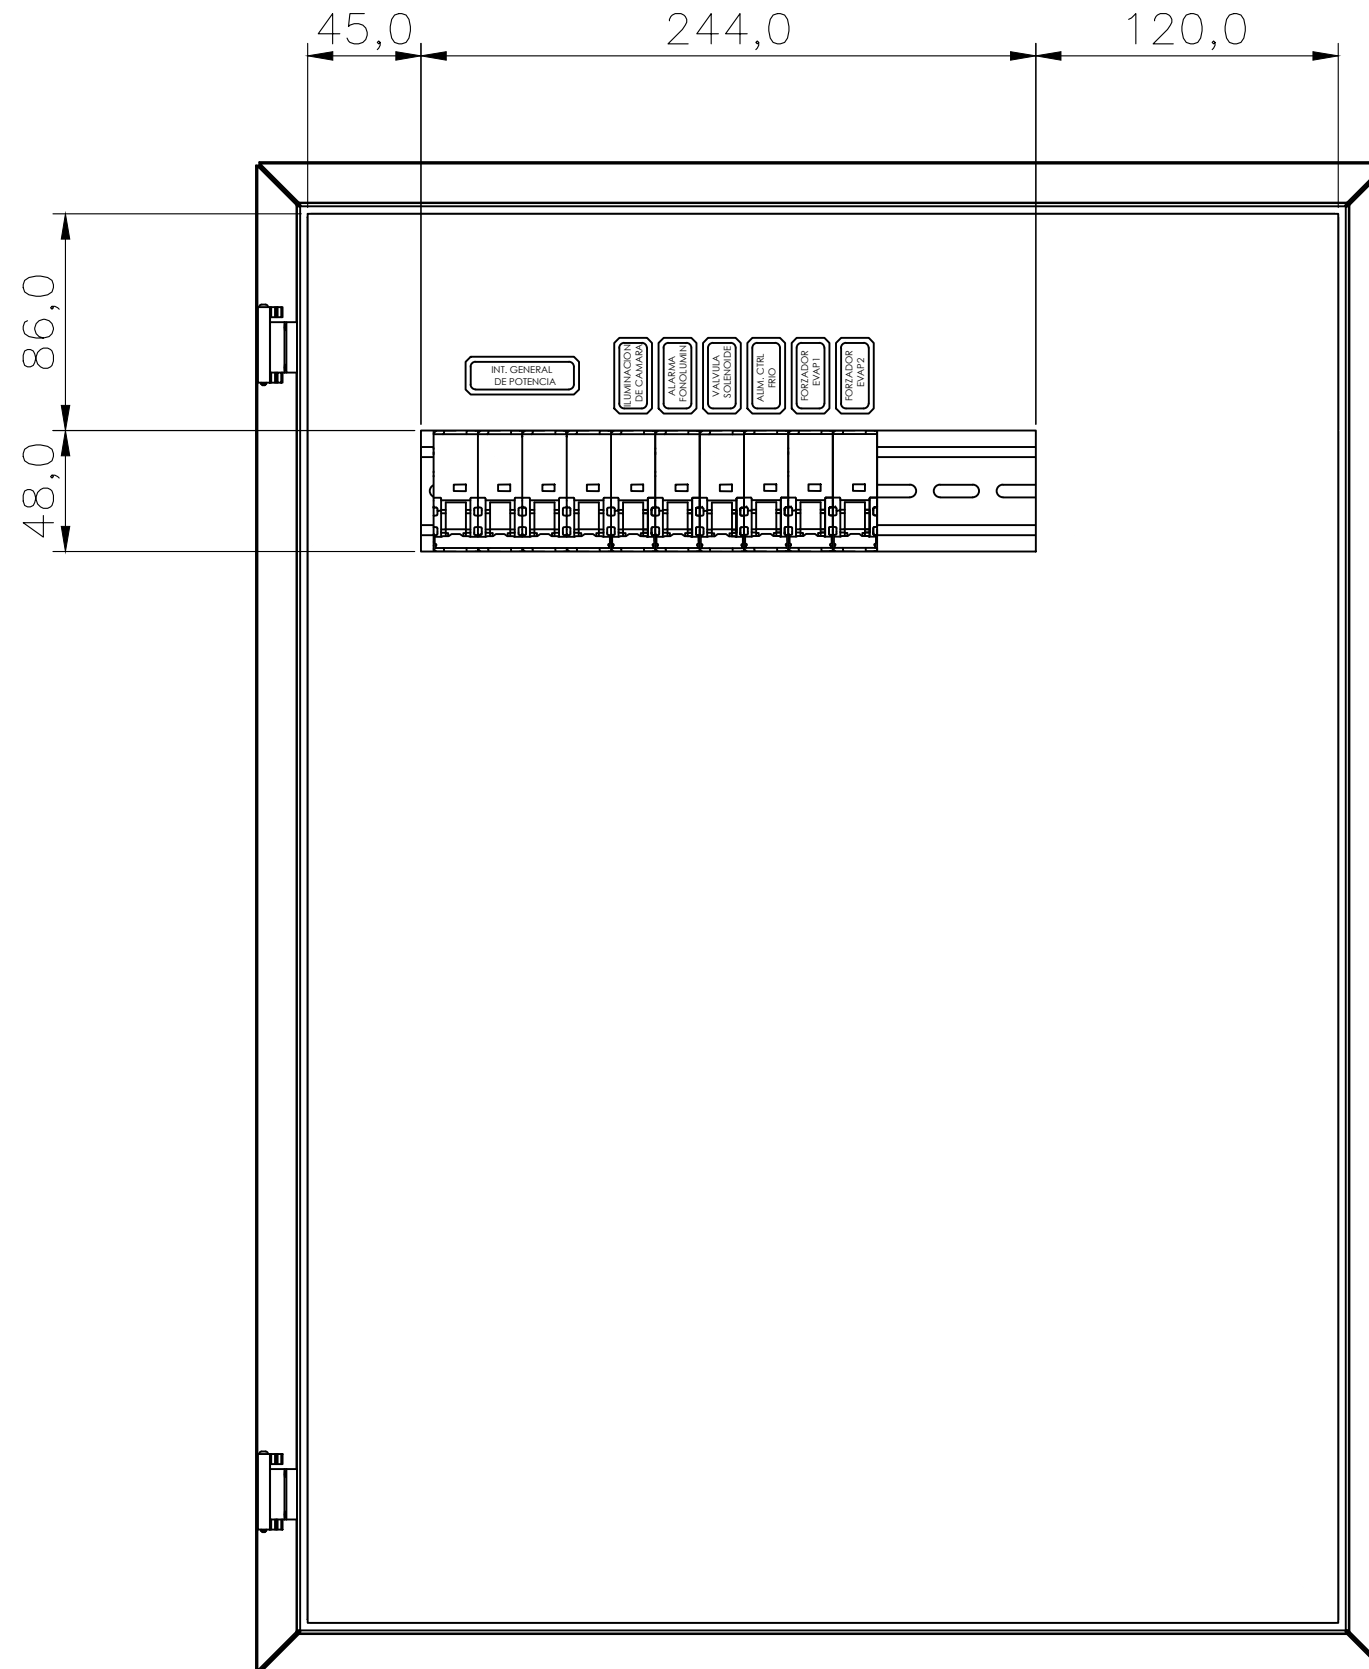

PROYECTO: L.PERNA	16/04/24
DIBUJO: L.PERNA	16/04/24
APROBO: N.DYKE	22/04/24

TABLERO DE CAMARAS
TOPOGRAFICO
VISTA INTERIOR CON CONTRAFRENTE (2 EVAP.)




Juan Pablo II 8050 Tel: +54(0) 341 410 6100
S2011PWA – Rosario Fax: +54(0) 341 410 6100


ARNEG
TAB 1CMSD 1CF xxx CB xMRO

0 ARCHIVO: REF-ARNEG-E-EU-XXXXXXX-2-0195XXX


PAGINA:	12E
CONTINUA:	13E
REVISION:	2

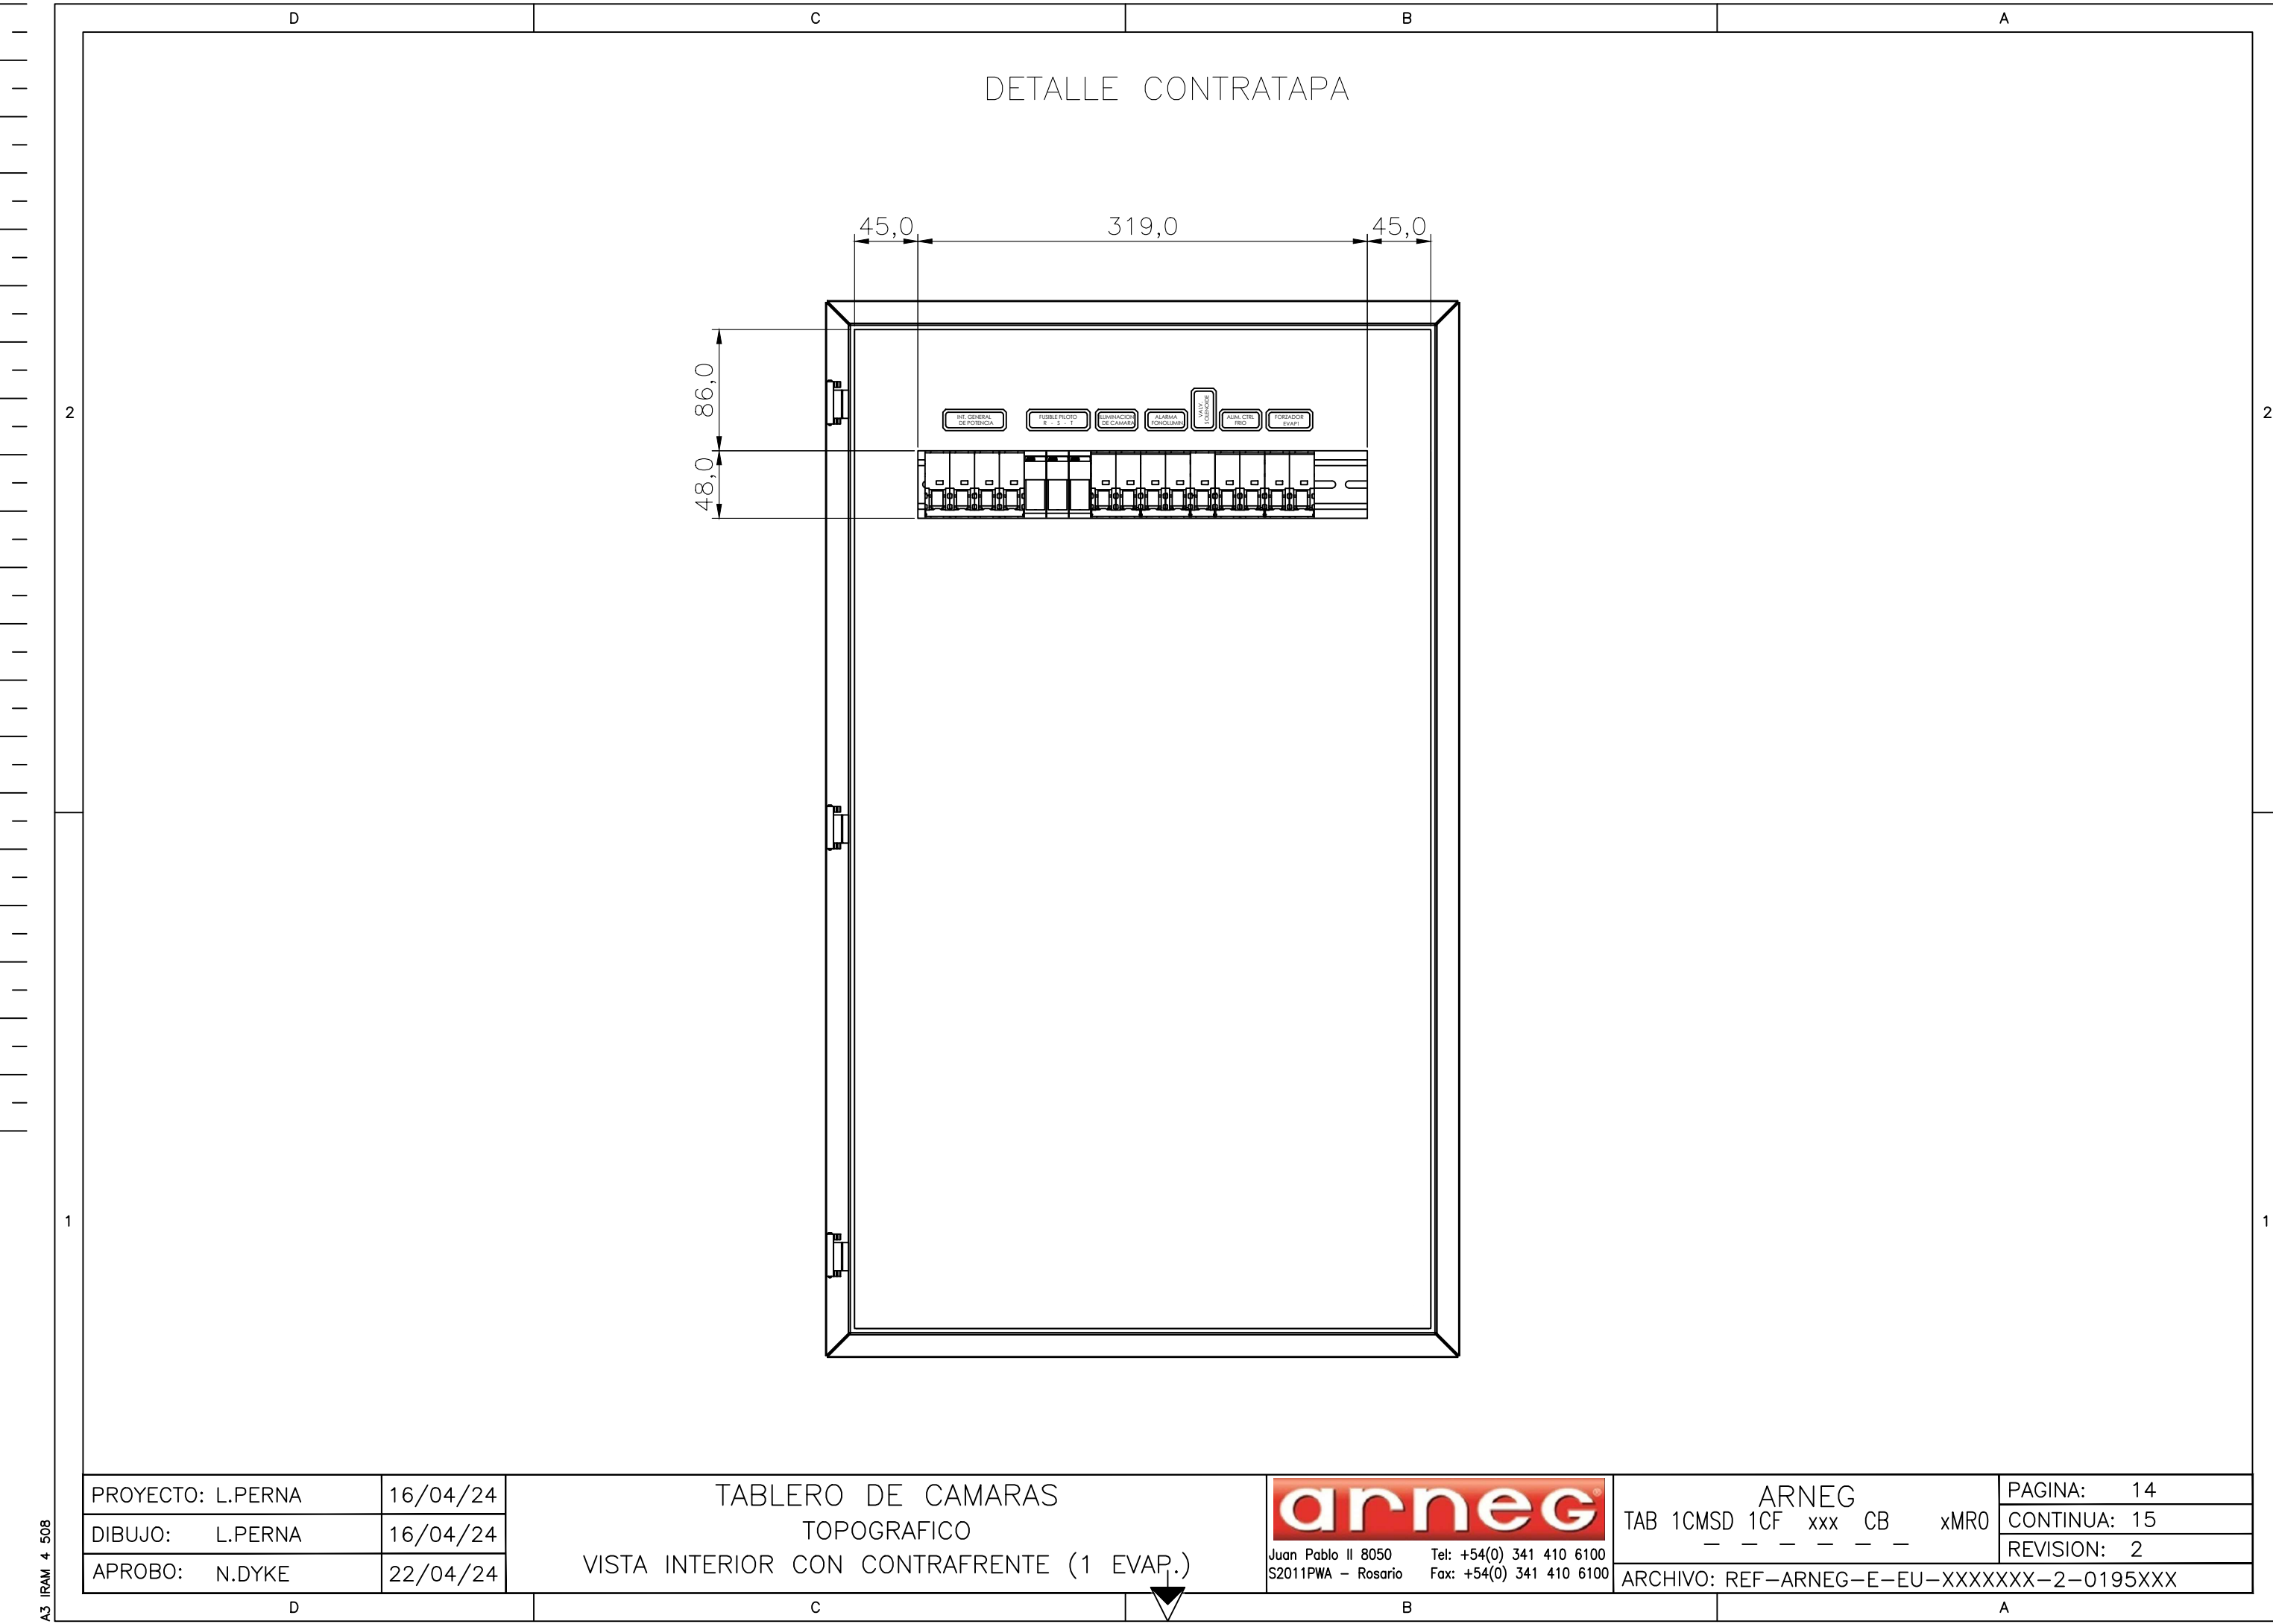


DETALLE CONTRATAPA

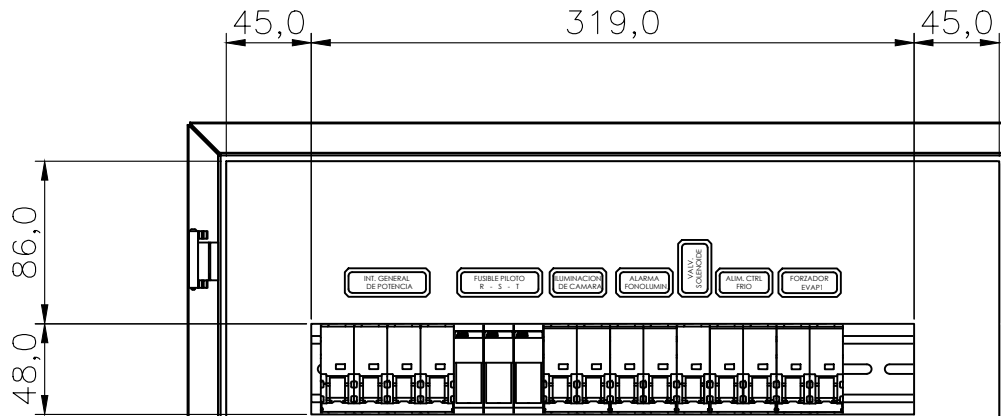


DETALLE CONTRATAPA

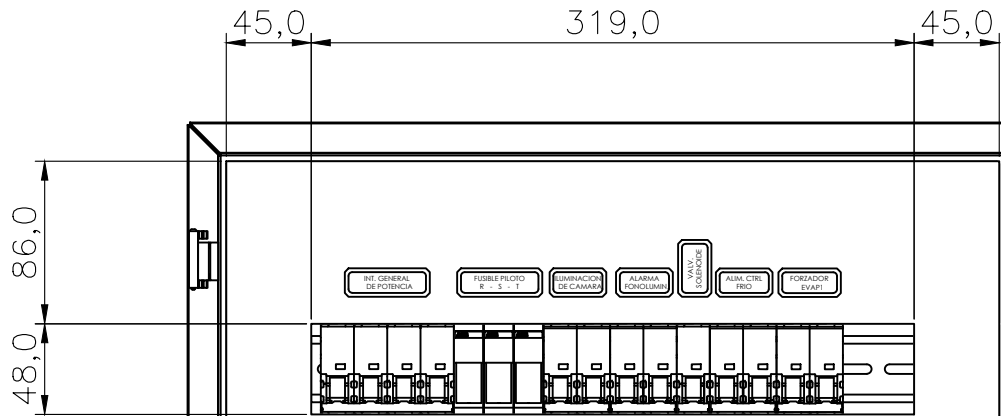


DETALLE CONTRATAPA

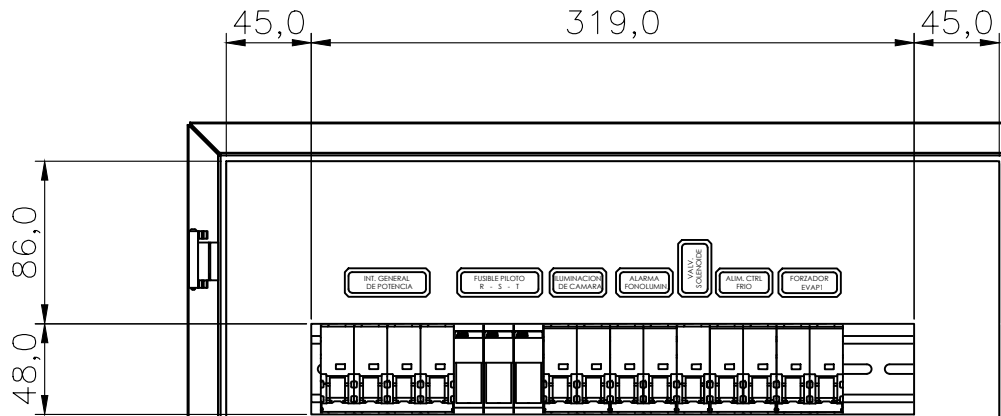


DETALLE CONTRATAPA

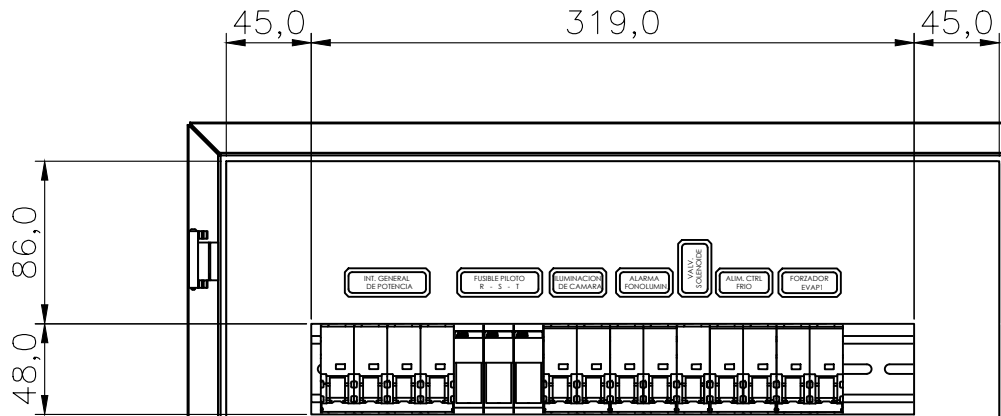


DETALLE CONTRATAPA

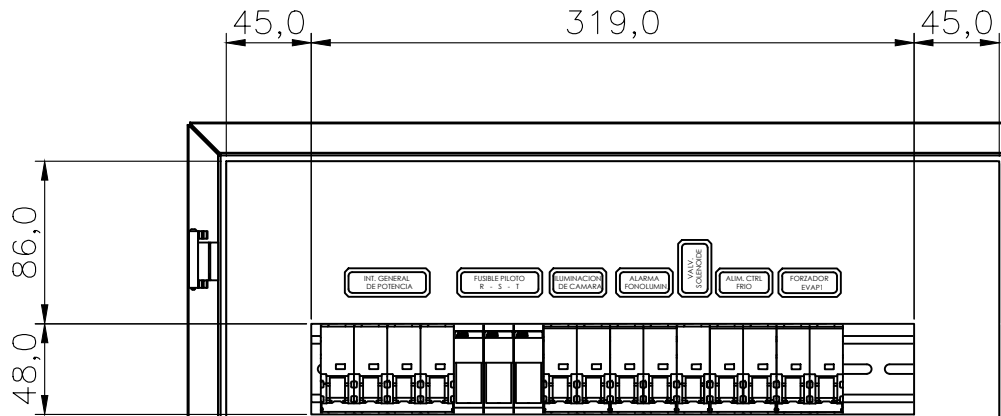


DETALLE CONTRATAPA

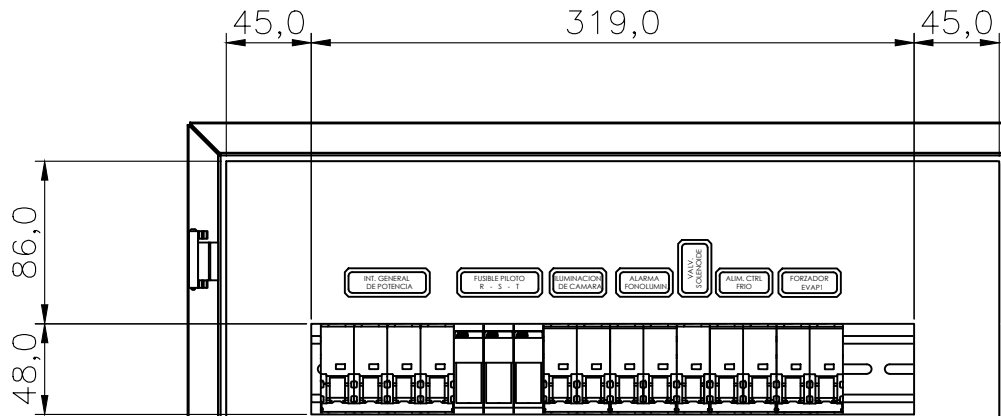


DETALLE CONTRATAPA

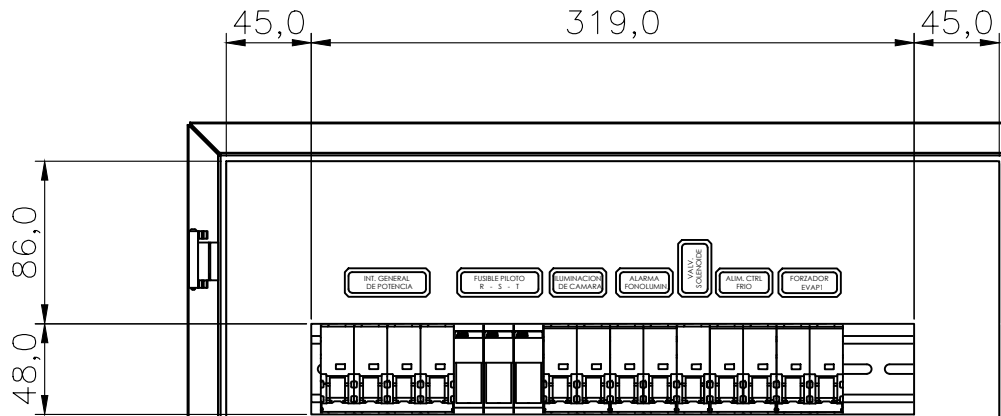


DETALLE CONTRATAPA

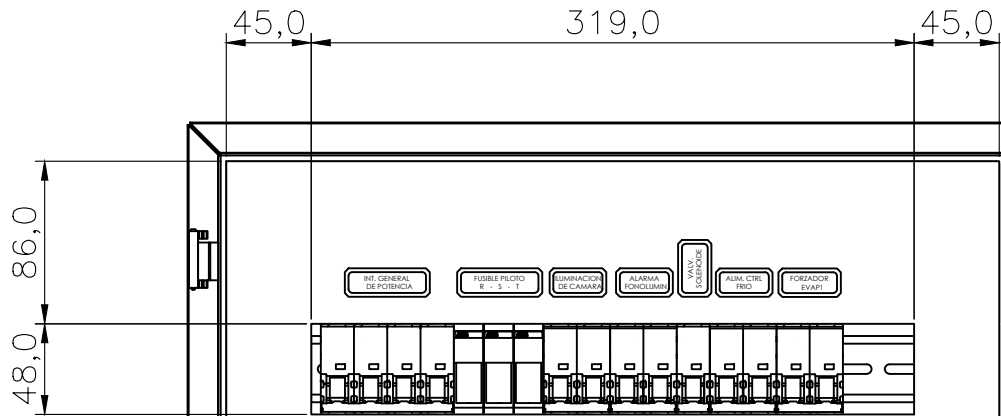


DETALLE CONTRATAPA

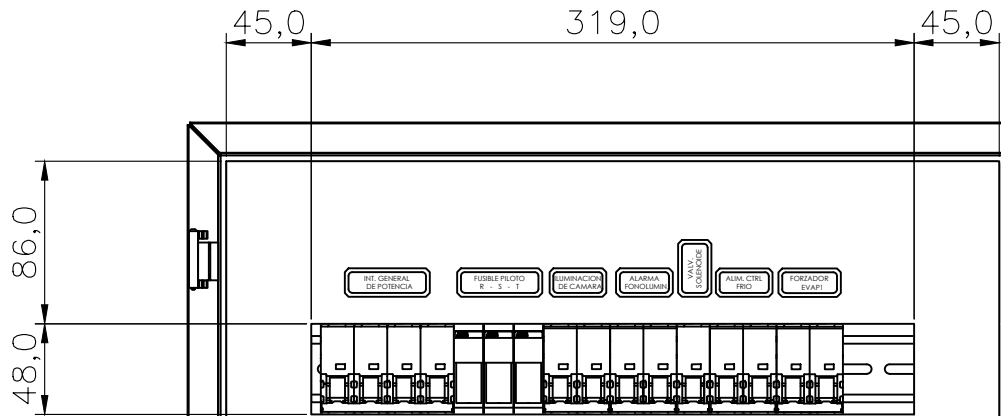


DETALLE CONTRATAPA

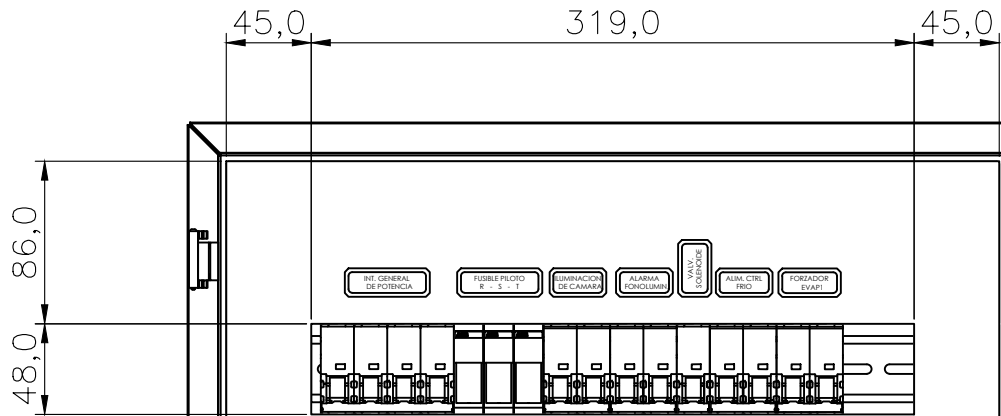


DETALLE CONTRATAPA

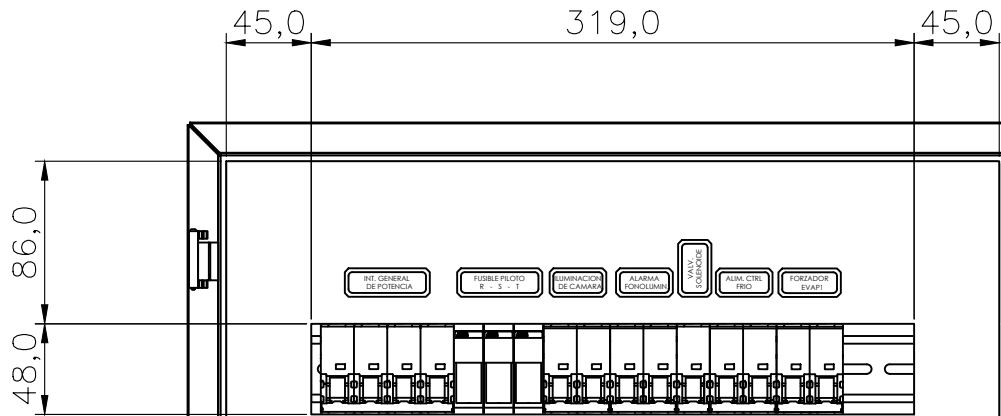


DETALLE CONTRATAPA

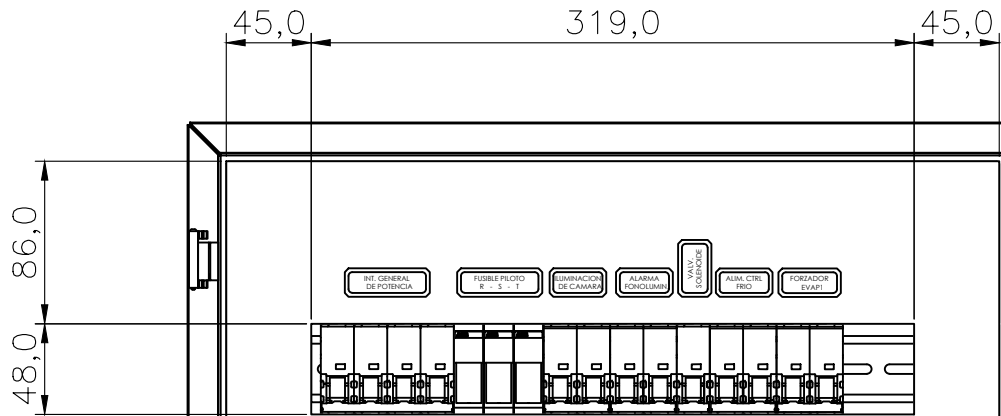


DETALLE CONTRATAPA

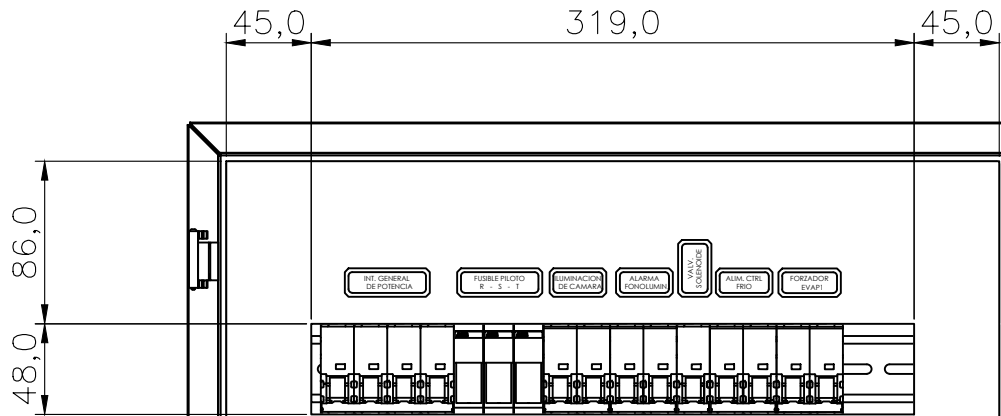


DETALLE CONTRATAPA

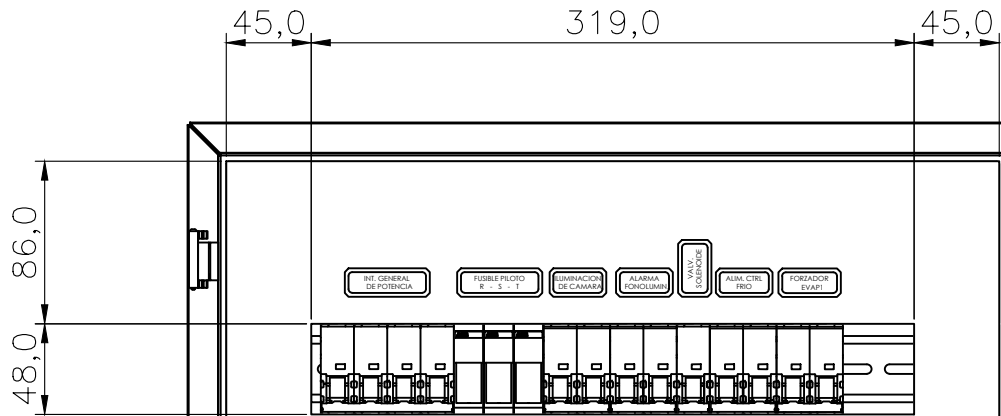


DETALLE CONTRATAPA

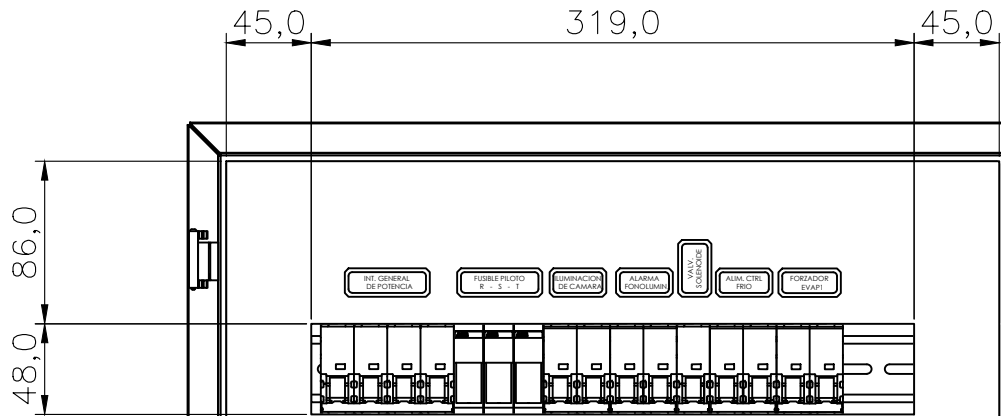


DETALLE CONTRATAPA

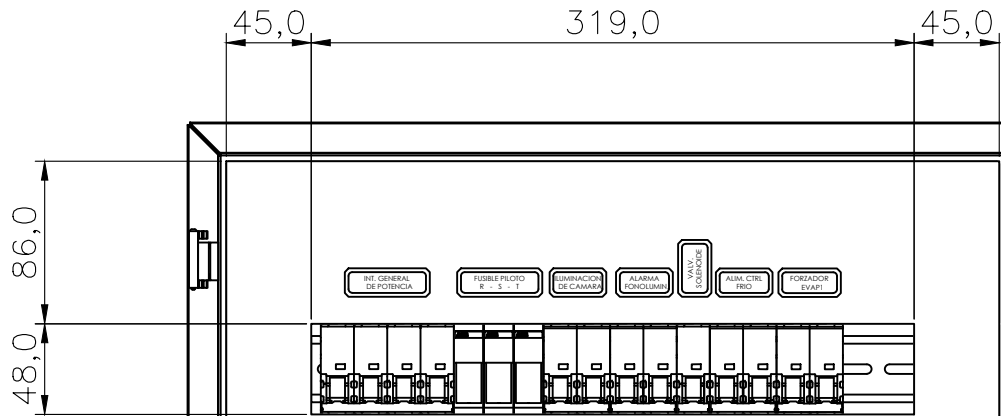


DETALLE CONTRATAPA

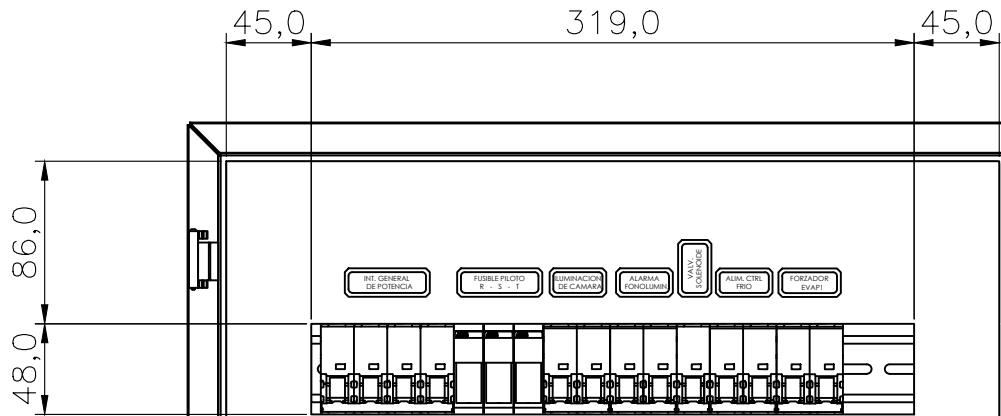


DETALLE CONTRATAPA

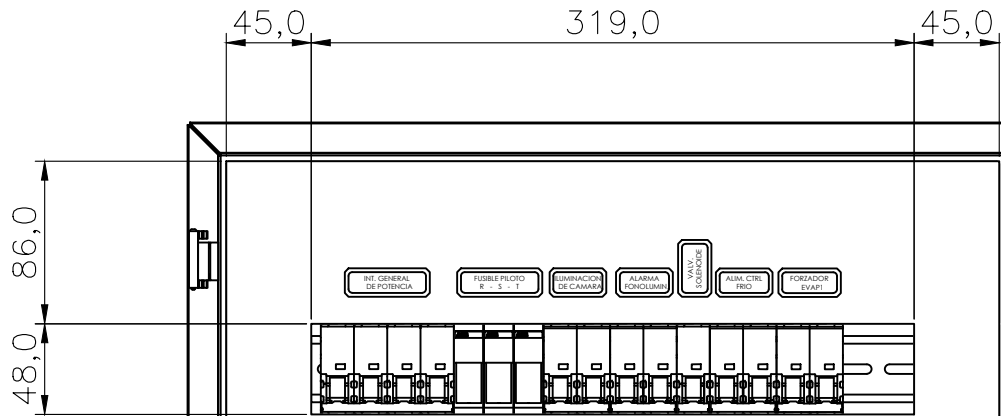


DETALLE CONTRATAPA

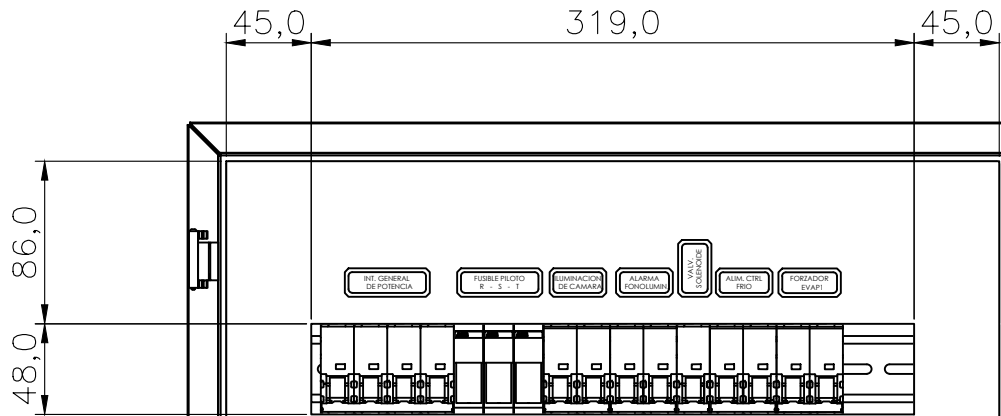


DETALLE CONTRATAPA

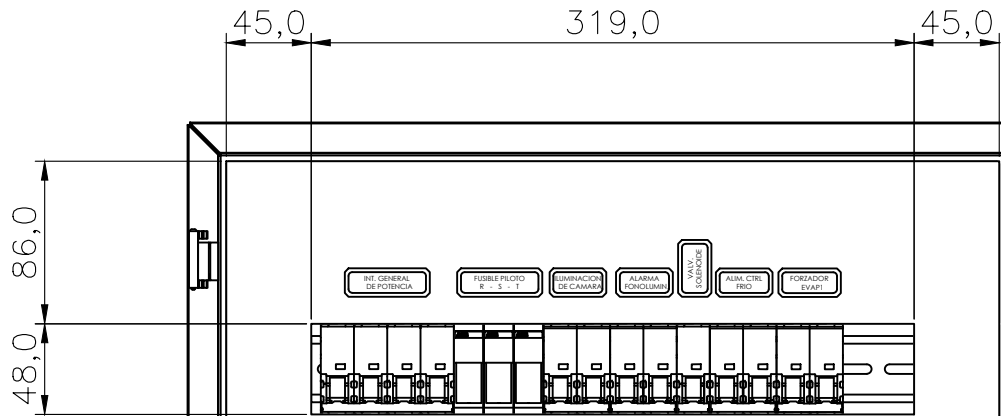


DETALLE CONTRATAPA

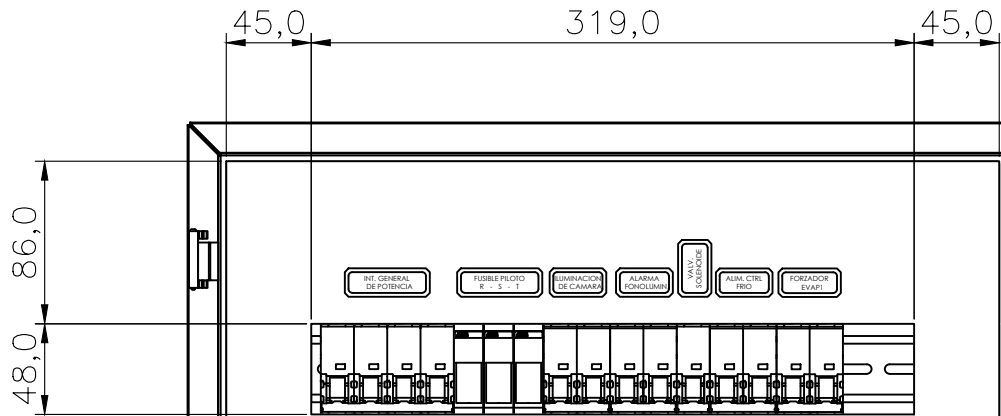


DETALLE CONTRATAPA

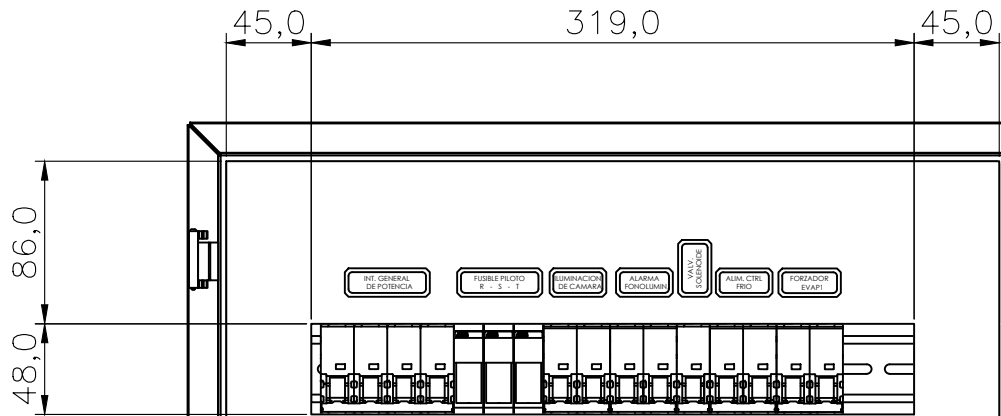


DETALLE CONTRATAPA

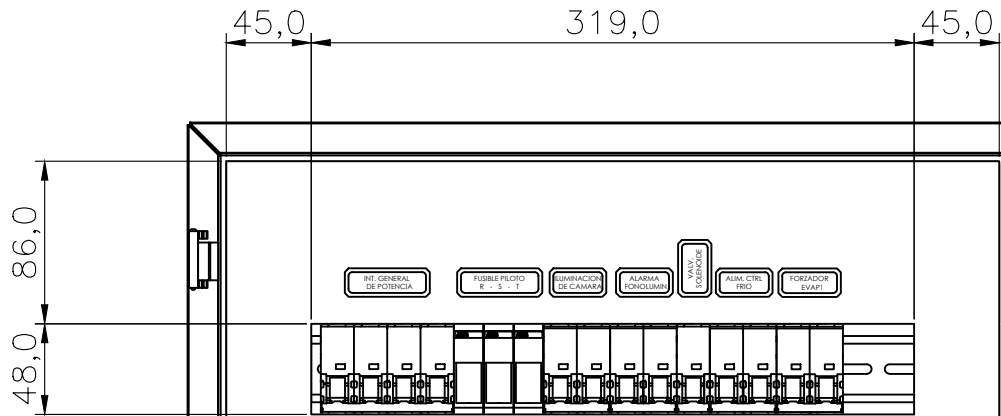


DETALLE CONTRATAPA

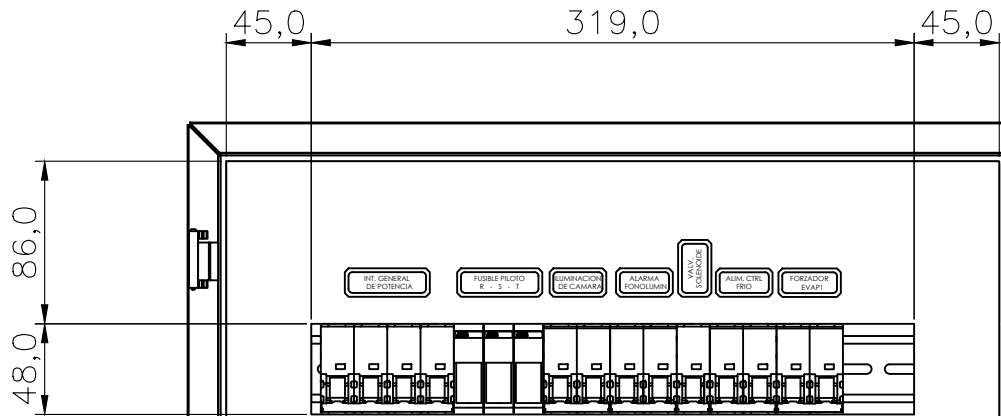


DETALLE CONTRATAPA

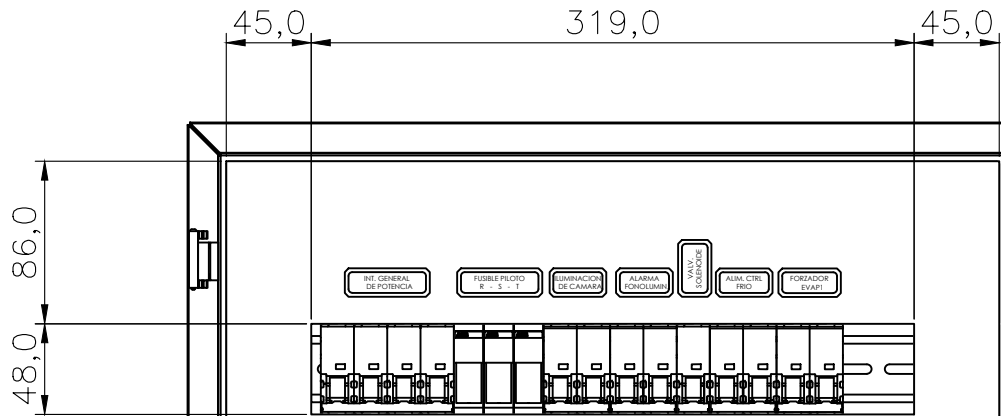


DETALLE CONTRATAPA

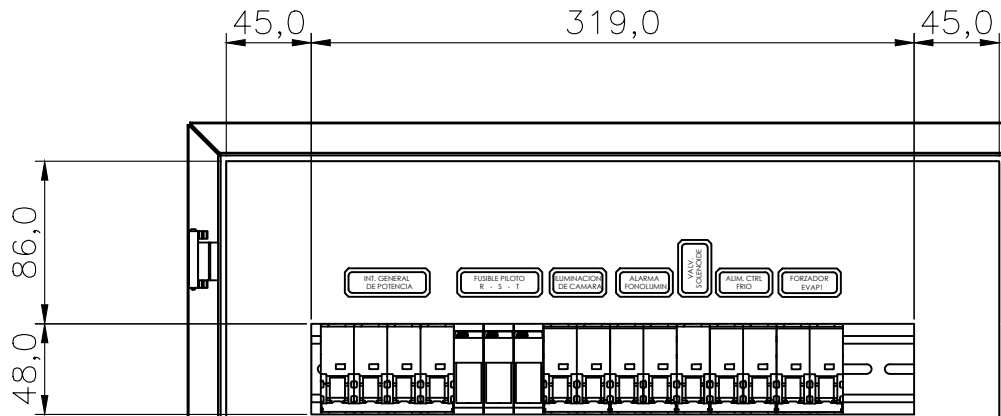


DETALLE CONTRATAPA

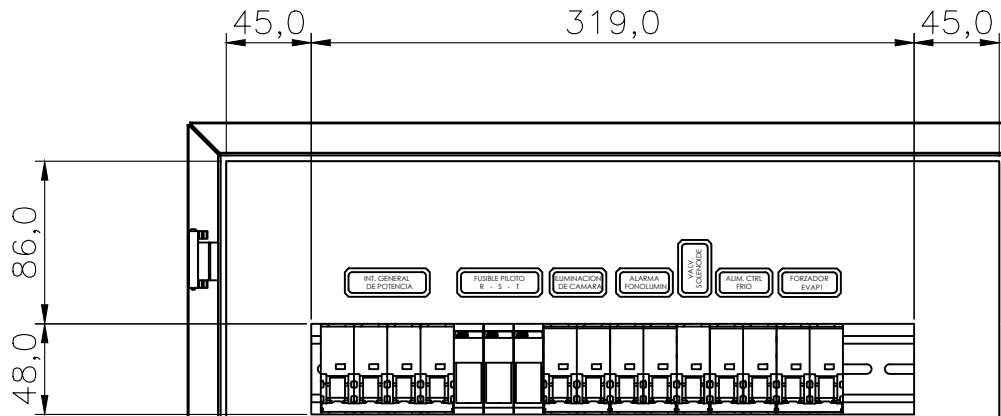


DETALLE CONTRATAPA

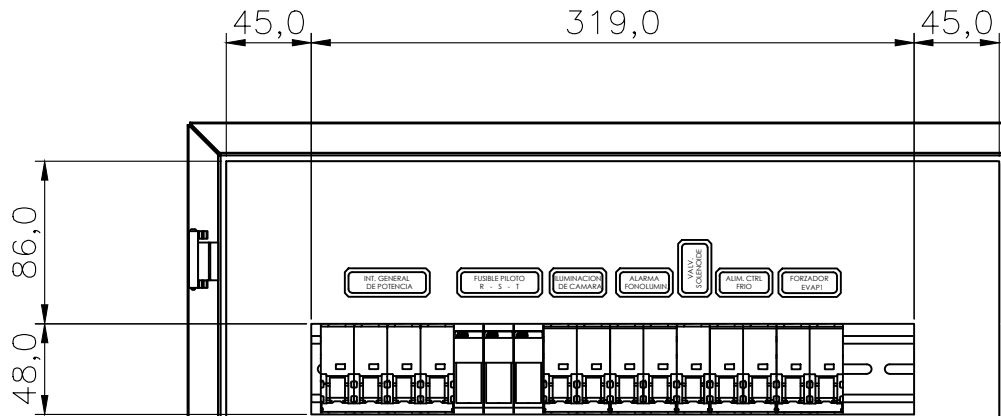


DETALLE CONTRATAPA

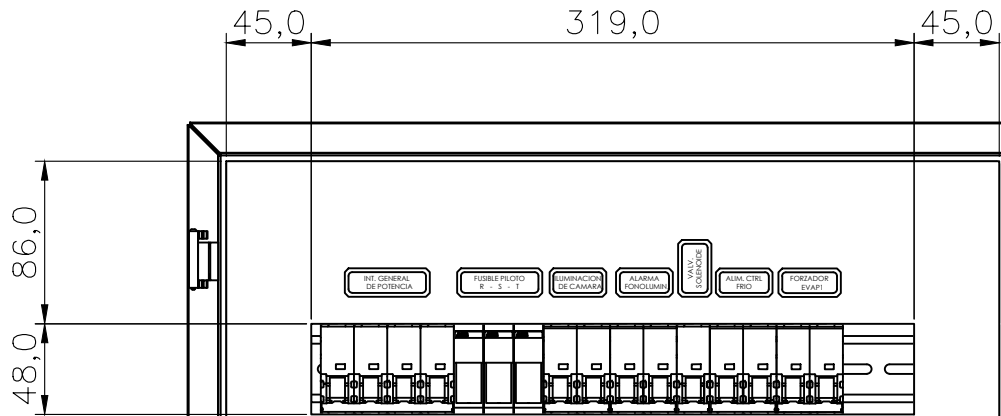


DETALLE CONTRATAPA

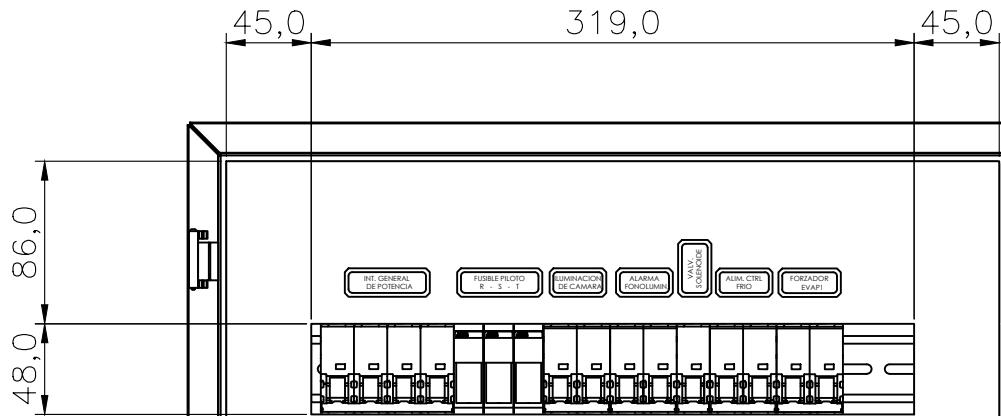


DETALLE CONTRATAPA

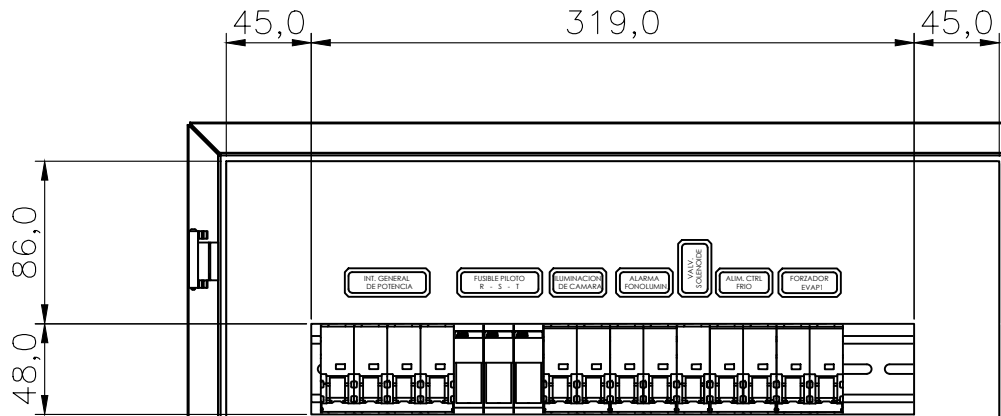


DETALLE CONTRATAPA

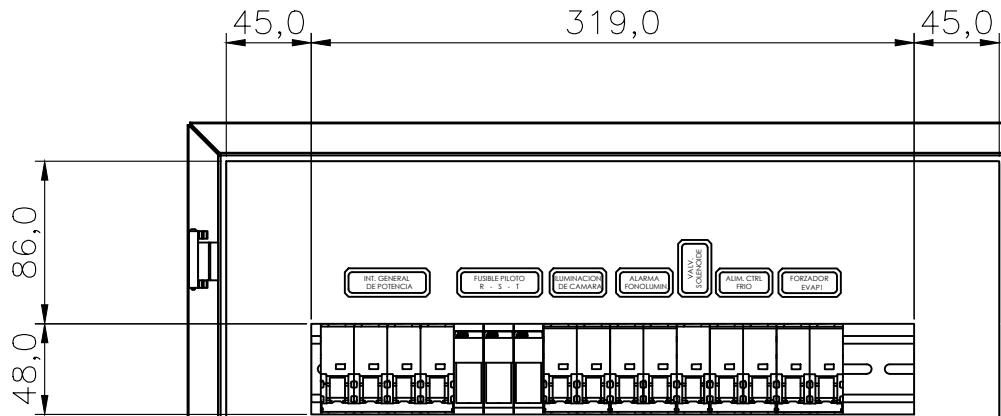


DETALLE CONTRATAPA

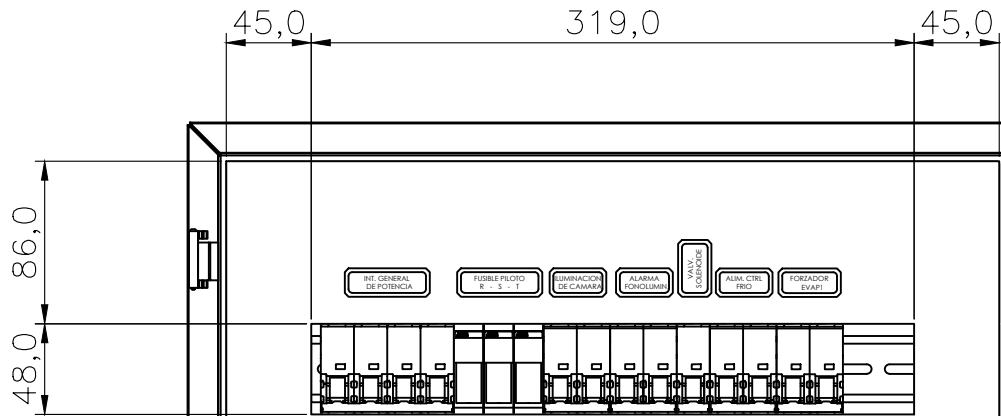


DETALLE CONTRATAPA

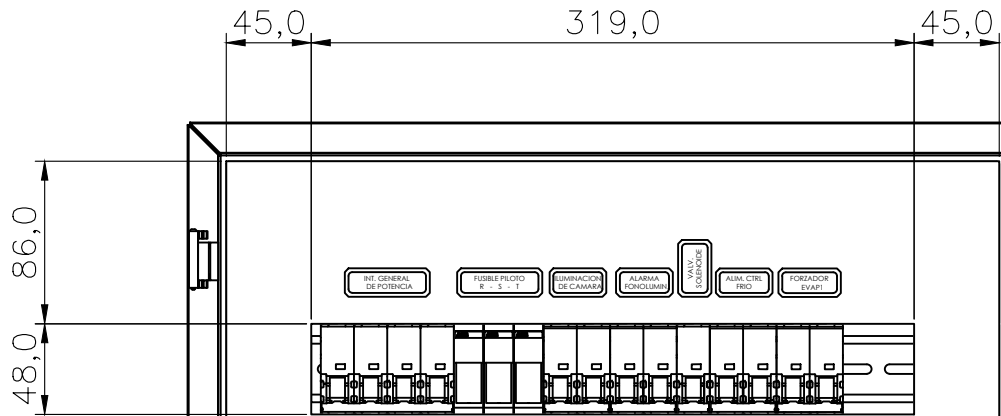


DETALLE CONTRATAPA

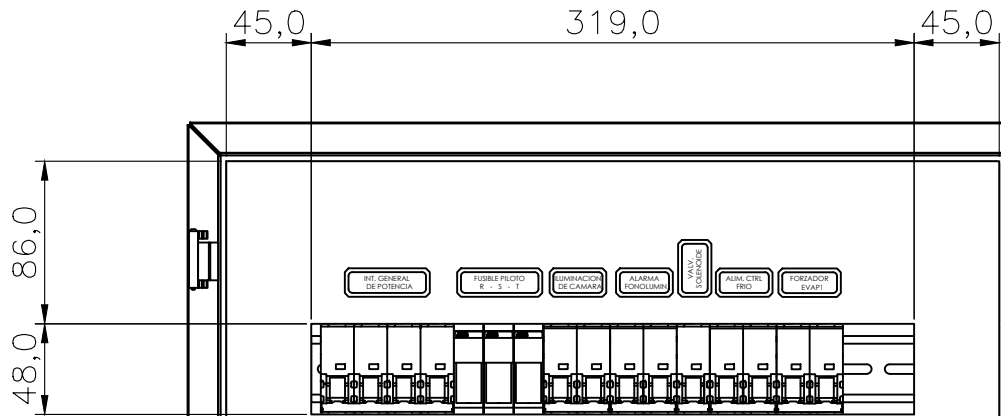


DETALLE CONTRATAPA

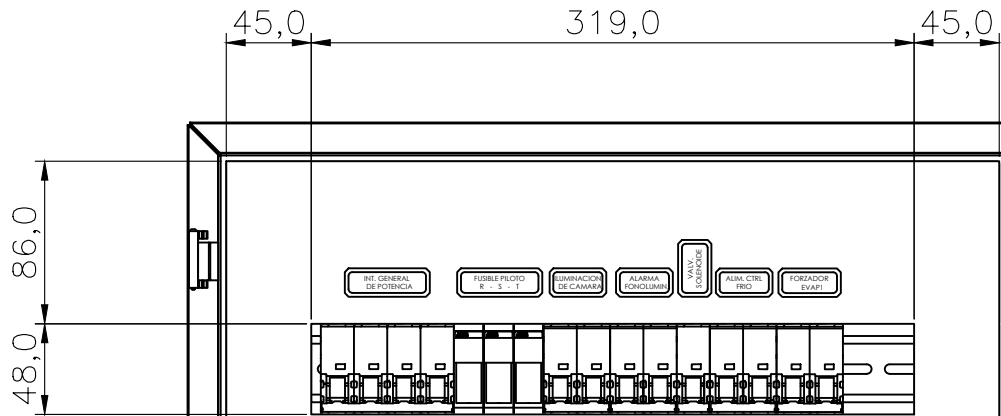


DETALLE CONTRATAPA

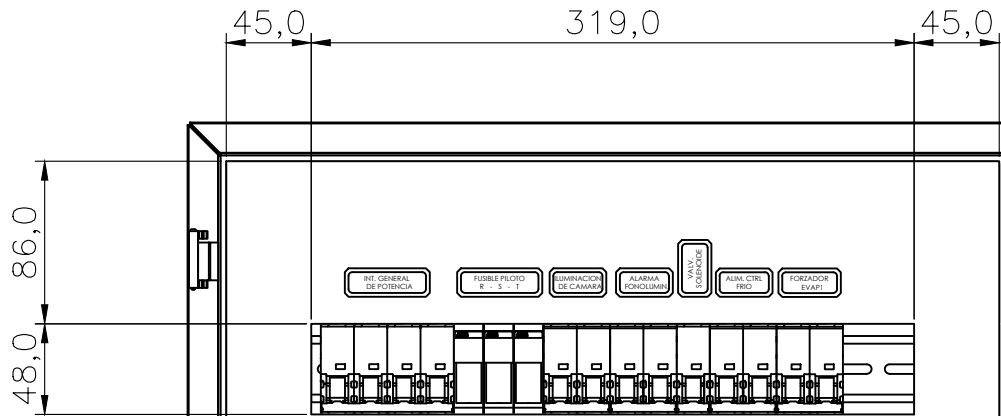


DETALLE CONTRATAPA

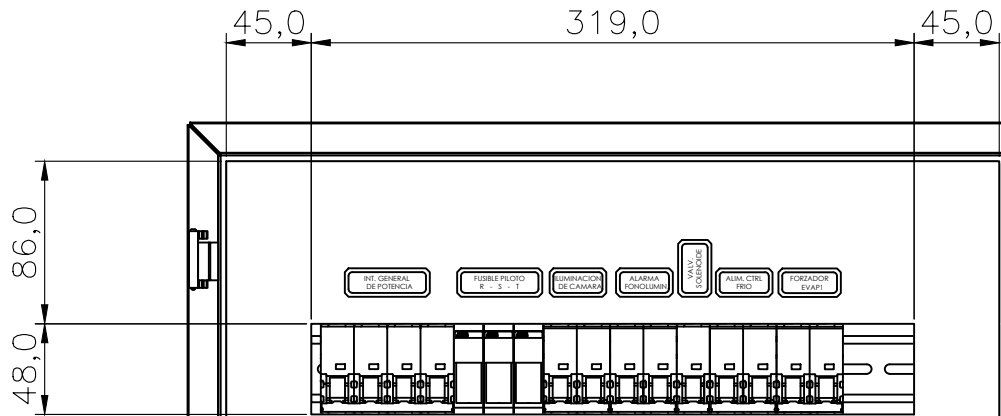


DETALLE CONTRATAPA

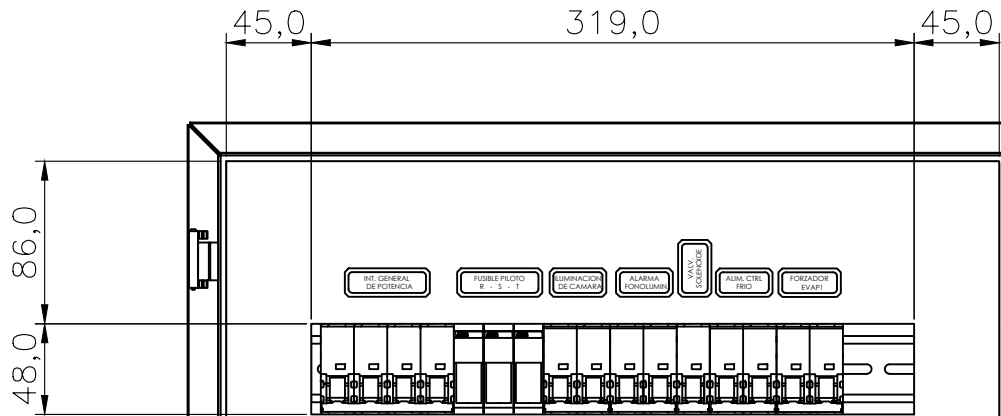


DETALLE CONTRATAPA

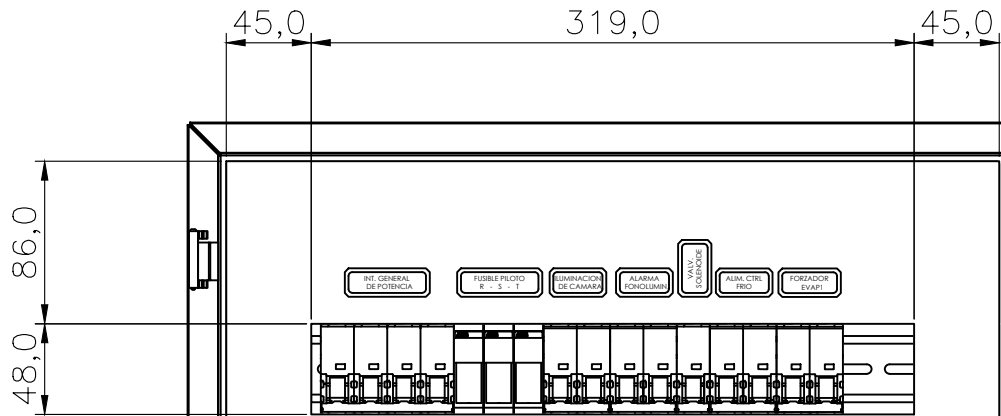


DETALLE CONTRATAPA

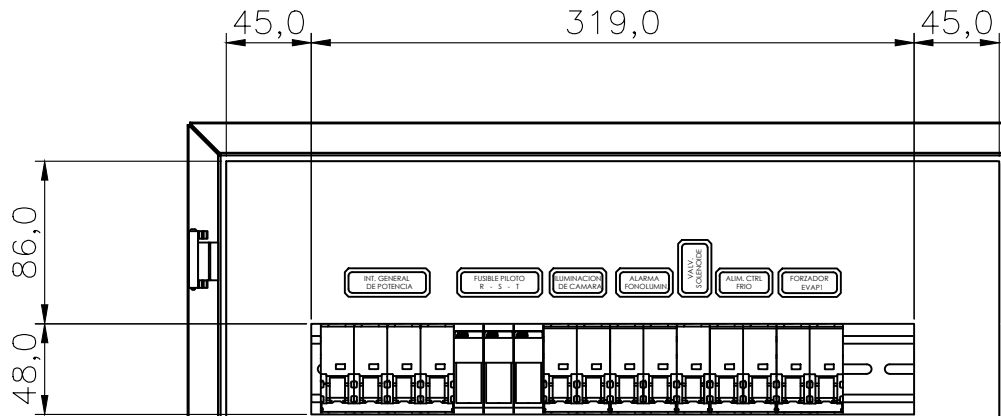


DETALLE CONTRATAPA

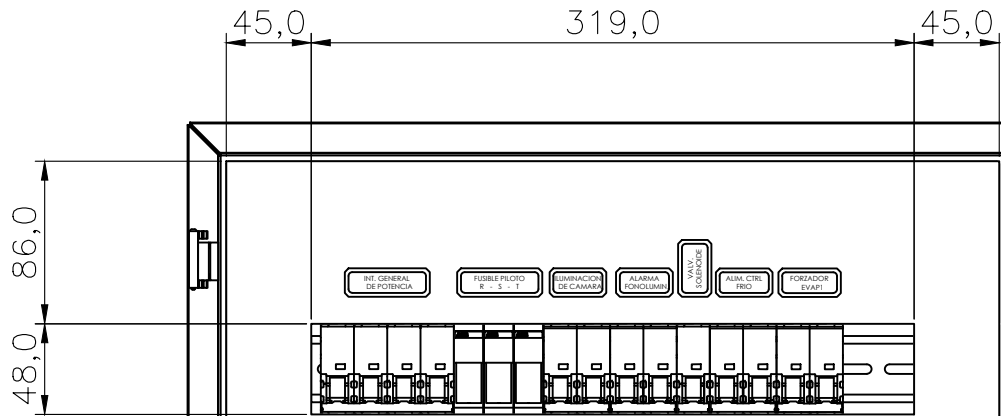


DETALLE CONTRATAPA

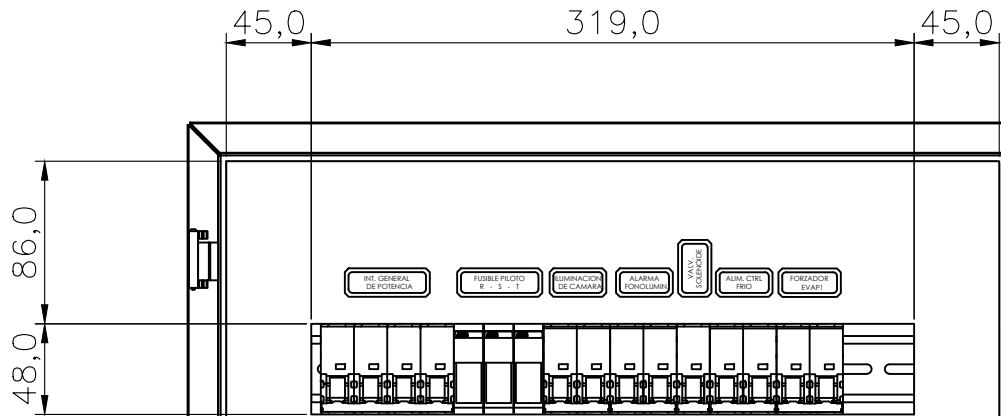


DETALLE CONTRATAPA

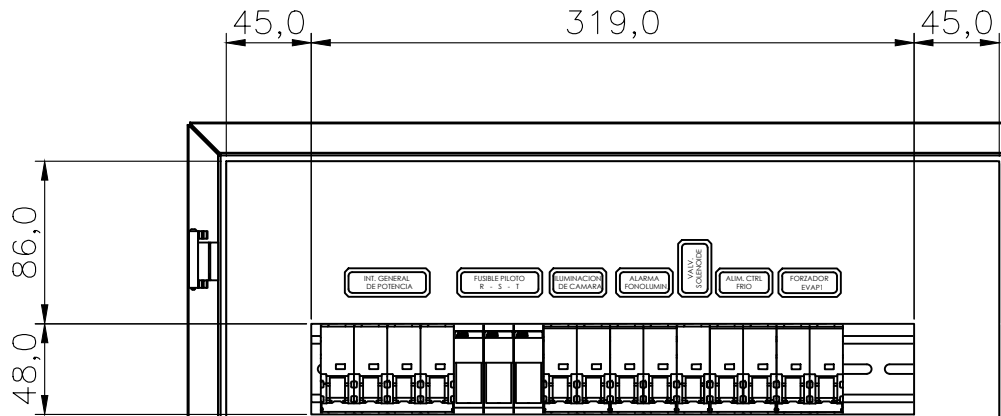


DETALLE CONTRATAPA

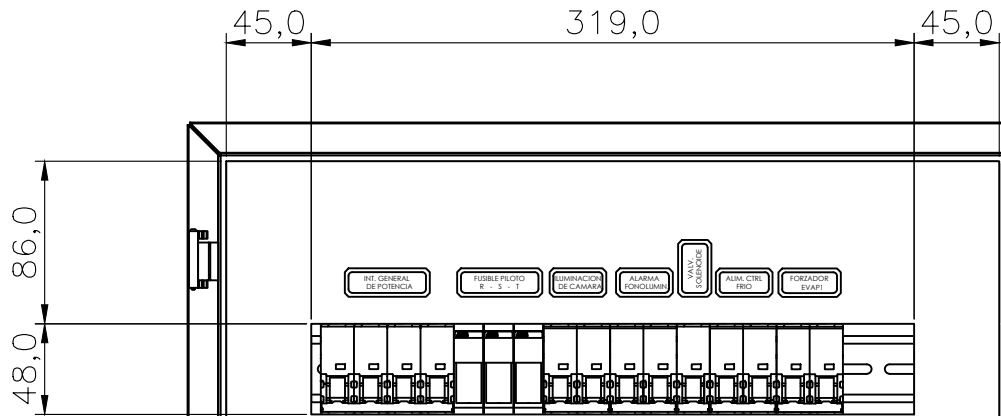


DETALLE CONTRATAPA

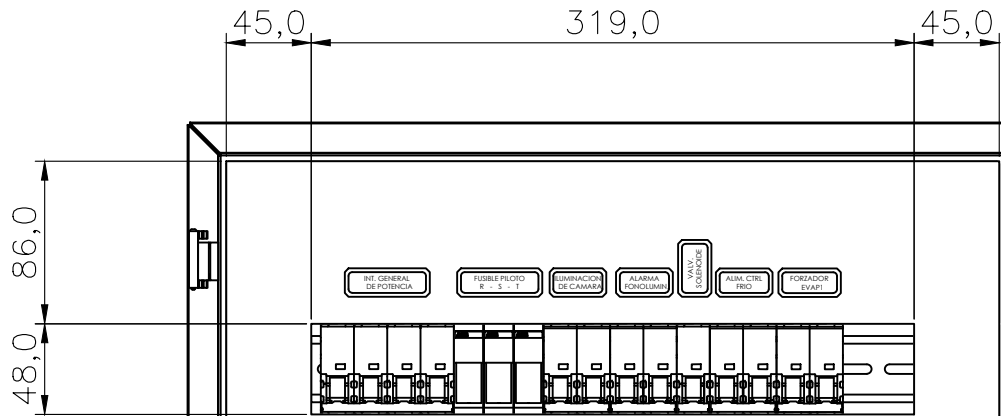


DETALLE CONTRATAPA

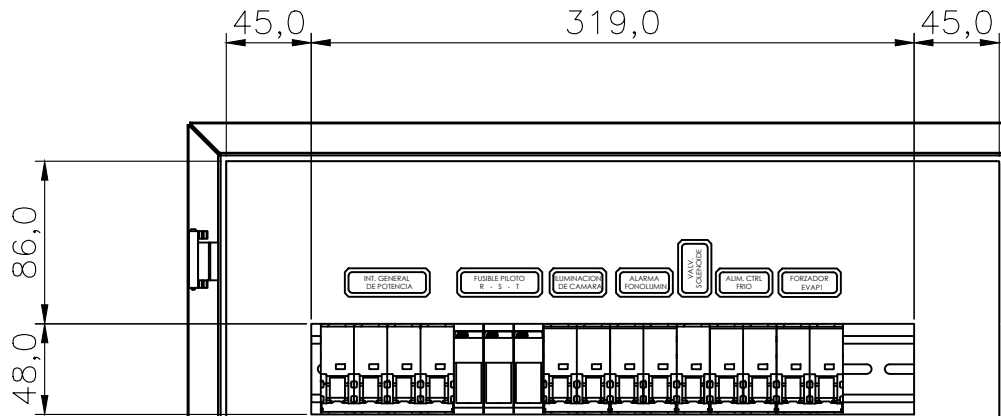


DETALLE CONTRATAPA

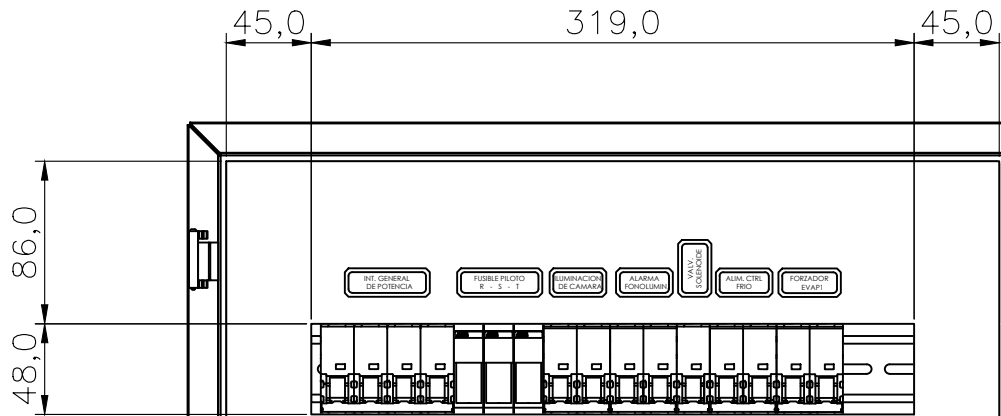


DETALLE CONTRATAPA

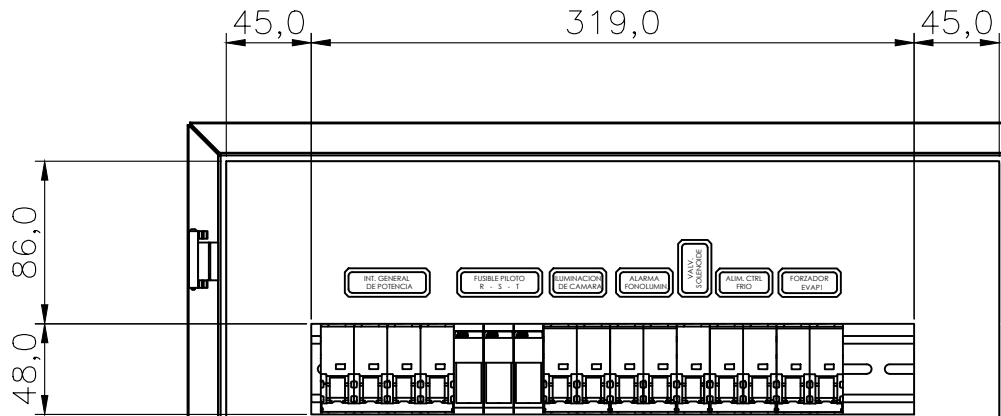


DETALLE CONTRATAPA

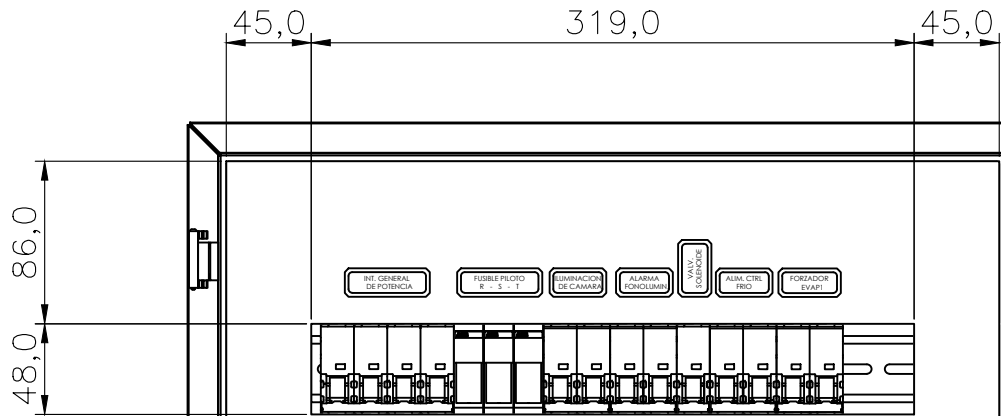


DETALLE CONTRATAPA

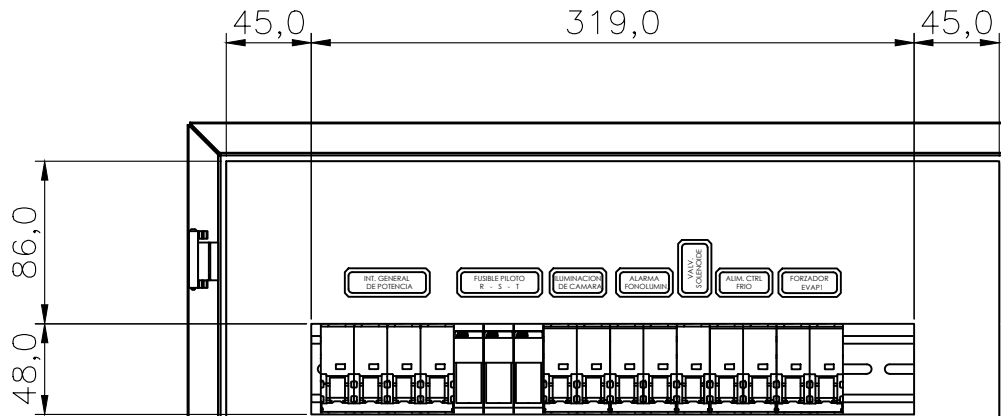


DETALLE CONTRATAPA

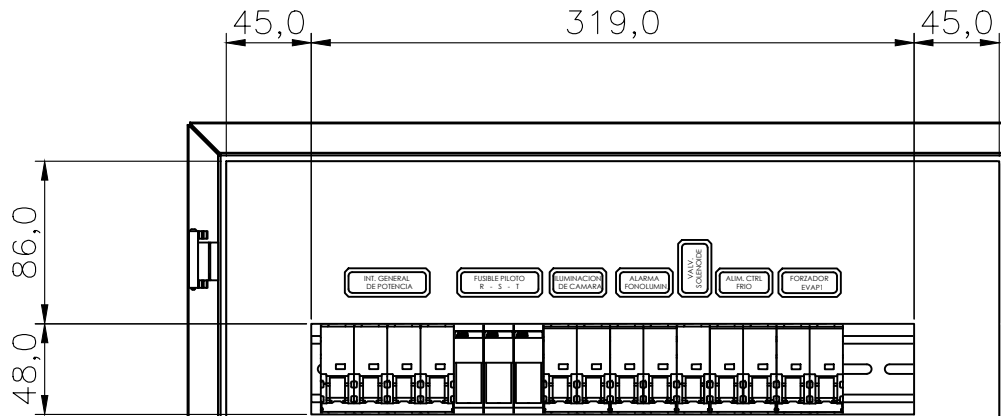


DETALLE CONTRATAPA

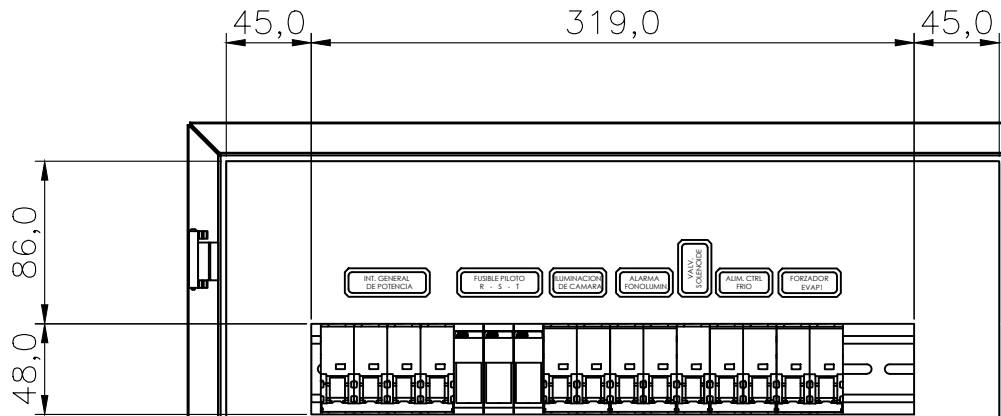


DETALLE CONTRATAPA

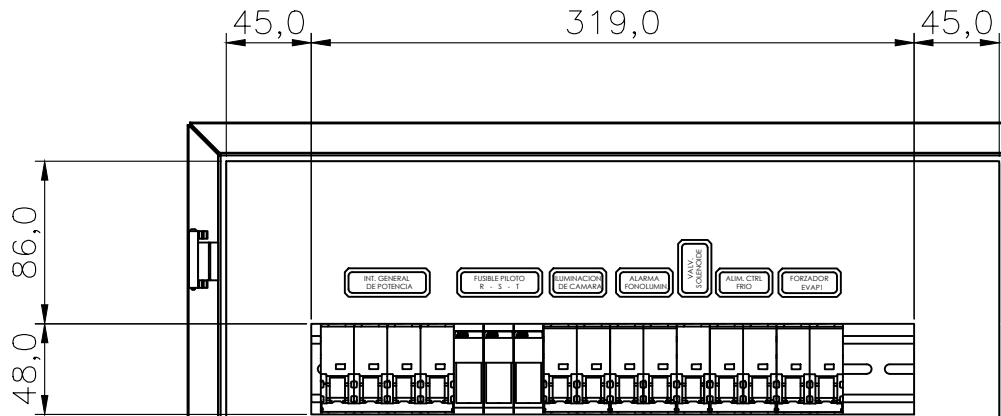


DETALLE CONTRATAPA

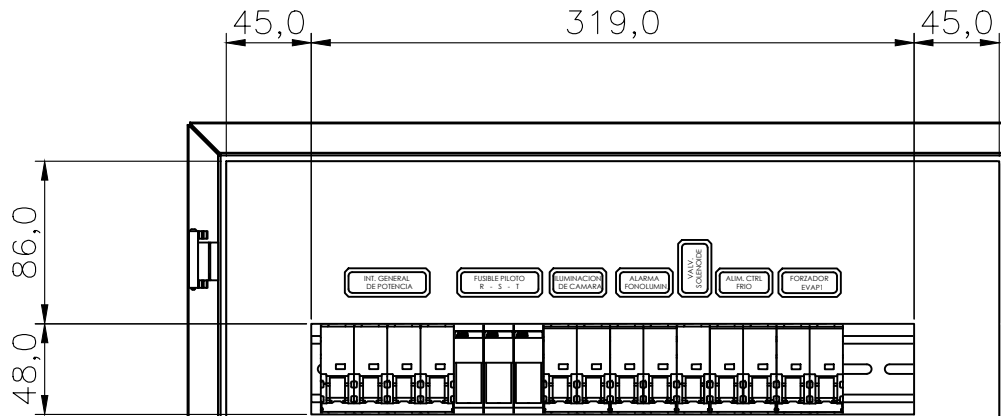


DETALLE CONTRATAPA

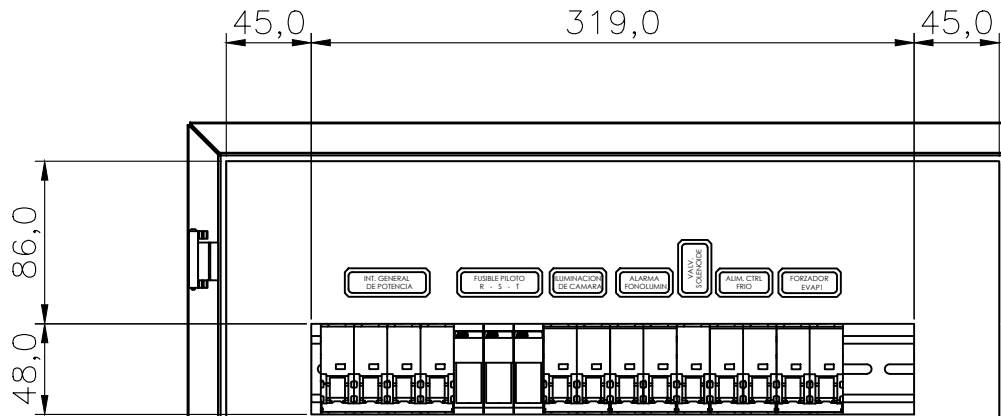


DETALLE CONTRATAPA

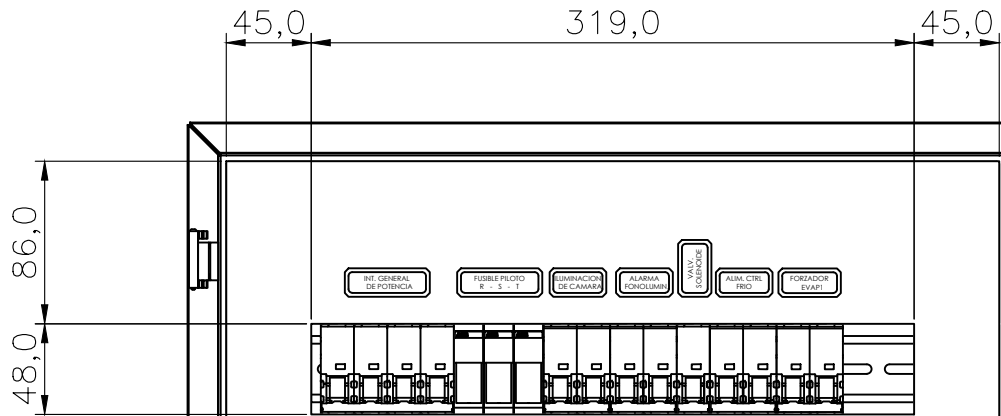


DETALLE CONTRATAPA

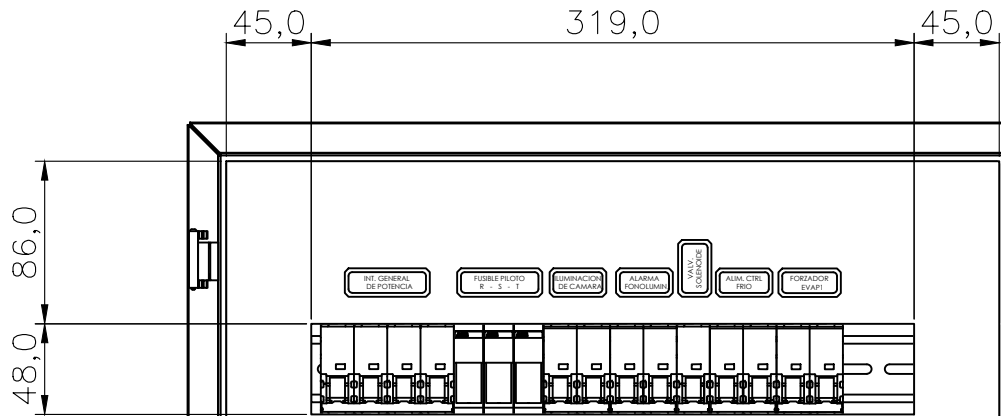


DETALLE CONTRATAPA

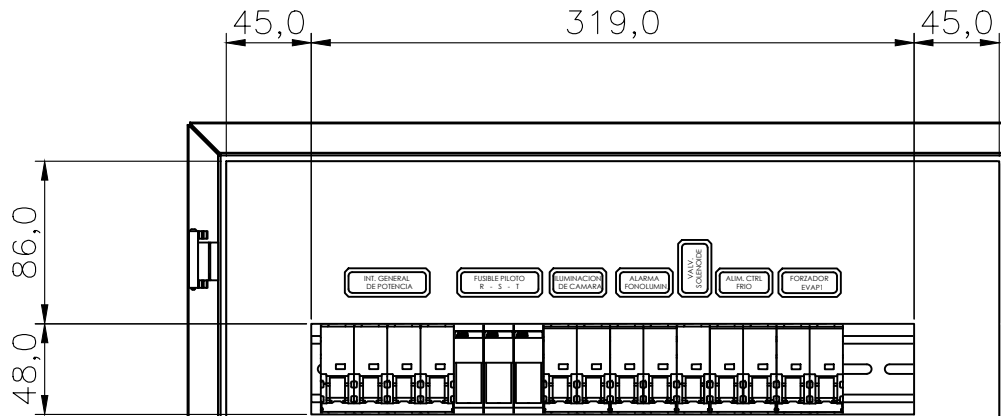


DETALLE CONTRATAPA

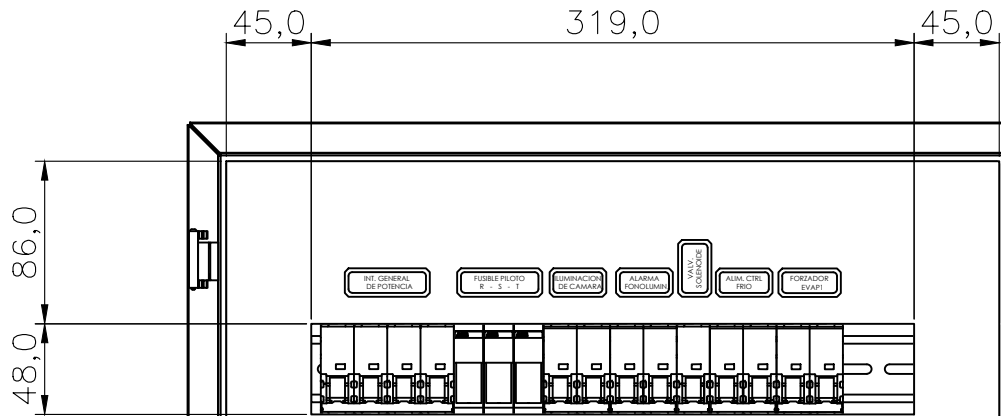


DETALLE CONTRATAPA

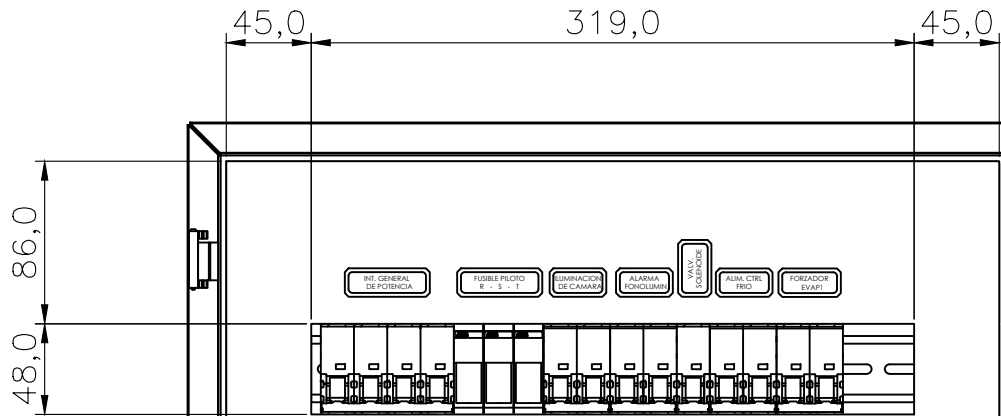


DETALLE CONTRATAPA

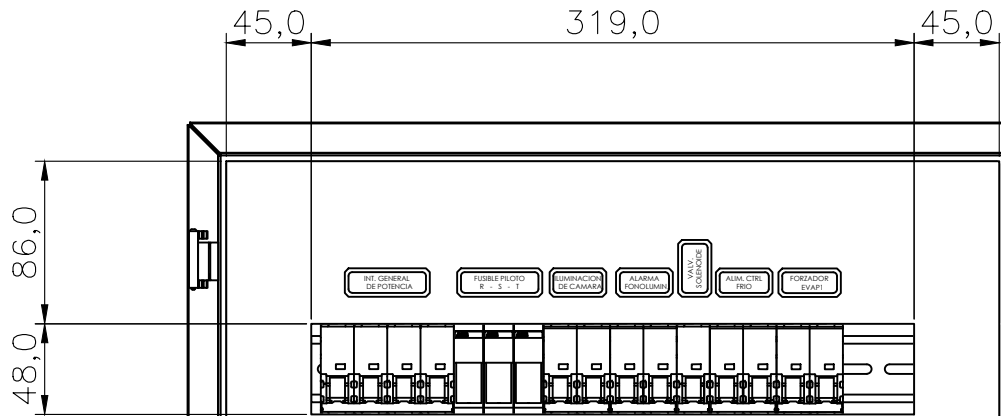


DETALLE CONTRATAPA

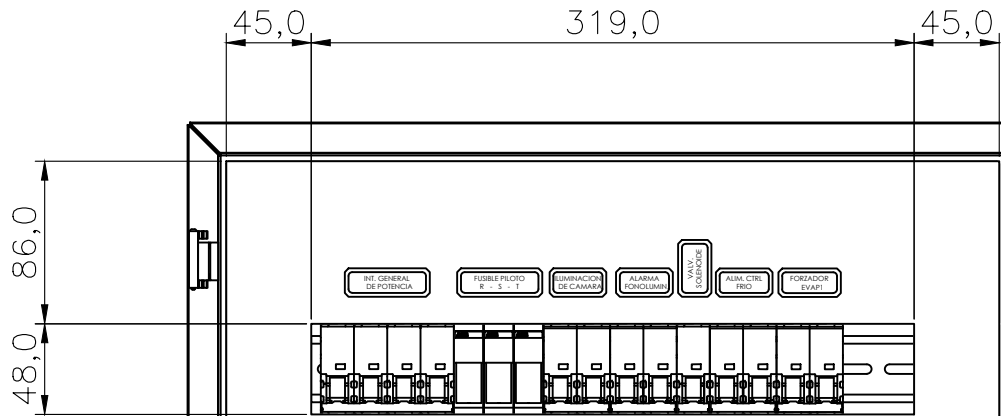


DETALLE CONTRATAPA

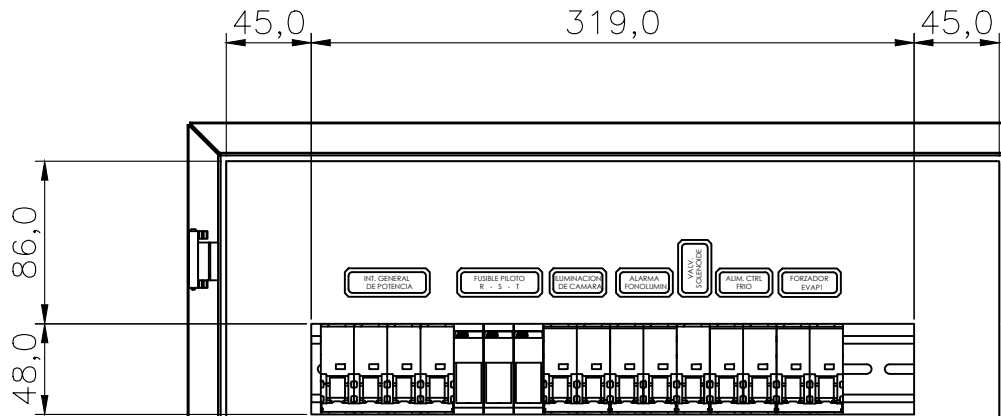


DETALLE CONTRATAPA

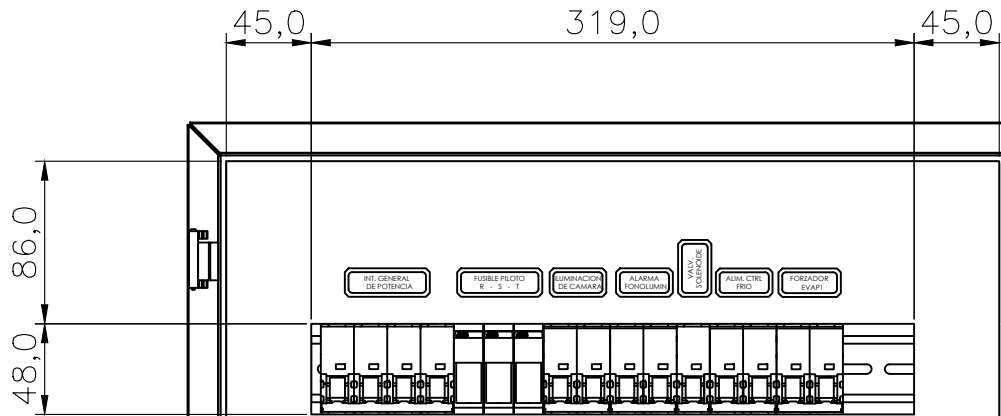


DETALLE CONTRATAPA

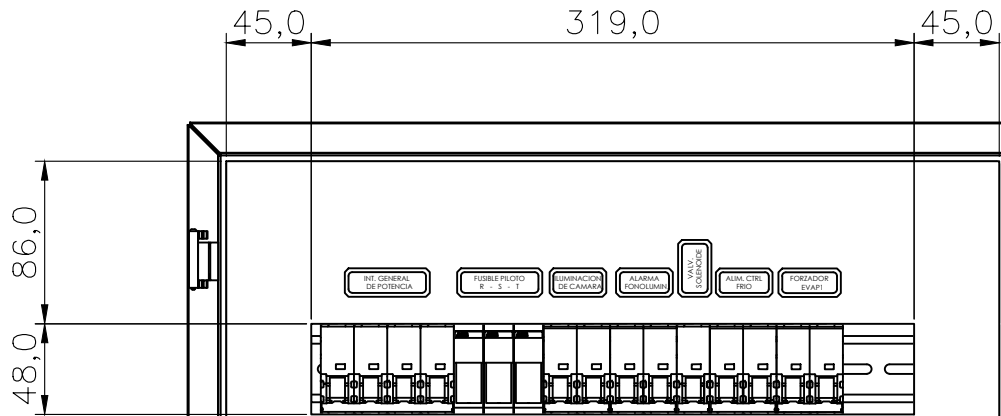


DETALLE CONTRATAPA

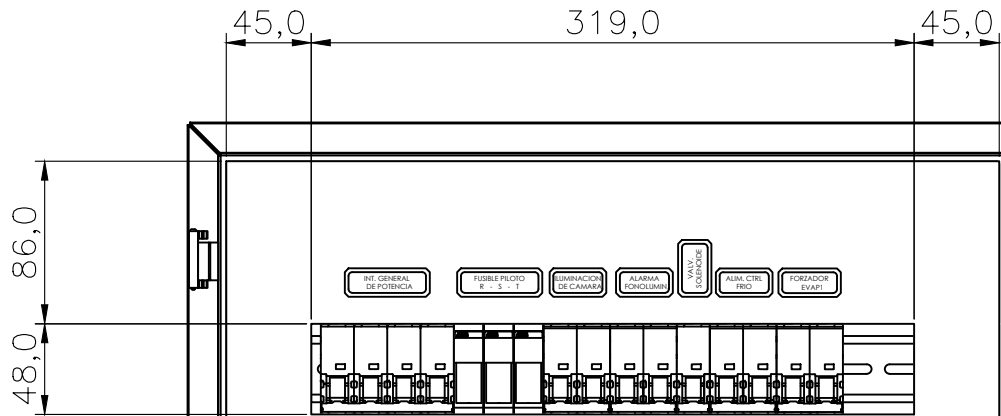


DETALLE CONTRATAPA

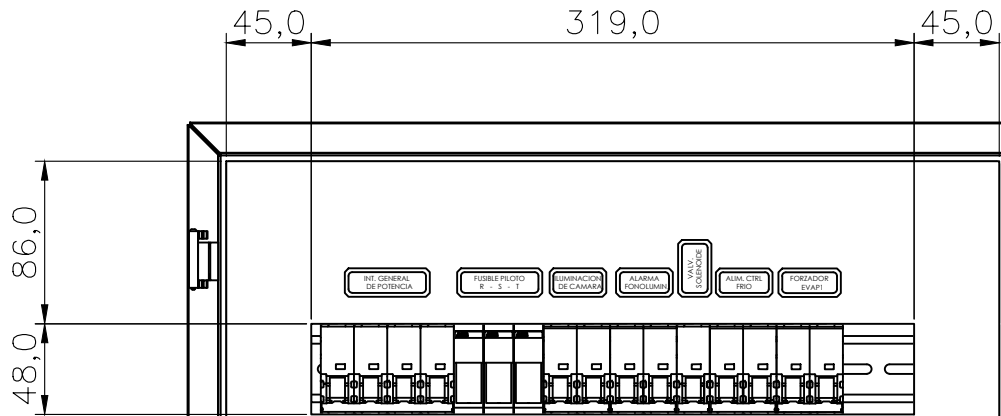


DETALLE CONTRATAPA

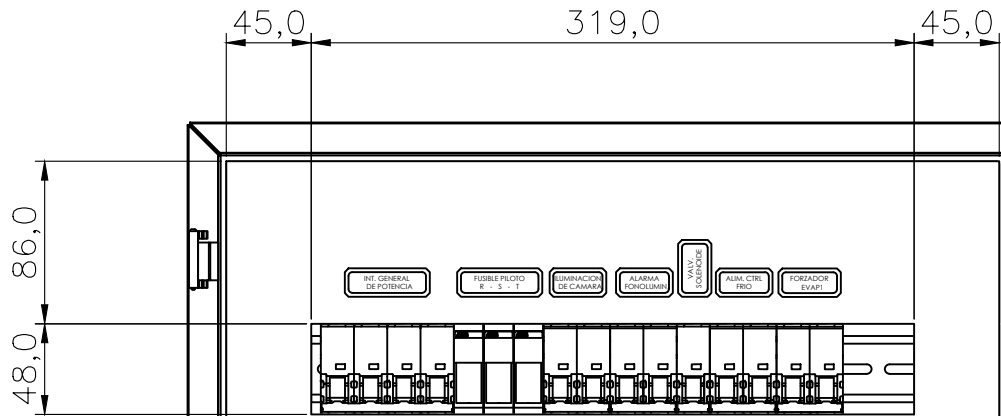

DETALLE CONTRATAPA

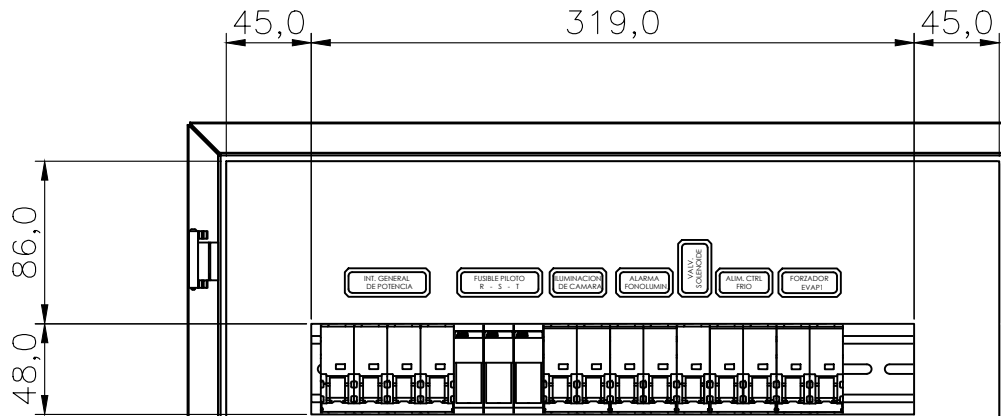

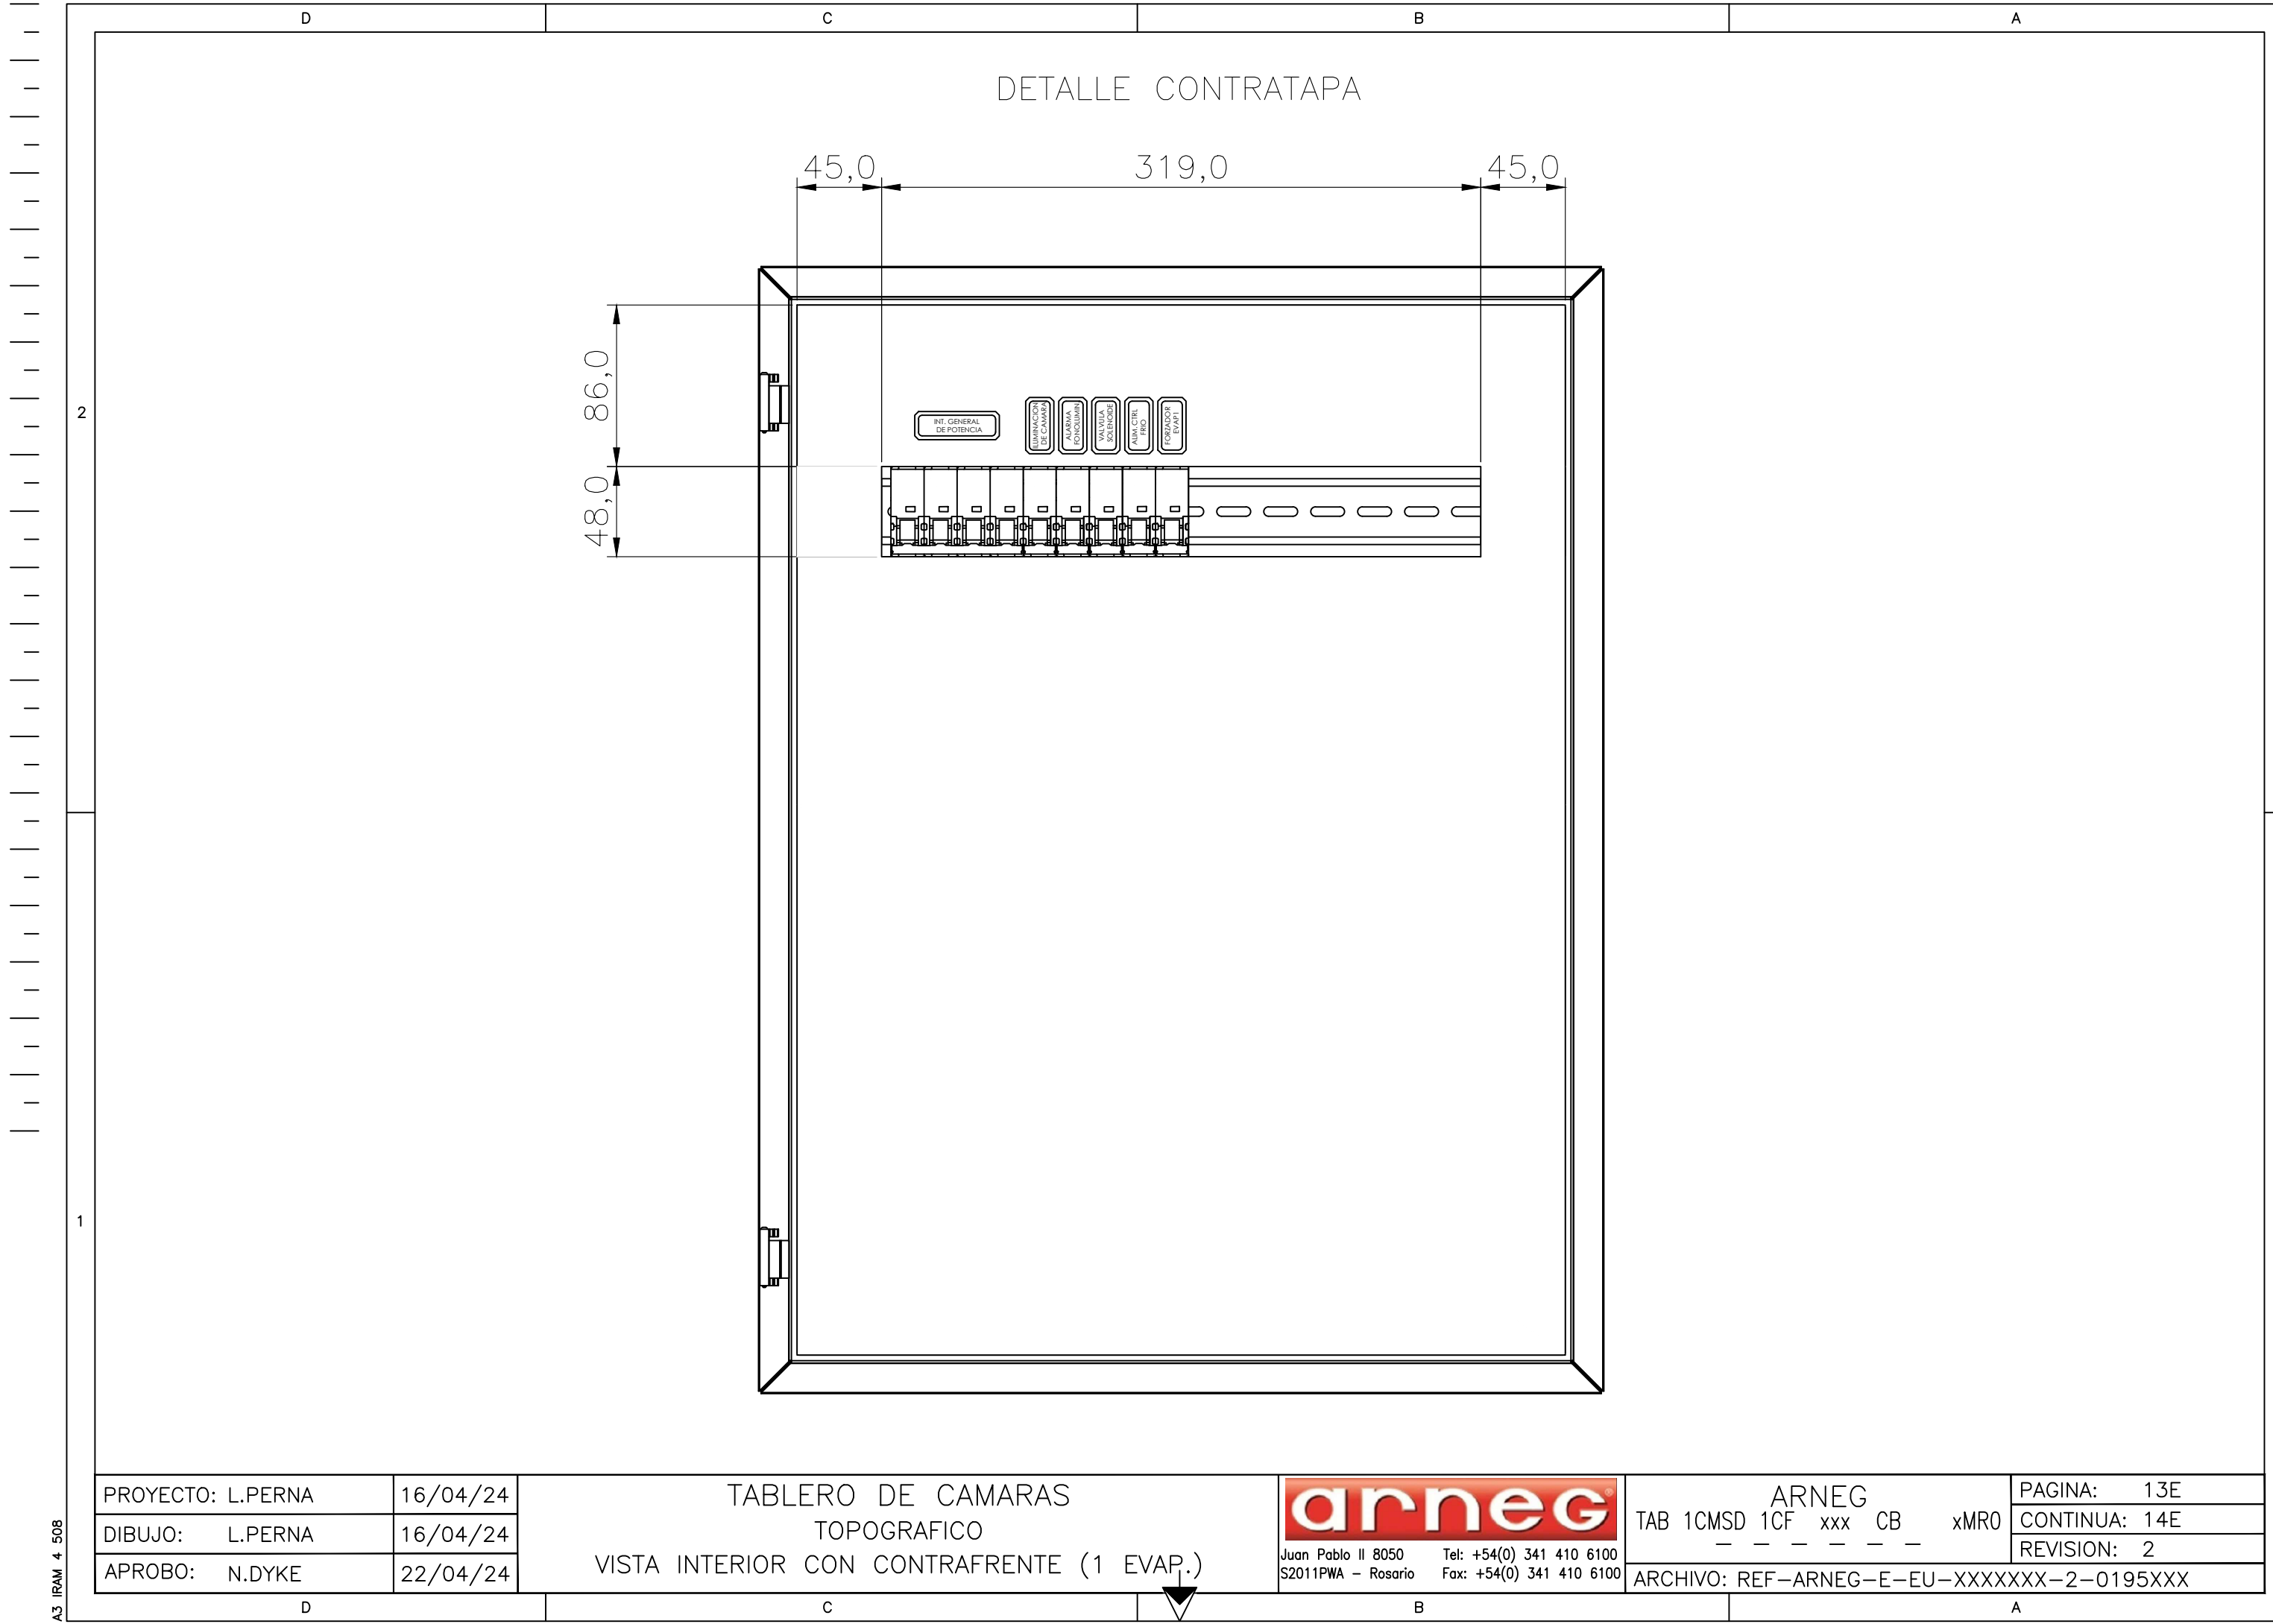

A3 IRAM 4 508

PROYECTO: L.PERNA	16/04/24
DIBUJO: L.PERNA	16/04/24
APROBO: N.DYKE	22/04/24

TABLERO DE CAMARAS
TOPOGRAFICO
VISTA INTERIOR CON CONTRAFRENTE (1 EVAP.)




Juan Pablo II 8050 Tel: +54(0) 341 410 6100
S2011PWA - Rosario Fax: +54(0) 341 410 6100

ARNEG
TAB 1CMSD 1CF xxx CB xMRO
- - - - -
ARCHIVO: REF-ARNEG-E-EU-XXXXXXX-2-0195XXX

PAGINA: 13E
CONTINUA: 14E
REVISION: 2

DETALLE CARTELES ACRILICOS

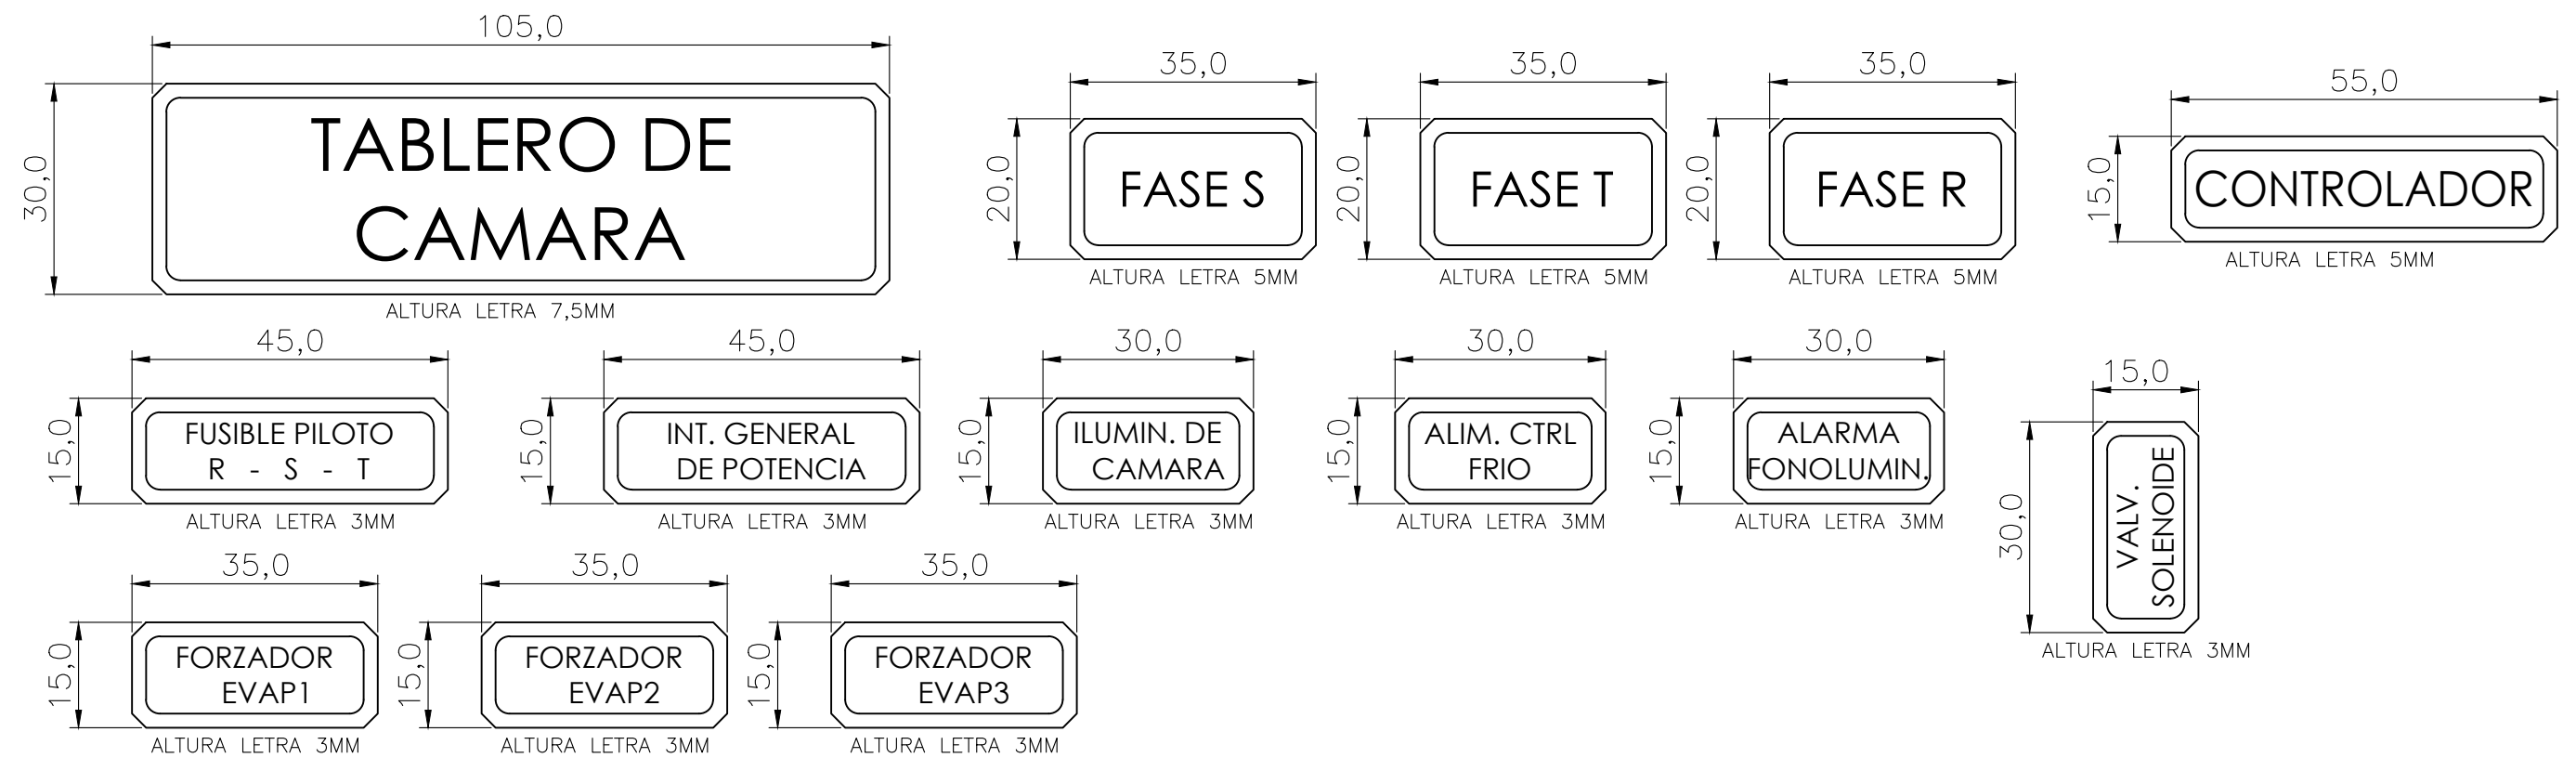


PROYECTO: L.PERNA	16/04/24
DIBUJO: L.PERNA	16/04/24
APROBO: N.DYKE	22/04/24

TABLERO DE CAMARAS
TOPOGRAFICO
DETALLE DE CARTELES ACRILICOS

arneg

Juan Pablo II 8050 Tel: +54(0) 341 410 6100
S2011PWA - Rosario Fax: +54(0) 341 410 6100

ARNEG TAB 1CMSD 1CF xxx CB xMRO _ _ _ _ _	PAGINA: 15
	CONTINUA: 16
	REVISION: 2
ARCHIVO: REF-ARNEG-E-EU-XXXXXXX-2-0195XXX	

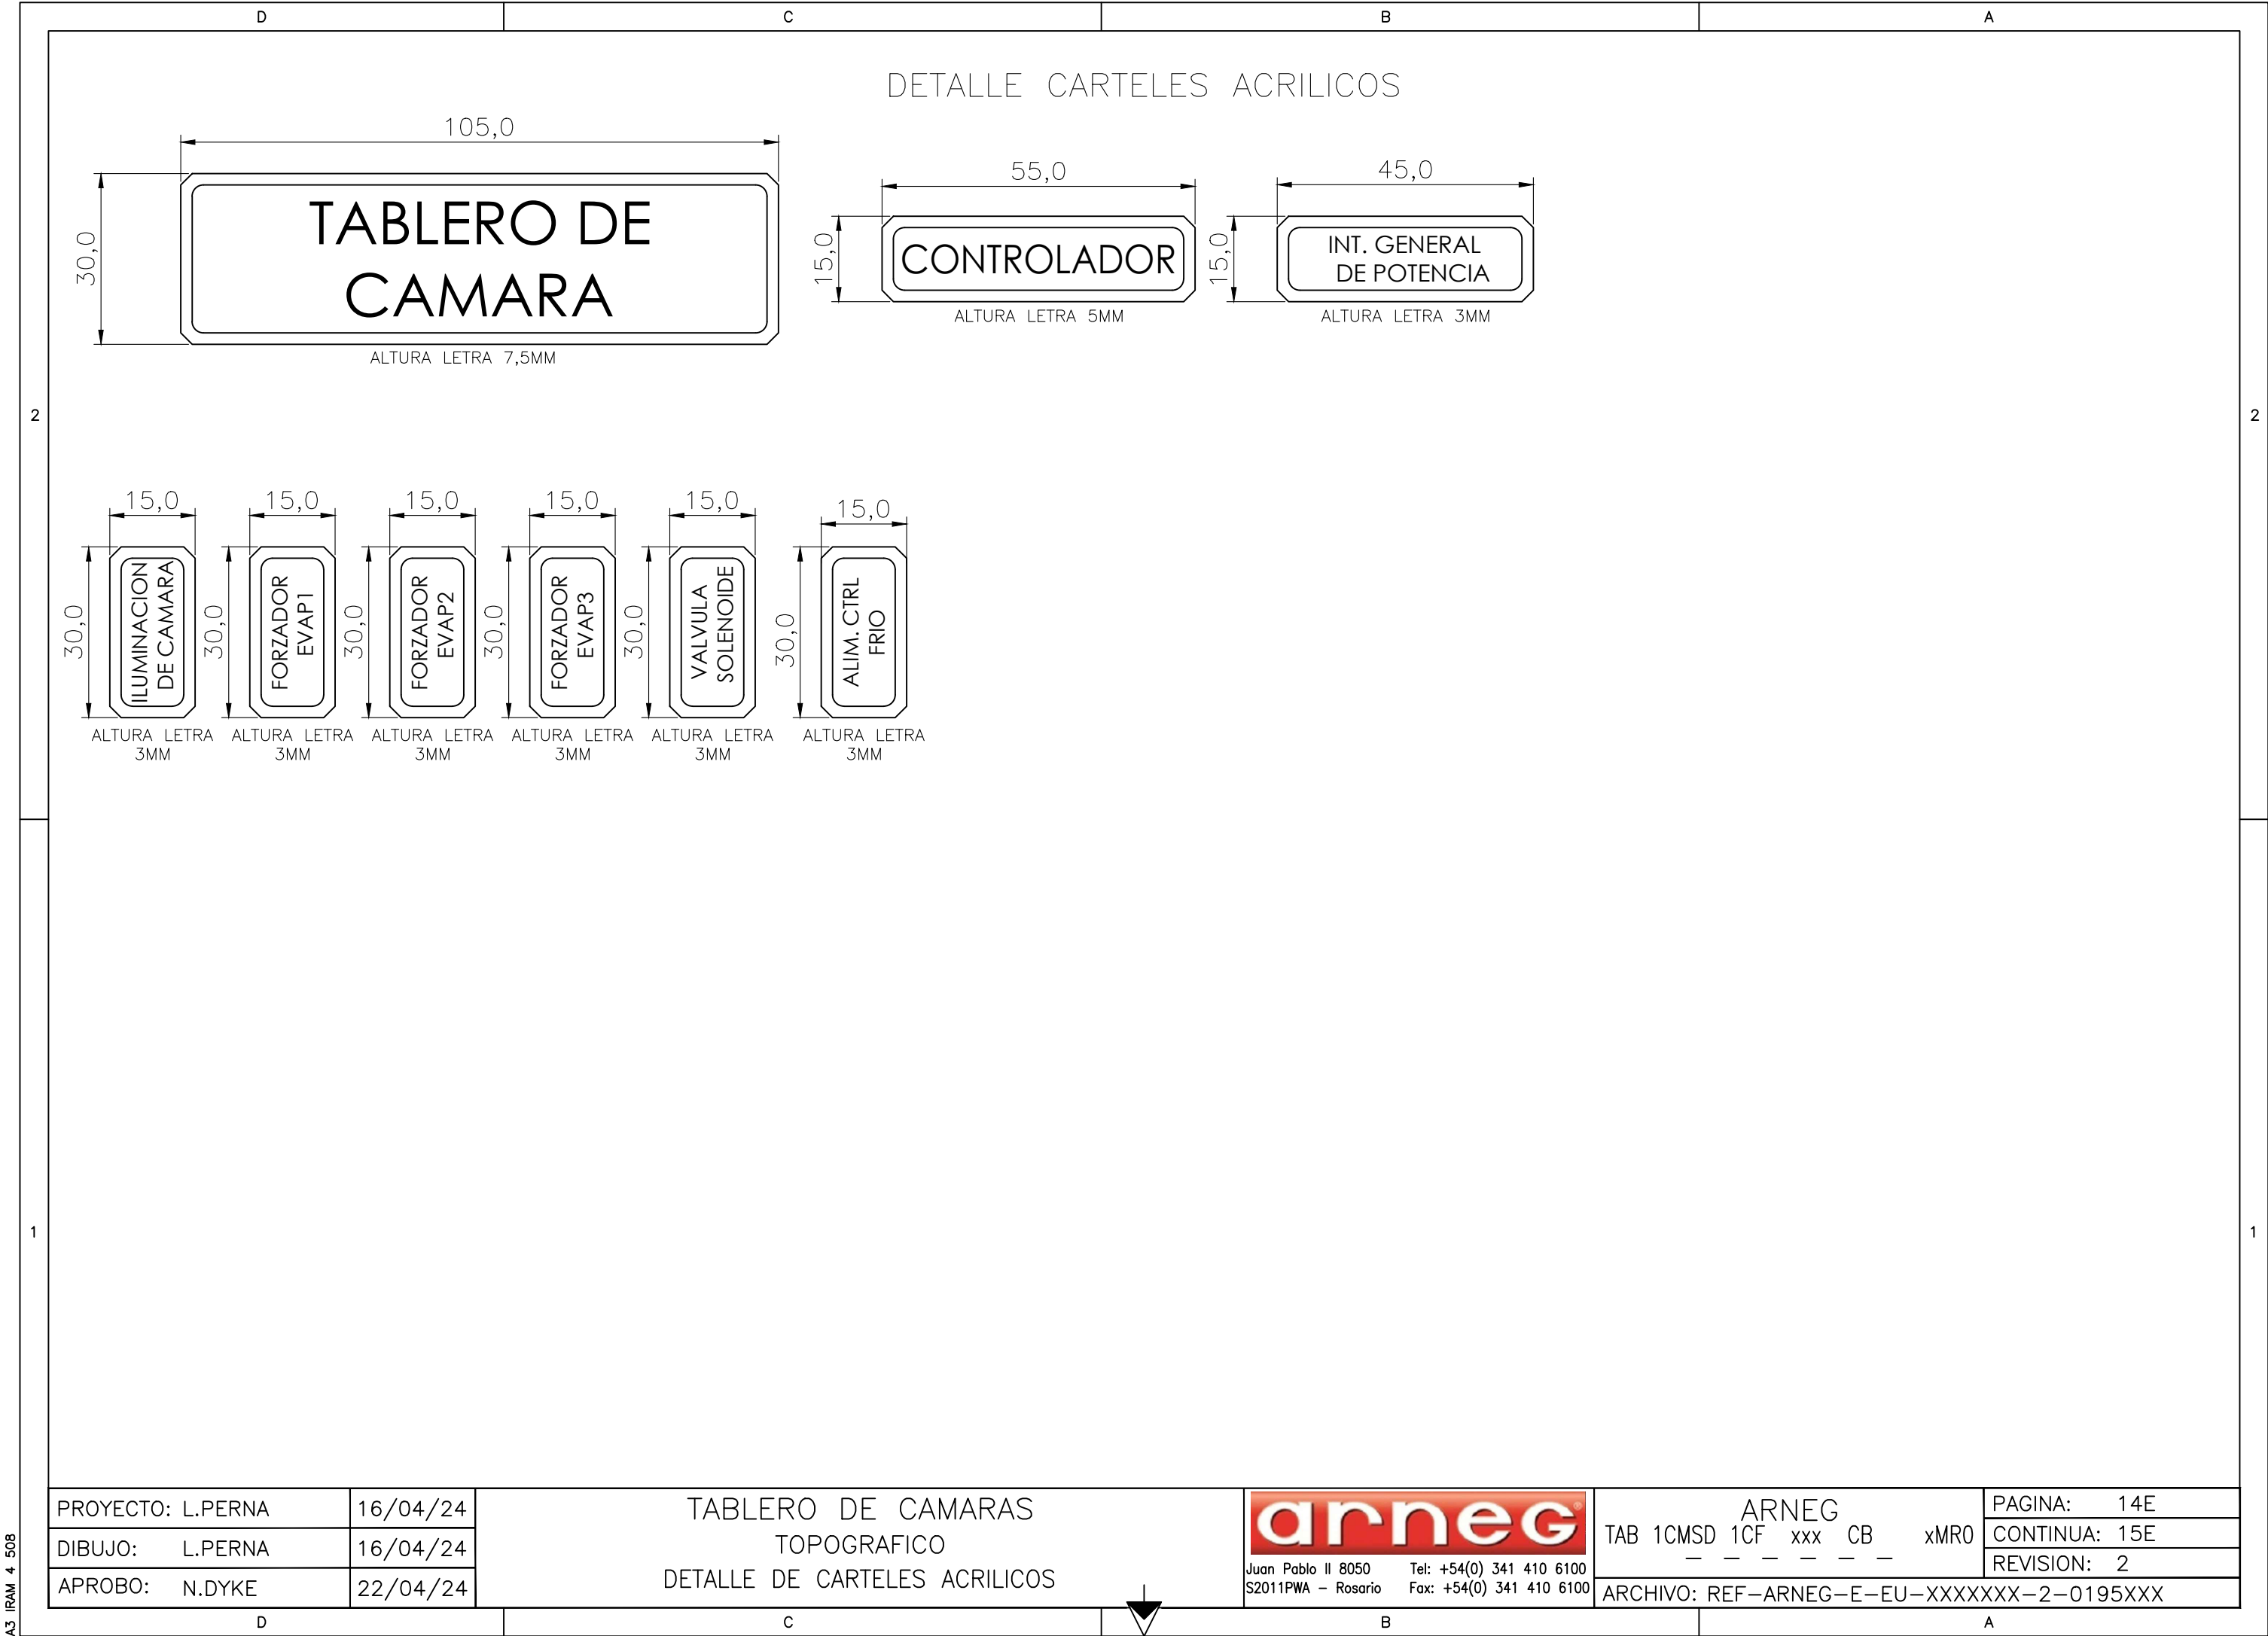

PROYECTO: L.PERNA	16/04/24
DIBUJO: L.PERNA	16/04/24
APROBO: N.DYKE	22/04/24


TABLERO DE CAMARAS
TOPOGRAFICO
DETALLE DE BORNERA (3 EVAP.)


arneg


Juan Pablo II 8050
S2011PWA - Rosario

Tel: +54(0) 341 410 6100
Fax: +54(0) 341 410 6100

TAB 1CMSD 1CF xxx CB xMR0	ARNEG	PAGINA: 16
	— — — — —	CONTINUA: 17
	ARCHIVO: REF-ARNEG-E-EU-XXXXXXX-2-0195XXX	REVISION: 2

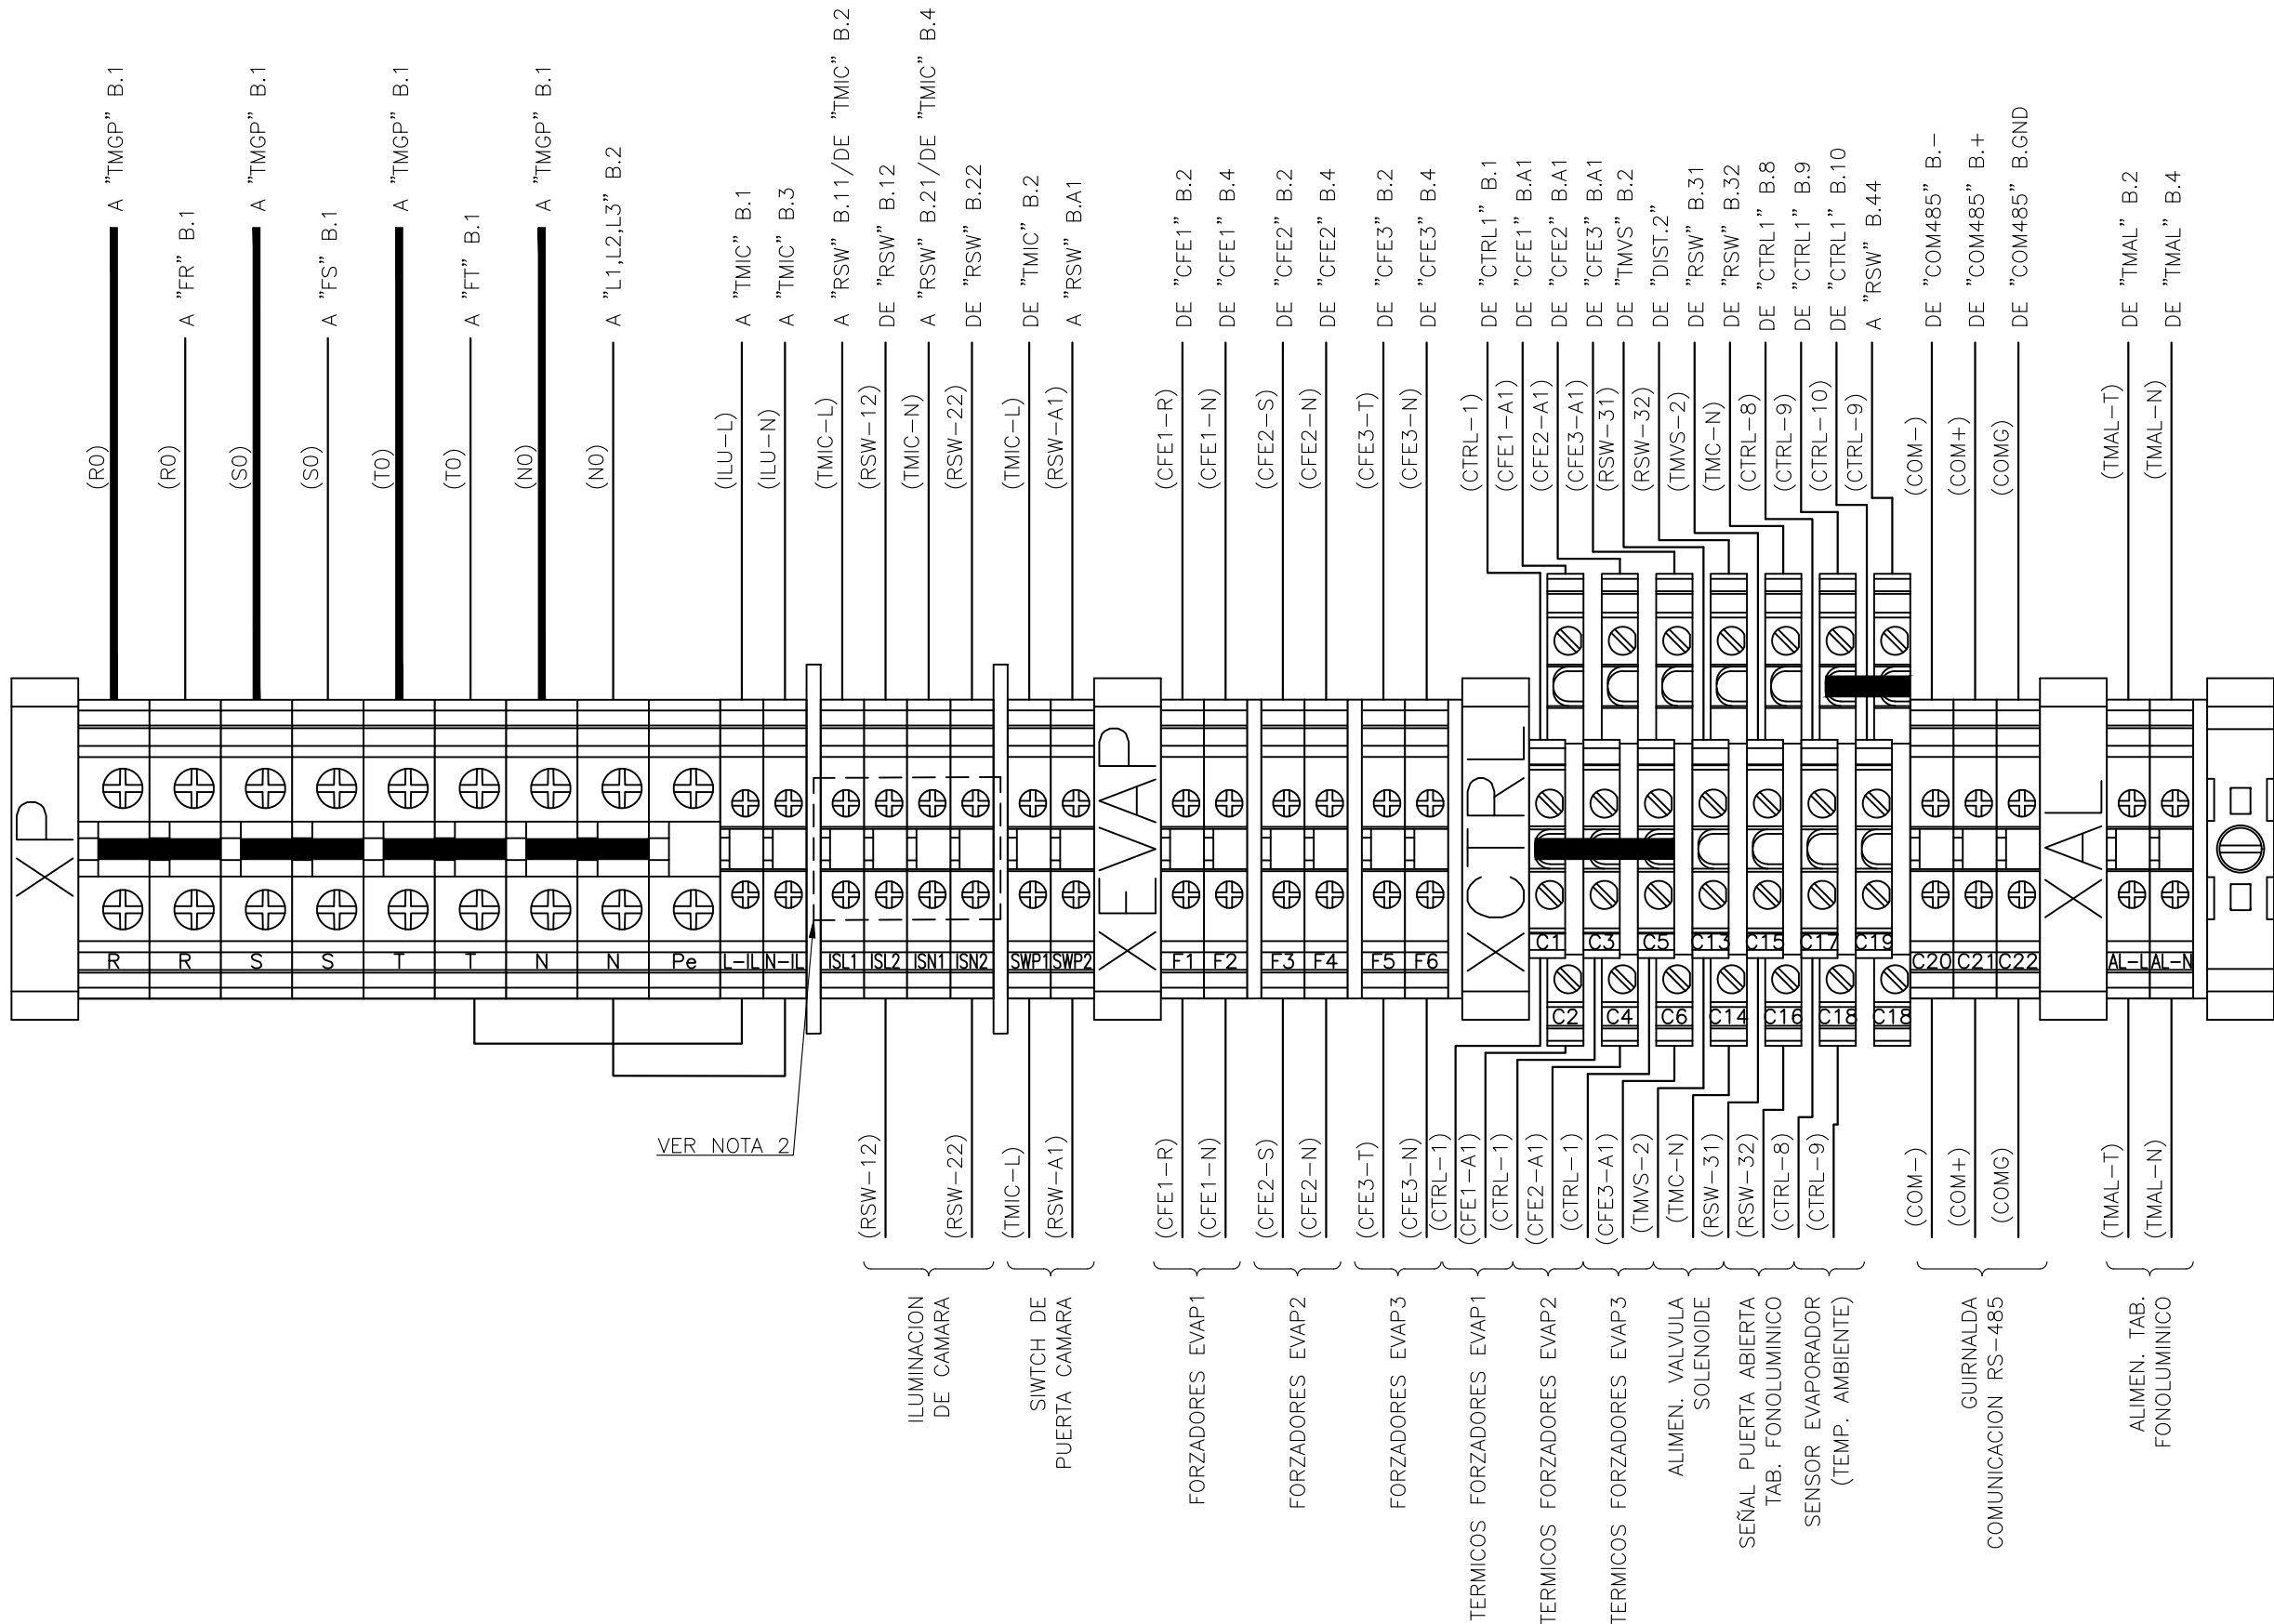

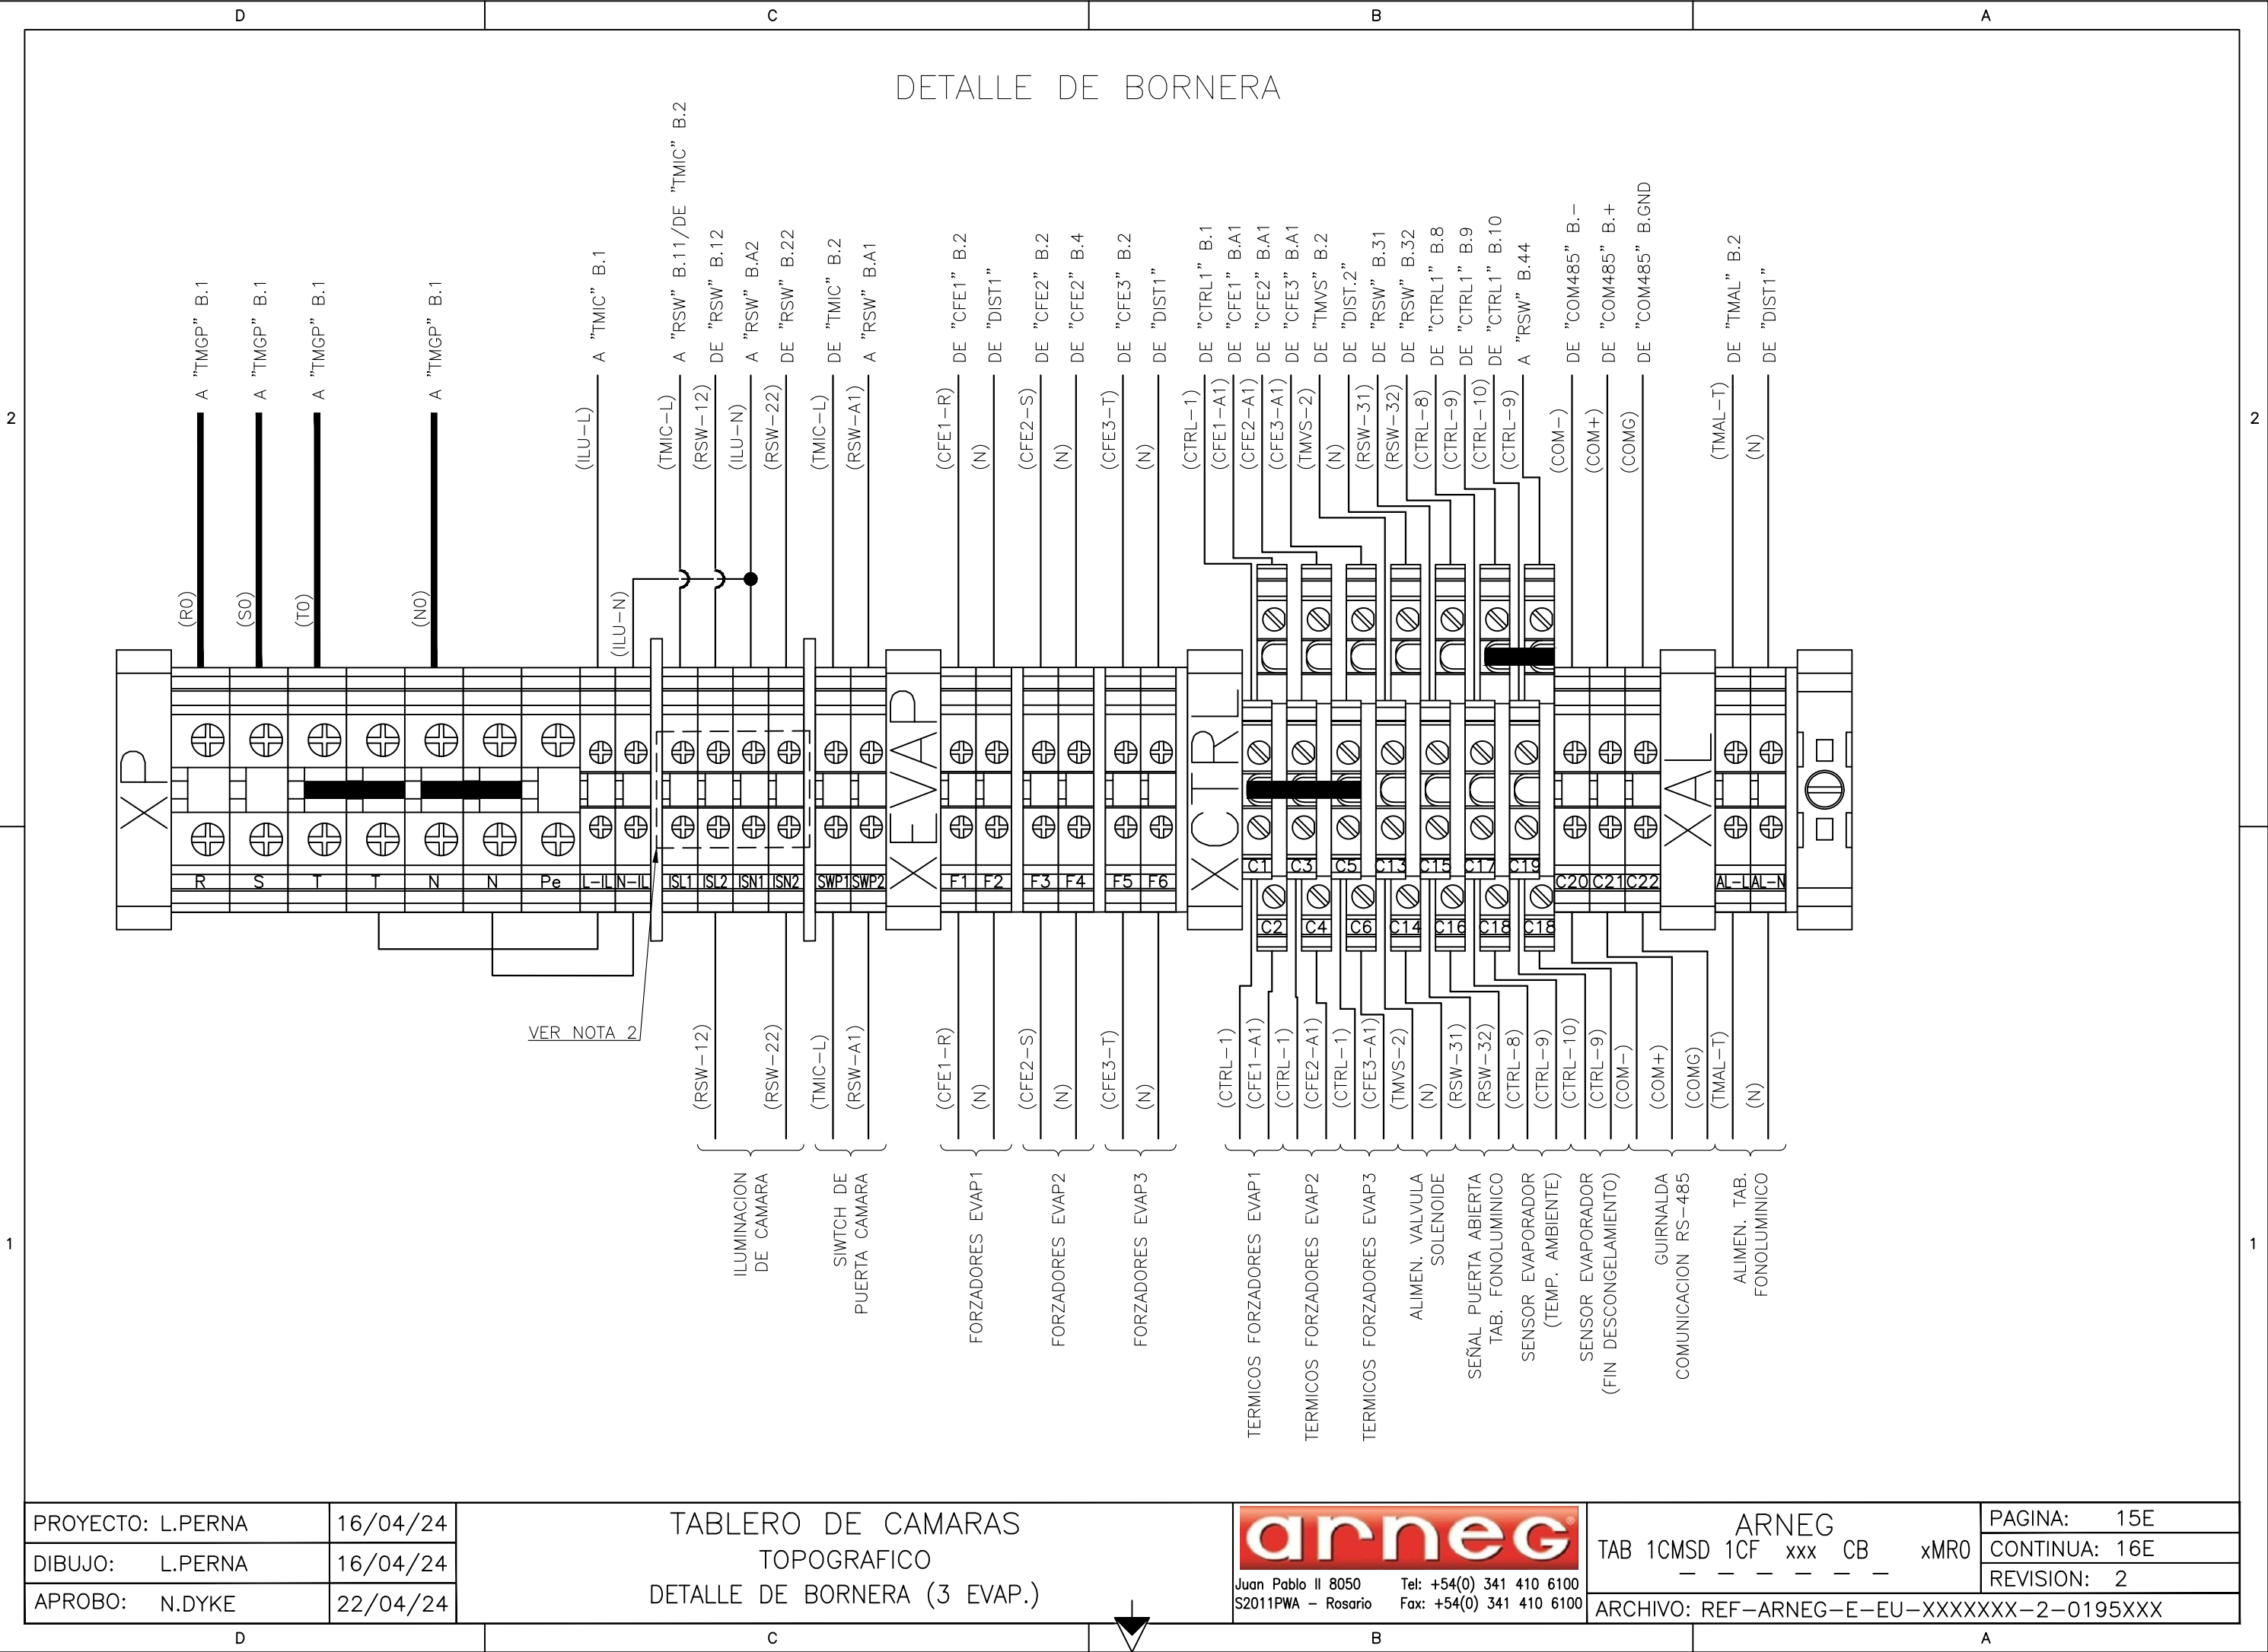

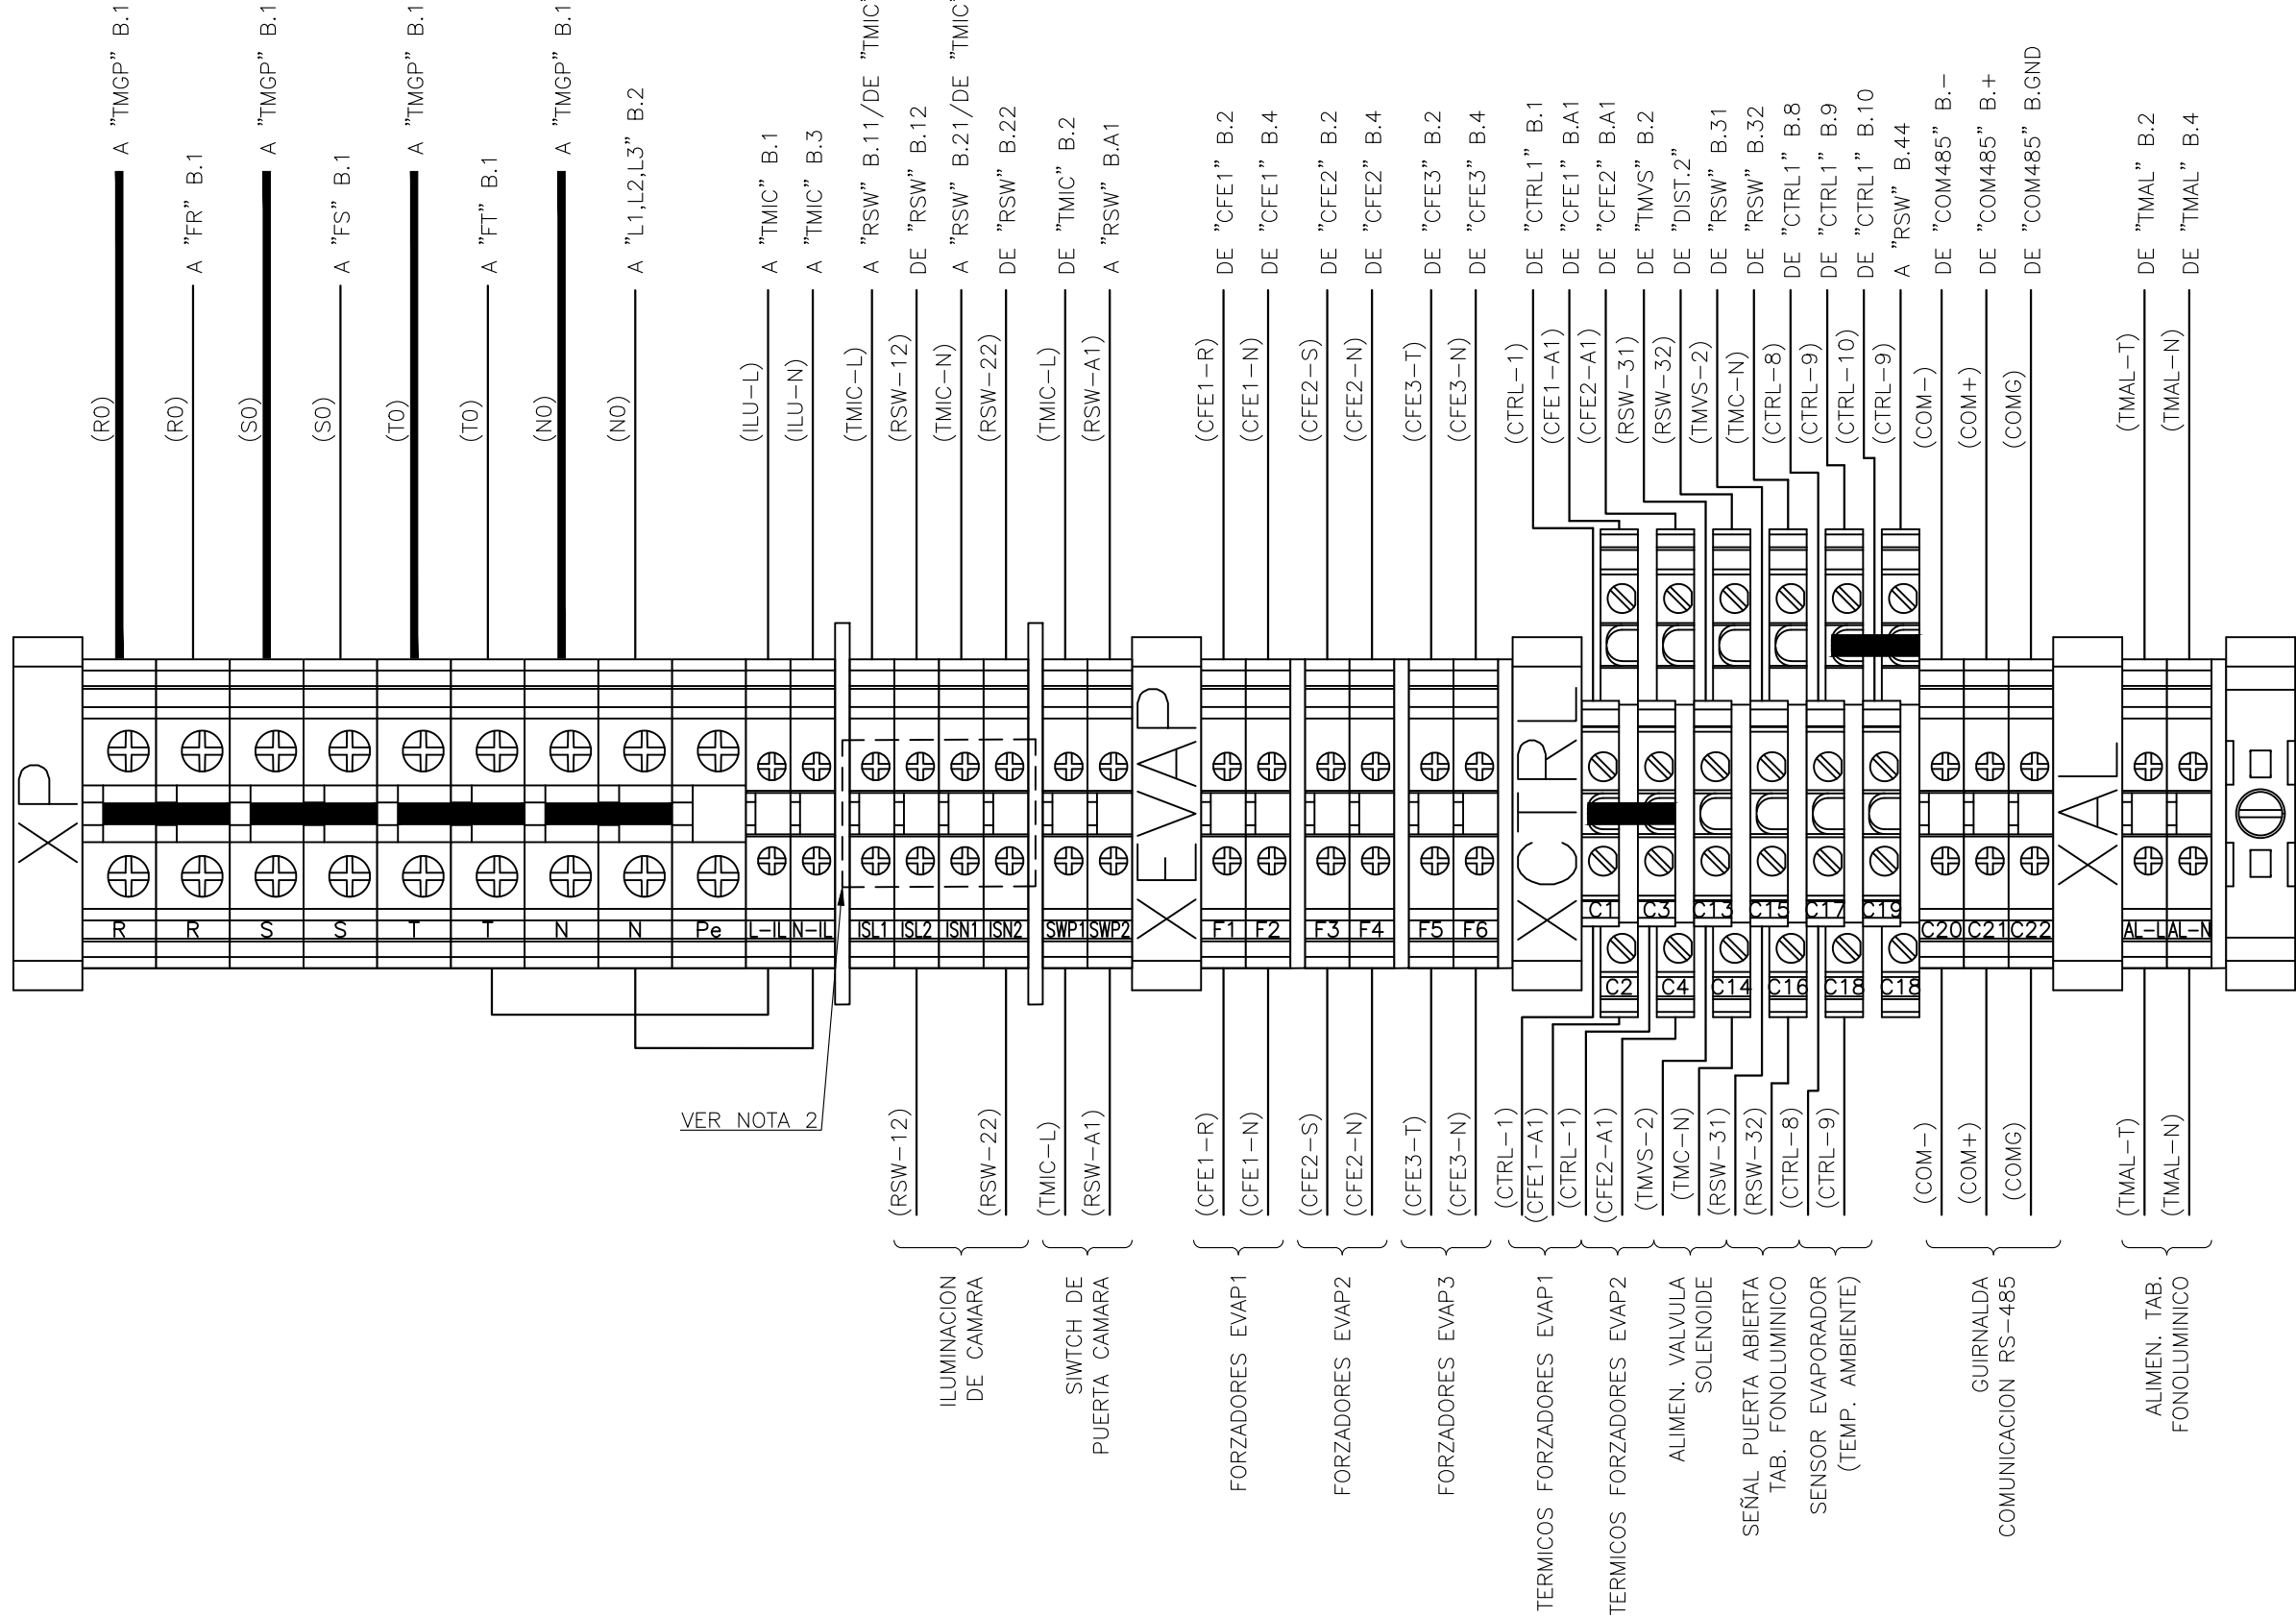

PROYECTO: L.PERNA	16/04/24
DIBUJO: L.PERNA	16/04/24
APROBO: N.DYKE	22/04/24


TABLERO DE CAMARAS
TOPOGRAFICO
DETALLE DE BORNERA (2 EVAP.)



Juan Pablo II 8050
S2011PWA - Rosario

Tel: +54(0) 341 410 6100
Fax: +54(0) 341 410 6100

ARNEG TAB 1CMSD 1CF xxx CB xMR0 — — — — —	PAGINA: 17
	CONTINUA: 18
	REVISION: 2
ARCHIVO: REF-ARNEG-E-EU-XXXXXXX-2-0195XXX	

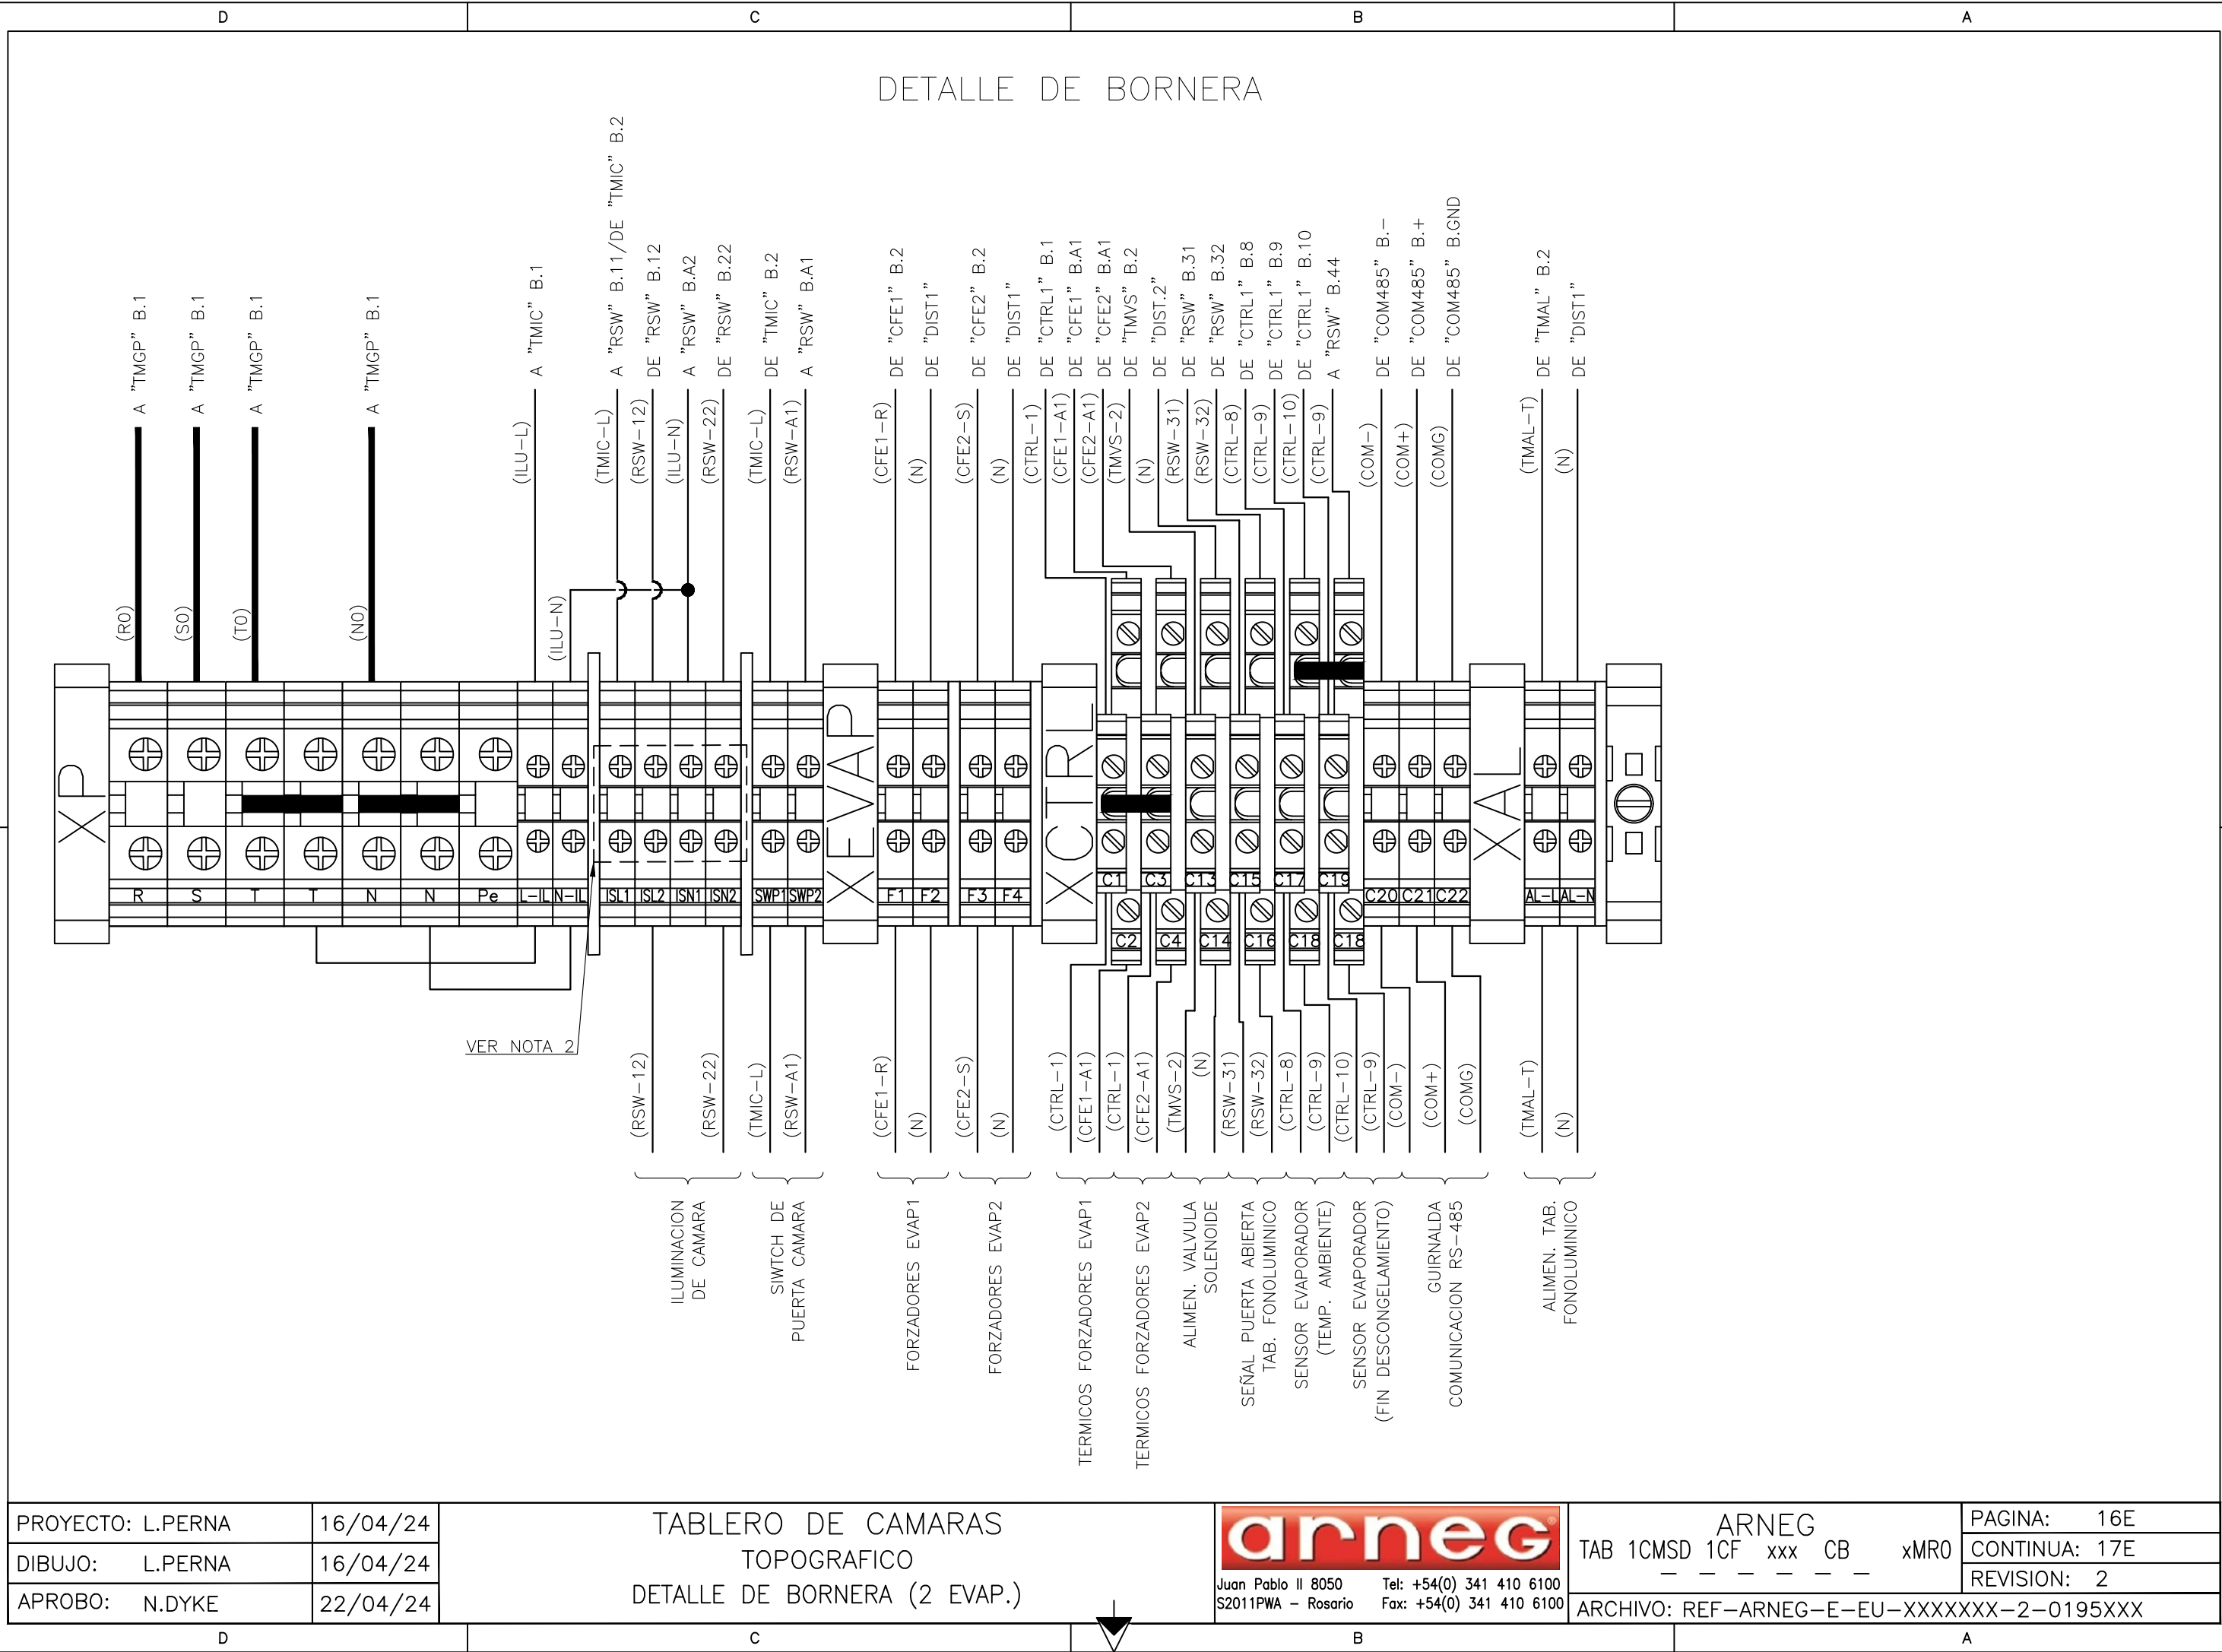




TABLERO DE CAMARAS
TOPOGRAFICO
DETALLE DE BORNERA (1 EVAP.)



ARCHIVO: REF-ARNEG-E-EU-XXXXXXX-2-0195XXX

DETALLE DE BORNERA

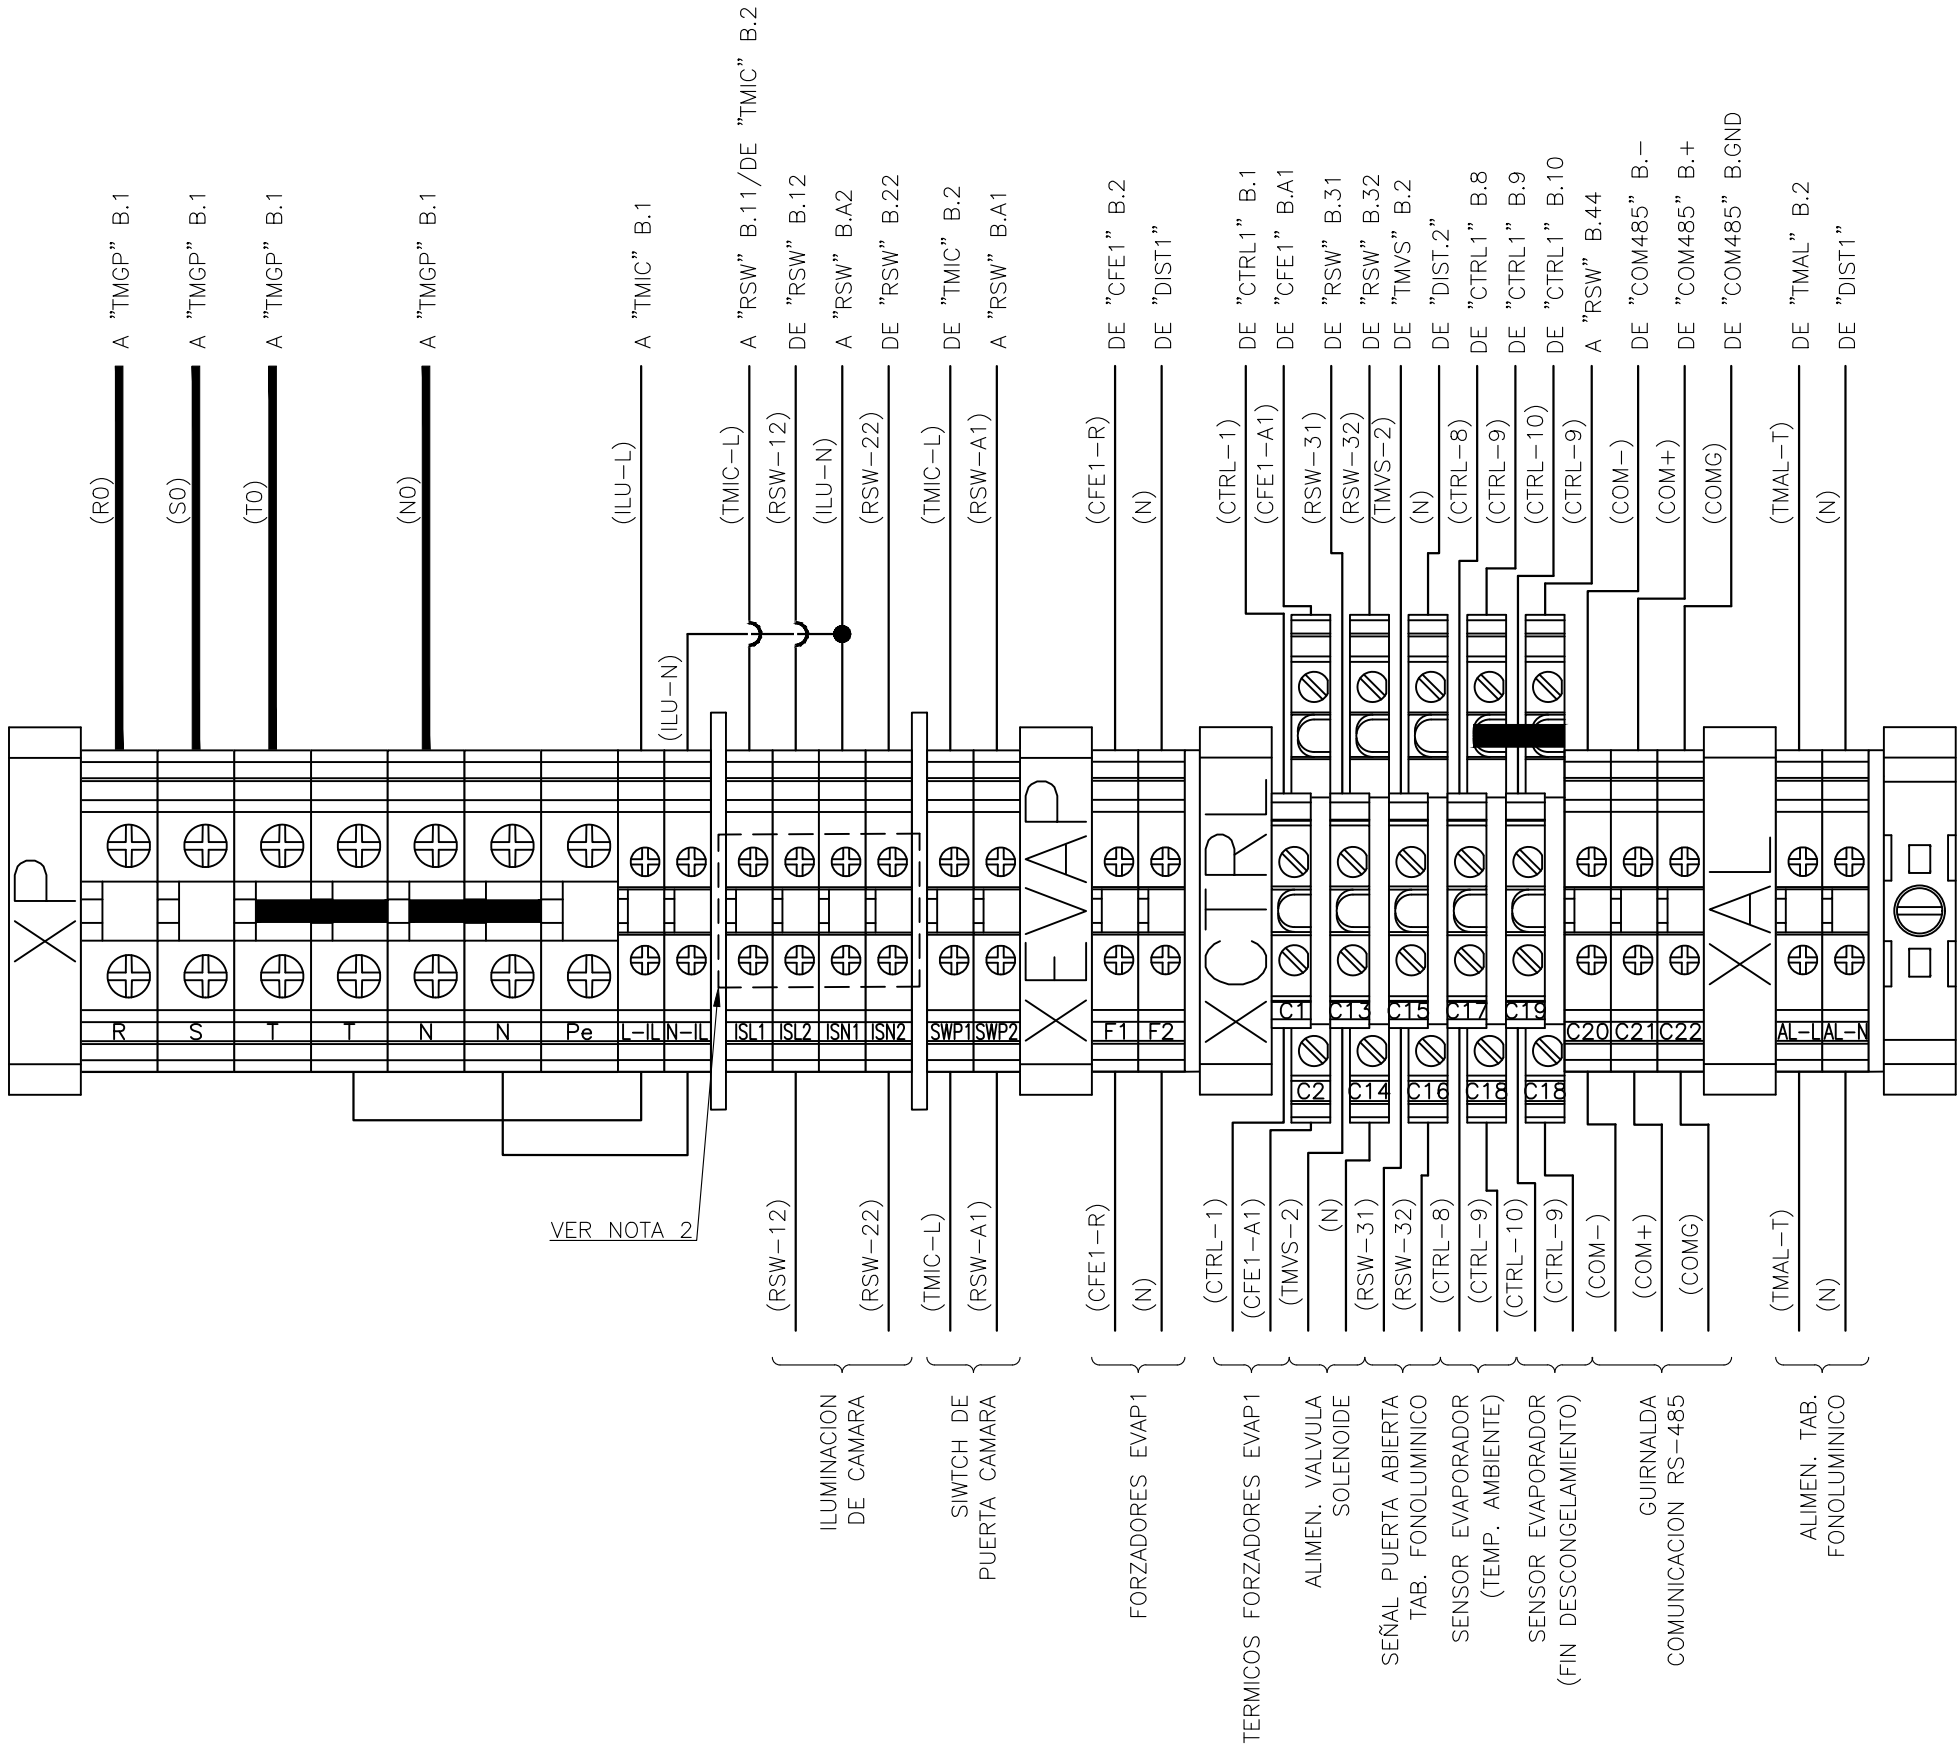

PROYECTO: L.PERNA	16/04/24
DIBUJO: L.PERNA	16/04/24
APROBO: N.DYKE	22/04/24


TABLERO DE CAMARAS
TOPOGRAFICO
DETALLE DE BORNERA (1 EVAP.)



Juan Pablo II 8050
S2011PWA - Rosario

Tel: +54(0) 341 410 6100
Fax: +54(0) 341 410 6100

ARNEG TAB 1CMSD 1CF xxx CB xMR0 — — — — —	PAGINA: 17E
	CONTINUA: 19/18E
	REVISION: 2
ARCHIVO: REF-ARNEG-E-EU-XXXXXXX-2-0195XXX	

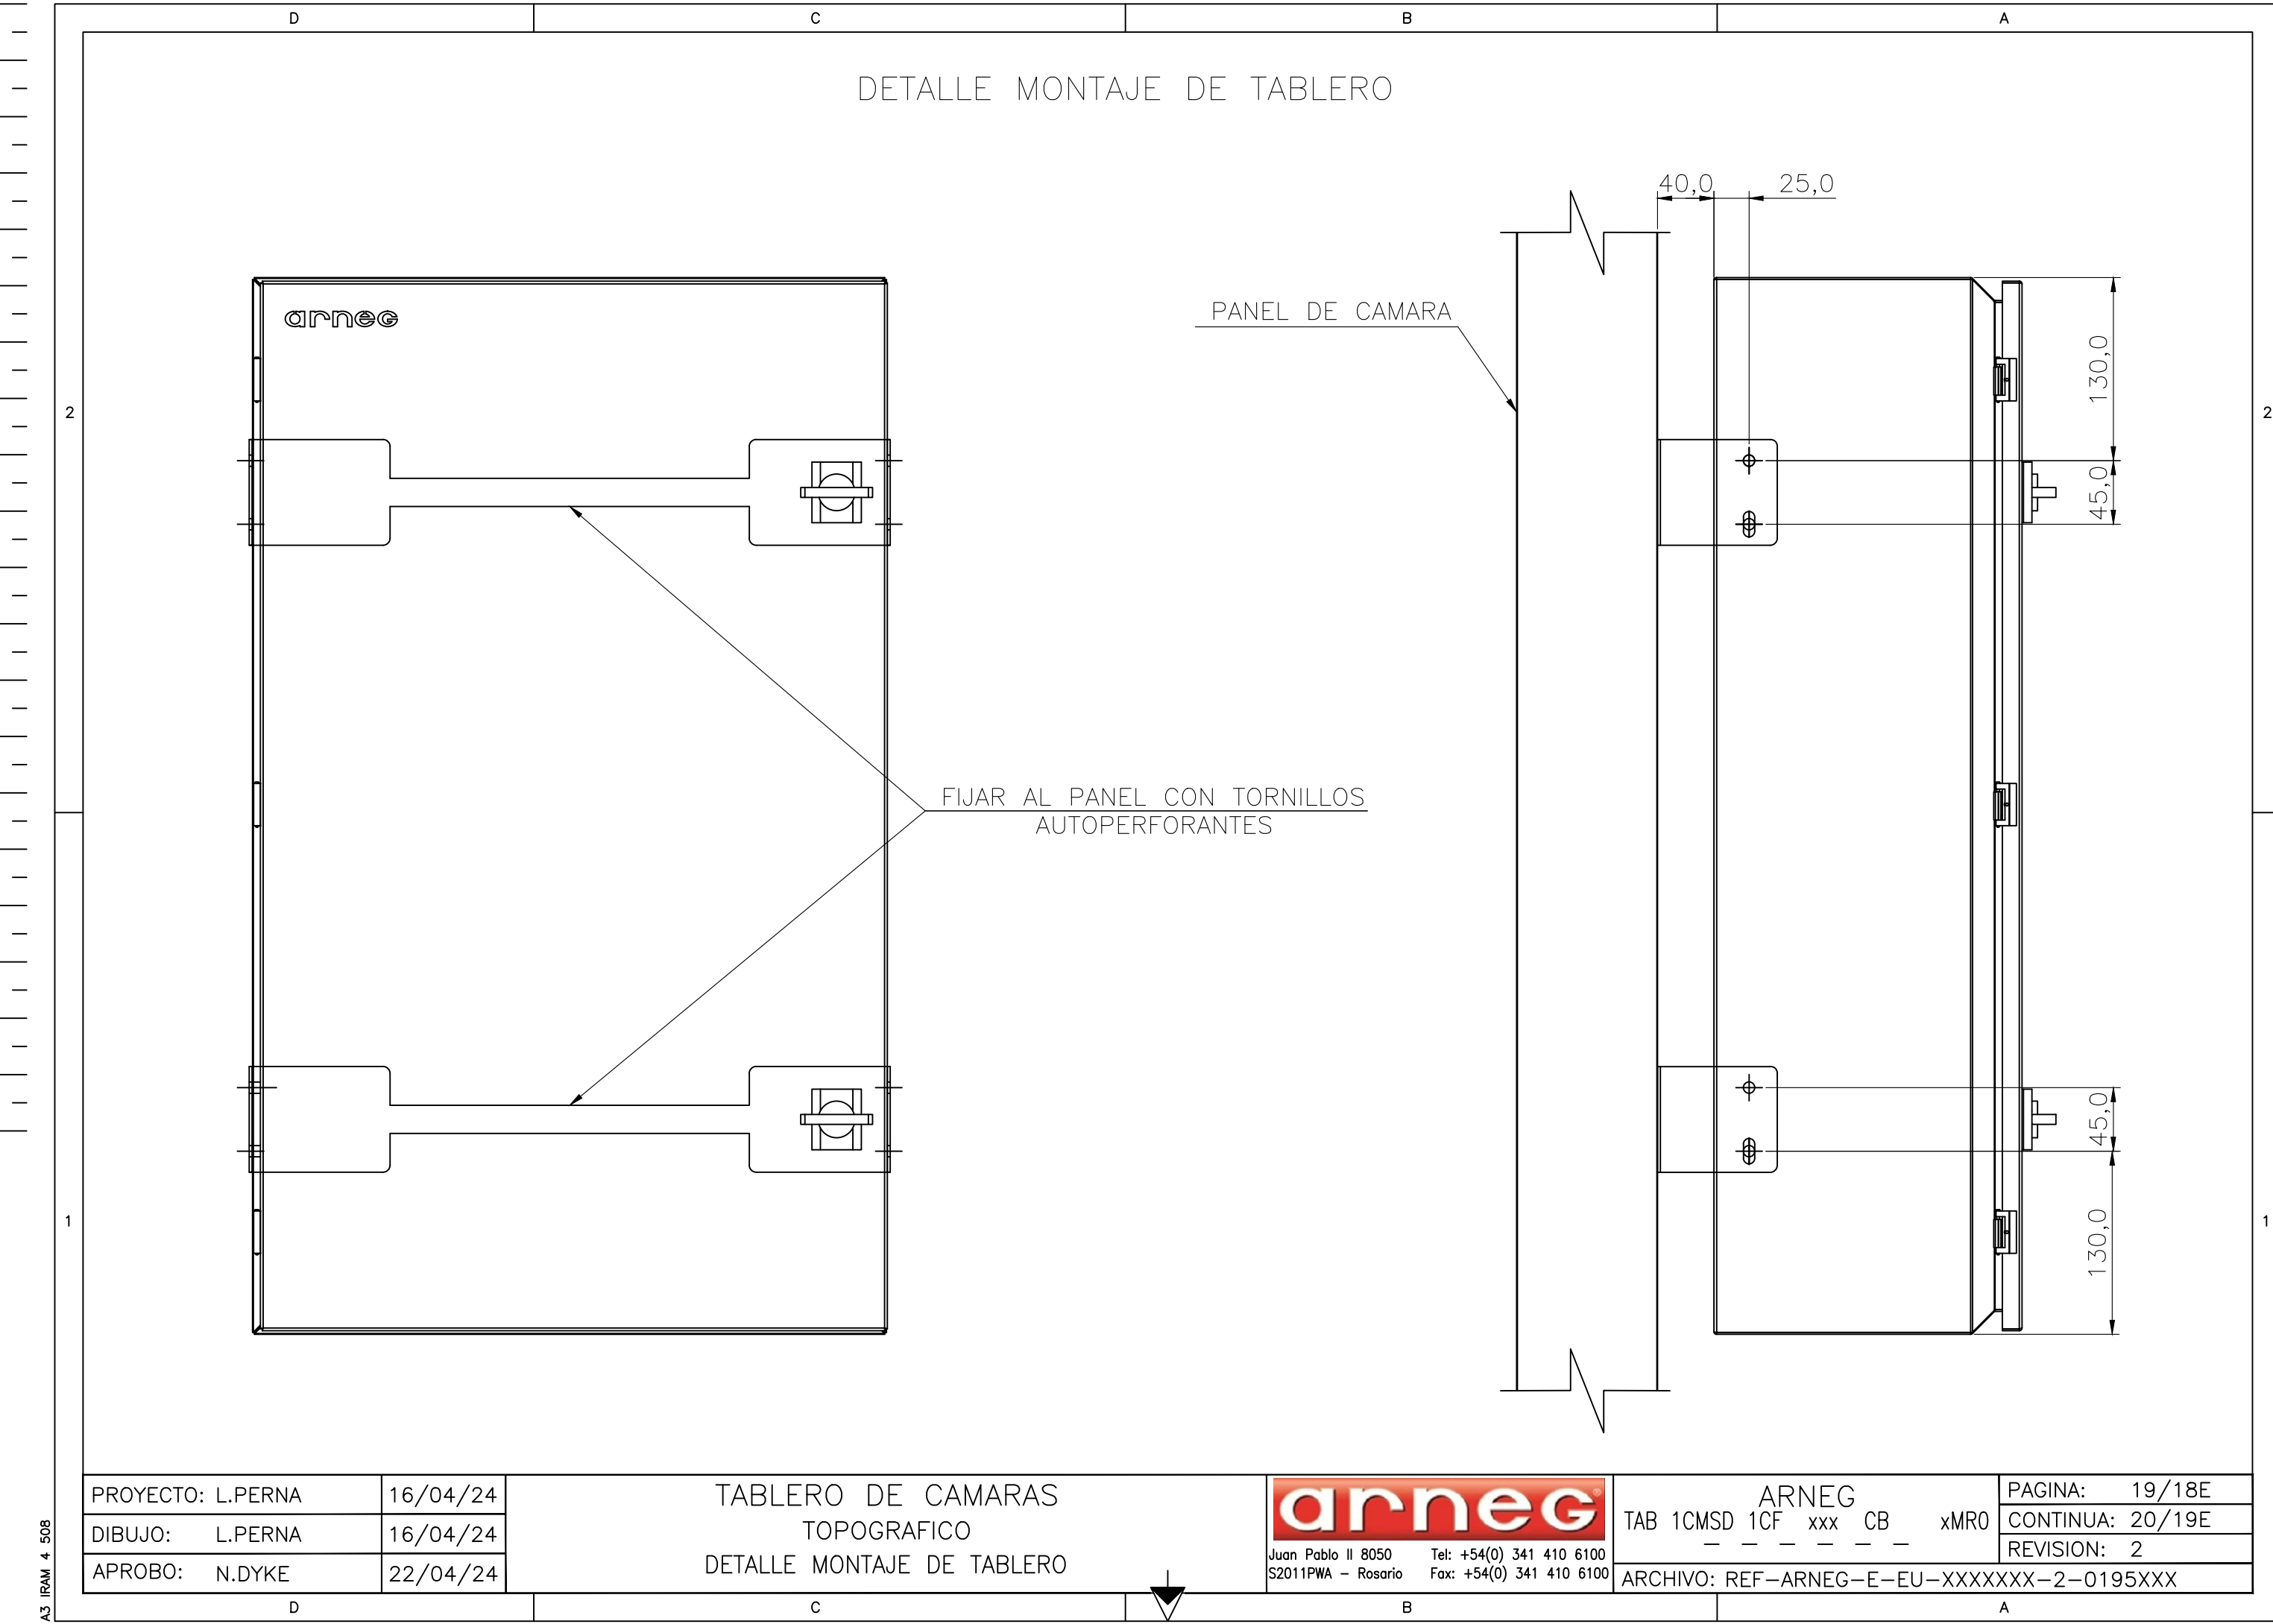

DETALLE MONTAJE DE TABLERO

PANEL DE CAMARA

FIJAR AL PANEL CON TORNILLOS
AUTOPERFORANTES

arneg

PROYECTO: L.PERNA	16/04/24
DIBUJO: L.PERNA	16/04/24
APROBO: N.DYKE	22/04/24

TABLERO DE CAMARAS
TOPOGRAFICO
DETALLE MONTAJE DE TABLERO

arneg


Juan Pablo II 8050
S2011PWA - Rosario

Tel: +54(0) 341 410 6100
Fax: +54(0) 341 410 6100

ARNEG
TAB 1CMSD 1CF xxx CB xMR0
— — — — —
ARCHIVO: REF-ARNEG-E-EU-XXXXXXX-2-0195XXX

PAGINA: 19/18E
CONTINUA: 20/19E
REVISION: 2

A3 IRAM 4 508

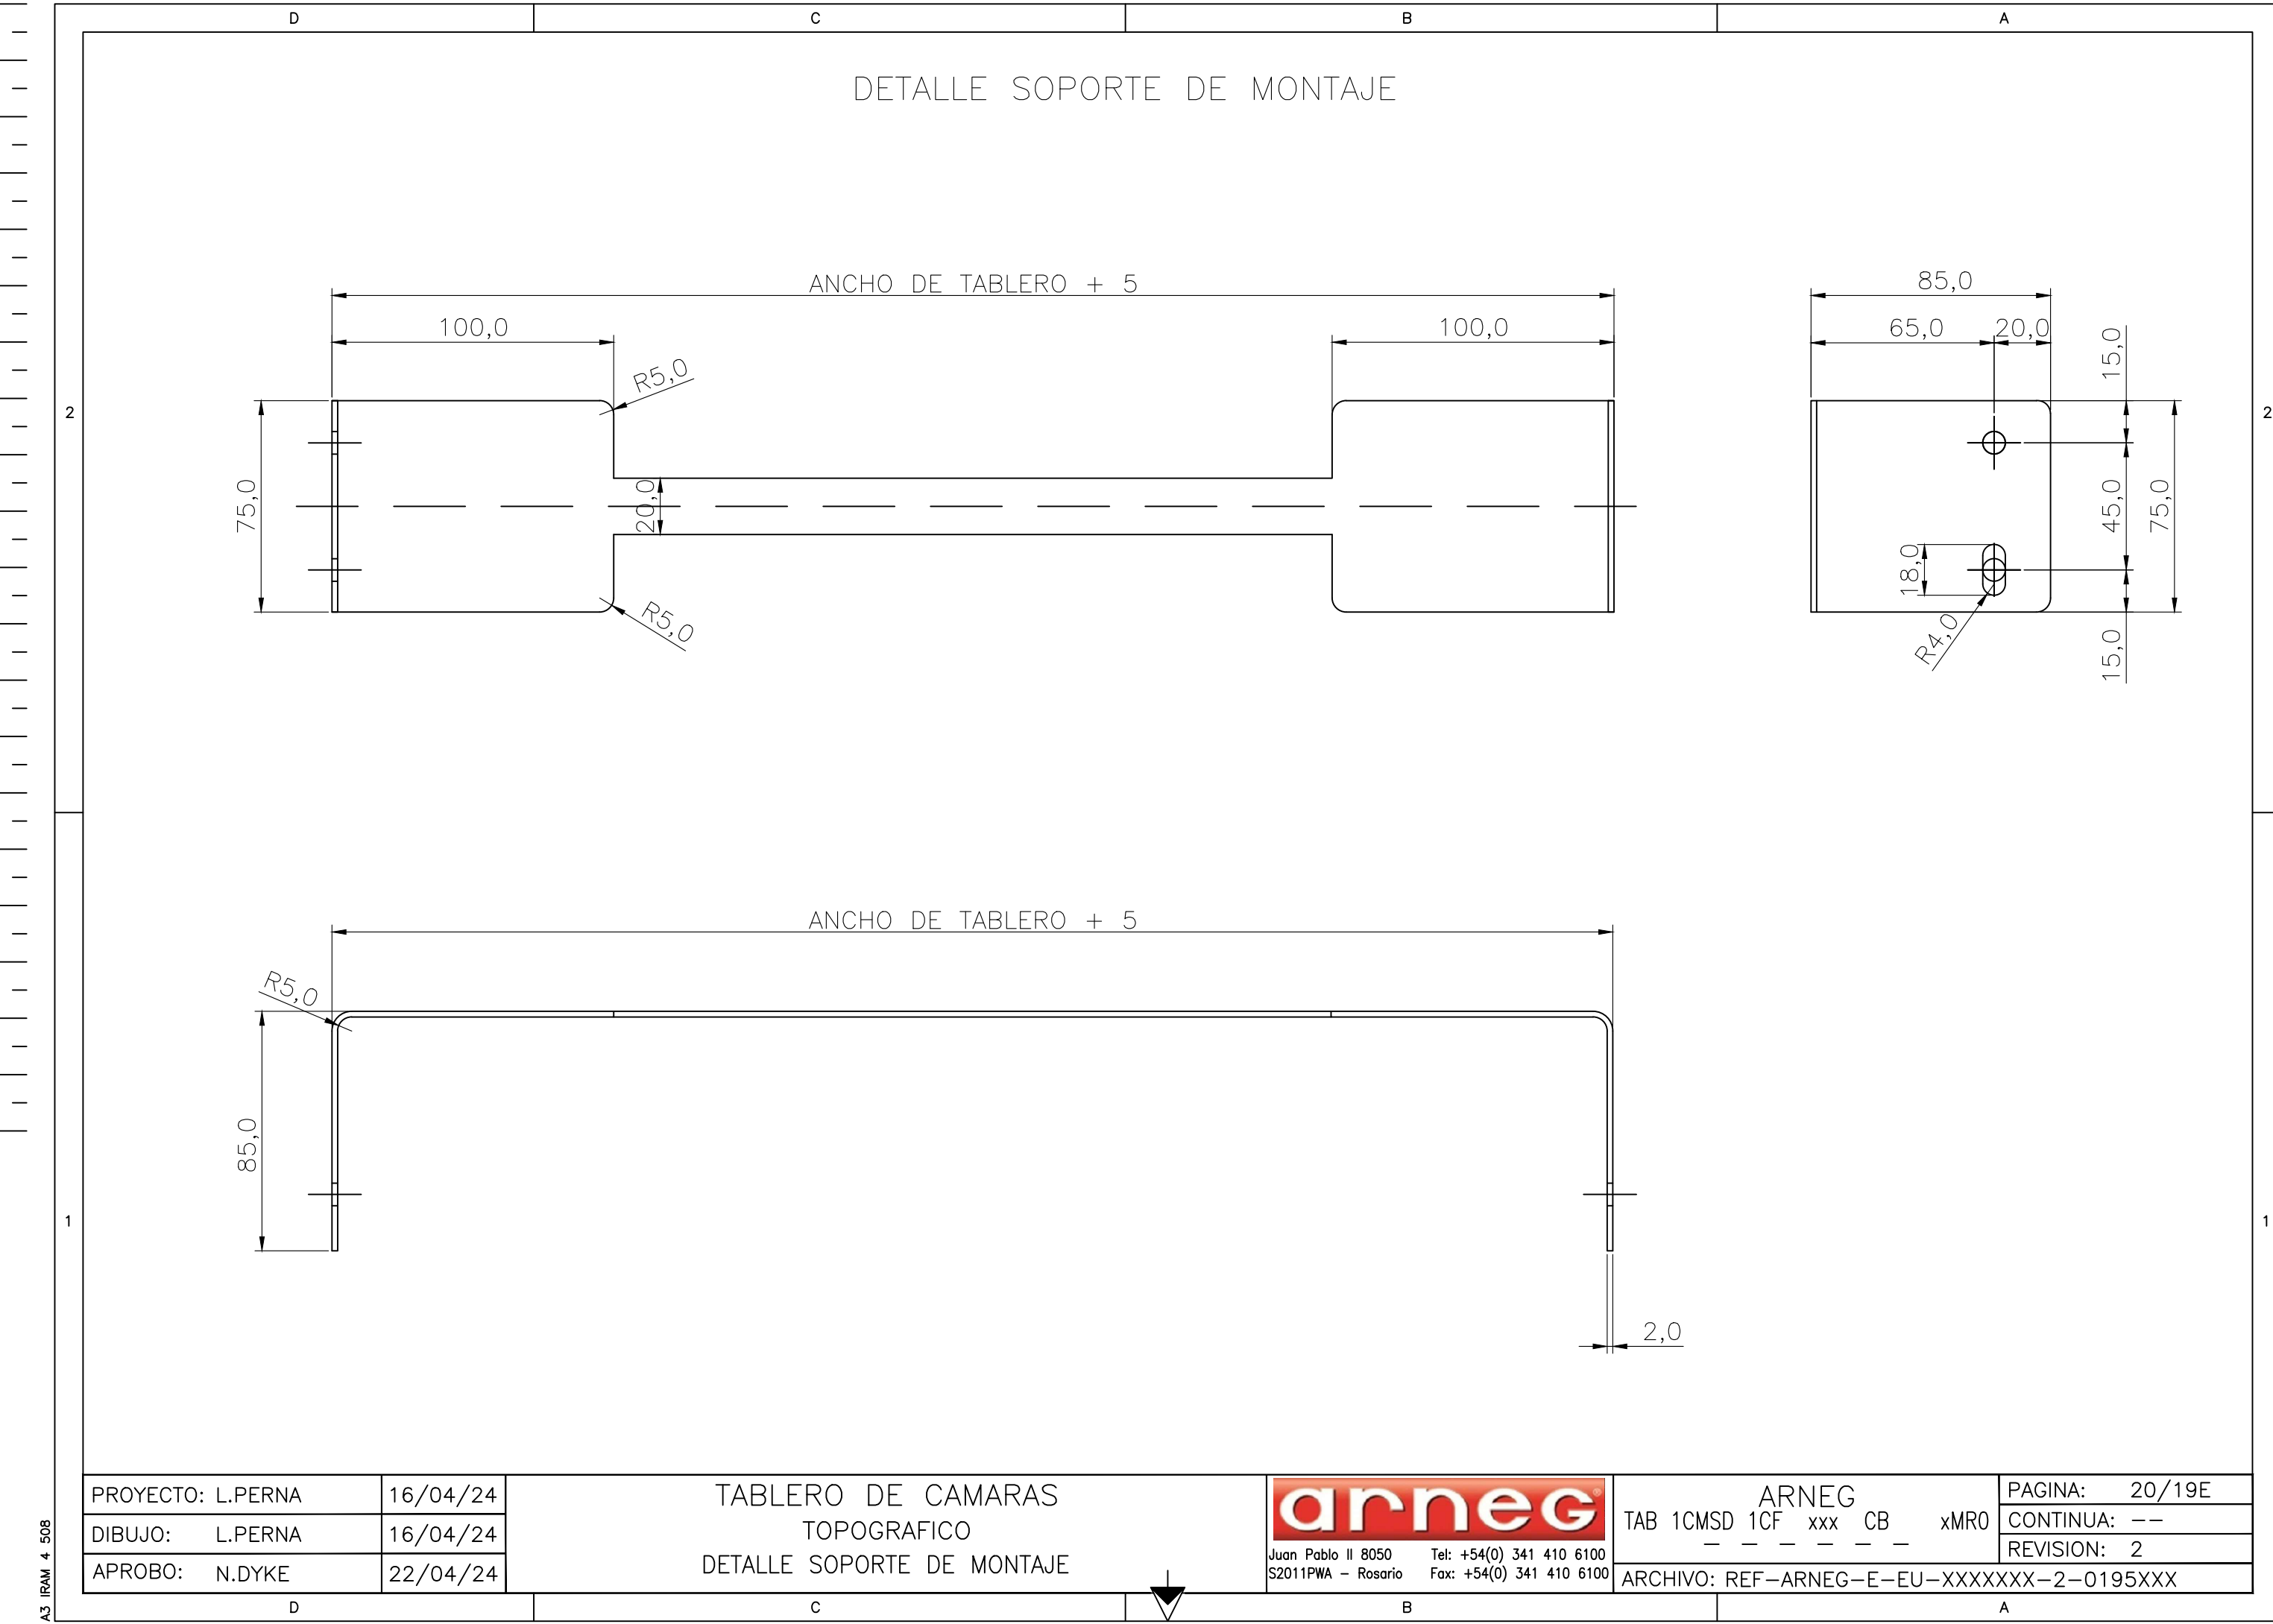

PROYECTO: L.PERNA	16/04/24
DIBUJO: L.PERNA	16/04/24
APROBO: N.DYKE	22/04/24

TABLERO DE CAMARAS
TOPOGRAFICO
DETALLE SOPORTE DE MONTAJE

arneg

Juan Pablo II 8050 Tel: +54(0) 341 410 6100
S2011PWA - Rosario Fax: +54(0) 341 410 6100

ARNEG
TAB 1CMSD 1CF xxx CB xMR0
— — — — —
ARCHIVO: REF-ARNEG-E-EU-XXXXXXX-2-0195XXX

PAGINA: 20/19E
CONTINUA: --
REVISION: 2