
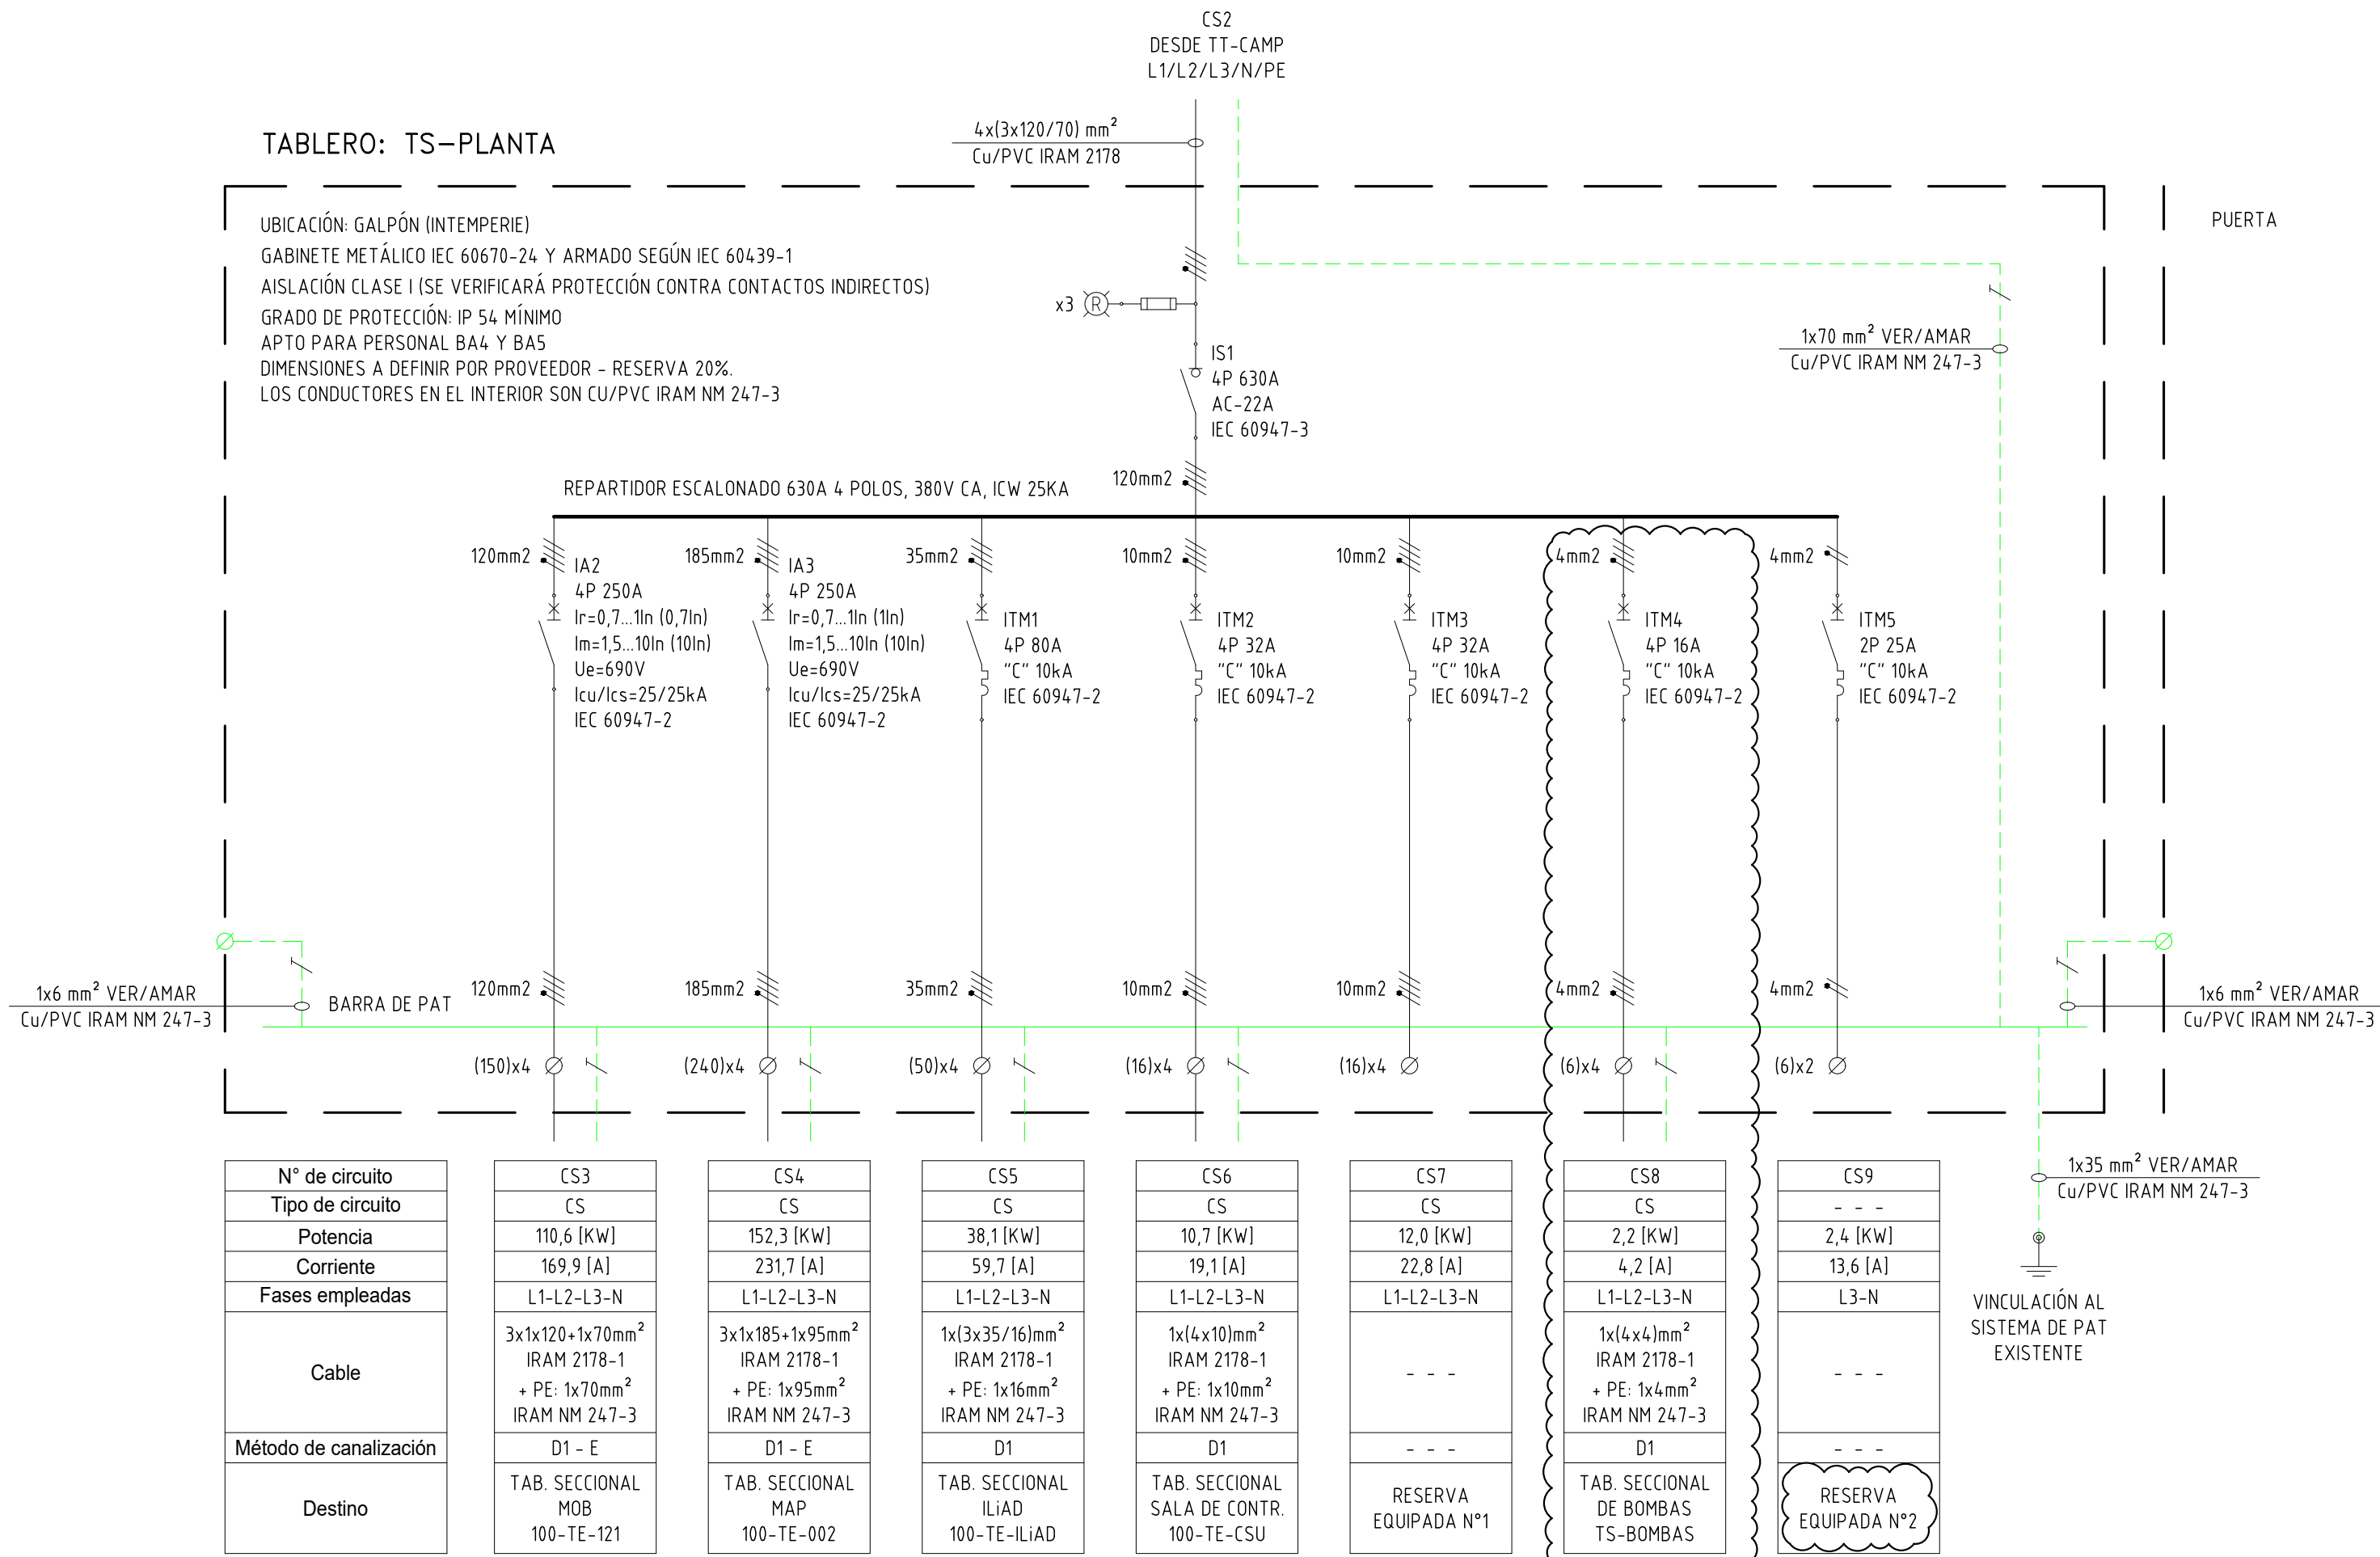


COL.	PUNTA
1	7 0.09
2	7 0.2
3	7 0.2
4	7 0.09
5	7 0.09
6	7 0.2
7	7 0.1
8	7 0.05
9	7 0.05
30	7 0.15
32	7 0.2
50	7 0.19
90	7 0.19
150	7 0.19

OTROS	2520.05
-------	---------

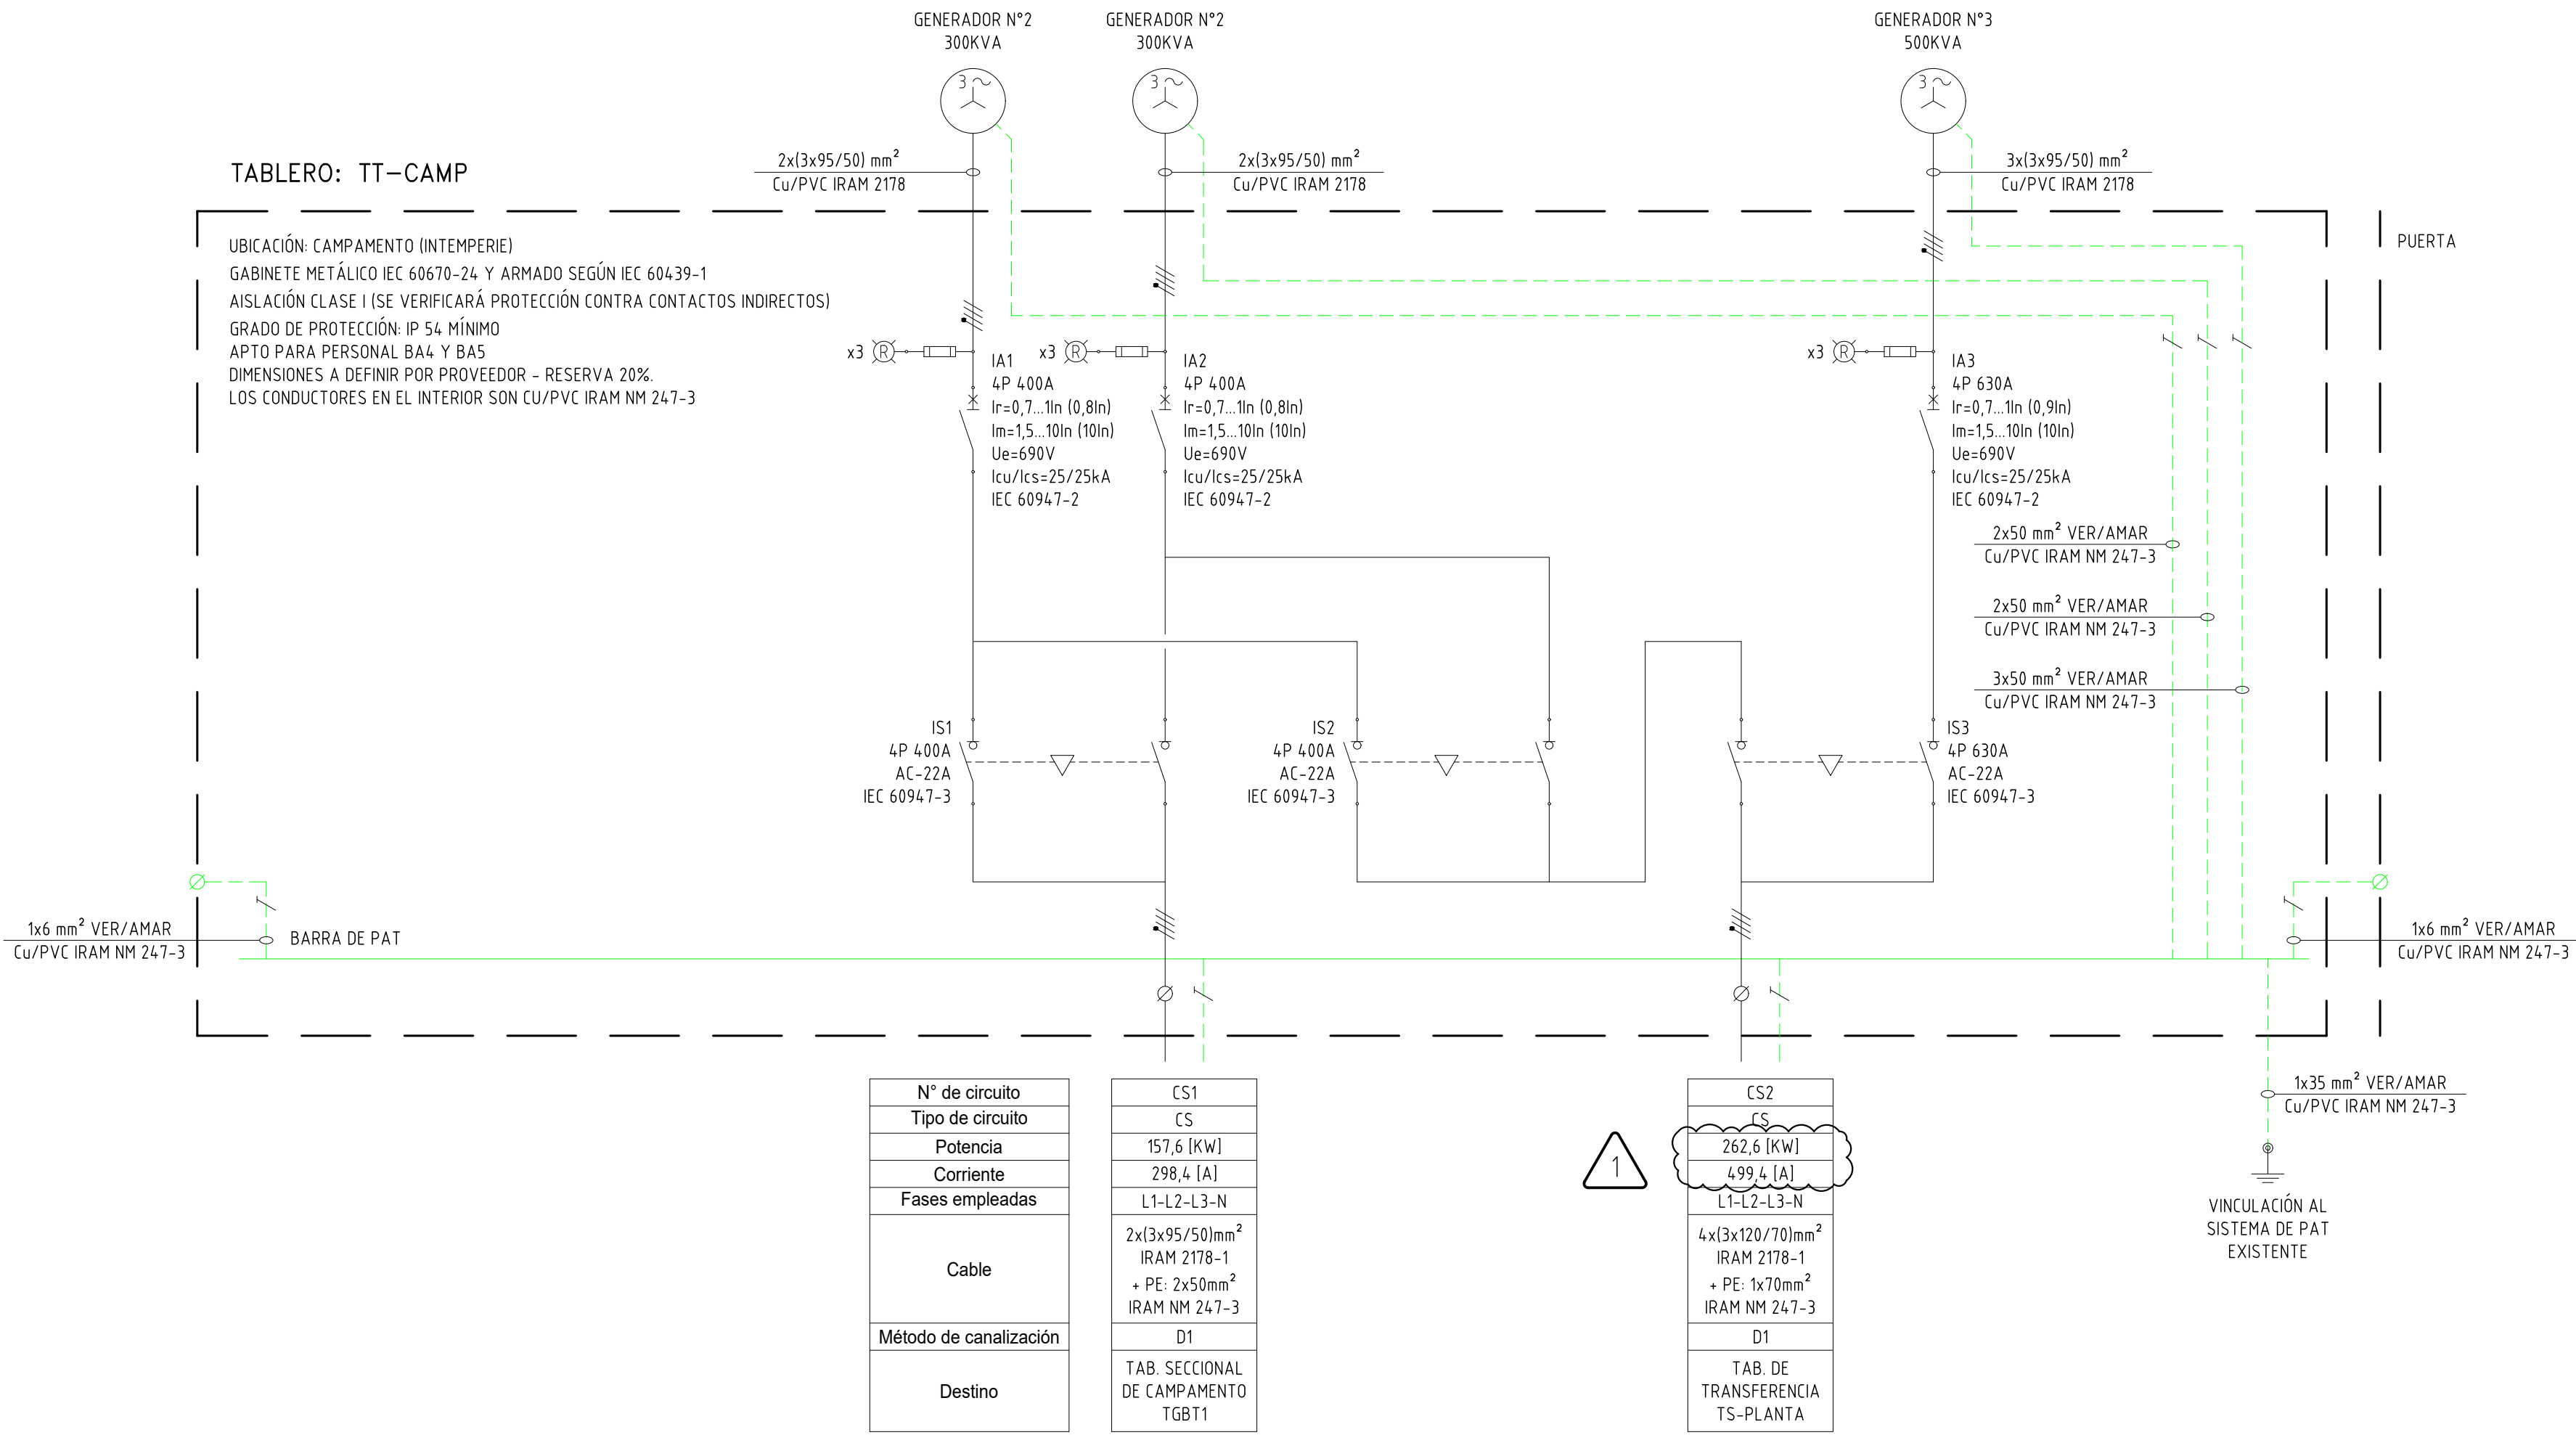

REFERENCIAS

	INTERRUPTOR DIFERENCIAL NORMA IEC 61008		INTERRUPTOR TERMOMAGNÉTICO NORMA IEC 60947-2 (CON REG. FIJA)
	INTERRUPTOR AUTOMÁTICO NORMA IEC 60947-2 (CON REG. VARIABLE)		INTERRUPTOR SECCIONADOR NORMA IEC 60947-3 (INTERRUPTOR MANUAL)
	ELEMENTO DE MANIOBRA Y ENCLAVAMIENTO MECANICO ENTRE INTERRUPTORES		CONDUCTOR DE LÍNEA, NEUTRO Y PE (RESPECTIVAMENTE)
	GENERADOR TRIFÁSICO		ELECTRODO DE PUESTA A TIERRA
	FUSIBLE		INDICADOR LUMINOSO
	BORNES PARA USO GENERAL NORMA IEC 60947-7-1 (4) BORNE 4mm² - 32A - 800V (6) BORNE 6mm² - 41A - 800V (10) BORNE 10mm² - 57A - 800V (16) BORNE 16mm² - 101A - 800V (50) BORNE 50mm² - 150A - 800V (150) BORNE 95mm² - 309A - 800V (240) BORNE 240mm² - 415A - 800V		

NOTAS

- EL TABLERO DEBERÁ SER PROYECTADO PARA UN SERVICIO CONTINUO LAS 24 HORAS DEL DÍA.
- TODAS LAS PARTES Y PIEZAS DEBEN SER FÁCILMENTE ACCESIBLES PARA INSPECCIÓN, MANTENIMIENTO, REEMPLAZO O REPARACIÓN.
- SE DEBERÁ CONTEMPLAR LA INSTALACIÓN DE LUCES PILOTO LED EN PUERTA DEL GABINETE PARA INDICAR PRESENCIA/AUSENCIA DE TENSIÓN EN LAS TRES FASES.
- EL FABRICANTE DEL TABLERO DEBERÁ GARANTIZAR LOS VALORES INDICADOS EN ESTE UNIFILAR PARA LAS CONDICIONES DEL SITIO, YA QUE NO SE HA SOBREDIMENSIONADO NINGÚN ELEMENTO DE PROTECCIÓN CON EL FIN DE COMPENSAR LOS EFECTOS GENERADOS POR LAS CONDICIONES AMBIENTALES DEL SITIO. SERÁ RESPONSABILIDAD DEL FABRICANTE LA CORRECTA ELECCIÓN DE LOS ELEMENTOS CONFORME A LA TECNOLOGÍA PROVISTA Y COMO SE COMPORTA LA MISMA EN PLANTA.
- SERÁ RESPONSABILIDAD DEL FABRICANTE LA CORRECTA ELECCIÓN DE LOS ELEMENTOS CONFORME A LA TECNOLOGÍA PROVISTA.
- LOS TABLEROS DEBERAN POSEER EN LA PARTE FRONTAL EXTERIOR DE SUS PUERTAS EL SIMBOLO DE "RIESGO ELECTRICO" (NORMA IRAM 10005-1) CON UNA ALTURA MINIMA DE 40mm. EL SIMBOLO DE "RIESGO ELECTRICO", ASI COMO LAS RESTANTES MARCACIONES EXIGIDAS POR LA NORMA DE PRODUCTO DEBERAN SER DURABLES Y ESTAR SIEMPRE VISIBLES, PODRAN ESTAR GRABADAS, PINTADAS EN FORMA INDELEBLE, O FIJADAS MEDIANTE UN METODO ADECUADO QUE ASEGURE SU PERMANENCIA EN EL TIEMPO.

DOCUMENTOS DE REFERENCIA

DOCUMENTO N°	DESCRIPCIÓN
TOL-0000-E-LC-300	LISTADO DE CARGAS ELÉCTRICAS Y MEMORIA DE CÁLCULO DE CABLES

APTO PARA CONSTRUCCION

FECHA: 13/09/2024 APROB. POR: J.P.G.

	PARA CONSTRUCCION	13/09/2024	C.C.M.	J.P.G.	J.P.G.
	PARA CONSTRUCCION	06/09/2024	C.C.M.	J.P.G.	J.P.G.
REV.	DESCRIPCIÓN	FECHA	EJEC.	CONTR.	APR.

DIBUJÓ: 13/09/2024	C.C.M.		
REVISÓ: 13/09/2024	J.P.G.	una compañía de Tecpetrol	
APROBÓ: 13/09/2024	J.P.G.		

ESCALA: S=1	PLANTA PILOTO	DOCUMENTO PROVEEDOR: XXXX-XXXX-XX-X-XXX
REVISION: 1	PLANTA DLE - SALAR	DOCUMENTO CLIENTE: TOL-0000-E-UE-300
HOJA: 1 - 1	UNIFILAR - ALIMENTACIÓN GENERAL	ESPECIALIDAD: ELÉCTRICA
	TT-CAMP / TS-PLANTA	