


GABINETE
TIPO GENROD
MODULAR serie 97
o similar
PUERTA CIEGA
cerradura a llave

GABINETE
TIPO GENROD
MODULAR serie 97
o similar

PUERTA CIEGA / similar c/ vidrio

Tablero Secc. Subsuelo TSSS


ENTRADA ENERGÍA
POR DEBAJO
DEL GABINETE
3 CAÑOS PVC 110

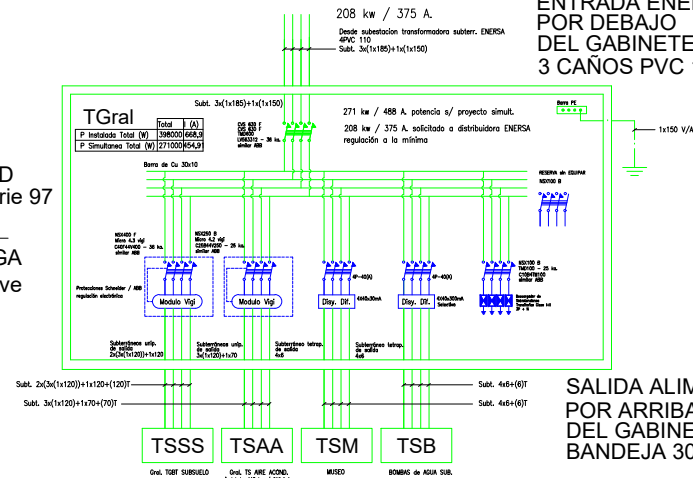

Salida Alimentadores
por arriba
del gabinete
bandeja 300 mm.

Entrada Alimentación
por arriba
del gabinete
bandeja 300 mm.

Salida Alimentadores
por arriba
del gabinete
bandeja 300 mm.

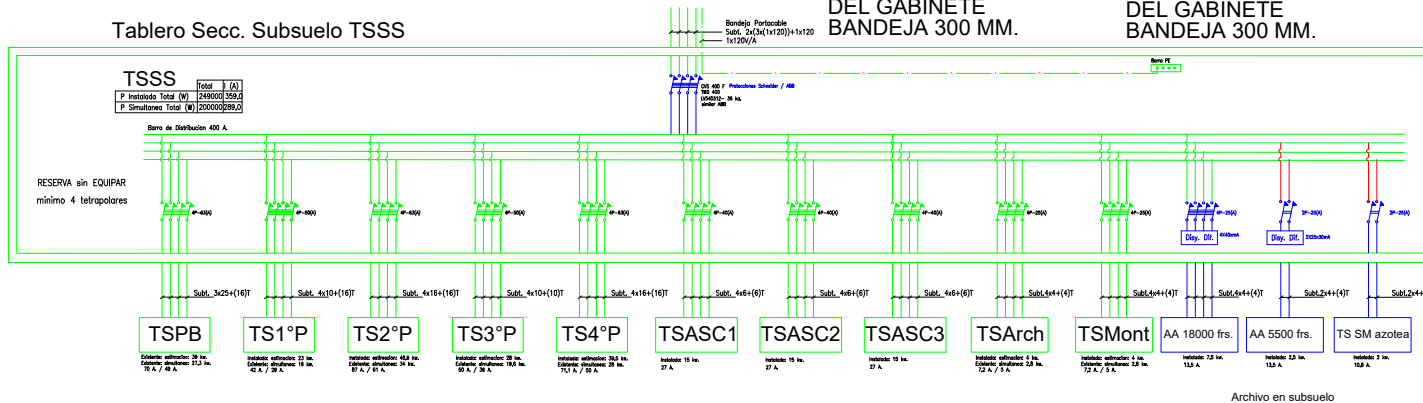

Archivo en subsuelo

PROYECTO EJECUTIVO

CEMYC S.R.L.

Obra: SEGUNDA ETAPA OBRA EDIFICIO
JEFATURA DEPARTAMENTAL PARANA

Localización: Calle Laprida 460

Departamento: Parana - Entre Rios.

Tipo de Obra:

Responsable:

Archivo:

Escala:

F/Esc.

Plano:

Esquema de Conexión - TGral - TSSubs

Fecha:

Octubre 2023