




VISTA FRONTAL
CON PUERTA

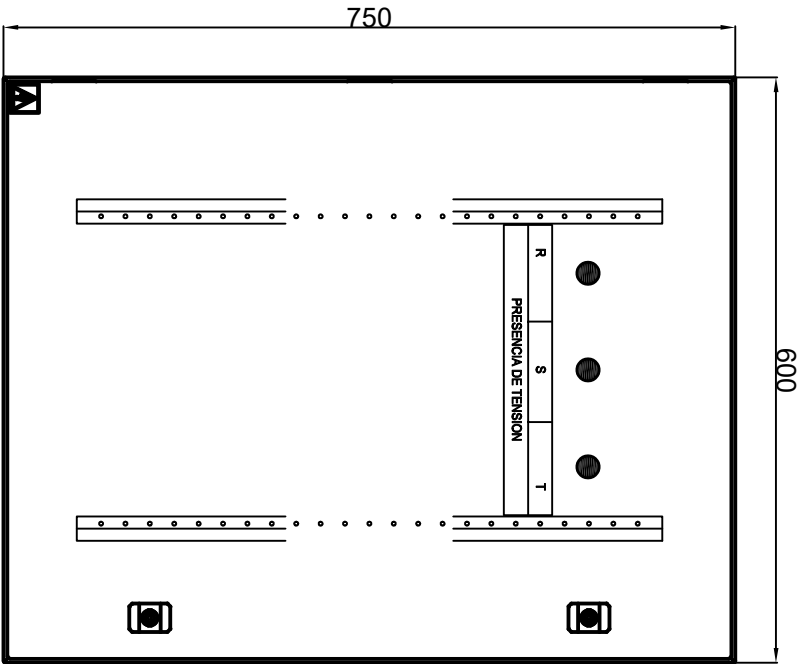


VISTA LATERAL
DERECHA

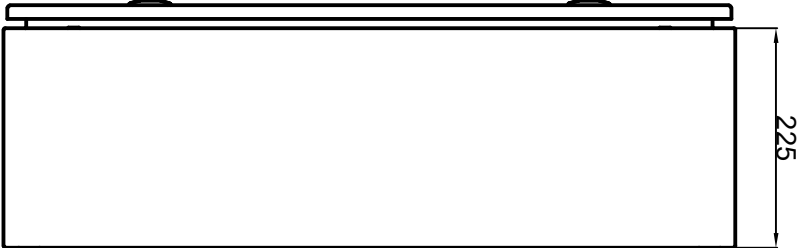


VISTA FRONTAL SIN PUERTA
CON BANDEJA

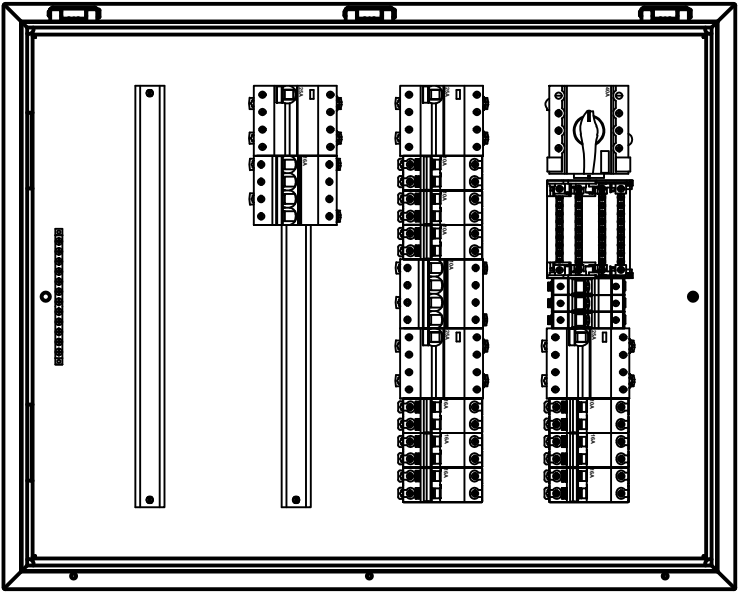

VISTA FRONTAL SIN PUERTA
CON CONTRAFRENTE

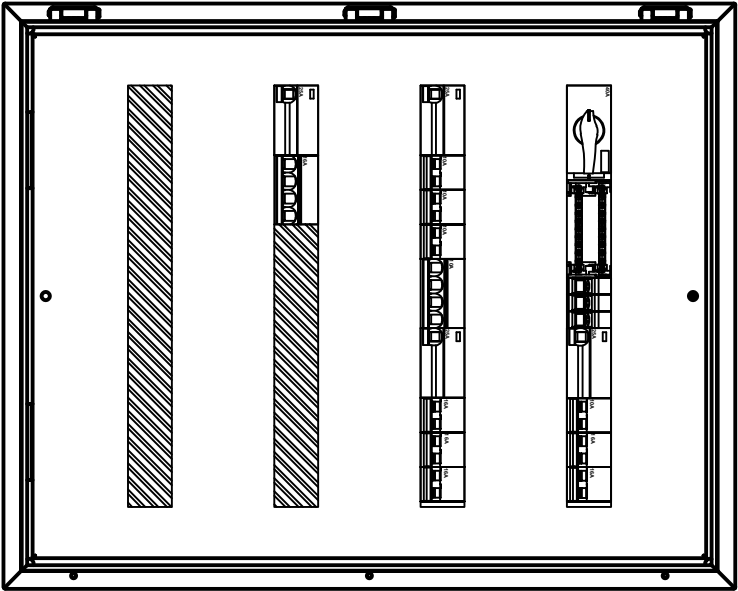

Tablero Seccional
Sector: - Gobierno Sub Unidad

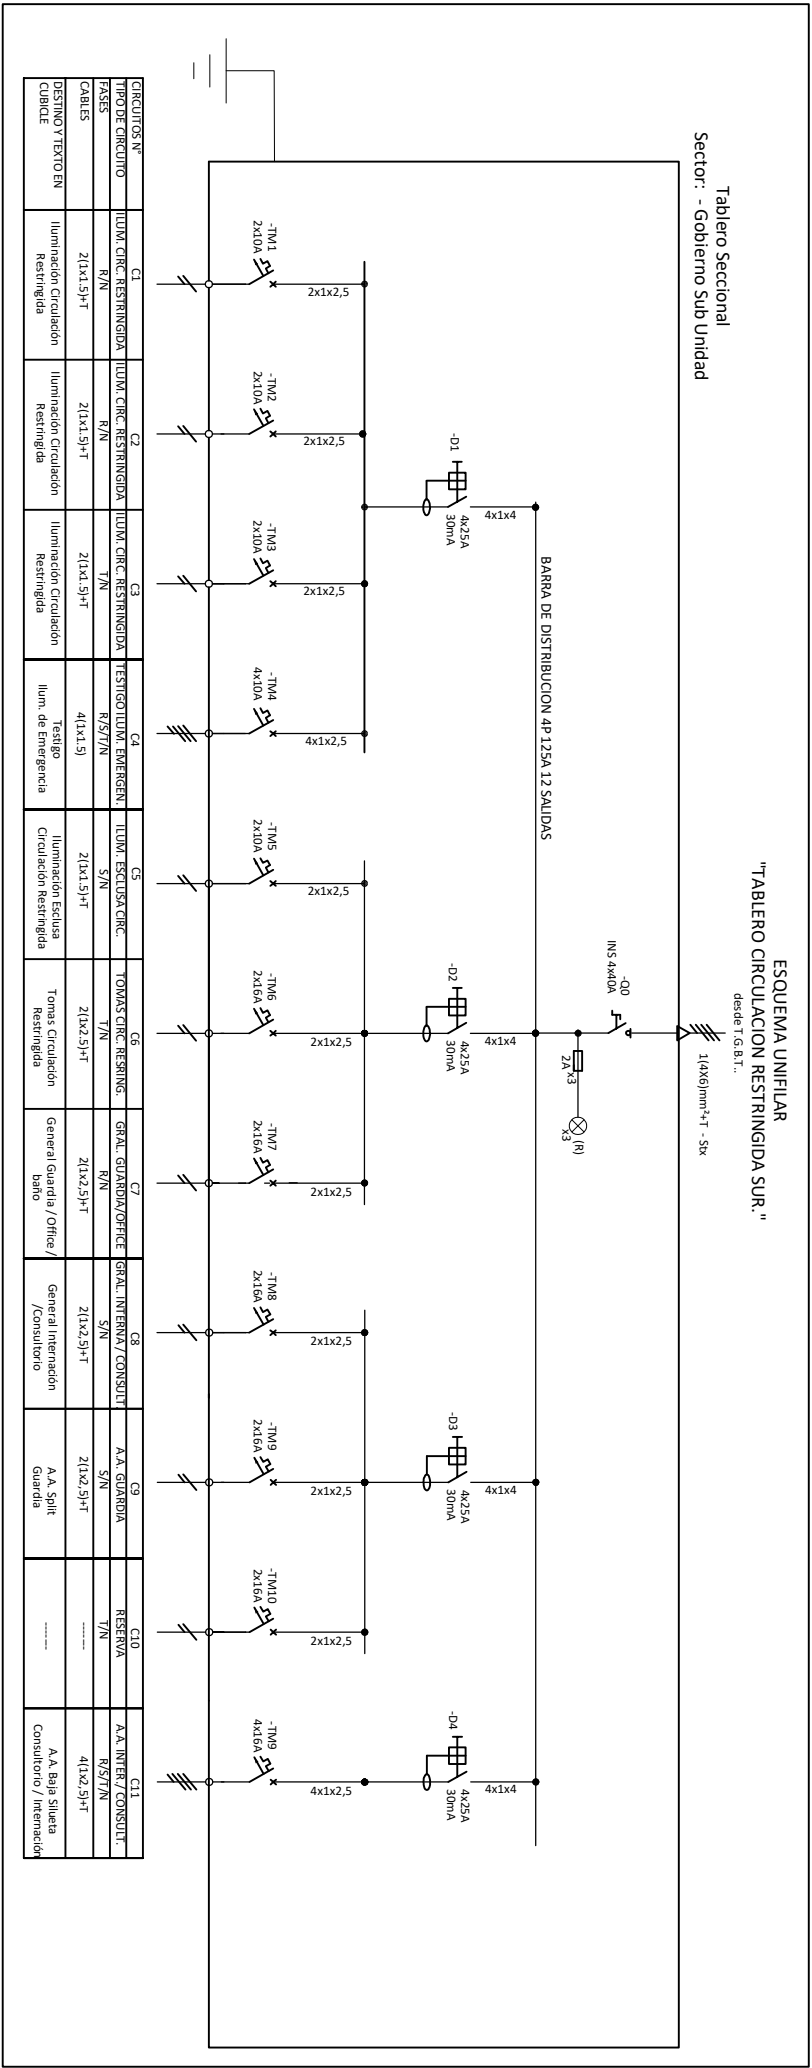

OBRA: LP N°8		REV A
COMITENTE: EIECA SA, PECAM SA, DYSCON SA, MINERVINO SA		
PLANO: UNIFILARES Y TOPOGRAFICOS		
ESCALA: Grafica		HOLD: 1/1
		FECHA: 01/05/2025