



VISTA FRONTAL
CON PUERTA

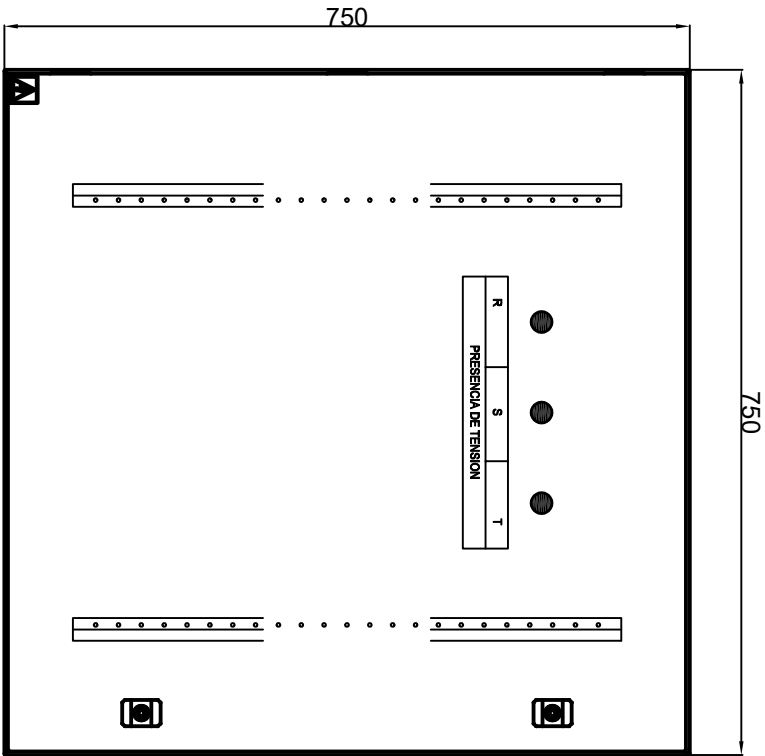


VISTA LATERAL
DERECHA




VISTA FRONTAL SIN PUERTA
CON BANDEJA

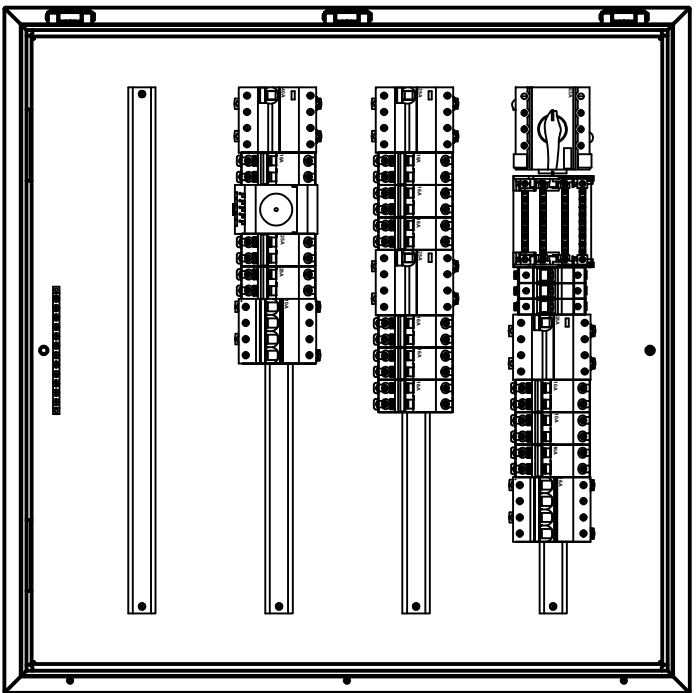

VISTA FRONTAL SIN PUERTA
CON CONTRARENTE

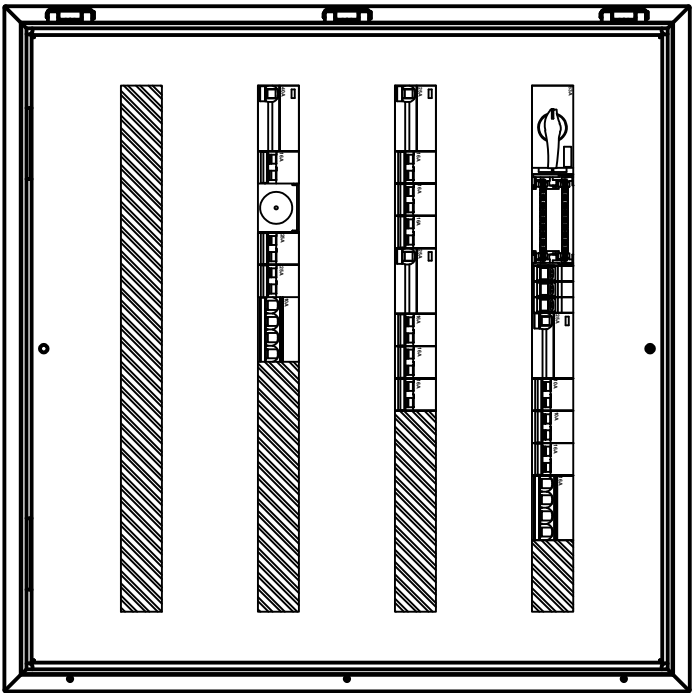

Tablero Seccional
Sector: - Gobierno Sub Unidad

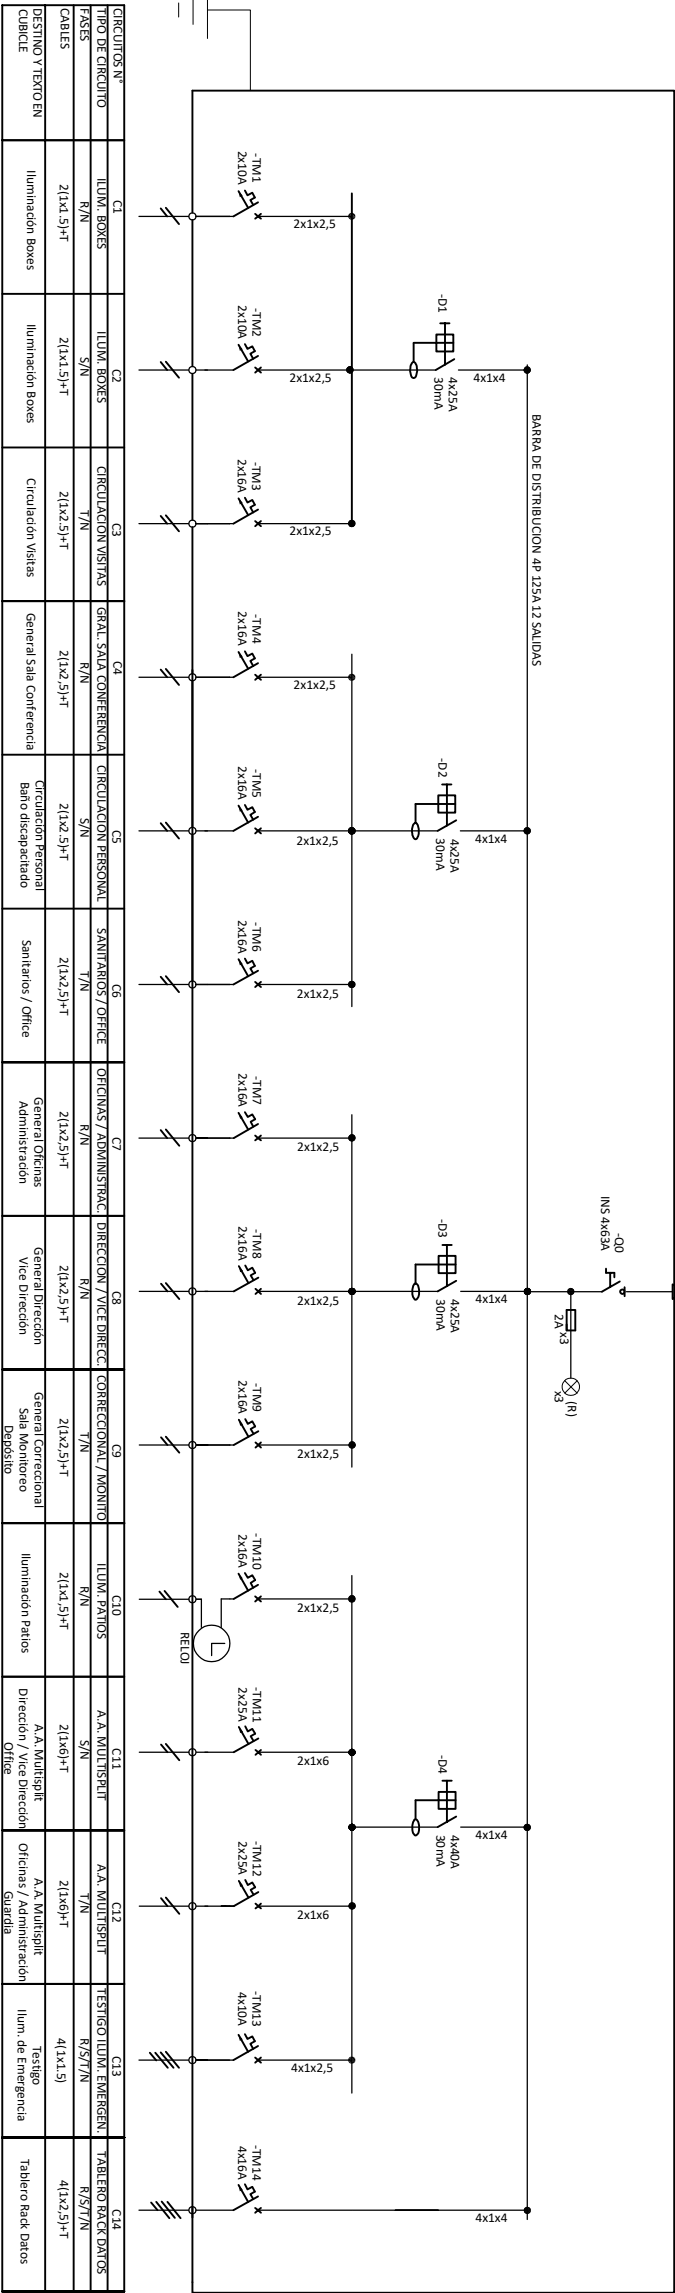

NOTA: TODOS LOS INTERRUPTORES SERÁN DE PRIMERA MARCA TIPO SCHNEIDER - SIEMENS O SIMILAR LAS ENVOYENTES SERÁN TIPO TECNODOX - GENROD O SIMILAR



OBRA: UP N°8		REVA
COMITENTE: EIECA SA, PECAM SA, DYSCON SA, MINERVINO SA		
PLANO: UNIFILARES Y TOPOGRAFICOS		FECHA: 01/05/2025
ESCALA: Grafica		HOLA: 1/1