
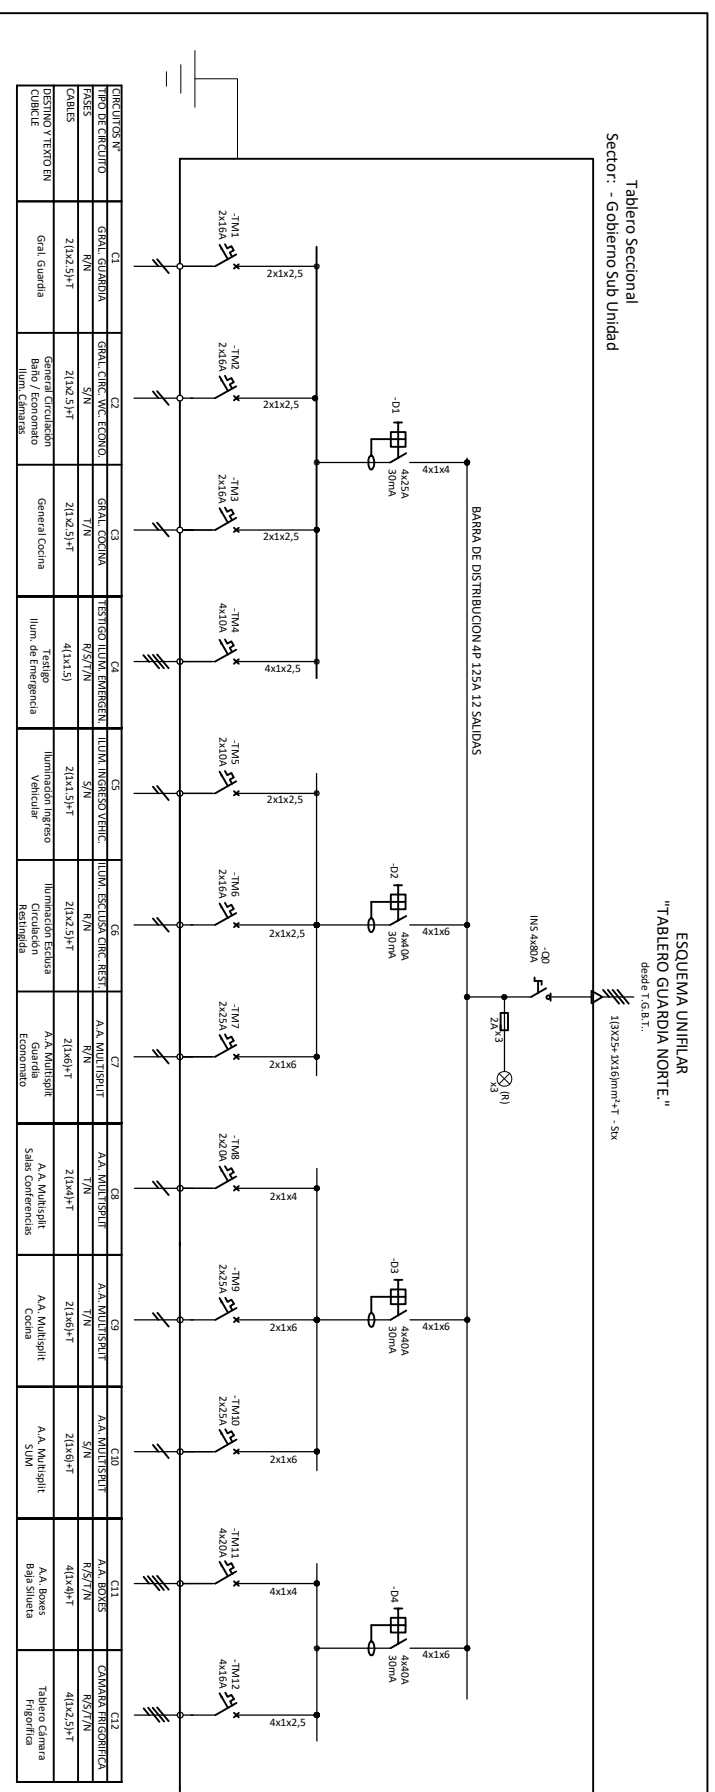
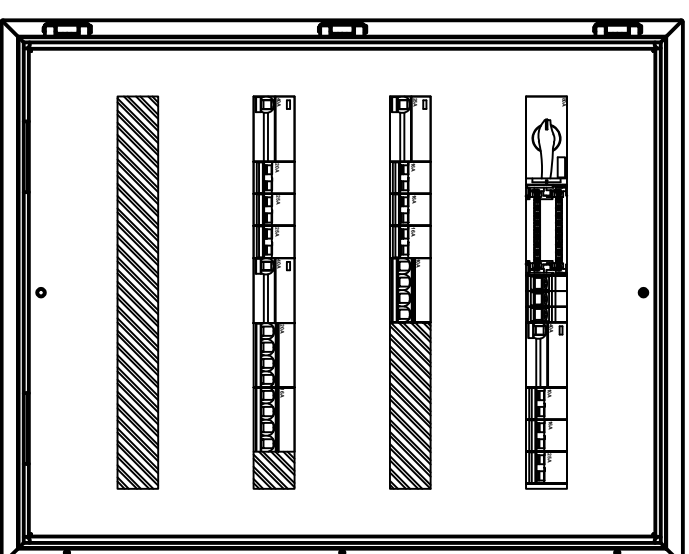
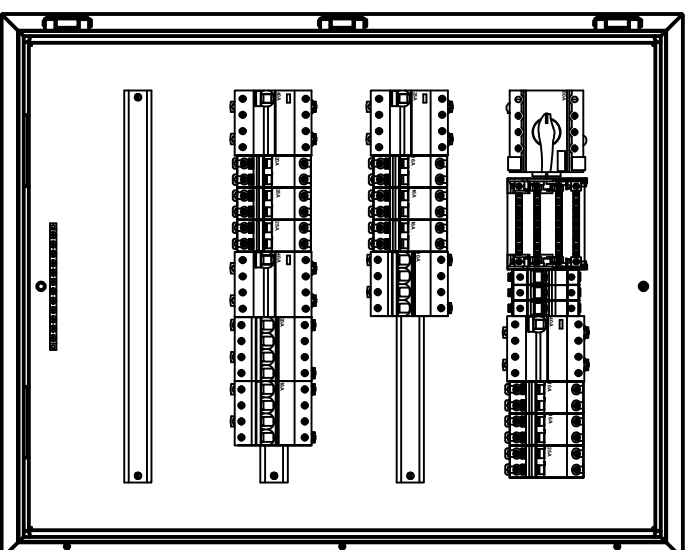


VISTA FRONTAL
CON PUERTA

VISTA LATERAL
DERECHA

VISTA FRONTAL SIN PUERTA
CON BANDEJA

VISTA FRONTAL SIN PUERTA
CON CONTRAFRENTE

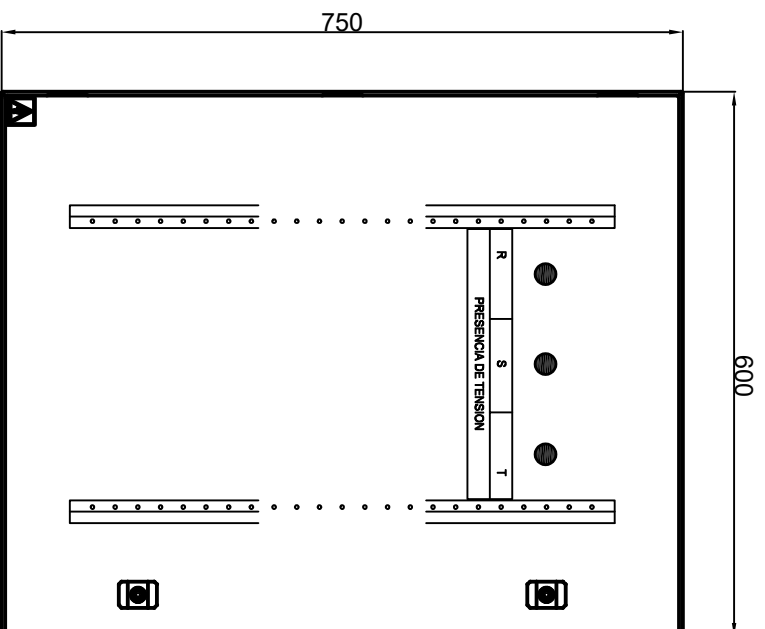

NOTA: TODOS LOS INTERRUPTORES SERAN DE PRIMERA MARCA TIPO SCHNEIDER - SIEMENS O SIMILAR
LAS ENVOLVENTES SERAN TIPO TECNOBOX - GENROD O SIMILAR

OBRA: UP N°8

COMITENTE: EDECA SA, PECAM SA, DYSCON SA, MINERVINO SA

REV A

PLANO: UNIFILARES Y TOPOGRAFICOS

FECHA: 01/05/2025

ESCALA: Gráfica

HOJA: 1/1



SEMI
CONSTRUCCIONES S.R.L.