




VISTA FRONTAL
CON PUERTA

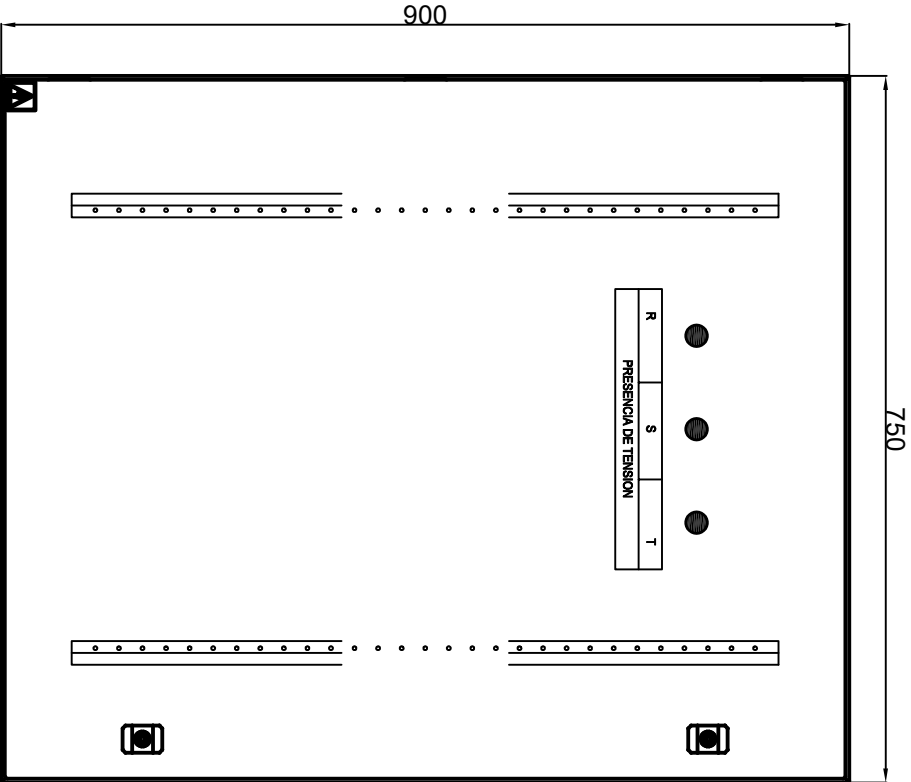


VISTA LATERAL
DERECHA

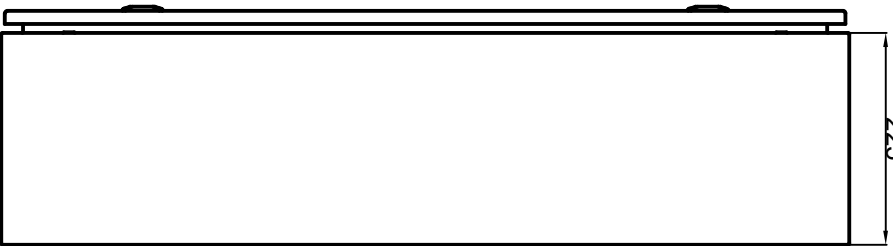


VISTA FRONTAL SIN PUERTA
CON BANDEJA

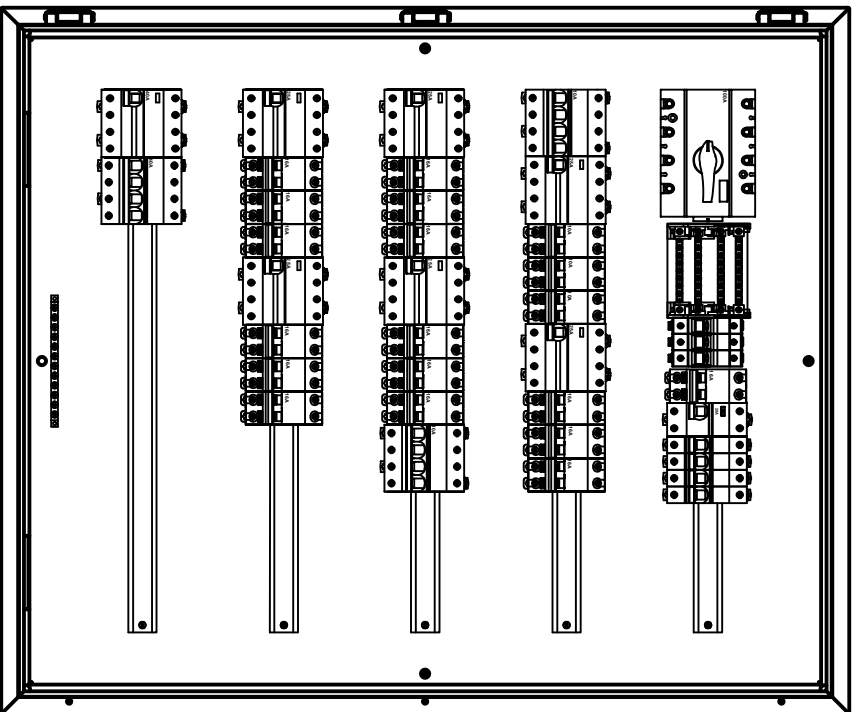

VISTA FRONTAL SIN PUERTA
CON CONTRAFRENTE

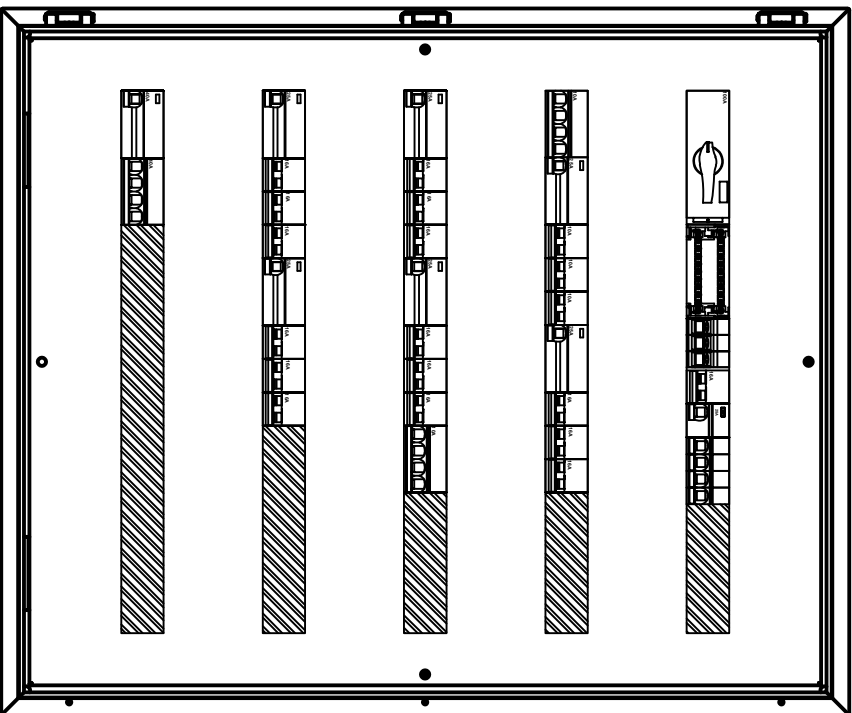

Tablero Seccional de Pabellones
Sector: Pabellón Tipo Planta Baja

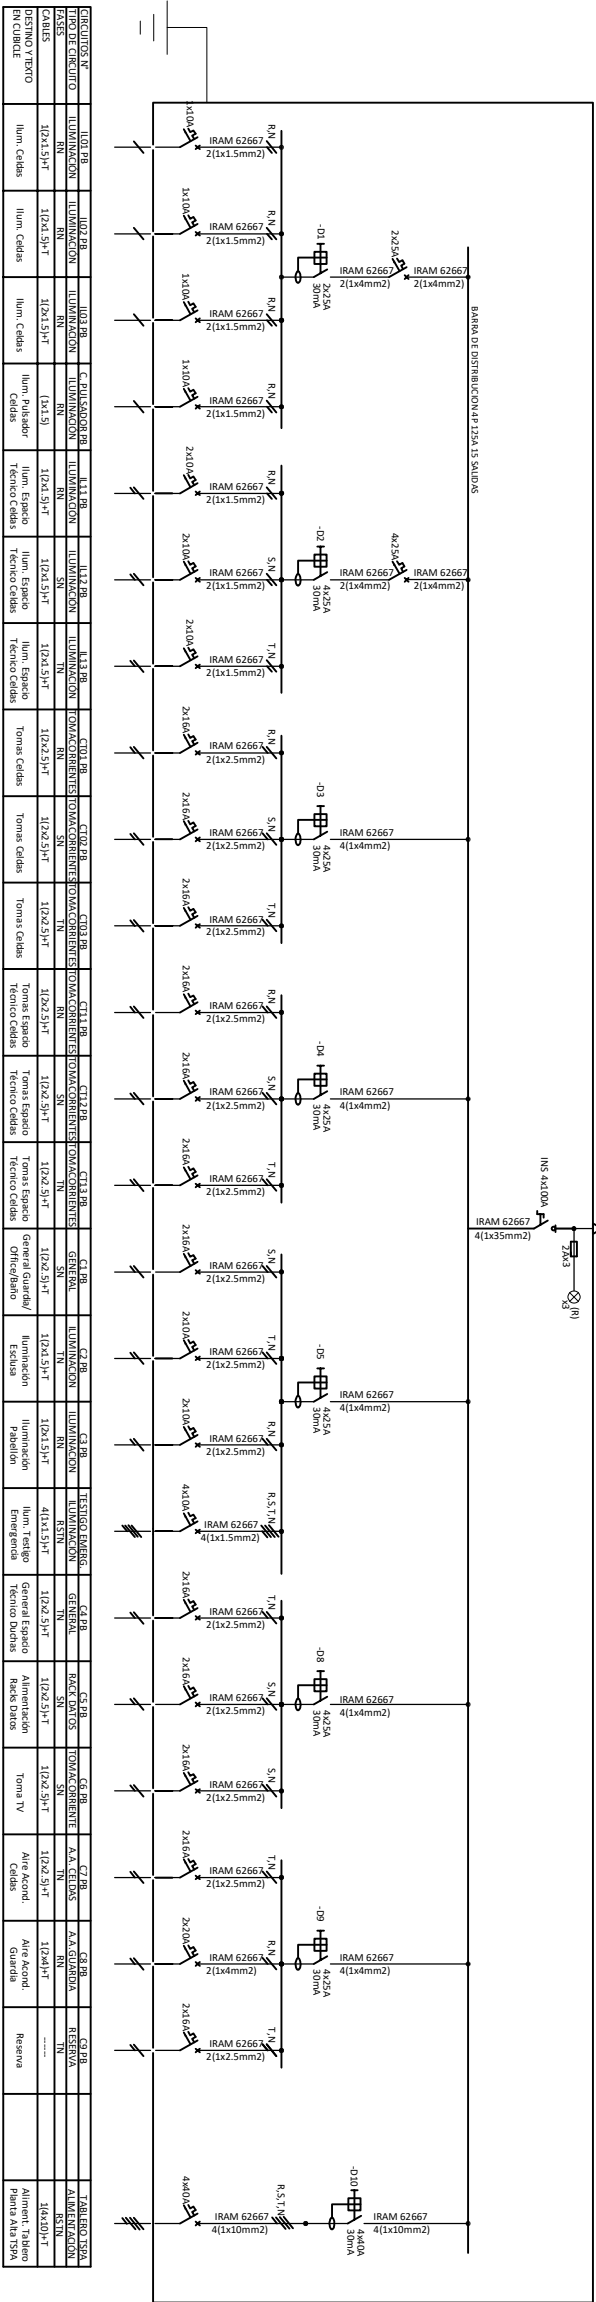

NOTA: TODOS LOS INTERRUPTORES SERÁN DE PRIMERA MARCA TIPO
SCHEIDER - SIEMENS O SIMILAR
LAS ENVOLVENTES SERÁN TIPO TECNODOX - GENIND O SIMILAR